

www.e-construct.in

Construct Your Dream Home with **E-CONSTRUCT**

 +91 9036744017


ECONSTRUCT
DESIGN & BUILD PVT. LTD.



ABOUT US

ECONSTRUCT Design & Build Pvt Ltd is a leading consultancy and contracting company in India that has executed construction work for some of the most significant projects in the country. We continue to alter the structural landscape through several other prestigious projects in the residential, commercial, and Institutional space.

We believe in exceeding clients' expectations by operating at par with global benchmarks for transparency, reliability and integrity. A commitment to sustainable development, safety and environment protection forms the genesis of our culture. Our clients value our allegiance to quality, timely deliveries, superior customer service and the experience of engaging in business with a highly qualified and experienced management. After creating our mark on the Mumbai landscape, we expanded to Bangalore, Tumkur, Mysore.

ECONSTRUCT is committed to maintaining the highest standards of business conduct and corporate governance. We believe this is essential for operating a successful business, serving our shareholders and maintaining our integrity in the marketplace. We look at each project as a mission our team has to achieve, for the sake of the client's dreams, pride of our shareholders and ultimately, self-satisfaction.

www.e-construct.in



FOUNDER'S INTRODUCTION

Sandeep Pingale Founder & MD

He has over 20+ years of experience in Civil & Structural engineering. International experience in structural analysis, Design, Execution and Management of up to G+81 story structure in Dubai.

He has worked with a various Multidisciplinary organization that has given him "State of Art" in providing the services with International quality standards.

He has worked by considering various International codes like ACI, CEBFIP, BS codes, IS codes that gave him the excellent exposure and immense knowledge about the civil engineering area.



FOUNDER'S INTRODUCTION

Shraddha Pingale Jt. Managing Director

M.Tech Graduate from a recognized university who co-founded ECONSTRUCT Design & Build Pvt Ltd. Well-known for her innovative techniques in Business Development, Creative Strategies, Brand Building, Corporate Trainings for Entrepreneurship. She is young, dynamic, self-motivated and she knows how to build the building blocks of the foundation of any company. She is the backbone of the company that stands straight in every challenging situation.



OUR HISTORY

2010

Establishment

ECONSTRUCT Design & Build Pvt. Ltd. was founded with a vision to deliver high-quality engineering, construction, and consultancy services, setting strong foundations in the residential, commercial, and institutional sectors.

2015

Growth & Expansion

After establishing a strong presence in Mumbai, the company expanded operations to Bangalore, Tumkur, and Mysore, executing multiple prestigious projects and strengthening its reputation for quality, transparency, and timely delivery.

2019

Leadership & Excellence

Emerged as a trusted industry leader, operating at global standards with a focus on sustainability, safety, corporate governance, and client satisfaction, while delivering complex, high-value projects across India and Abroad.





Building a home is not just construction —
— it's a lifetime investment. At E-Construct, we help you build
a home that is strong, budget-friendly, and designed for life.

we ensure every detail is handled with perfection,
so you can enjoy a stress-free construction journey.

From planning
to execution,





WHAT WE PROVIDE

- **Architectural Planning**
(Smart & Space-Optimized Designs)
- **Complete Structural Drawings**
(Safe & Strong Design)
- **3D Elevation**
(Visualize Before Construction)
- **Construction Services**
(Quality Execution)
- **Site Visit Support**
(Start to End Guidance)
- **Budget Planning**
(Cost-Controlled Solutions)

We provide 50+ detailed drawings for every project, including Architectural, Structural, and MEP designs.

Why? Because we truly care about your safety, budget, and long-term satisfaction.

With proper planning and complete drawings, you clearly understand every aspect of your home construction. This helps you make informed decisions and avoid costly mistakes.

Even if you want to make changes later, it won't lead to major expenses, because everything is already well-planned in advance.



We Provide

**50+ Detailed Drawings
for Every Project**

Including Architectural, Structural & MEP Designs

Why?

Because we truly care about your
Safety, Budget, and Long-Term Satisfaction.





 Safety |  Budget |  Satisfaction

See Our Completed Project – Understand Our Perfection

Go through our completed project drawings and plans to clearly understand what we deliver with accuracy and detailing.


Project Details

- **Client:** Manjunath
- **Location:** Battarahalli, KR Puram
- **Plot Size:** 60' x 40'
- **Status:** Completed & Client Staying
 - Ground Floor – Parking + Servant Room
 - 1st, 2nd & 3rd Floor – Triplex House
- **Project Timeline:** 14 Months (Including Interior Work)

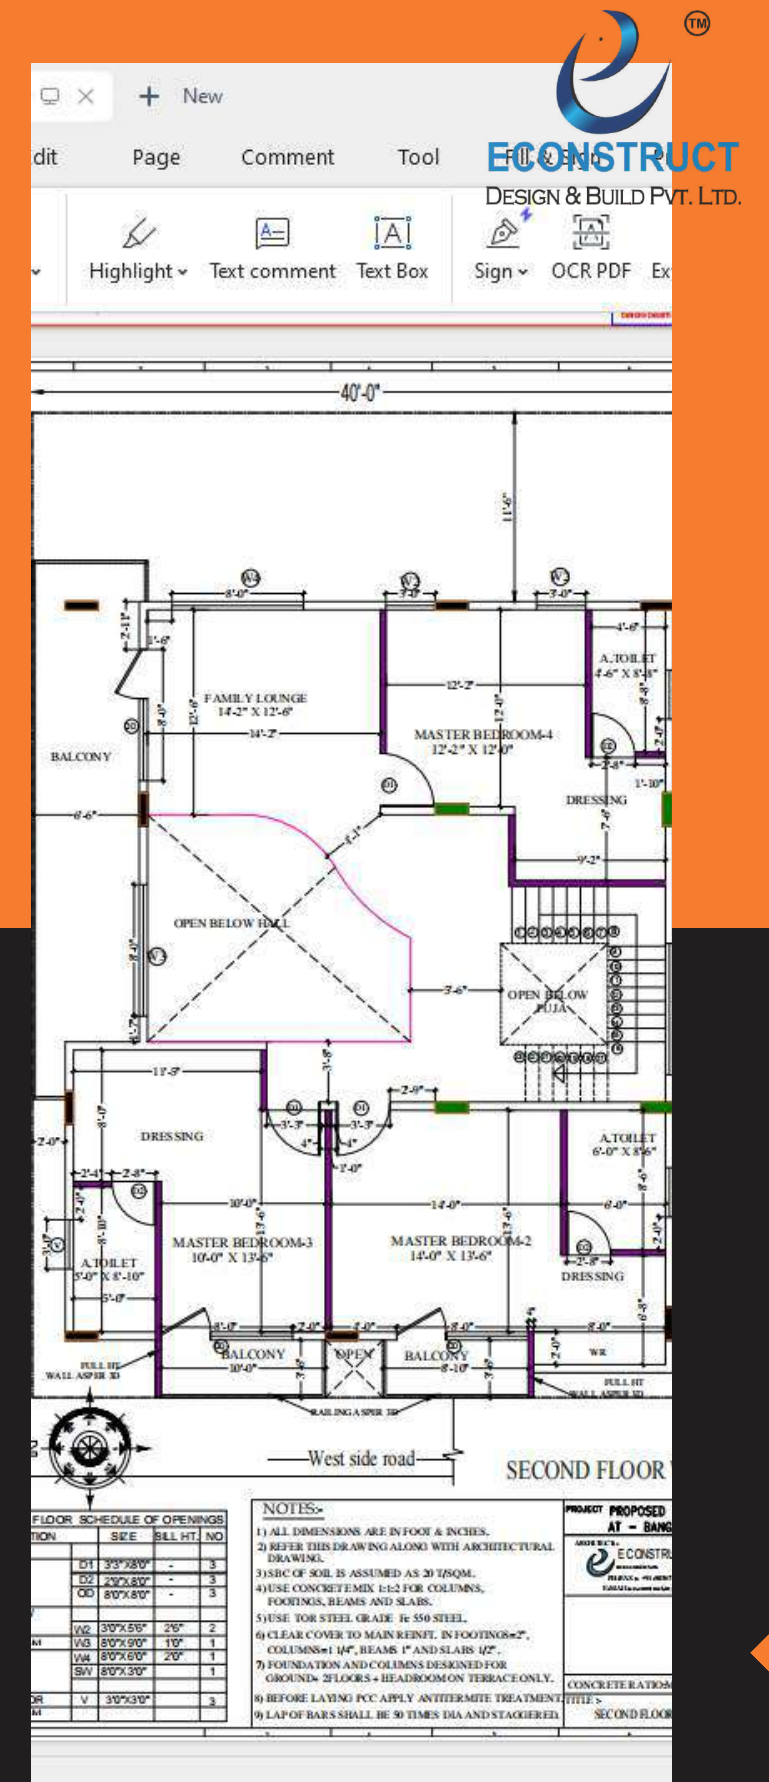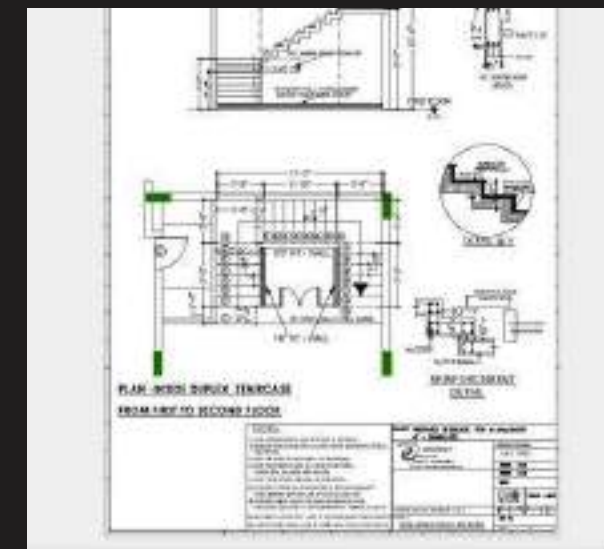



Structural Drawings Included

- Column Marking Layout
- Footing Marking Layout
- Column & Footing RC Details
- Pedestal Reinforcement
- Plinth Beam Layout & Reinforcement
- Ground Floor Beam & Slab Details
- First Floor Beam & Slab Details (Revised)
- Second Floor Beam & Slab Details
- Terrace Beam & Slab Details
- Beam Shuttering Layouts (All Floors)
- Complete Reinforcement Detailing

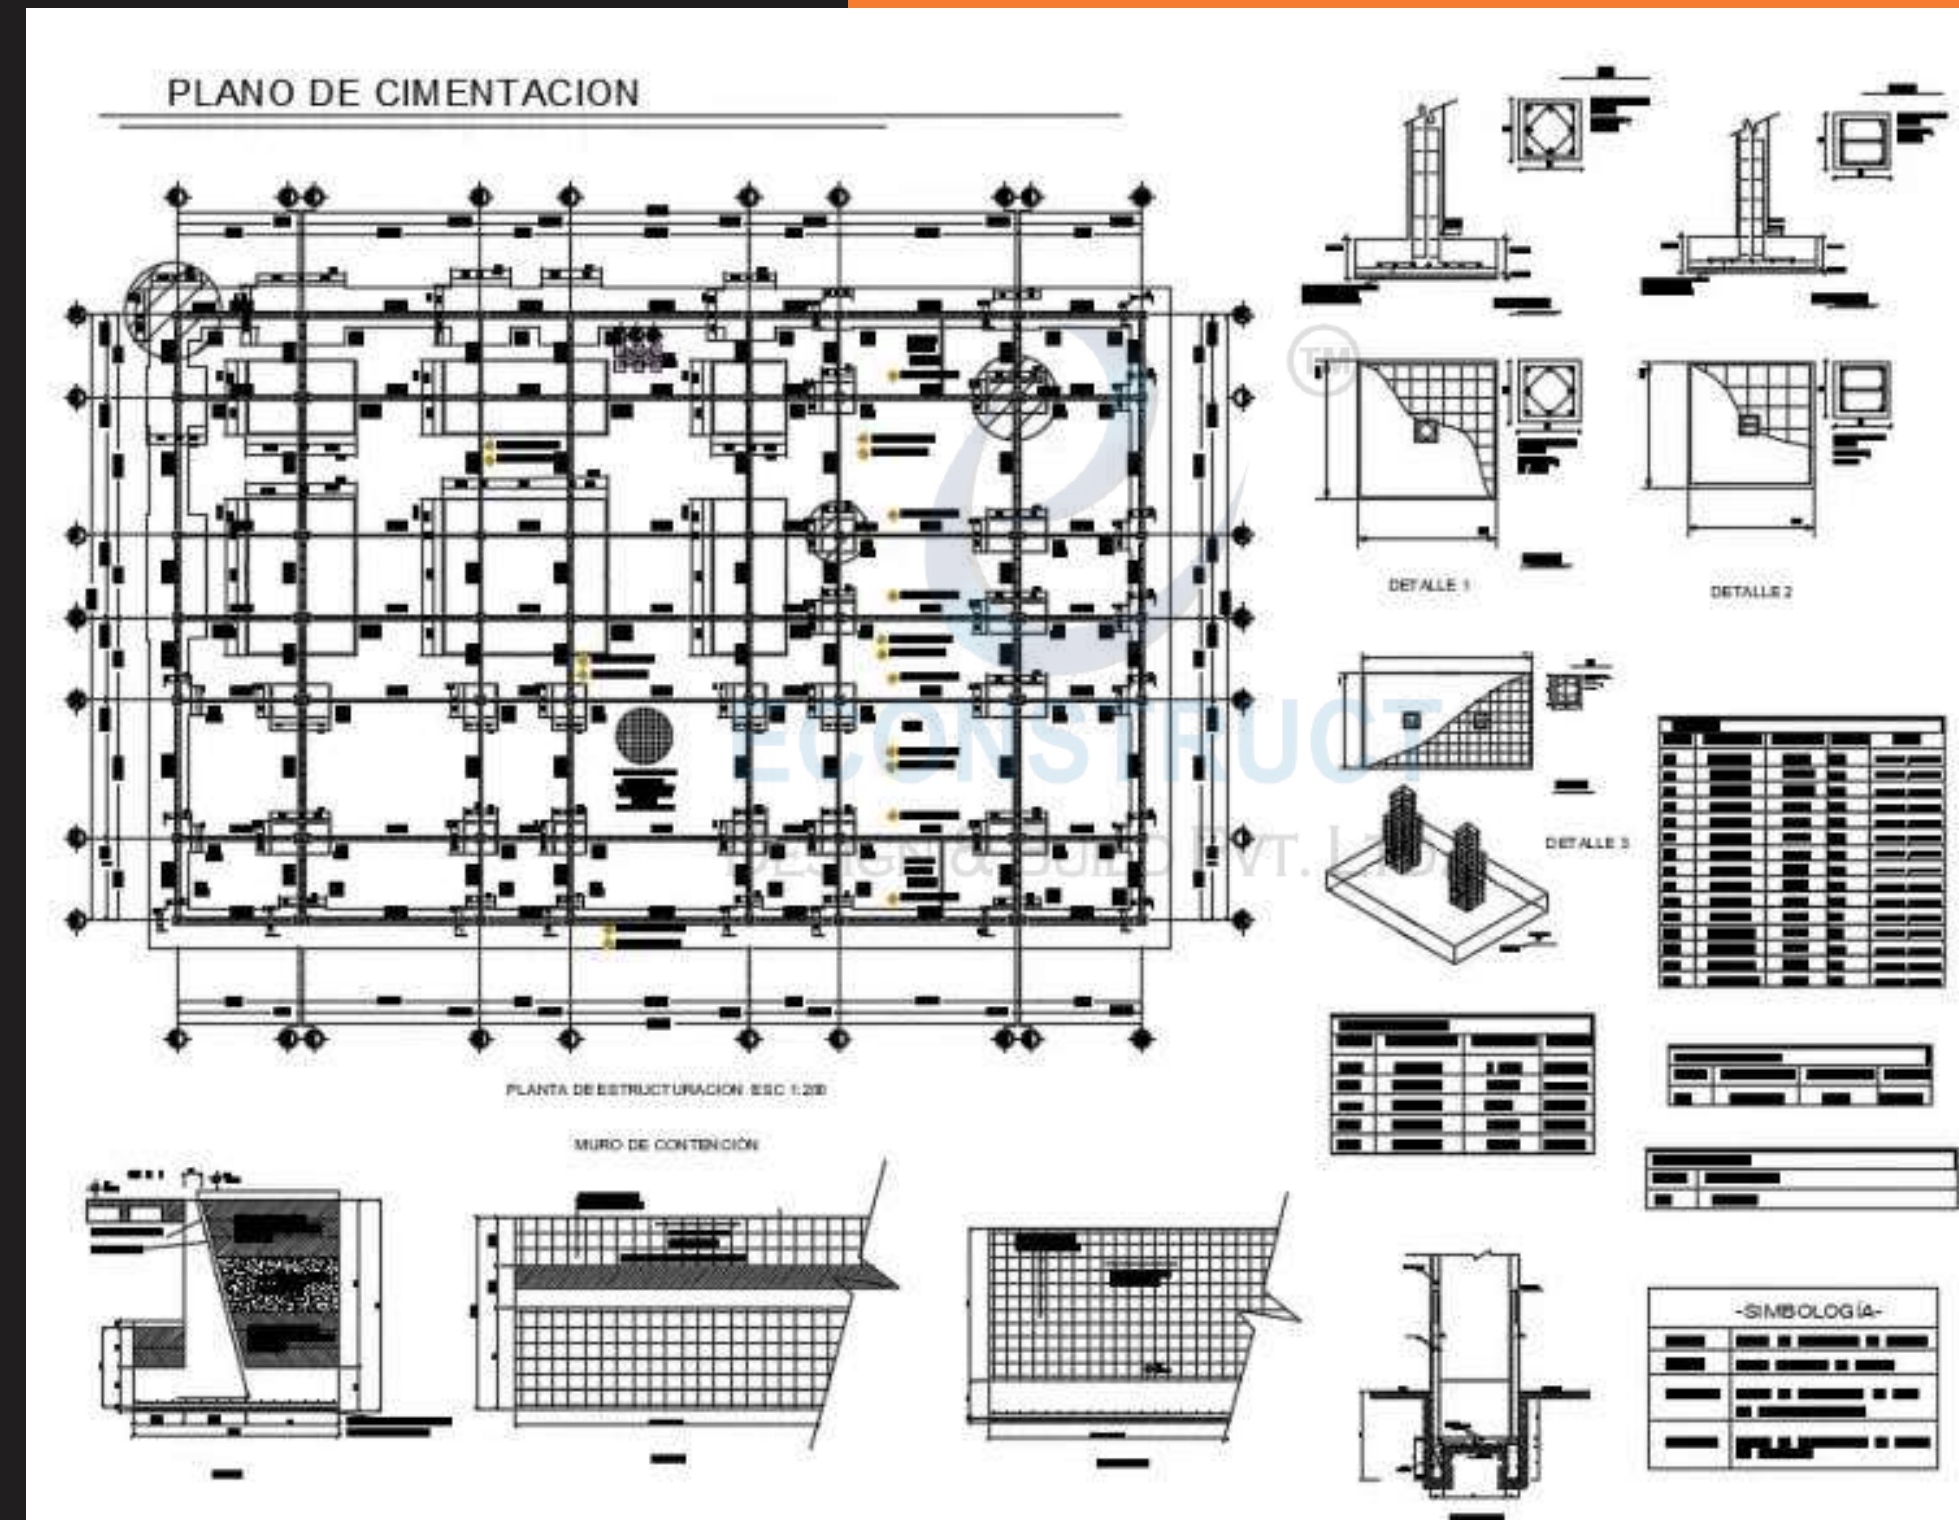

01

COLUMN MARKING LAYOUT

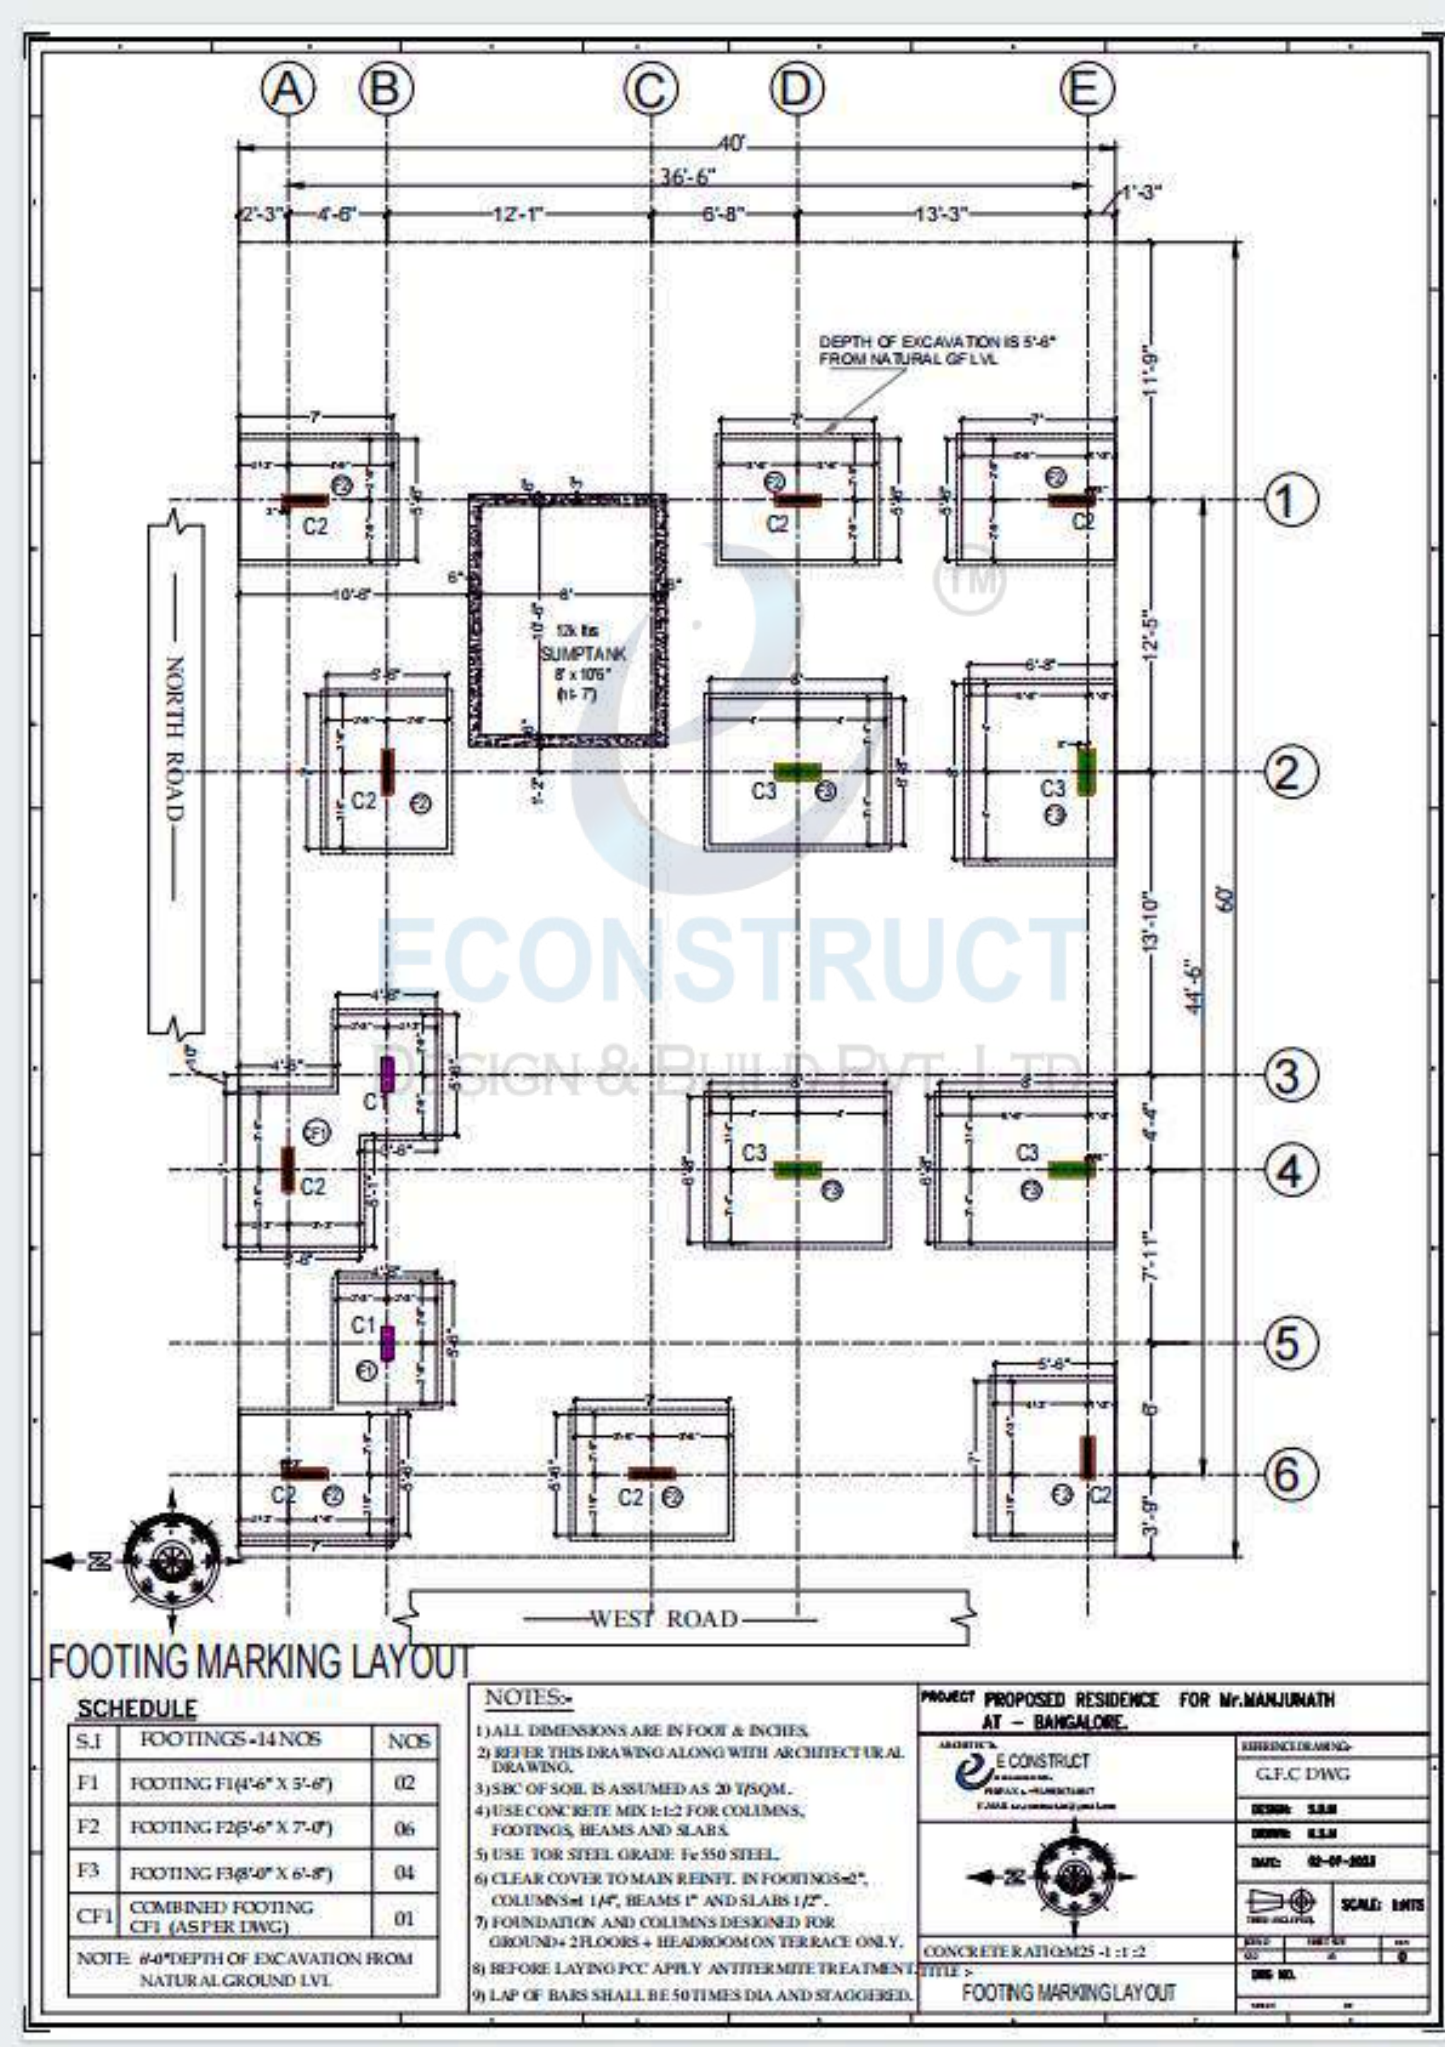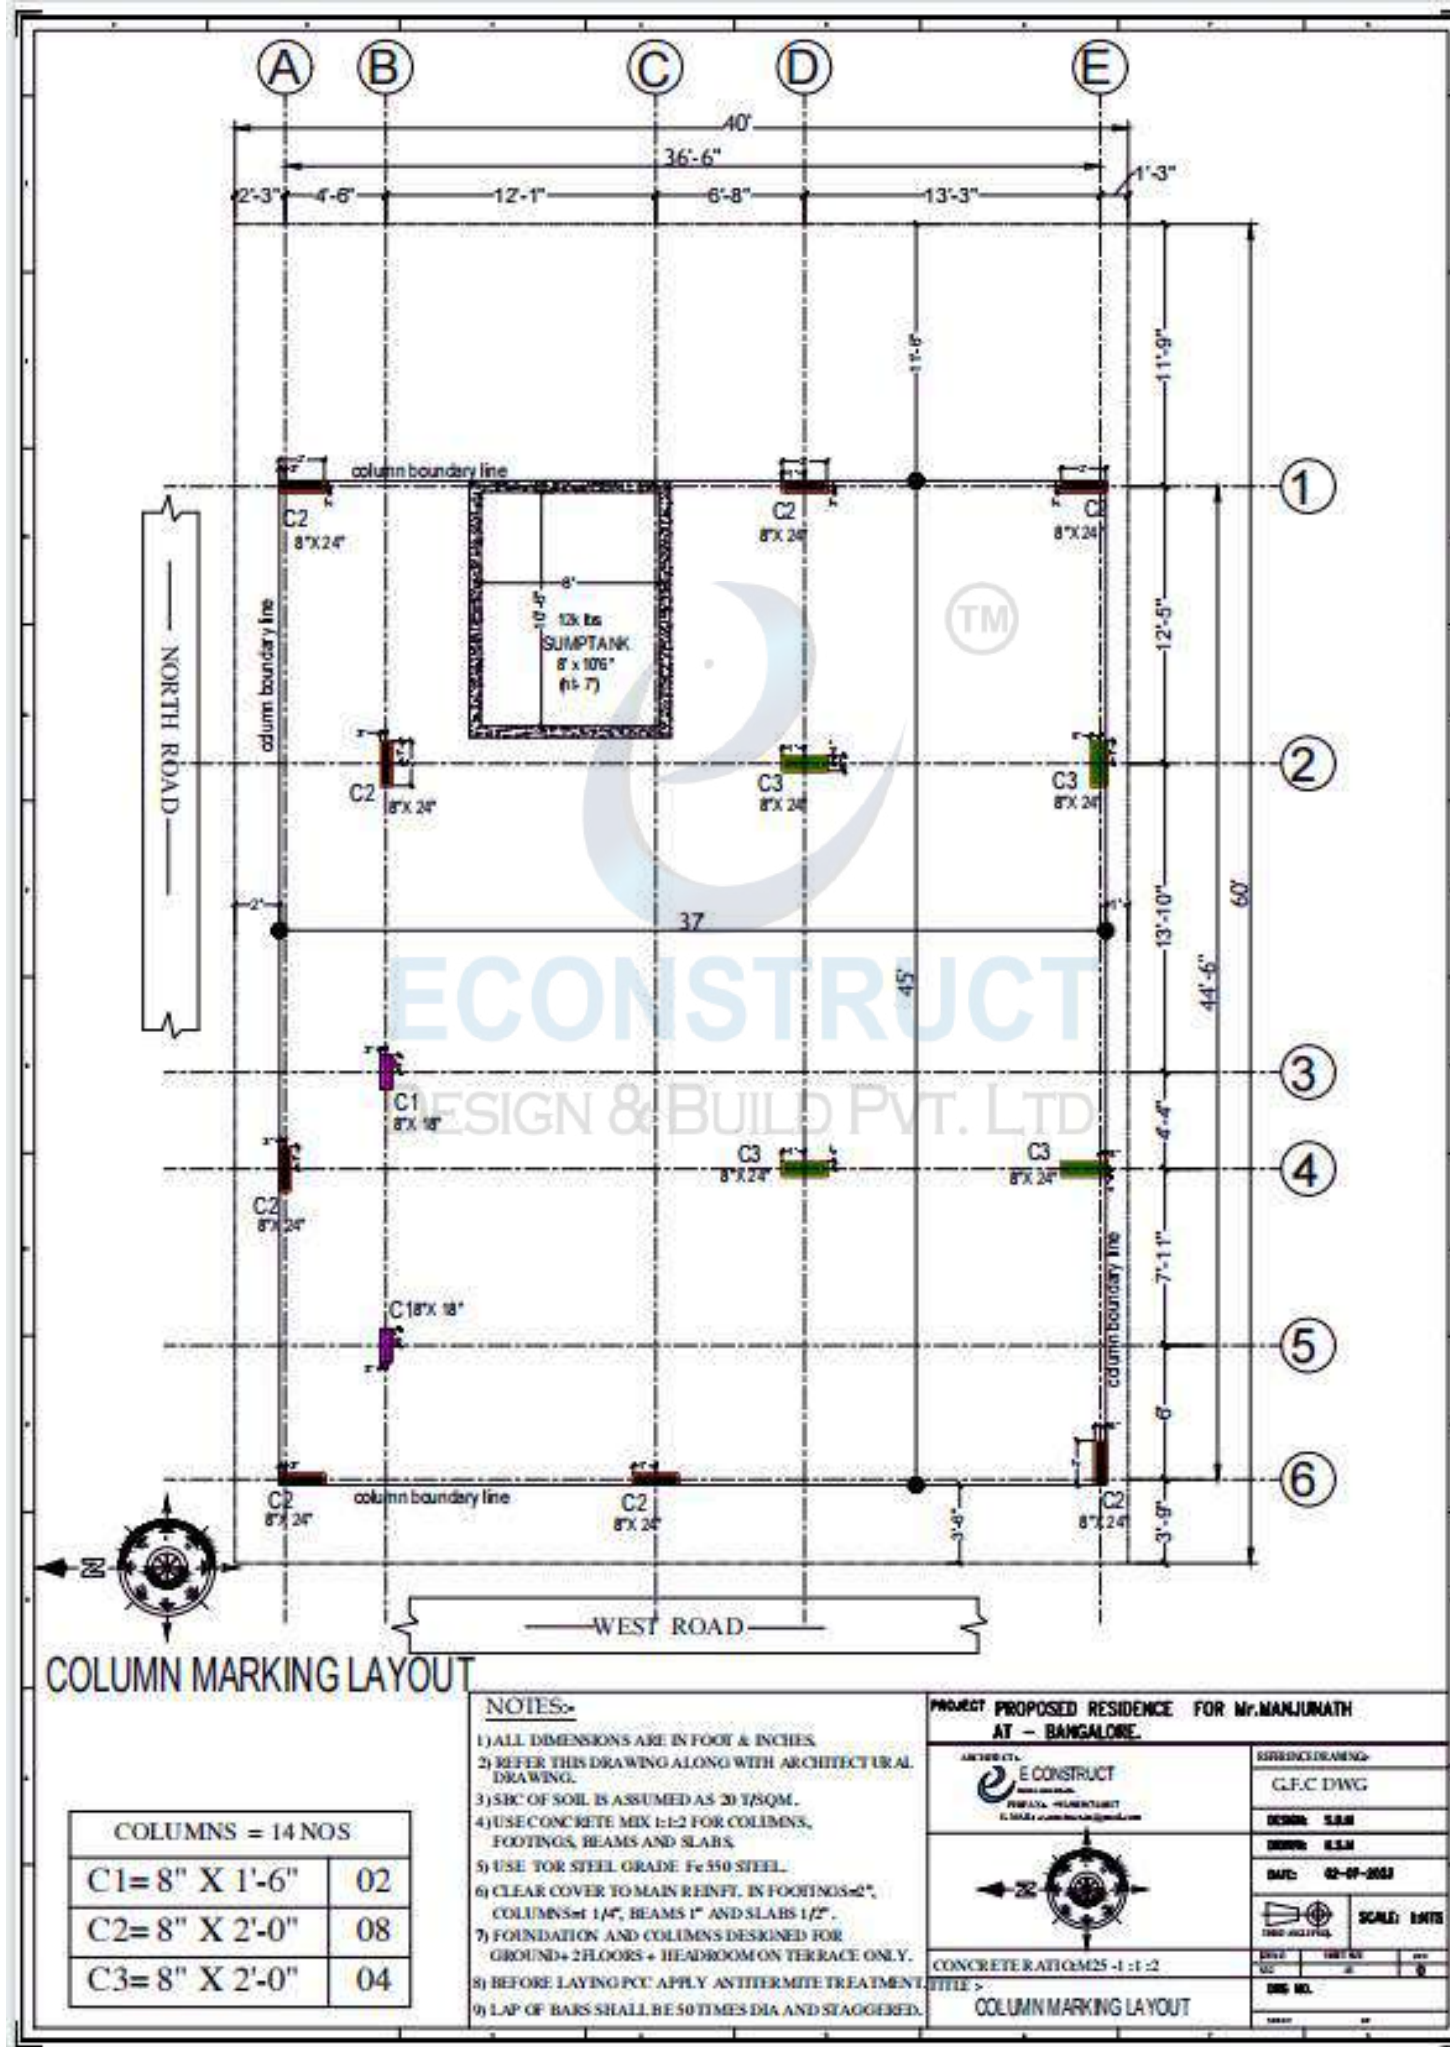

02

FOOTING MARKING LAYOUT

03

COLUMN & FOOTING RC DETAILS

SCHEDULE OF FOOTINGS

TYPE	SIZE OF FOOTING L X W	DEPTH D	REINFORCEMENT	
			SHORT BAR a	LONG BAR b
F1	4'-6" X 5'-6"	18"	10# @ 6"	10# @ 6"
F2	5'-6" X 7'-0"	20"	10# @ 6"	10# @ 6"
F3	8'-0" X 6'-8"	24"	10# @ 5"	10# @ 5"
SF	sumptank	12"	10# @ 8"	10# @ 8"
CF	as per dwg	24"	10# @ 5"	10# @ 5"
ONLY FOR CF FOOTING DOUBLE MAT (REFER DETAIL-A)				

COLUMNS = 14 NOS

C1= 8" X 1'-6"	02
C2= 8" X 2'-0"	08
C3= 8" X 2'-0"	04

SCHEDULE OF COLUMNS

COL. NOS	COLUMN SIZE	GROUND FLOOR	FIRST FLOOR	SECOND FLOOR
C1 2 NOS	8" X 18"			CANCEL FROM SECOND FLOOR
C2 8 NOS	8" X 24"		NO CHANGE	
C3 4 NOS	8" X 24"		NO CHANGE	NO CHANGE
GRADE OF CONCRETE	—	M25	M25	M25

COLUMN & FOOTING RC DETAILS

NOTES:-


- 1) ALL DIMENSIONS ARE IN FOOT & INCHES.
- 2) REFER THIS DRAWING ALONG WITH ARCHITECTURAL DRAWING.
- 3) SBC OF SOIL IS ASSUMED AS 20 T/SQM.
- 4) USE CONCRETE MIX 1:1:2 FOR COLUMNS, FOOTINGS, BEAMS AND SLABS.
- 5) USE TOR STEEL GRADE Fe 550 STEEL.
- 6) CLEAR COVER TO MAIN REINFT. IN FOOTINGS=2", COLUMNS=1 1/4", BEAMS 1" AND SLABS 1/2".
- 7) FOUNDATION AND COLUMNS DESIGNED FOR GROUND+2 FLOORS + HEADROOM ON TERRACE ONLY.
- 8) BEFORE LAYING PCC APPLY ANTITERMITE TREATMENT.
- 9) LAP OF BARS SHALL BE 50 TIMES DIA AND STAGGERED.

PROJECT PROPOSED RESIDENCE FOR Mr. MANJUNATH
AT - BANGALORE.

 ARCHITECT: E CONSTRUCT PROJECT - 14081410017 14081410017@gmail.com	REFERENCE DRAWING:-
	G.F.C DWG
	DESIGN: S.B.M
	DRAWN: K.S.M
 ARCHITECT: E CONSTRUCT PROJECT - 14081410017 14081410017@gmail.com	DATE: 02-07-2023
	SCALE: 1/16"
	DATE: 02-07-2023
	SCALE: 1/16"
CONCRETE RATIO M25 - 1:1:2 TITLE: >	DATE: 02-07-2023
	SCALE: 1/16"
	DATE: 02-07-2023
	SCALE: 1/16"

PEDESTAL REINFORCEMENT

COLUMN SIZE	PEDESTAL SIZE	PEDESTAL REINFORCEMENT
8" X 18"	14" X 24" HT-TILL PLINTH BEAM	 4 NOS X12# 2L-8# @ 8" C/C
8" X 24"	14" X 30" HT-TILL PLINTH BEAM	 6 NOS X12# 2L-8# @ 8" C/C
8" X 24"	14" X 30" HT-TILL PLINTH BEAM	 6 NOS X12# 2L-8# @ 8" C/C

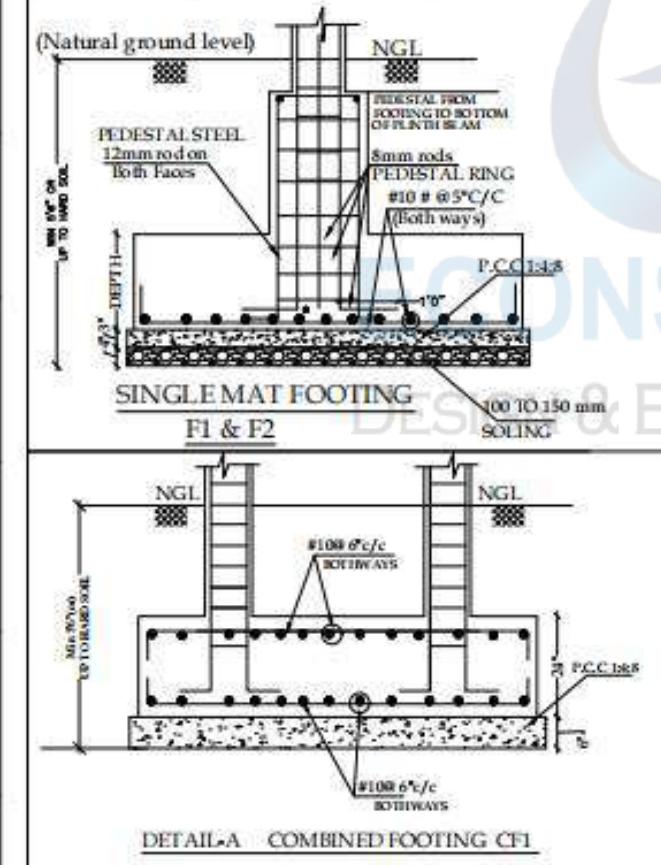

PEDESTAL DETAILS & FOOTING SECTION


NOTES:-

- 1) ALL DIMENSIONS ARE IN FOOT & INCHES.
- 2) REFER THIS DRAWING ALONG WITH ARCHITECTURAL DRAWING.
- 3) SBC OF SOIL IS ASSUMED AS 20 T/SQM.
- 4) USE CONCRETE MIX 1:1:2 FOR COLUMNS, FOOTINGS, BEAMS AND SLABS.
- 5) USE TOR STEEL GRADE Fe 550 STEEL.
- 6) CLEAR COVER TO MAIN REINFT. IN FOOTINGS=2", COLUMNS=1 1/4", BEAMS 1" AND SLABS 1/2".
- 7) FOUNDATION AND COLUMNS DESIGNED FOR GROUND+2 FLOORS + HEADROOM ON TERRACE ONLY.
- 8) BEFORE LAYING PCC APPLY ANTITERMITE TREATMENT.
- 9) LAP OF BARS SHALL BE 50 TIMES DIA AND STAGGERED.

PROJECT PROPOSED RESIDENCE FOR Mr. MANJUNATH
AT - BANGALORE.

 ARCHITECT: E CONSTRUCT PROJECT - 14081410017 14081410017@gmail.com	REFERENCE DRAWING:-
	G.F.C DWG
	DESIGN: S.B.M
	DRAWN: K.S.M
 ARCHITECT: E CONSTRUCT PROJECT - 14081410017 14081410017@gmail.com	DATE: 02-07-2023
	SCALE: 1/16"
	DATE: 02-07-2023
	SCALE: 1/16"
CONCRETE RATIO M25 - 1:1:2 TITLE: >	DATE: 02-07-2023
	SCALE: 1/16"
	DATE: 02-07-2023
	SCALE: 1/16"


COLUMN LAP DETAIL

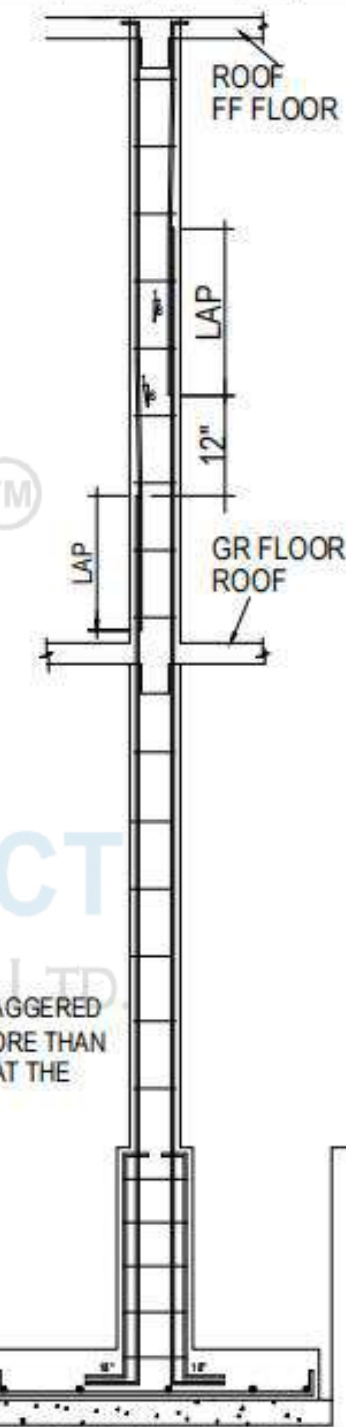


04

PEDESTAL REINFORCEMENT



05

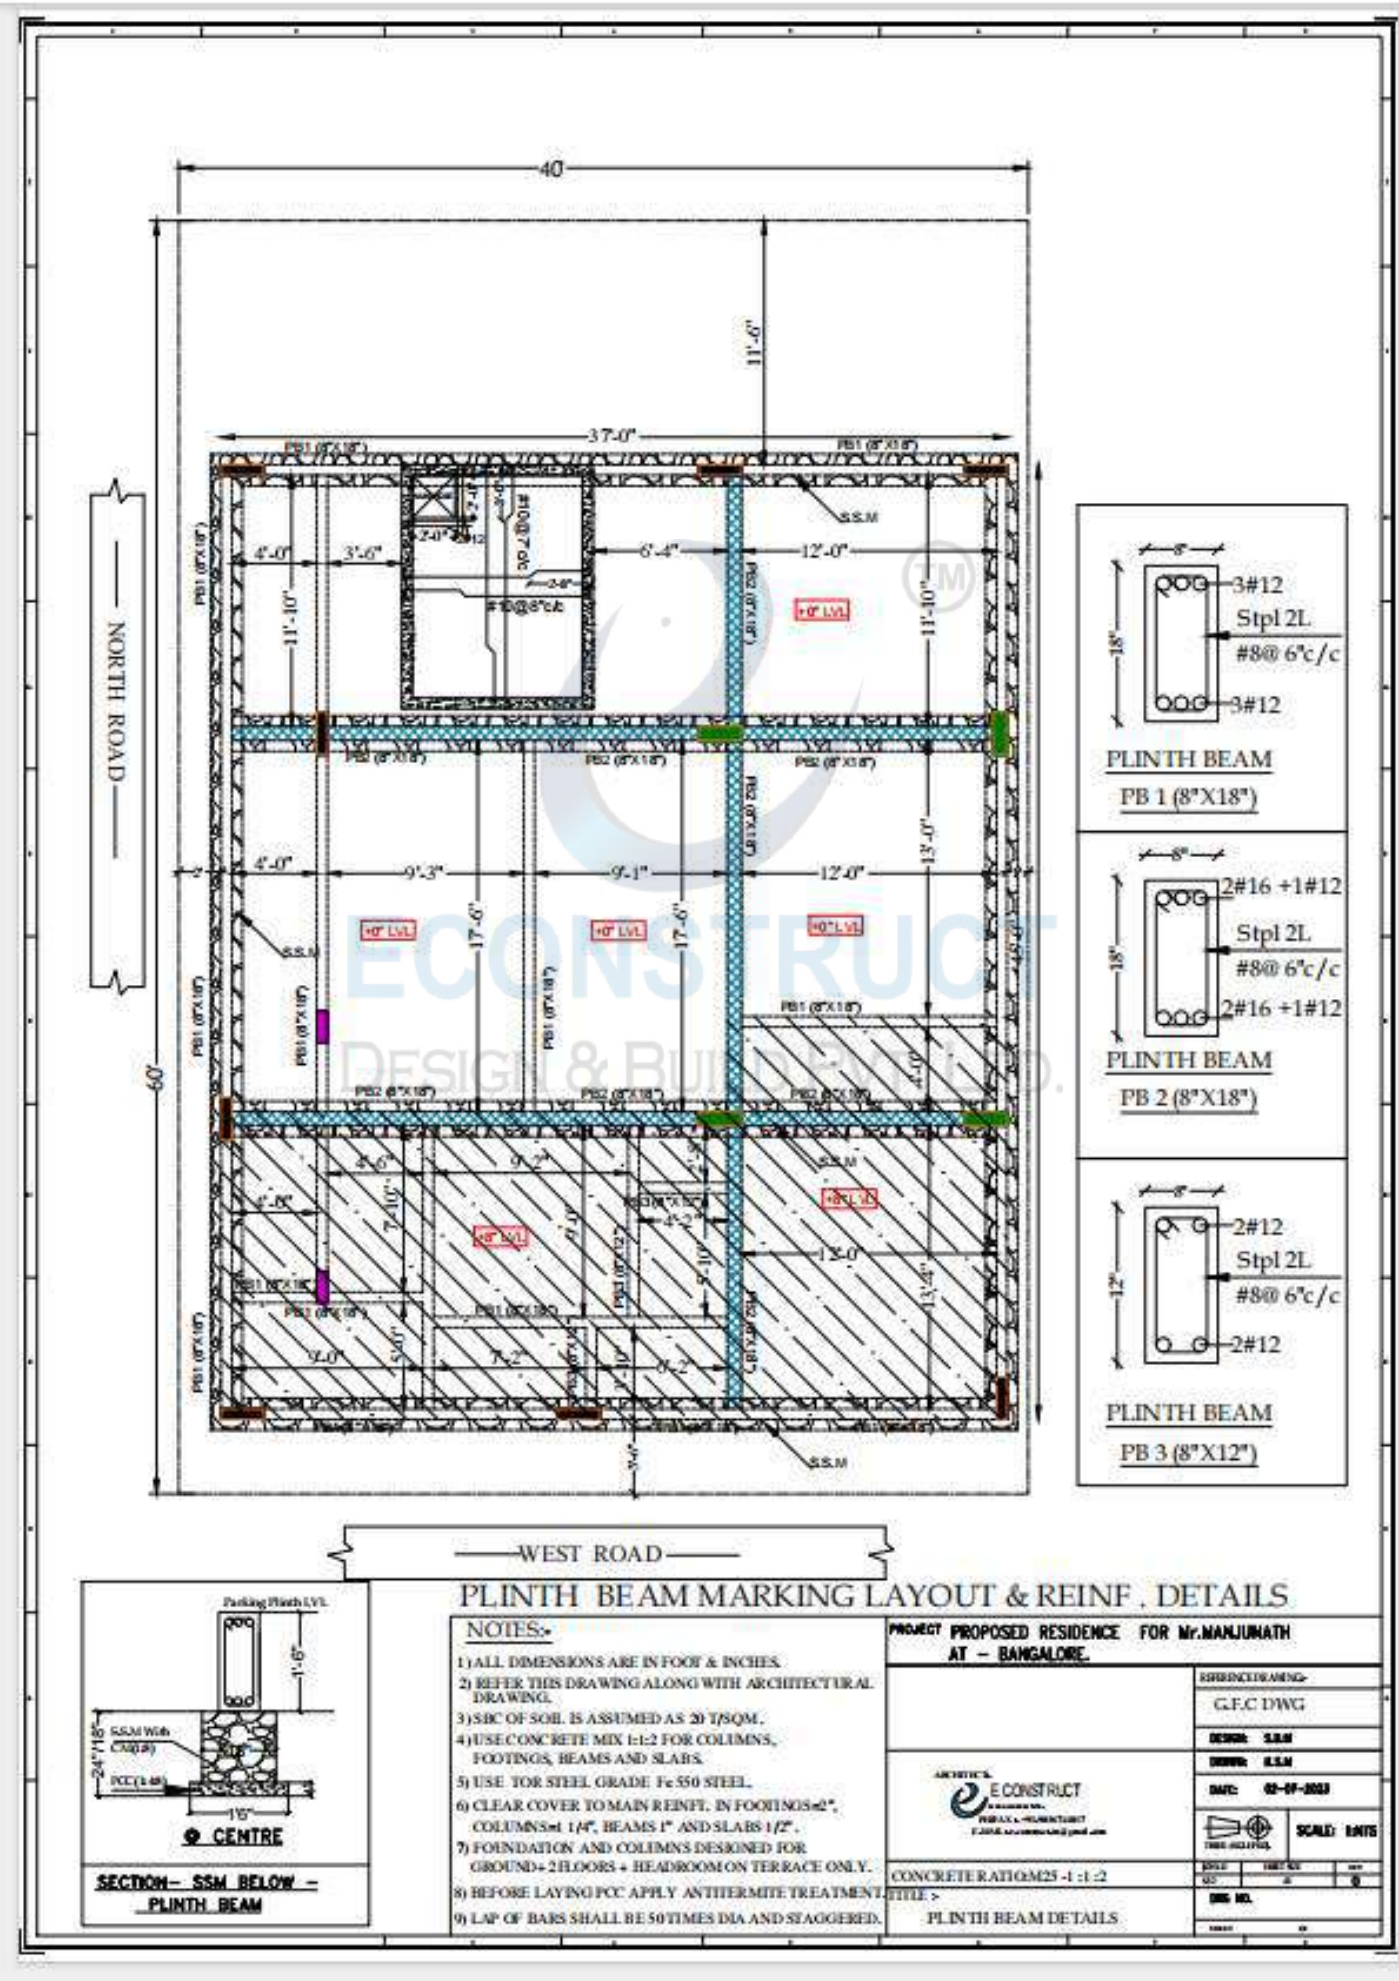PLINTH BEAM MARKING LAYOUT
& REINF. DETAILS

06


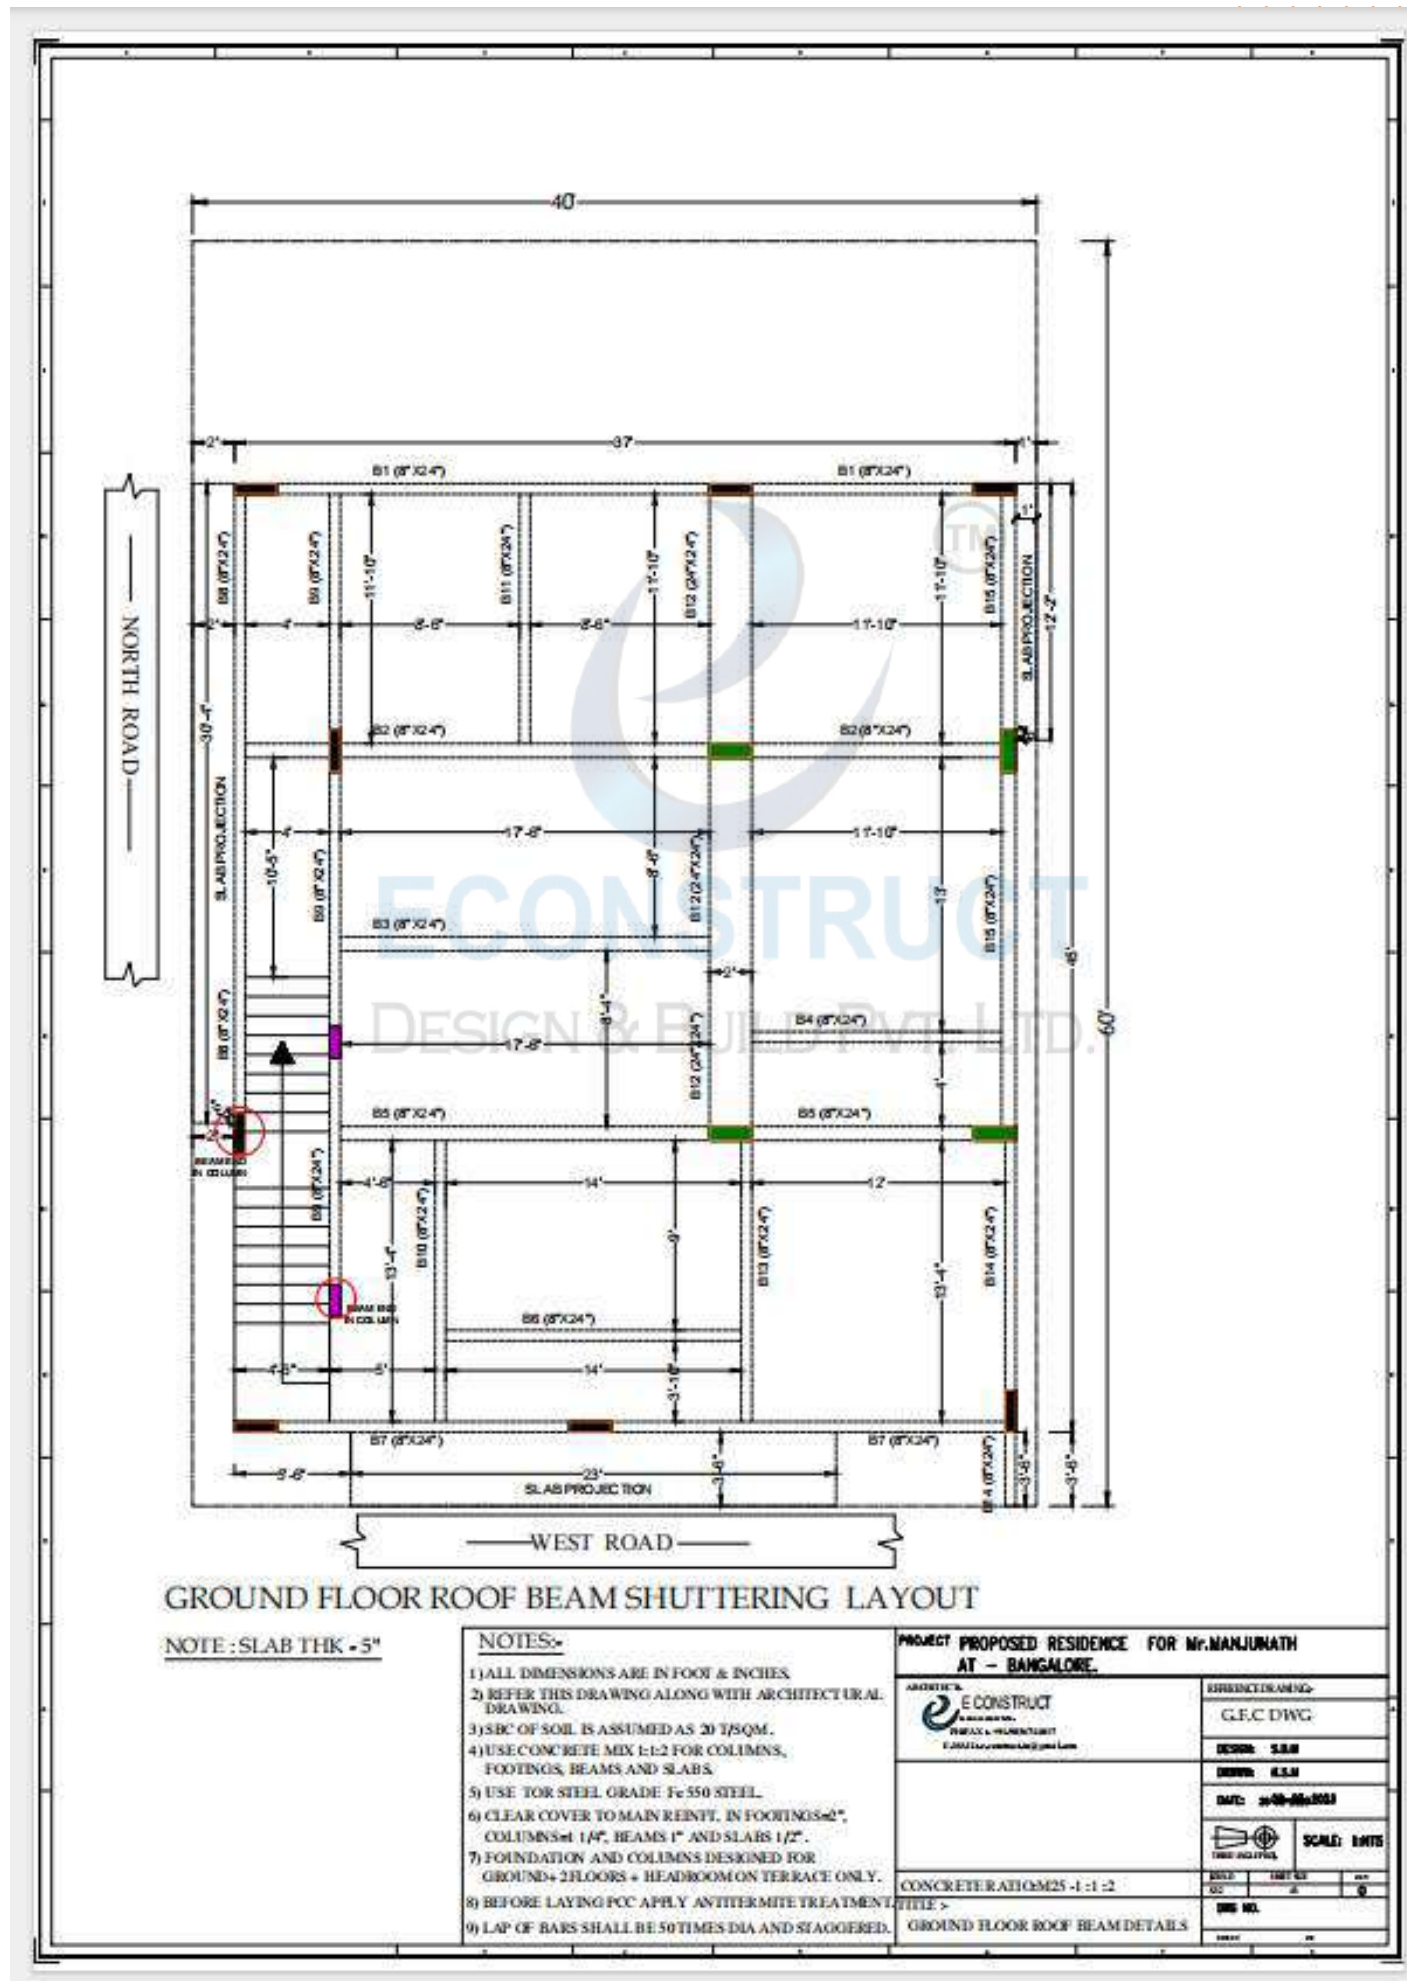
GROUND FLOOR ROOF BEAM
SHUTTERING LAYOUT

07

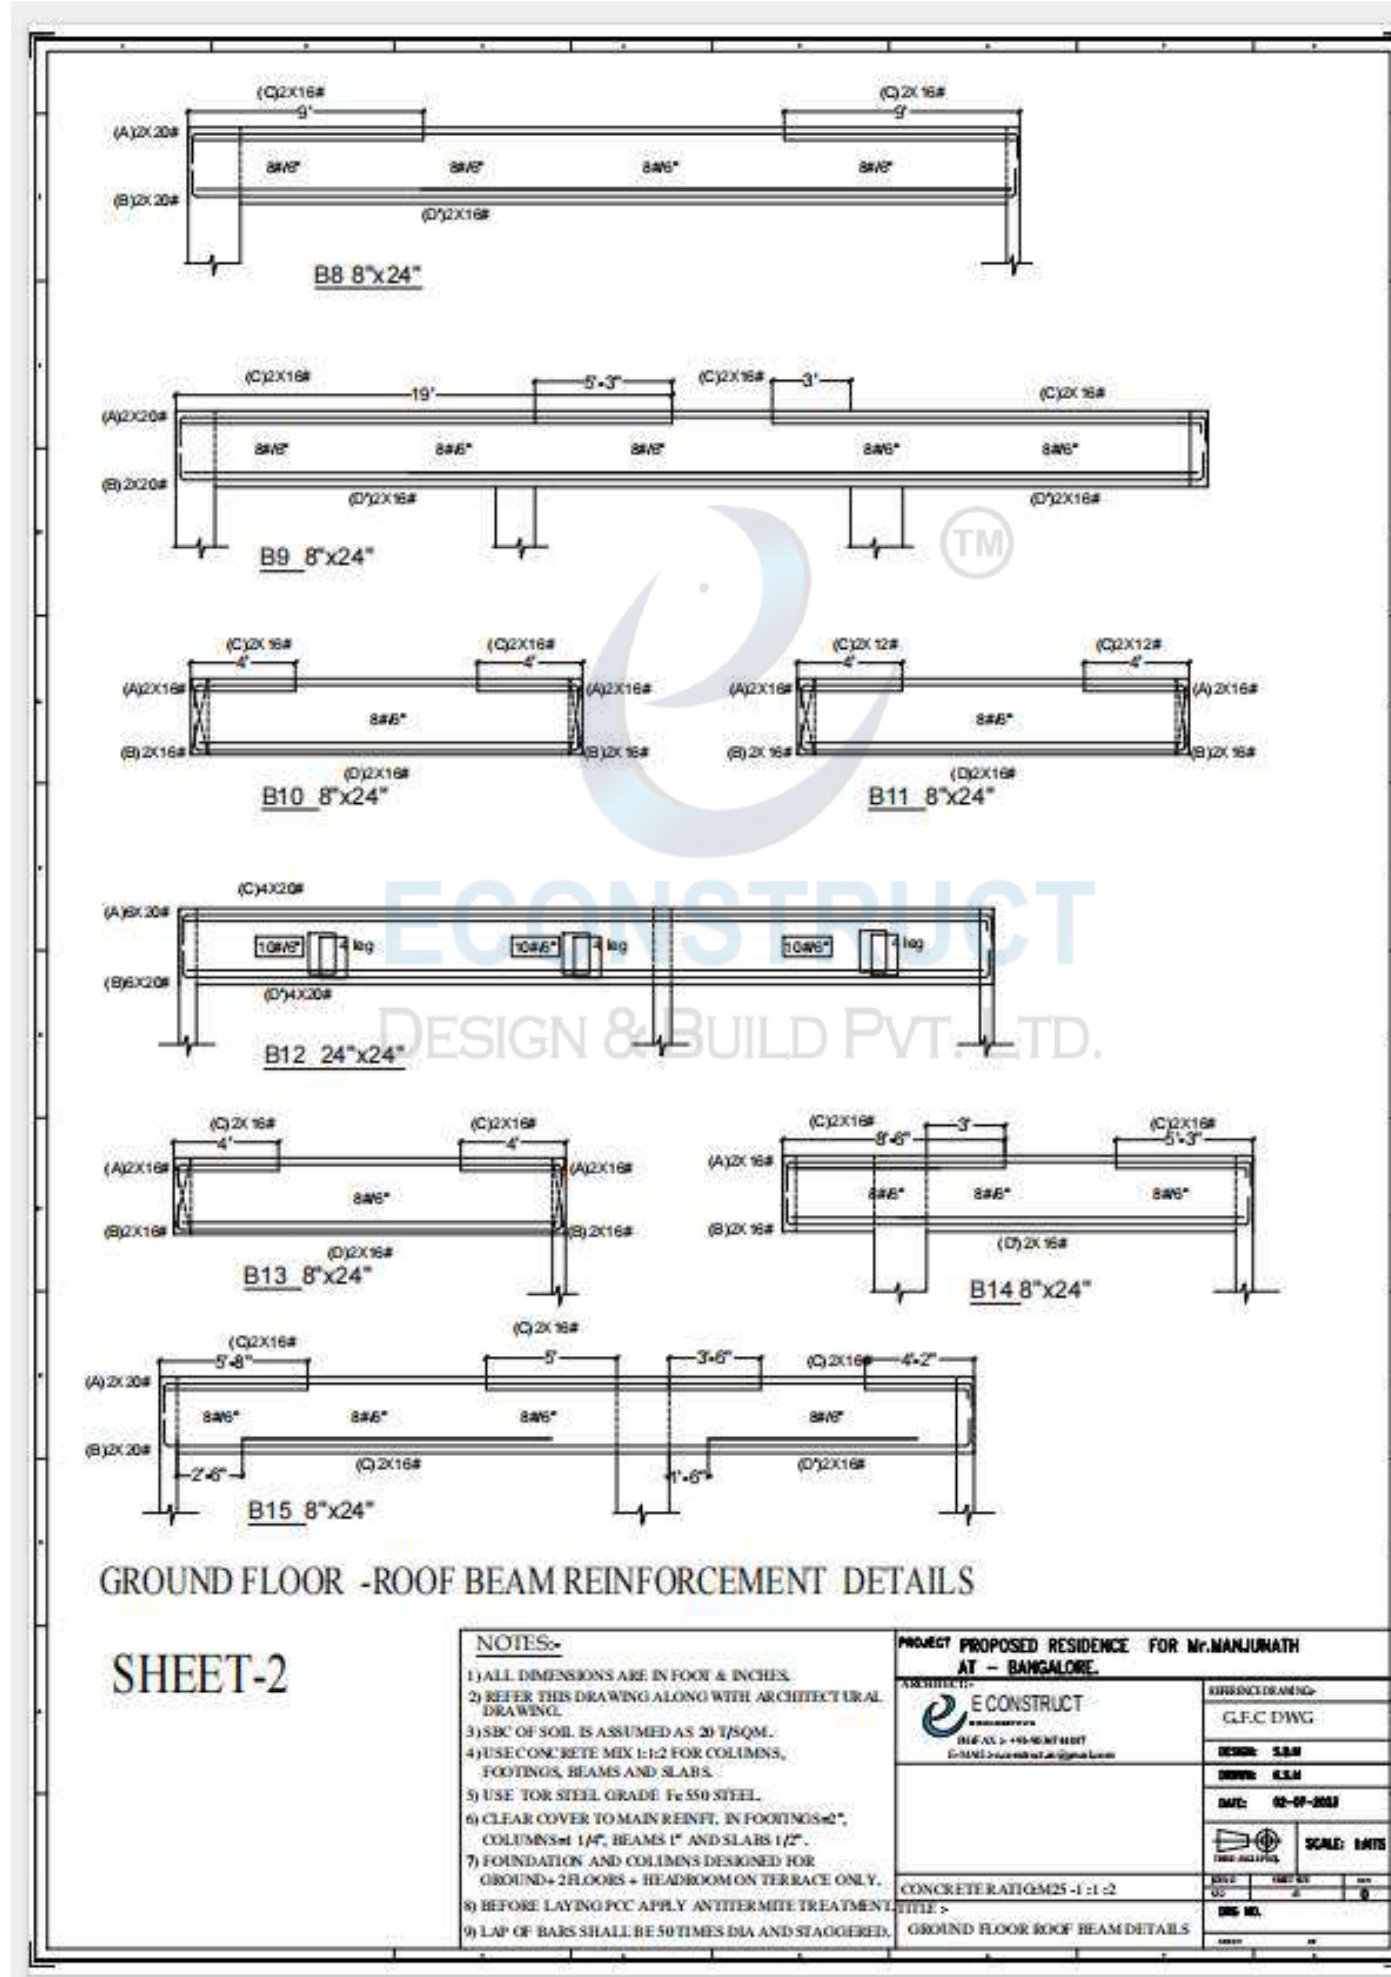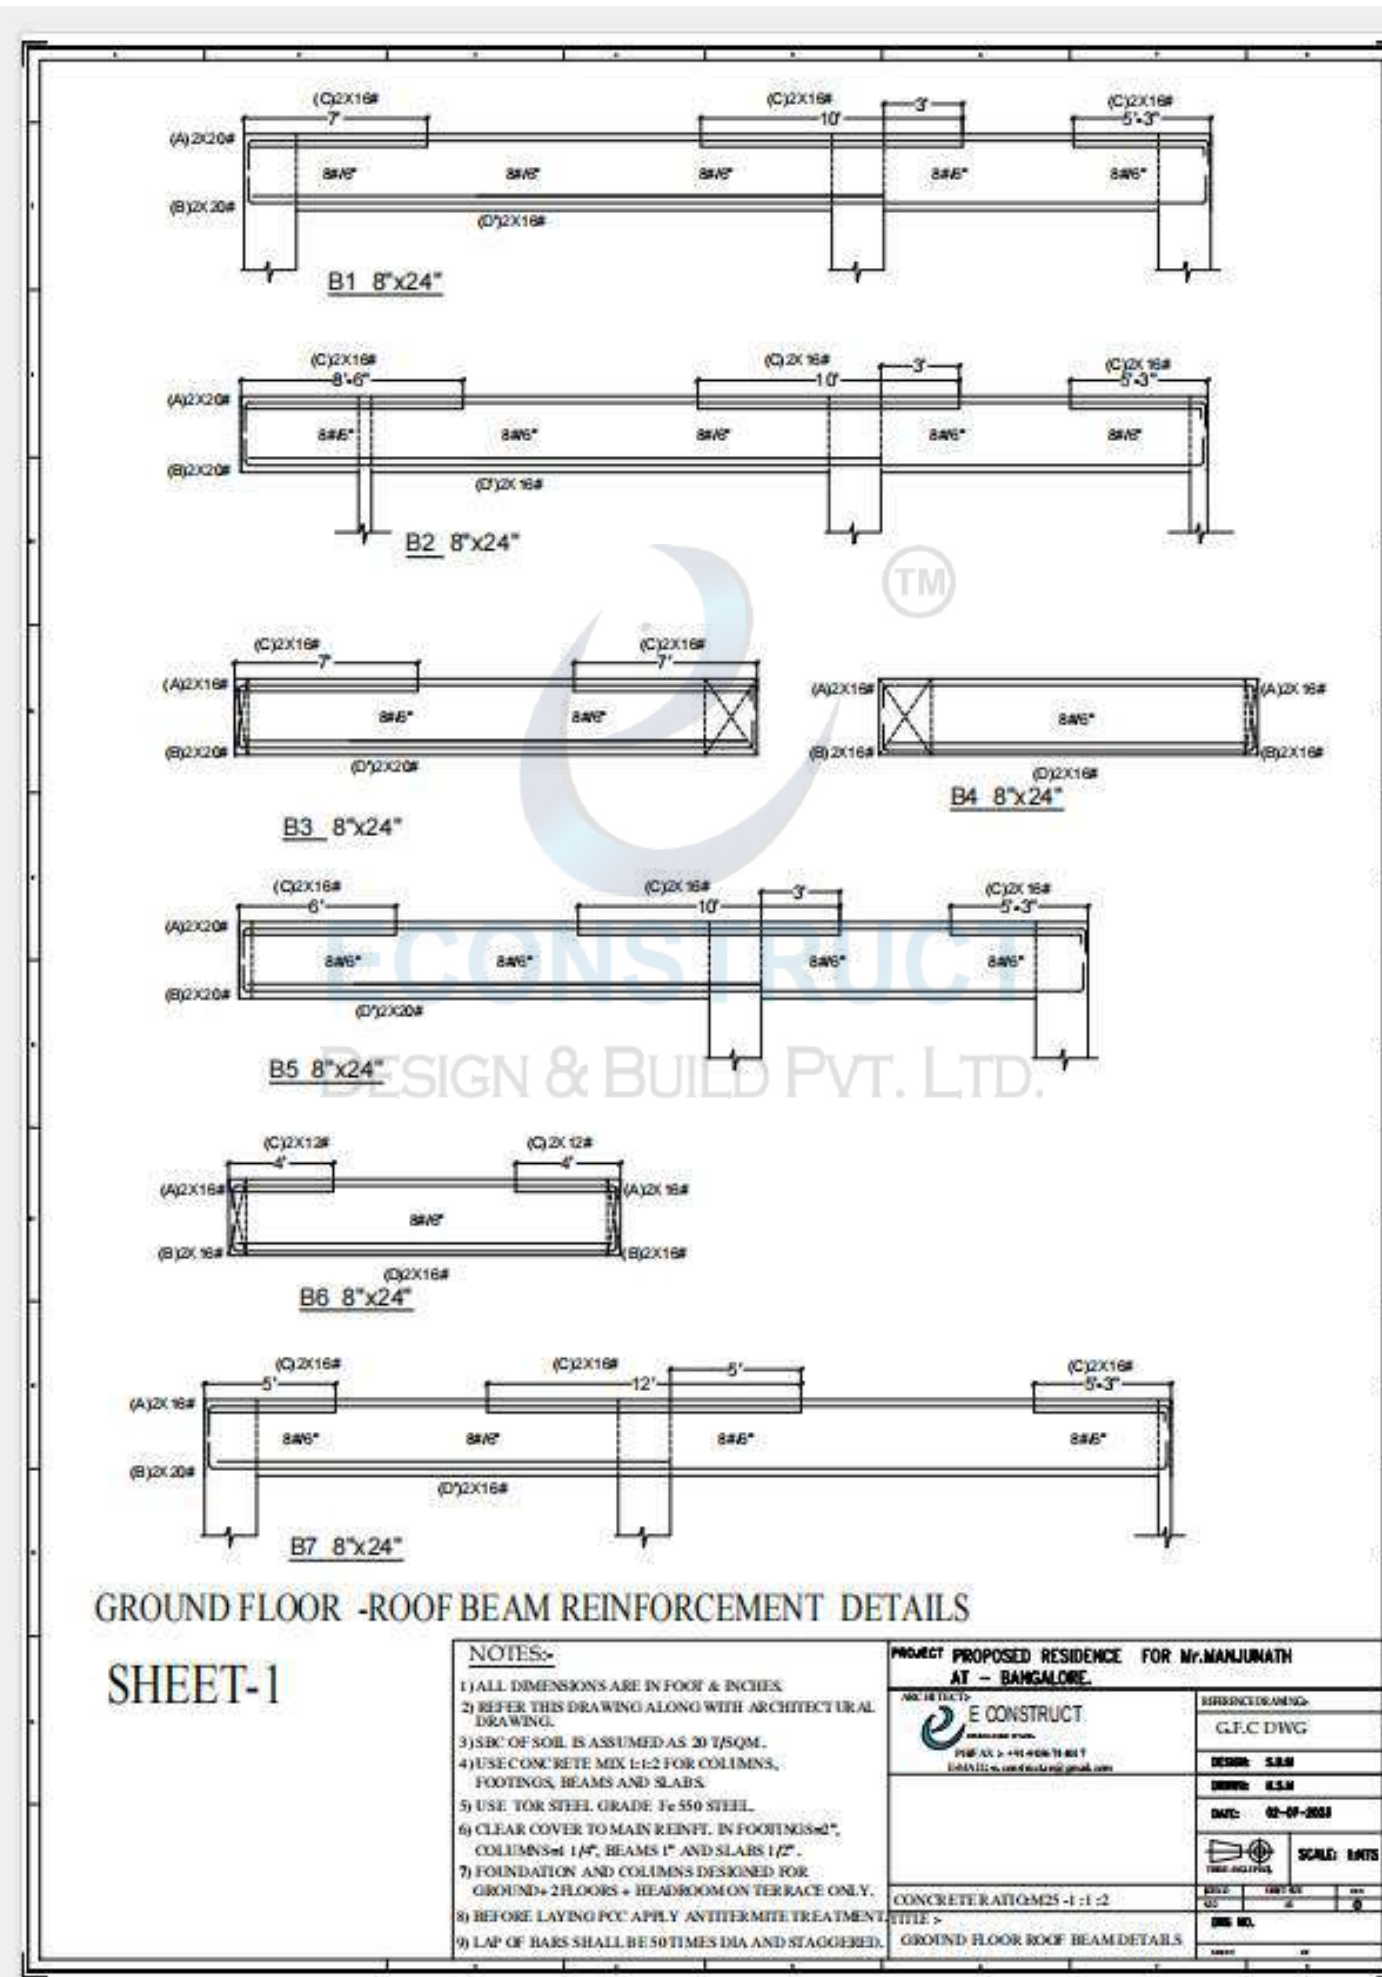GROUND FLOOR - ROOF BEAM
REINFORCEMENT DETAILS



08

GROUND FLOOR - ROOF BEAM
REINFORCEMENT DETAILS

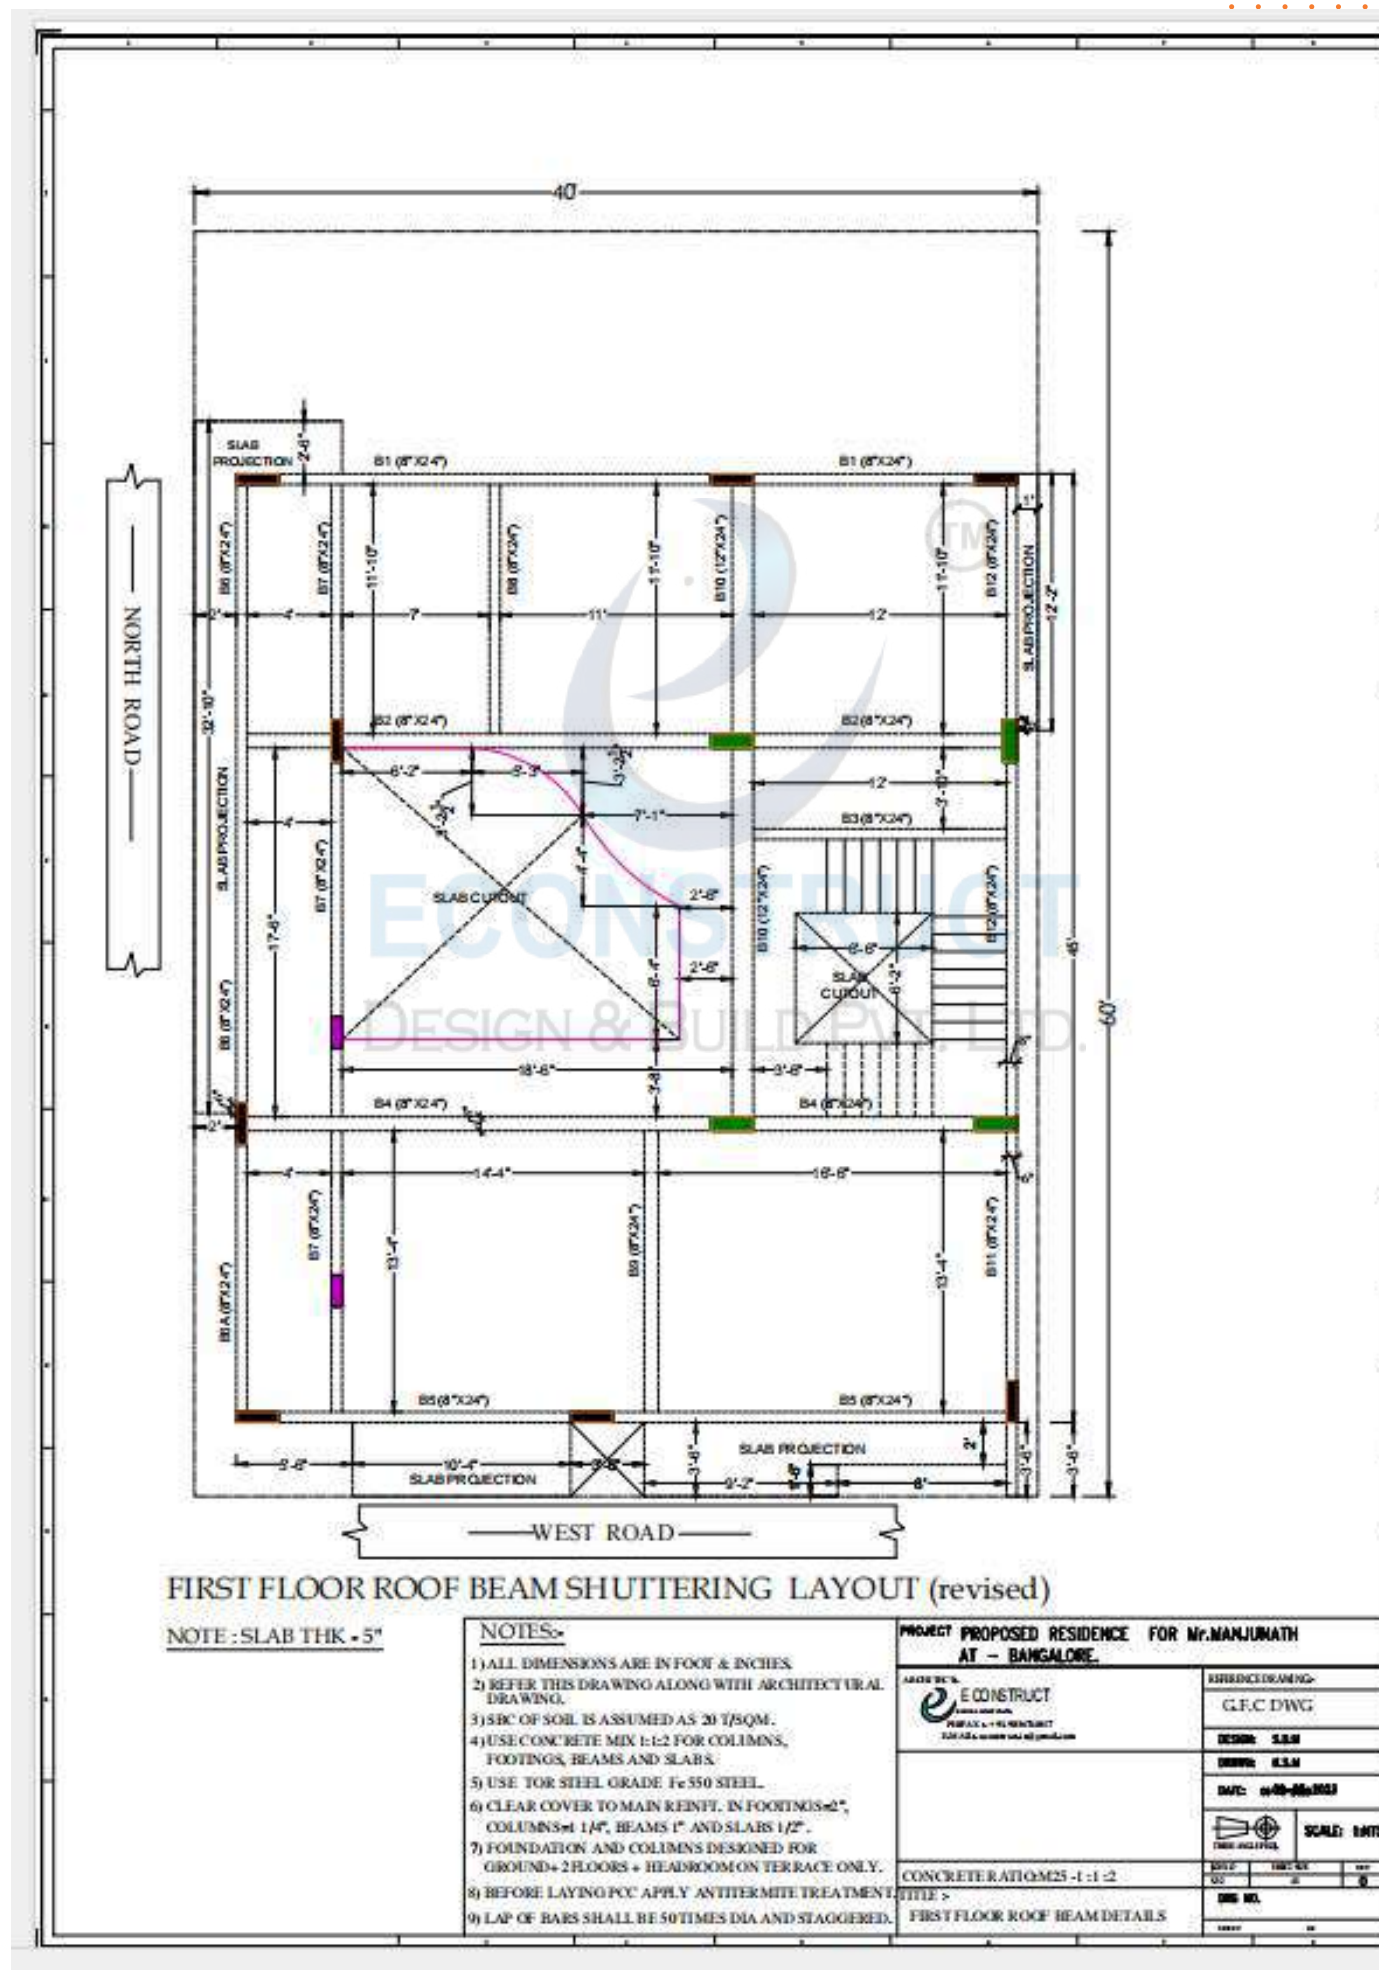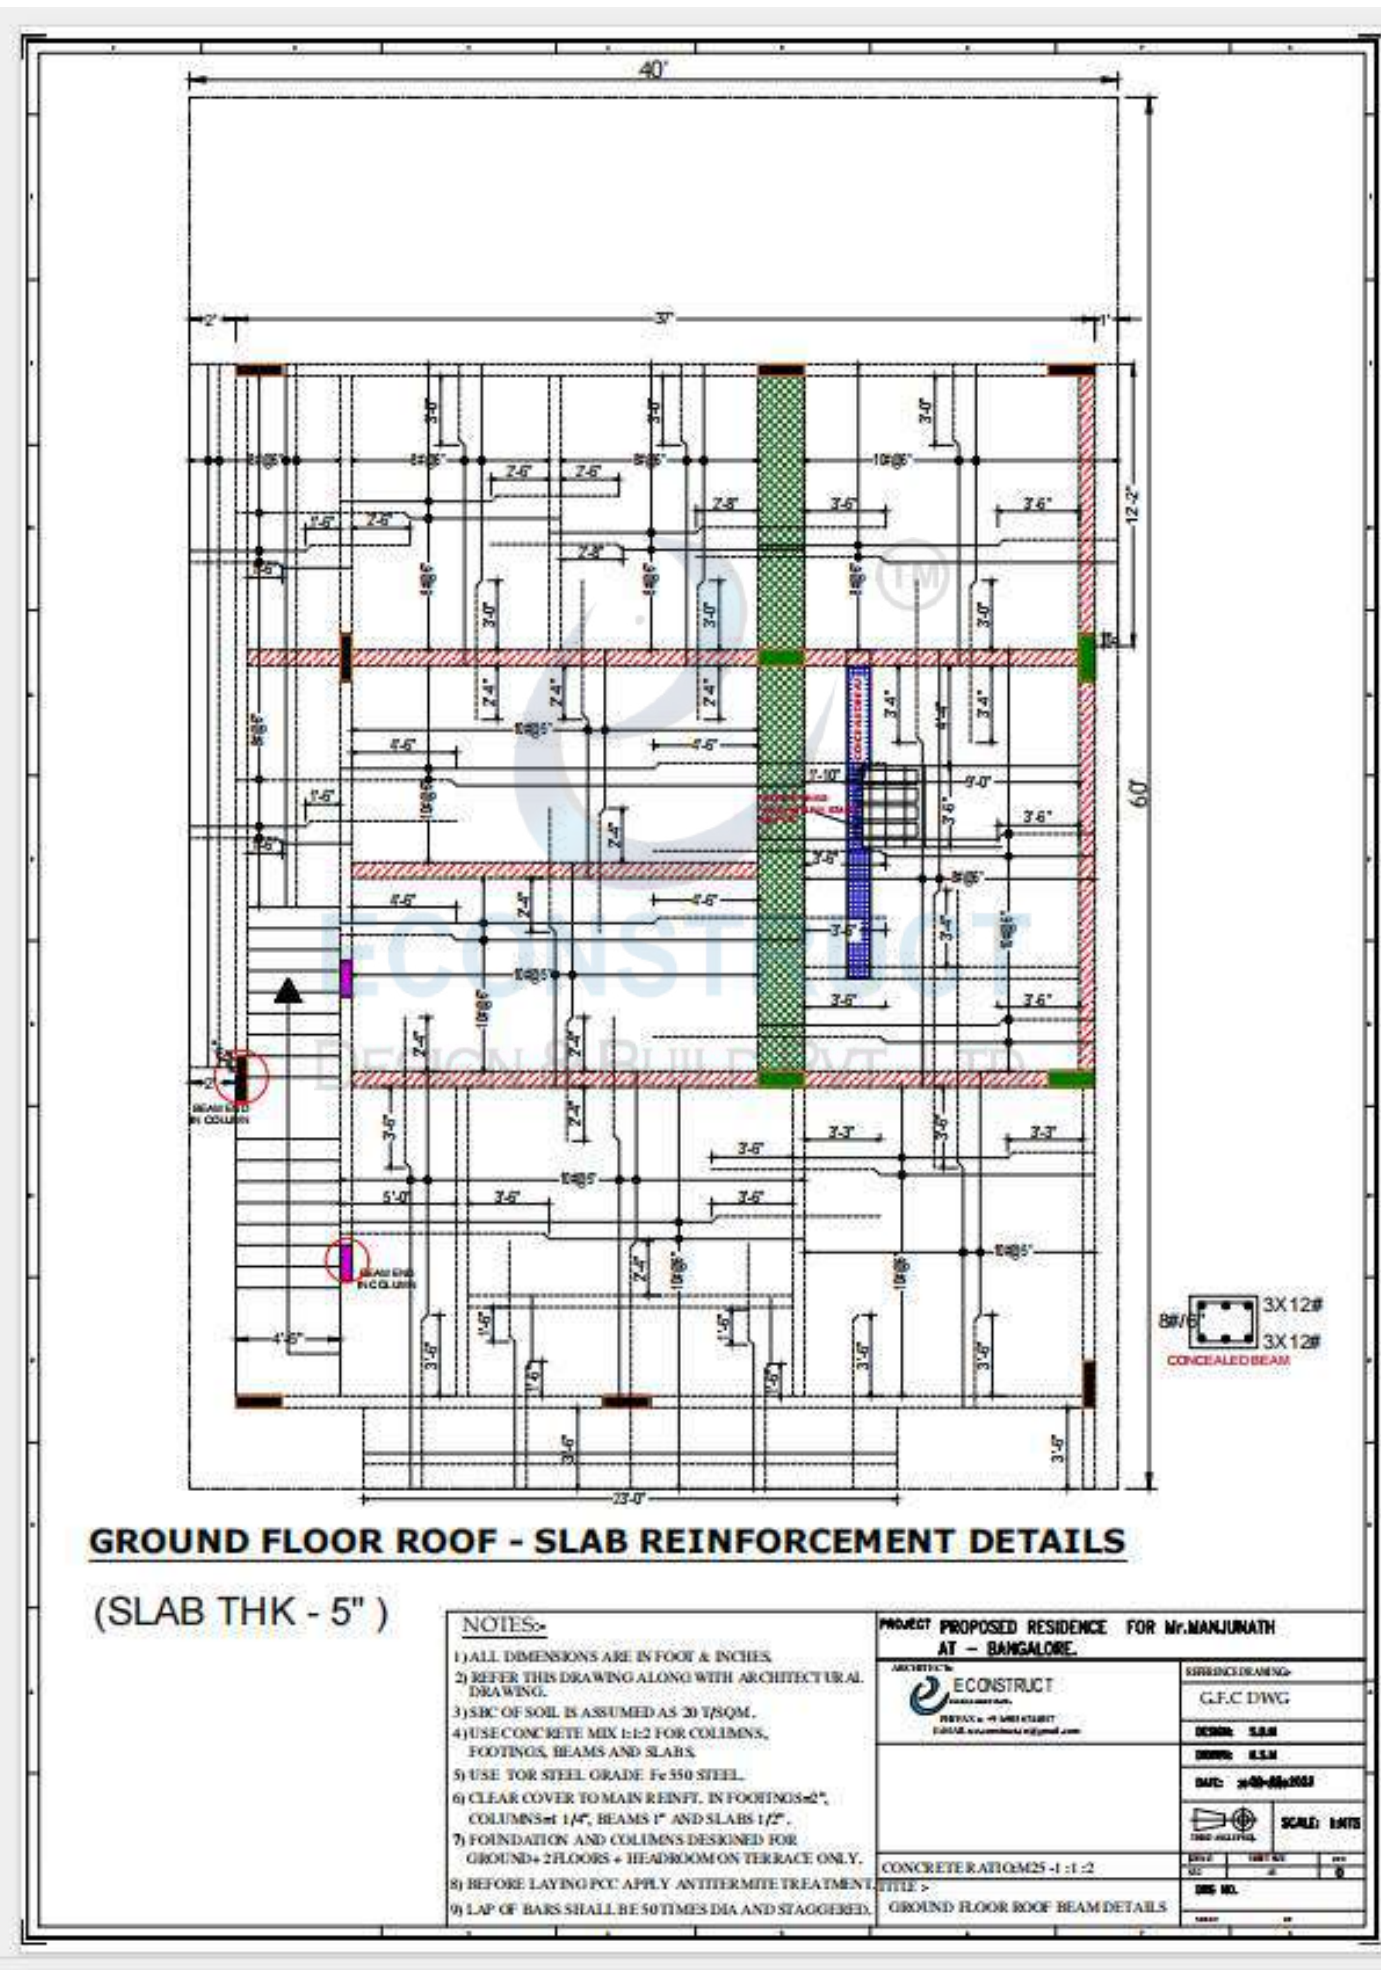

11

FIRST FLOOR - ROOF BEAM REINFORCEMENT DETAILS - SHEET-1

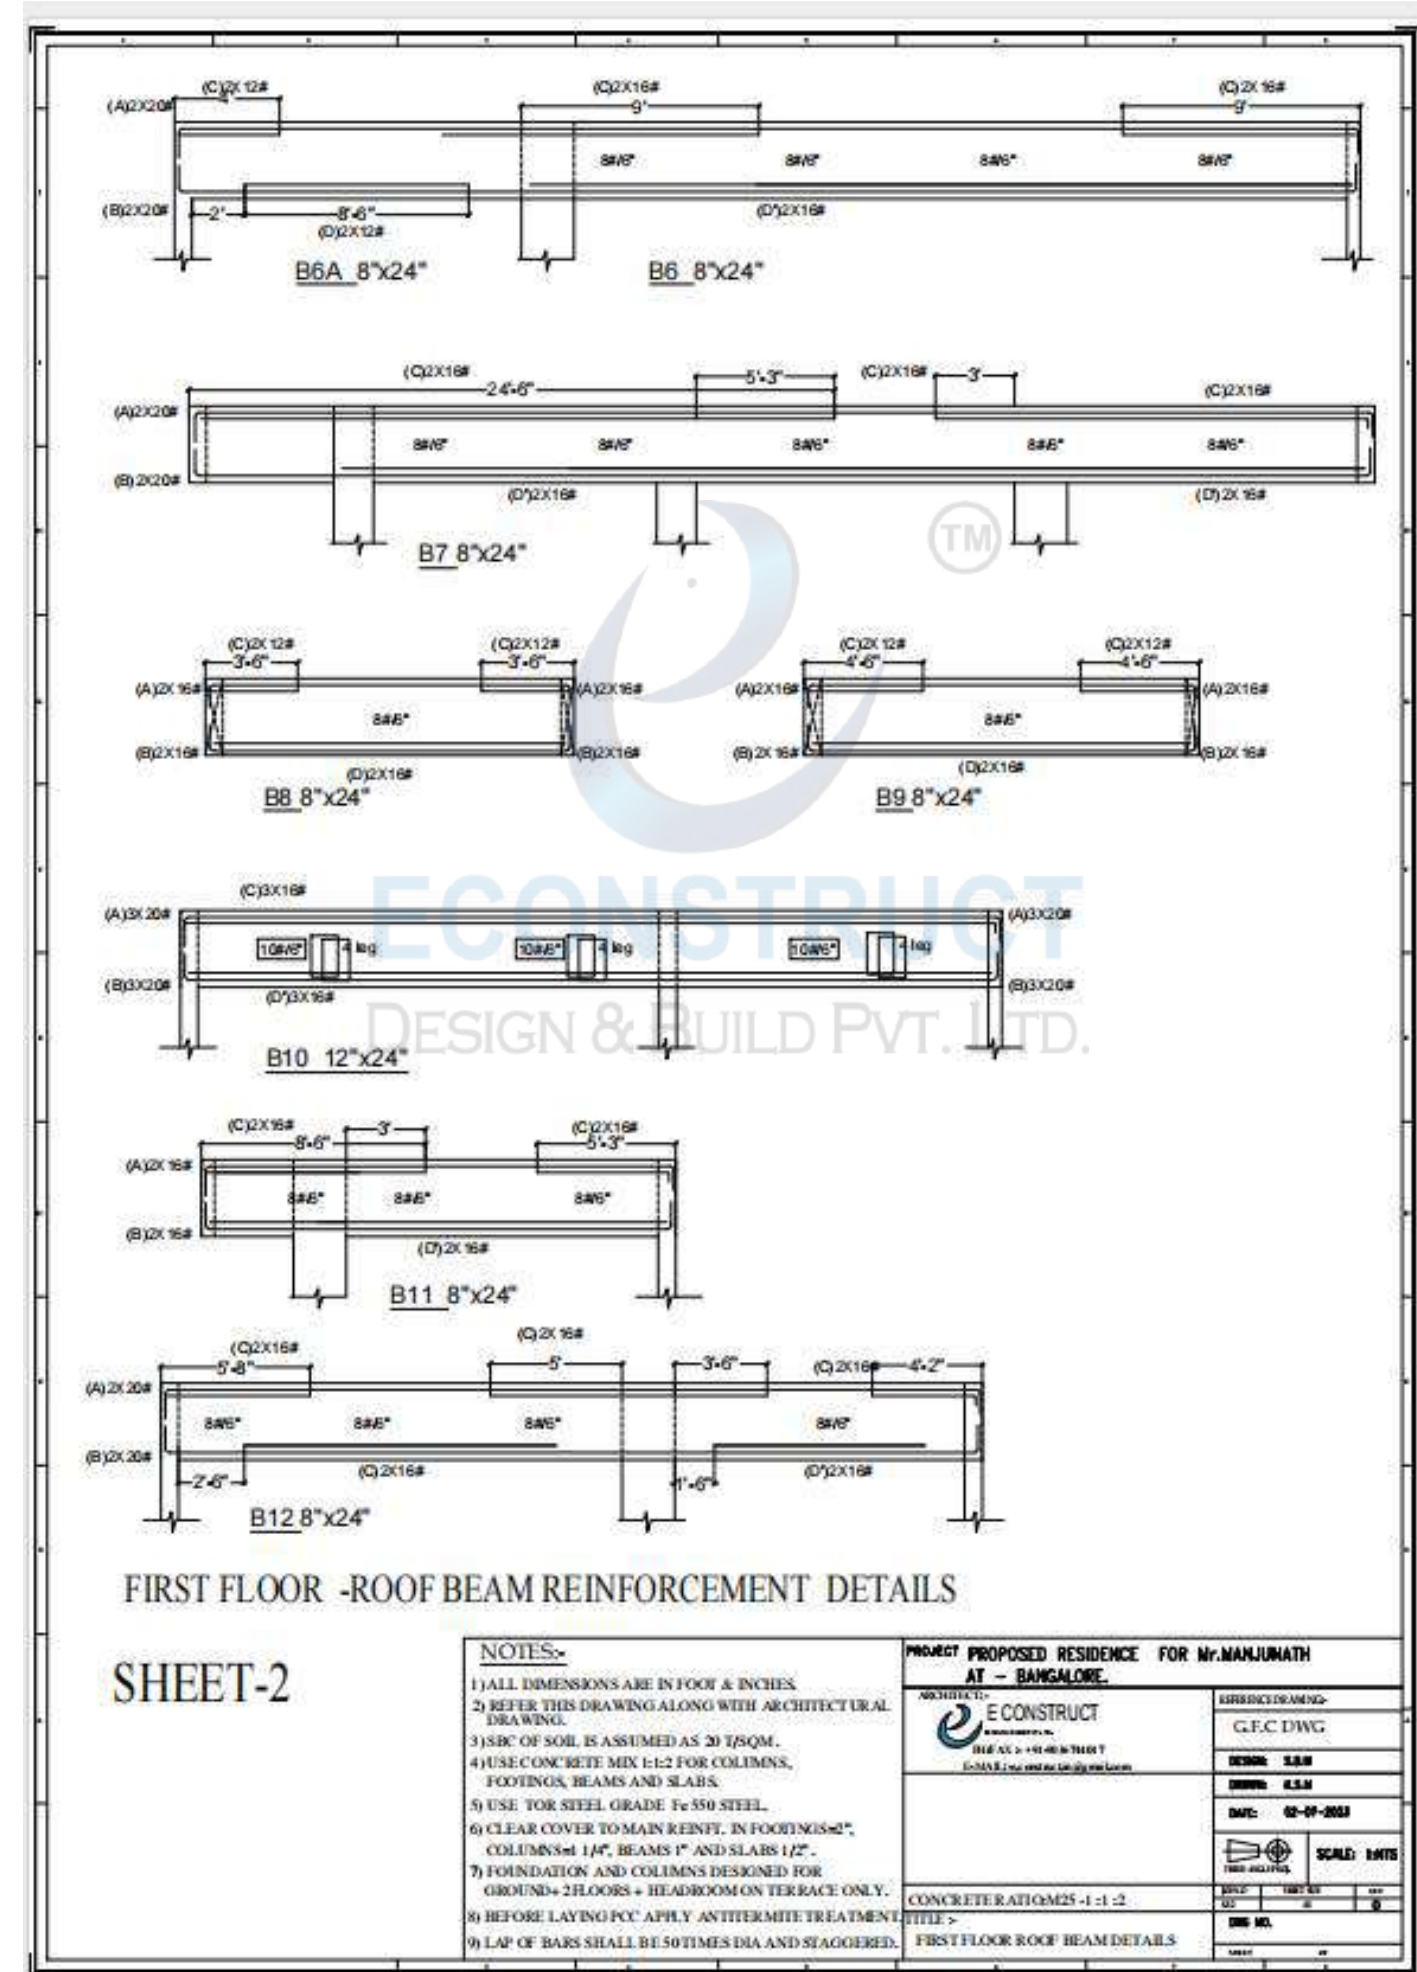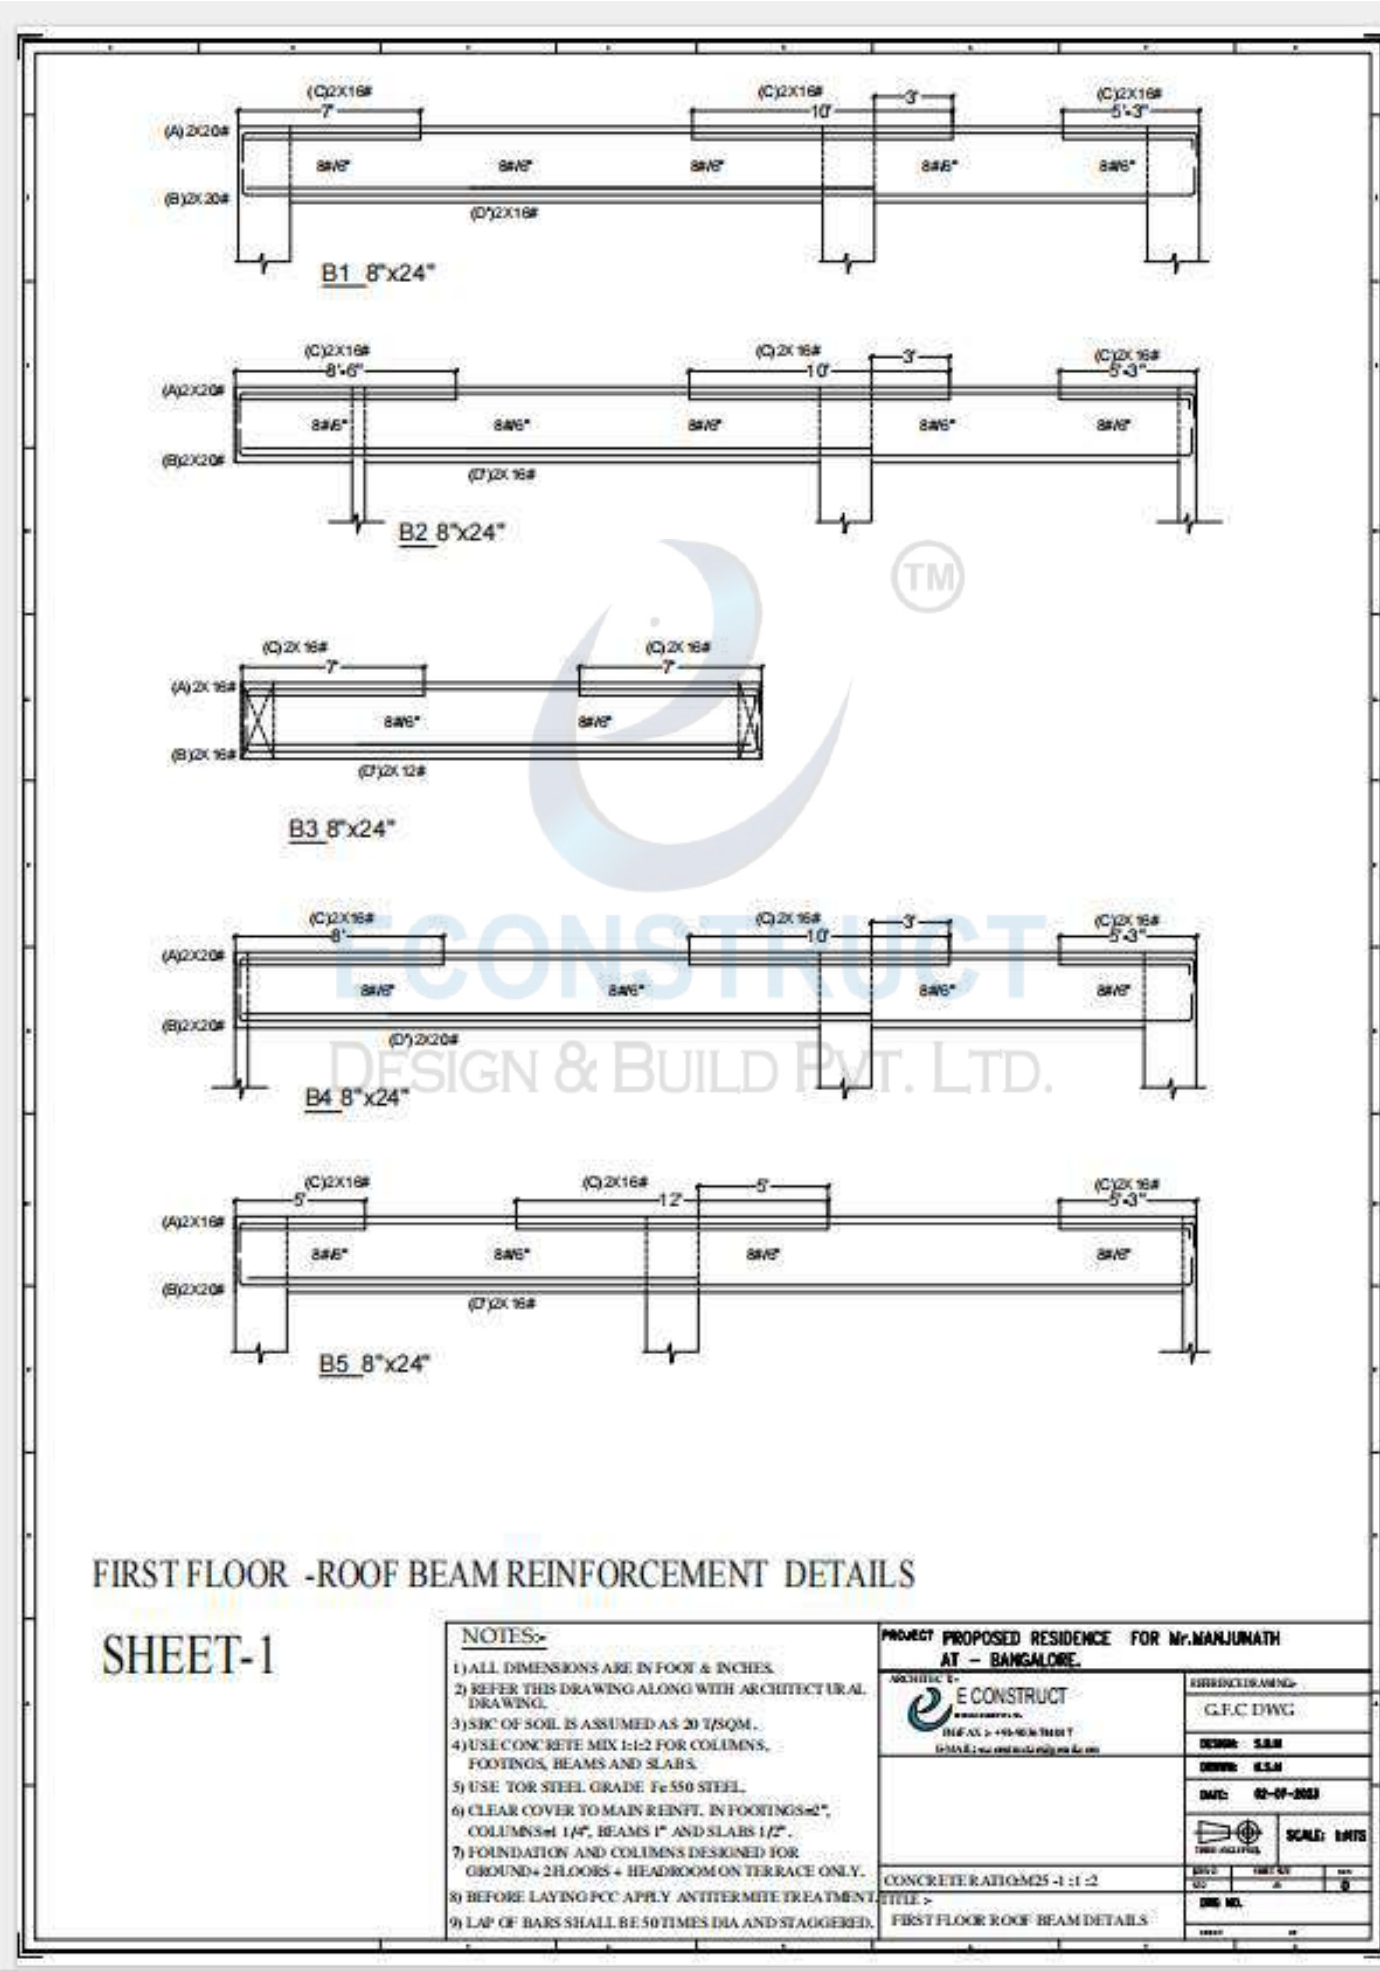


12

FIRST FLOOR - ROOF BEAM REINFORCEMENT DETAILS - SHEET-2


13

FIRST FLOOR ROOF - SLAB REINFORCEMENT DETAILS (REVISED)

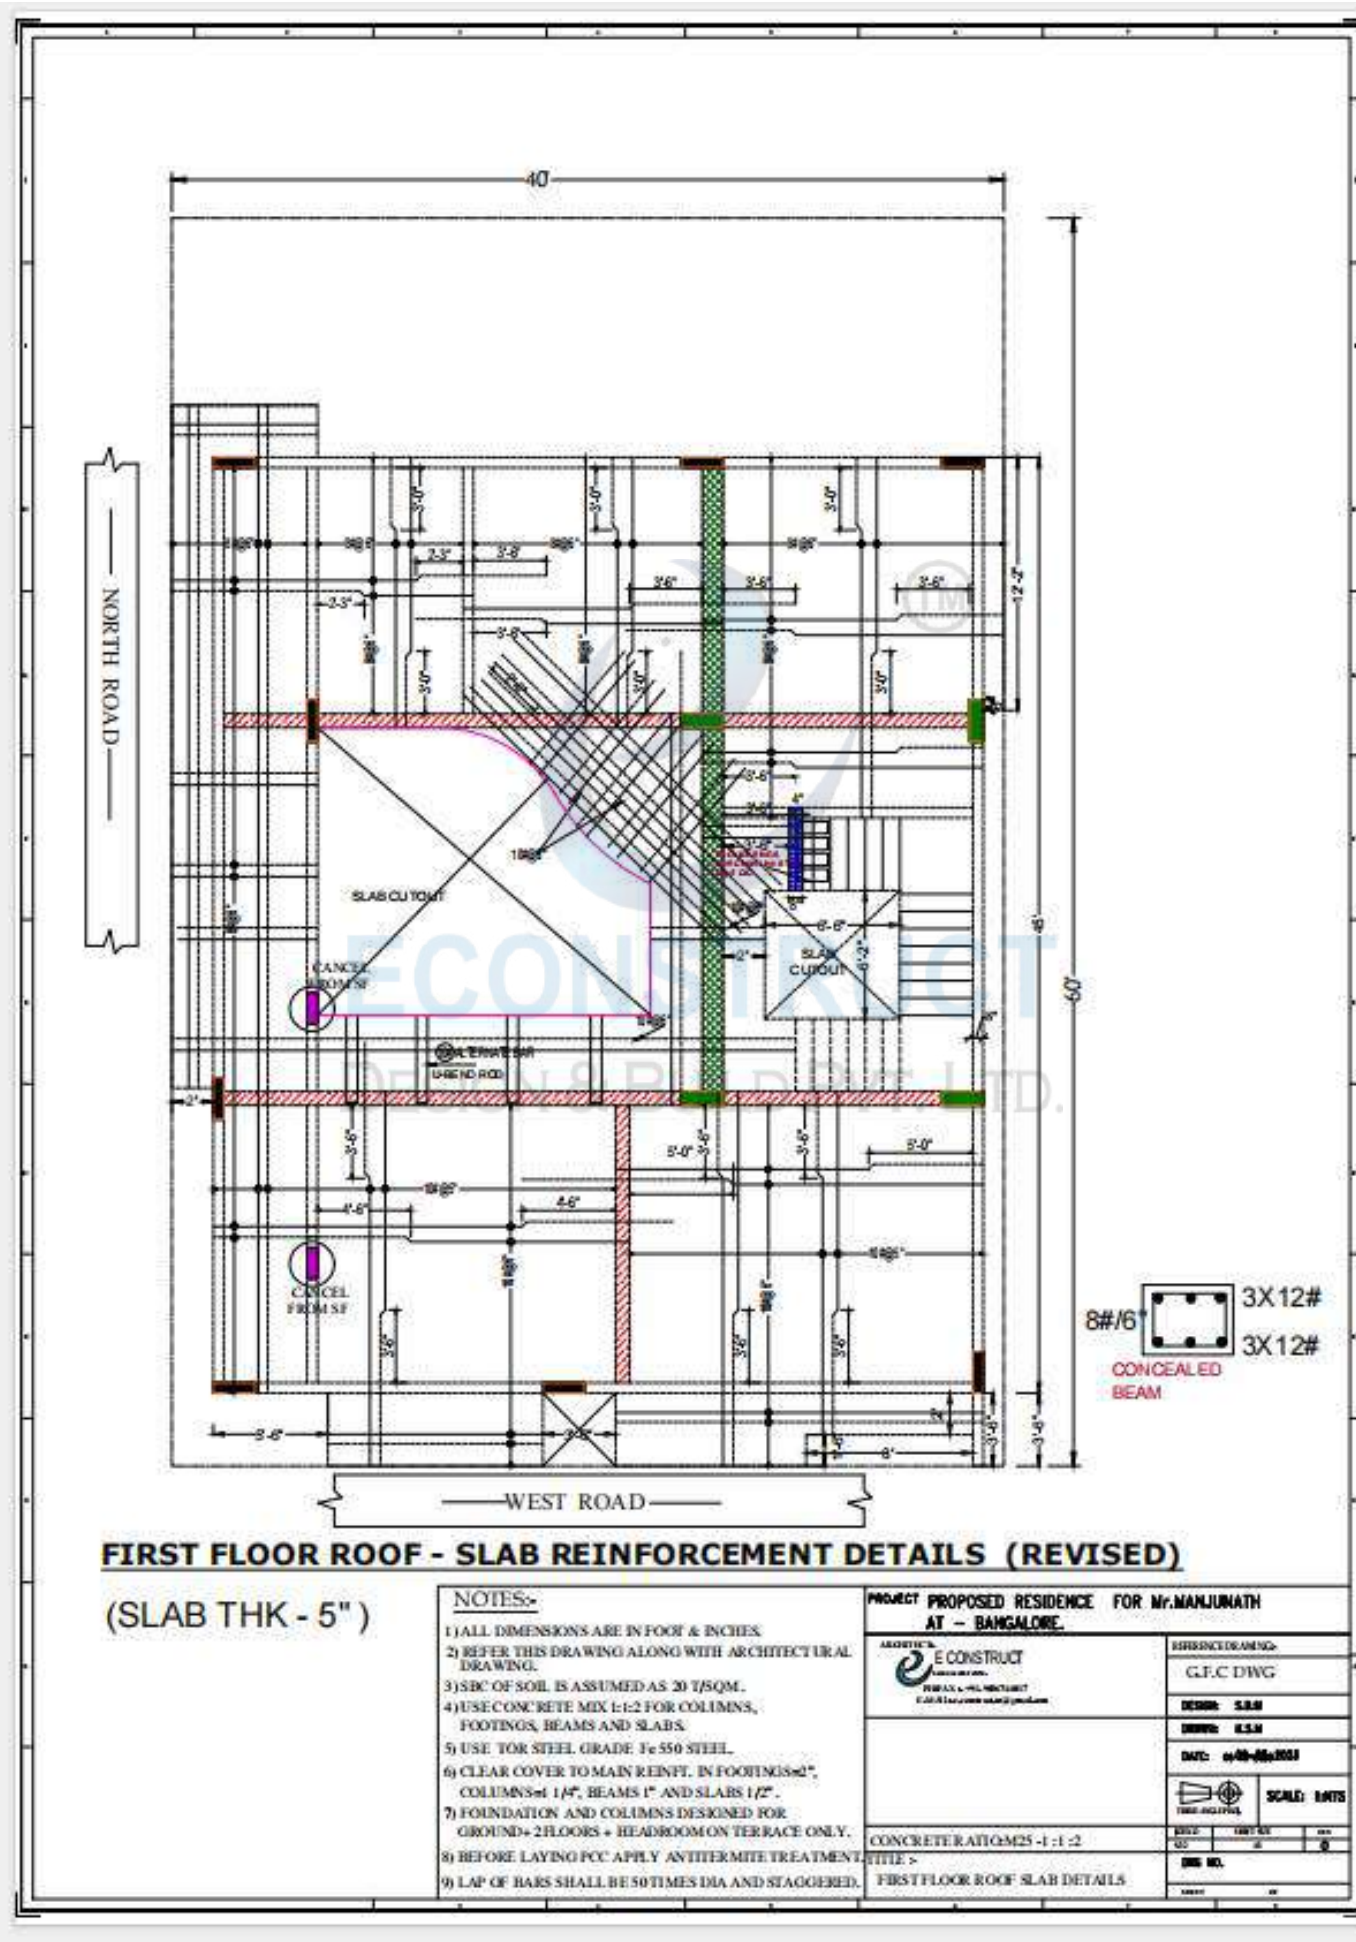


14

SECOND FLOOR ROOF BEAM SHUTTERING LAYOUT-rvsd

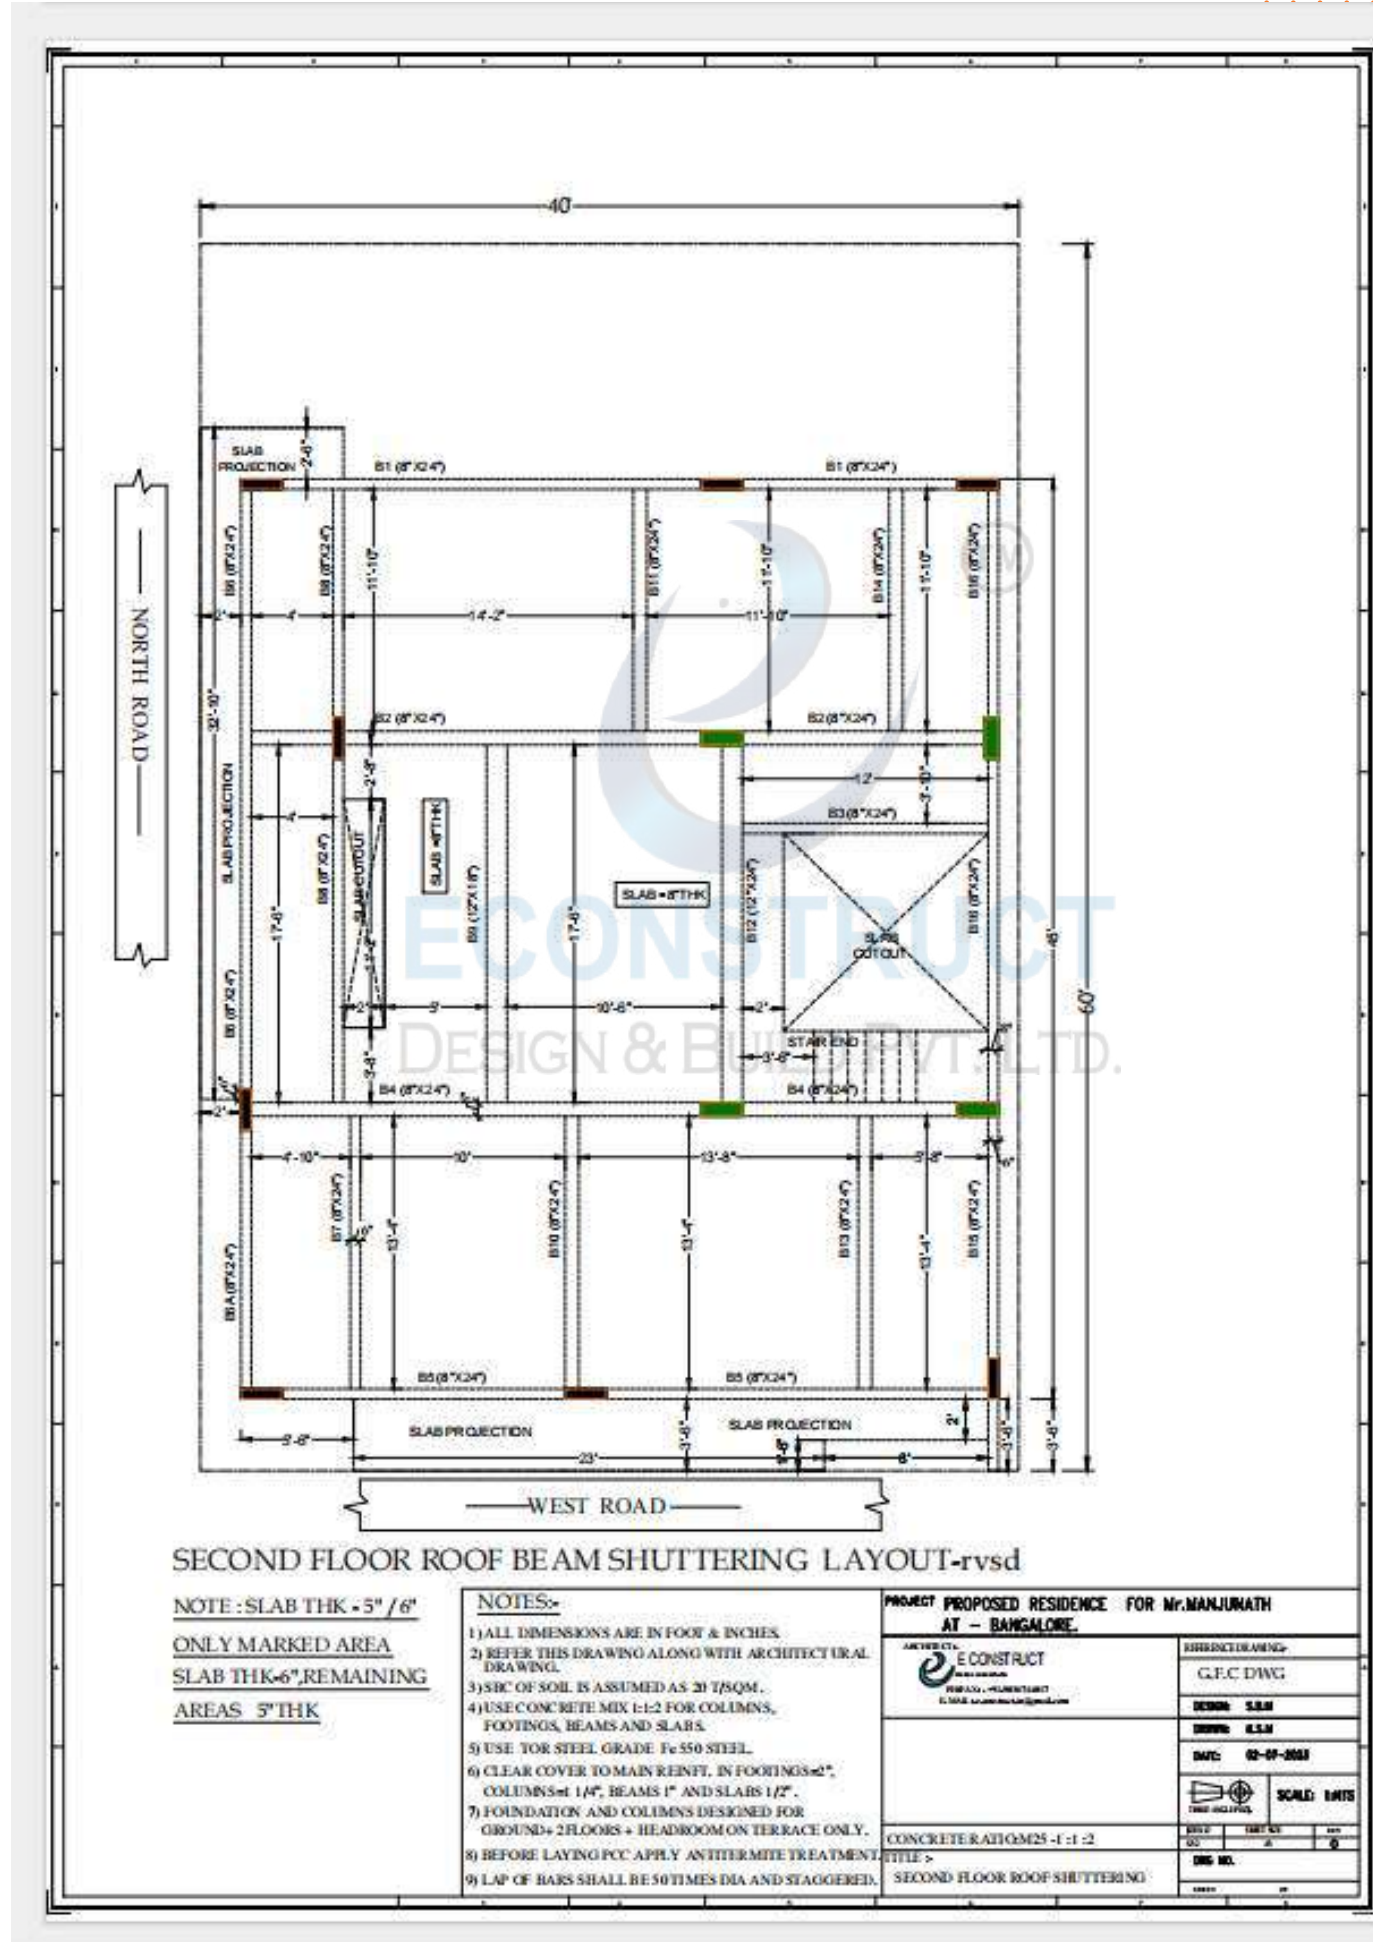


15

15. SECOND FLOOR -ROOF BEAM REINFORCEMENT DETAILS - SHEET-1

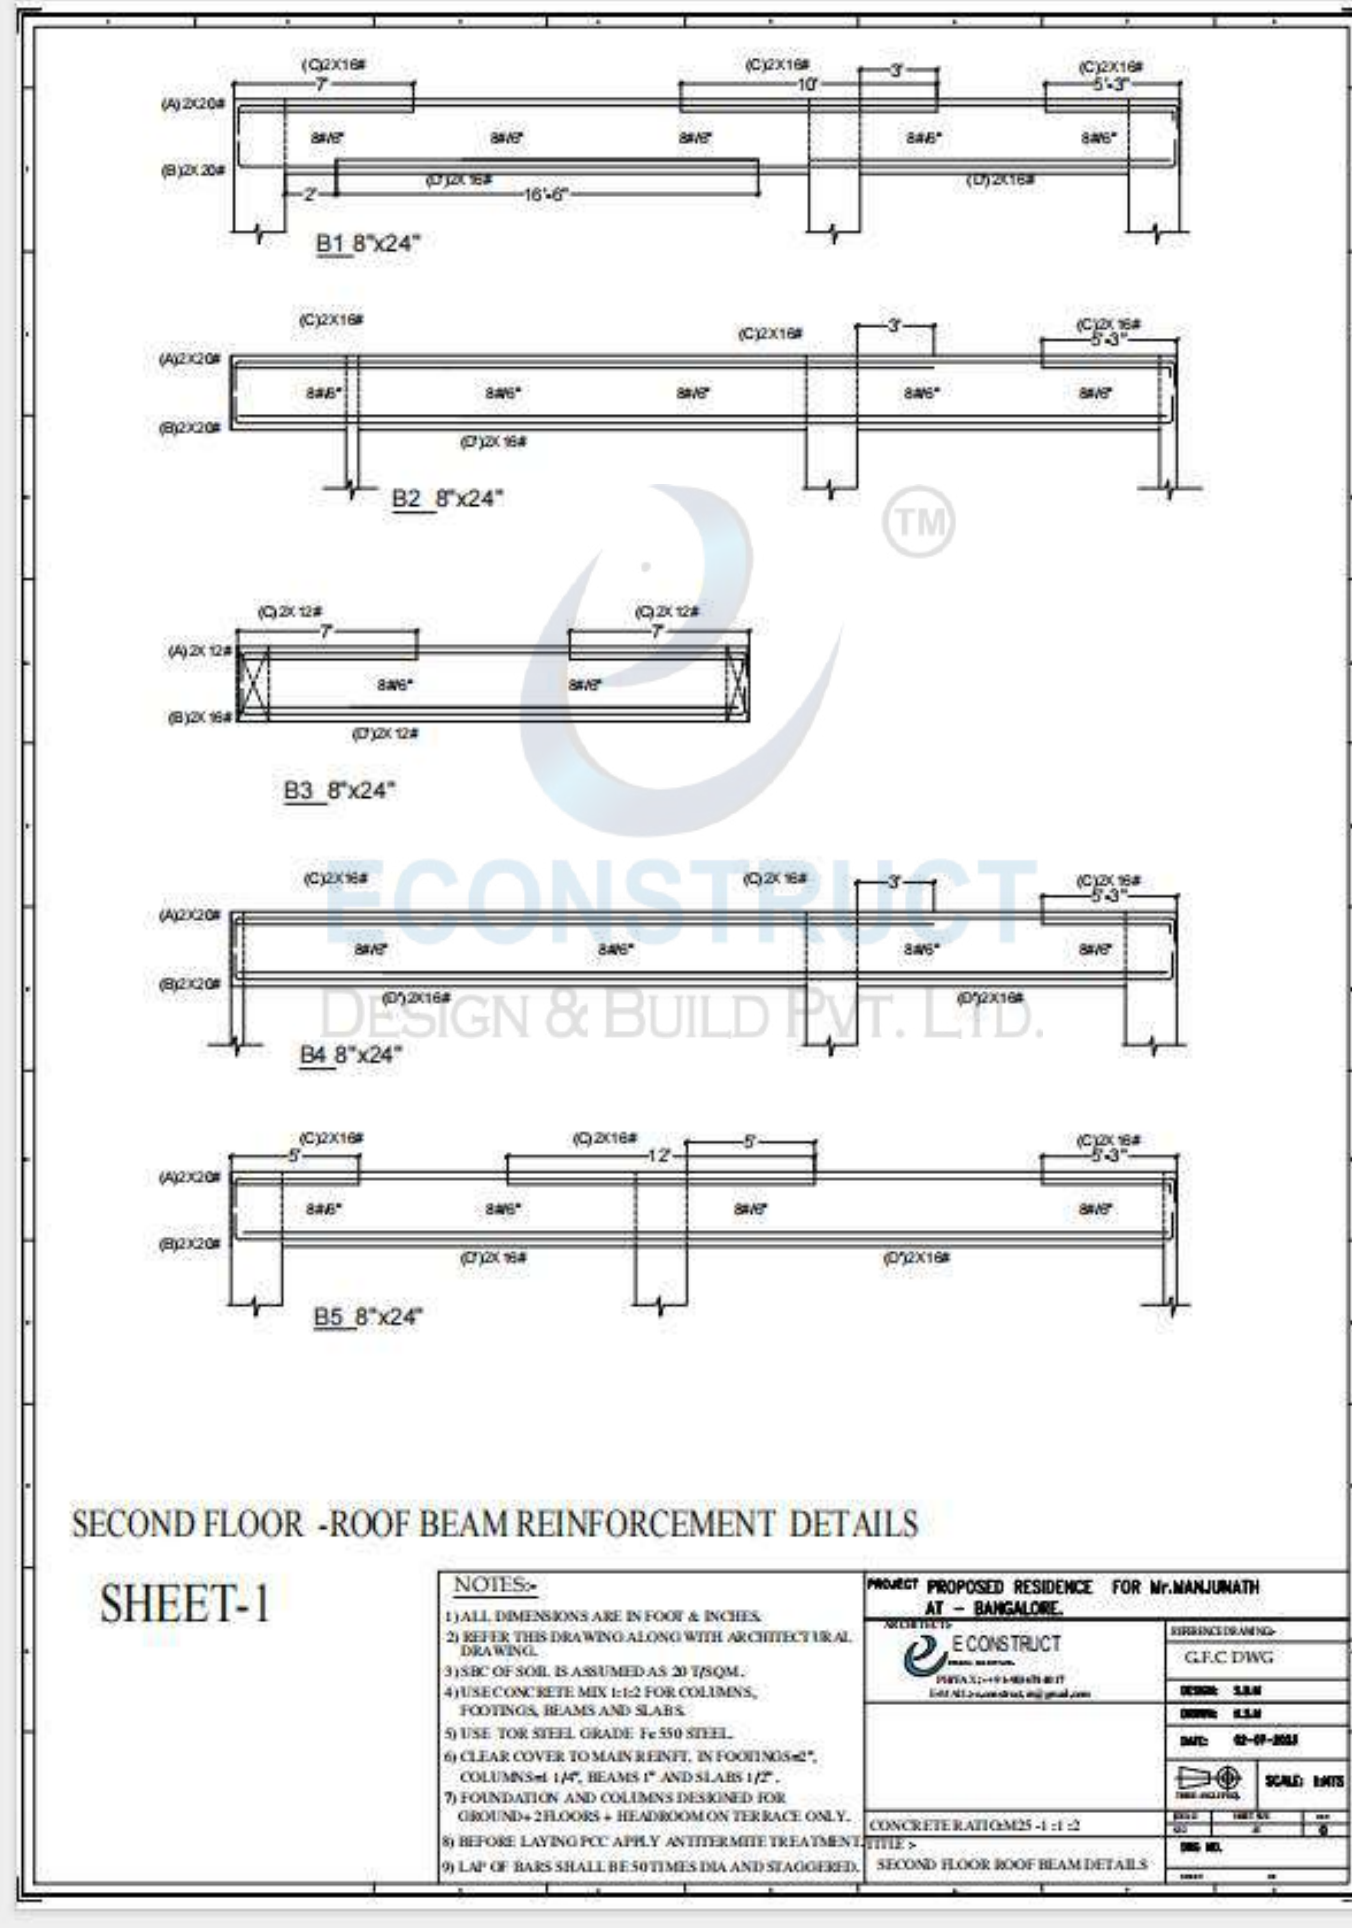


16

16. SECOND FLOOR -ROOF BEAM REINFORCEMENT DETAILS - SHEET-2

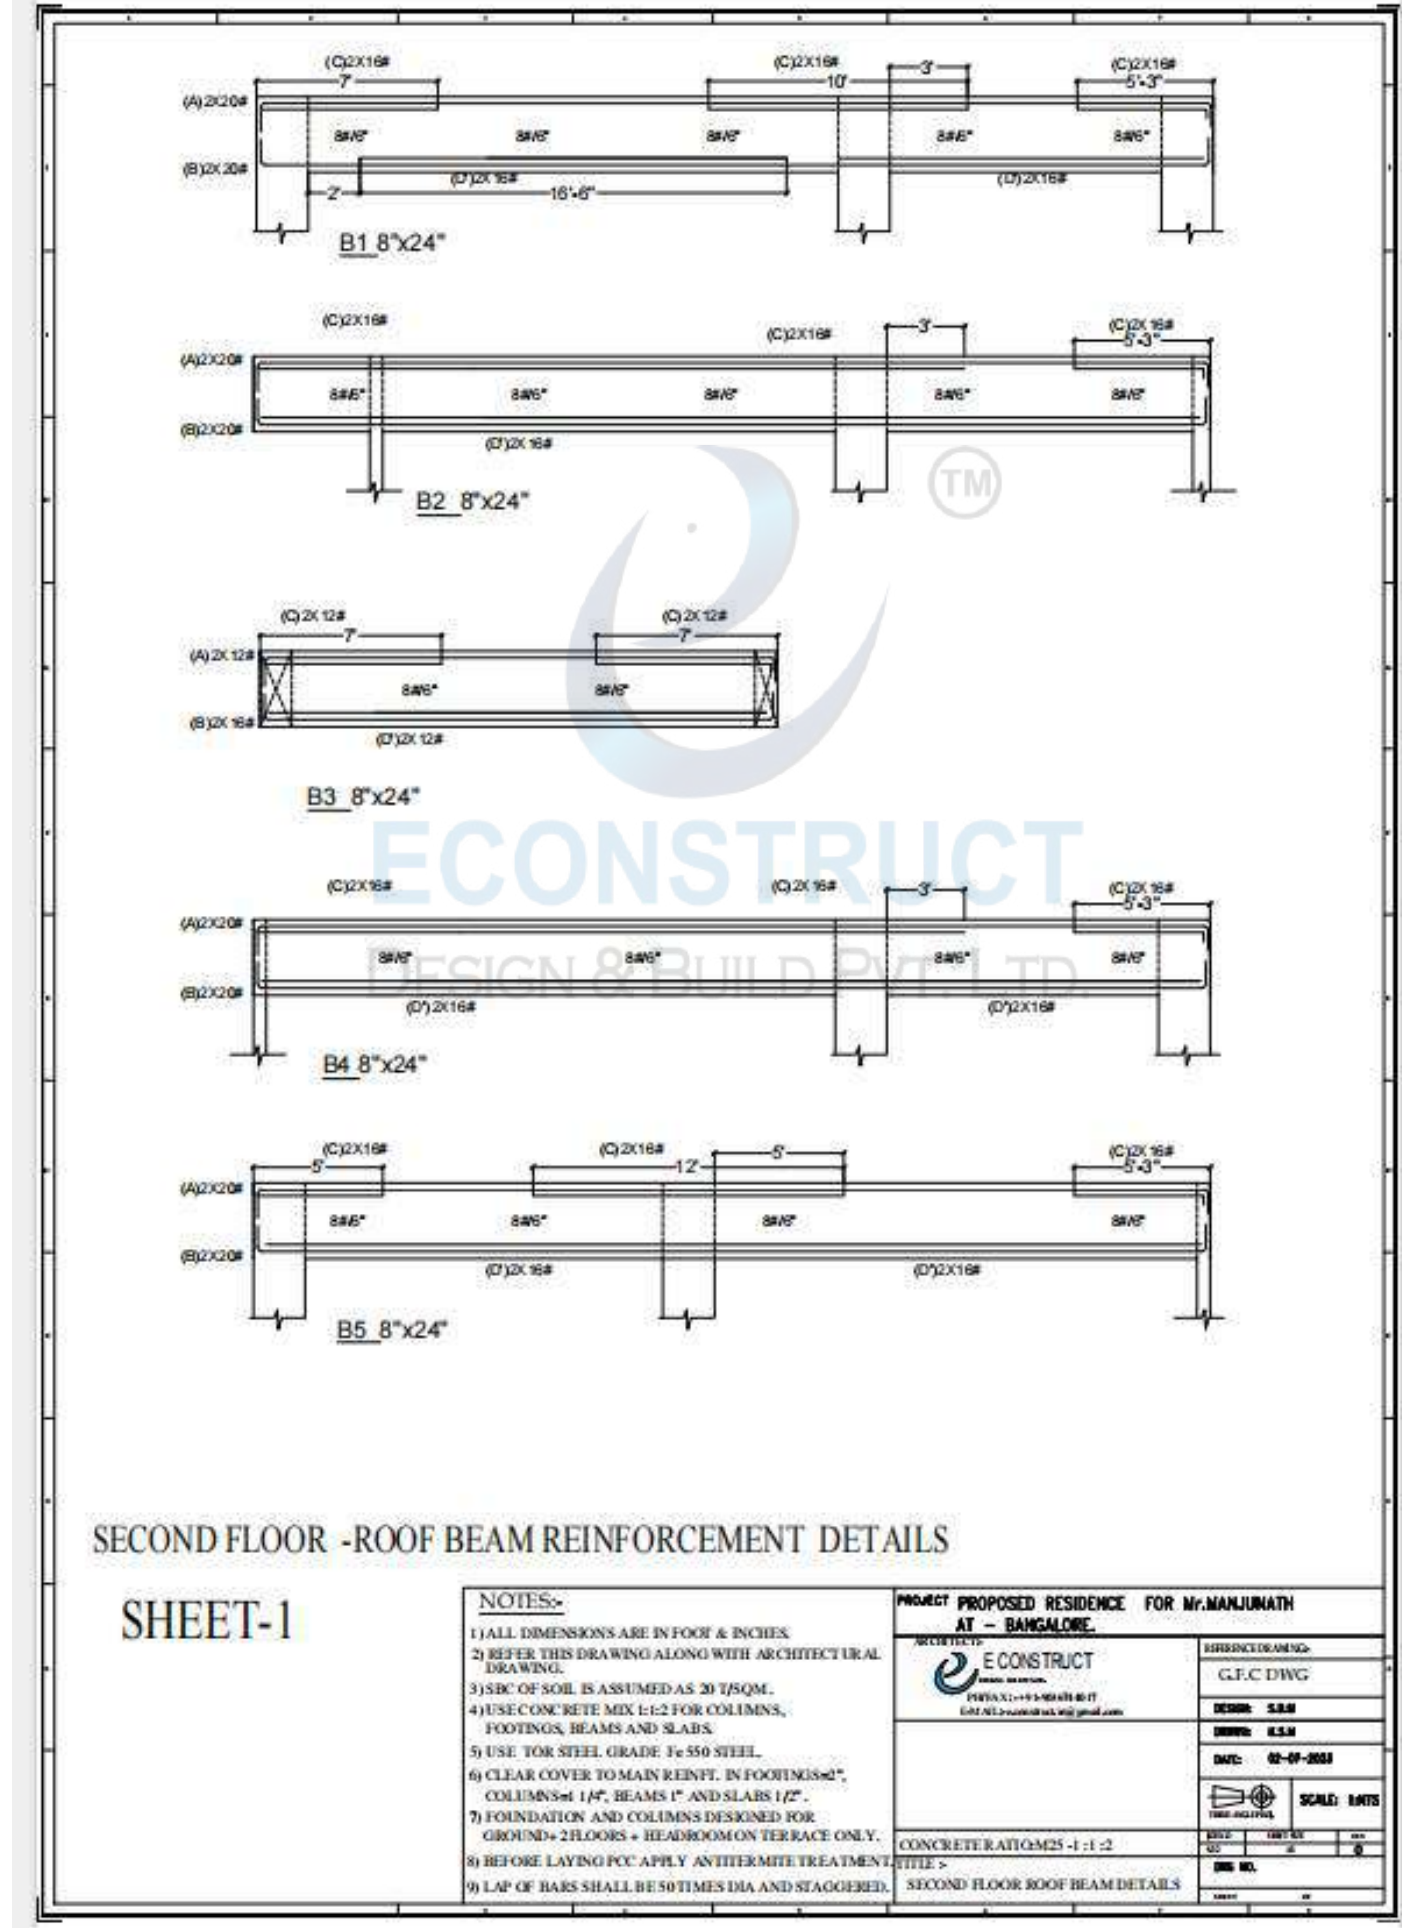


17



SECOND FLOOR ROOF - SLAB REINFORCEMENT DETAILS

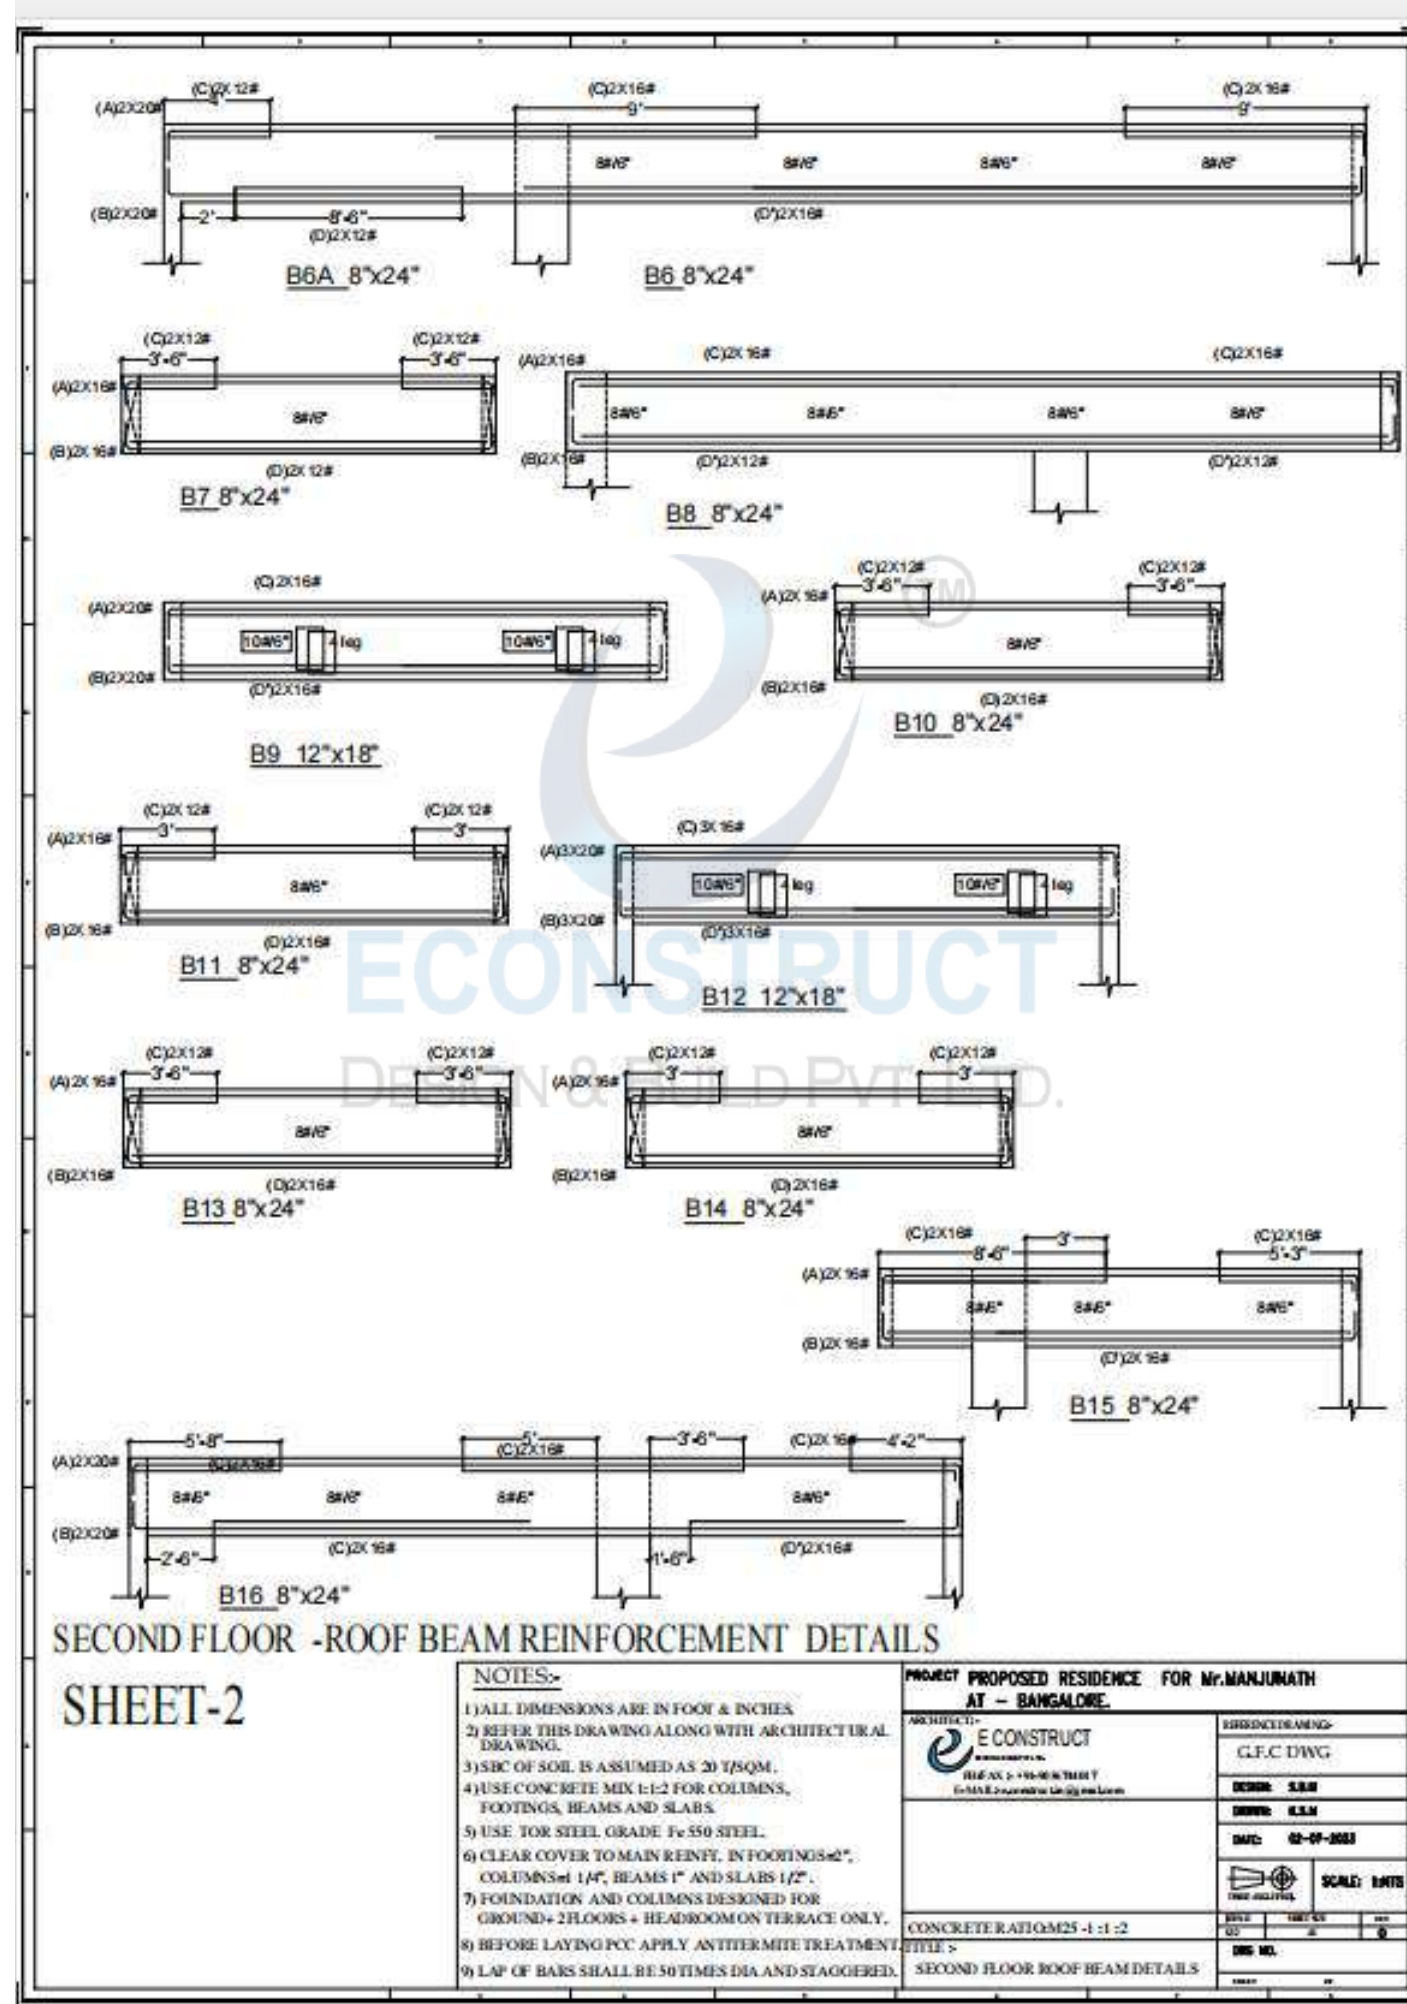

18


TERRACE FLOOR ROOF - SLAB REINFORCEMENT DETAILS

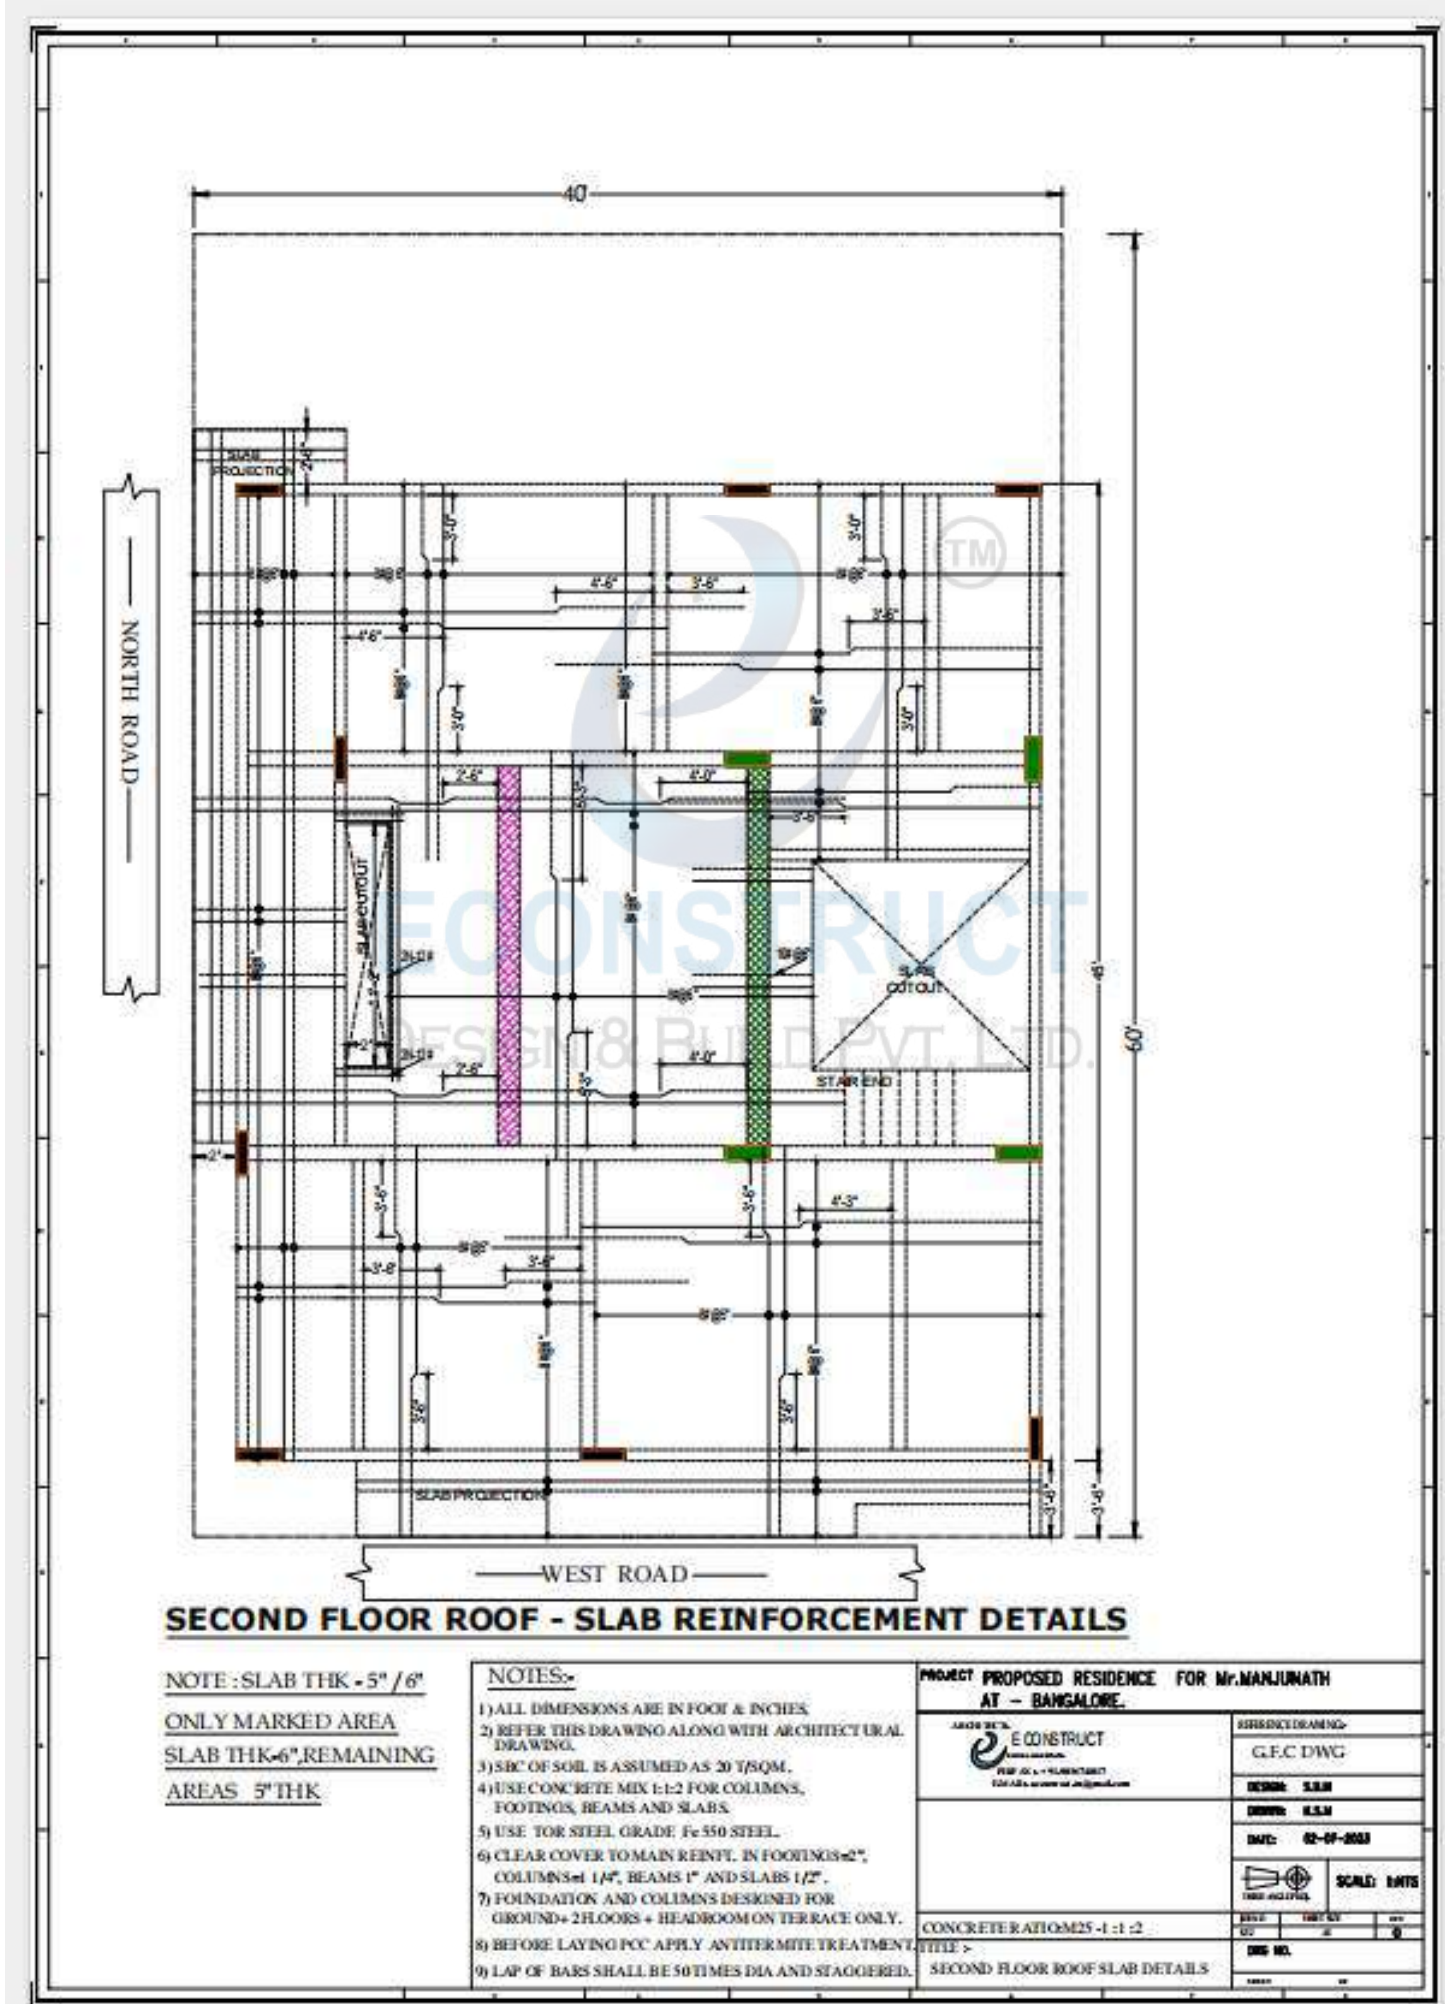

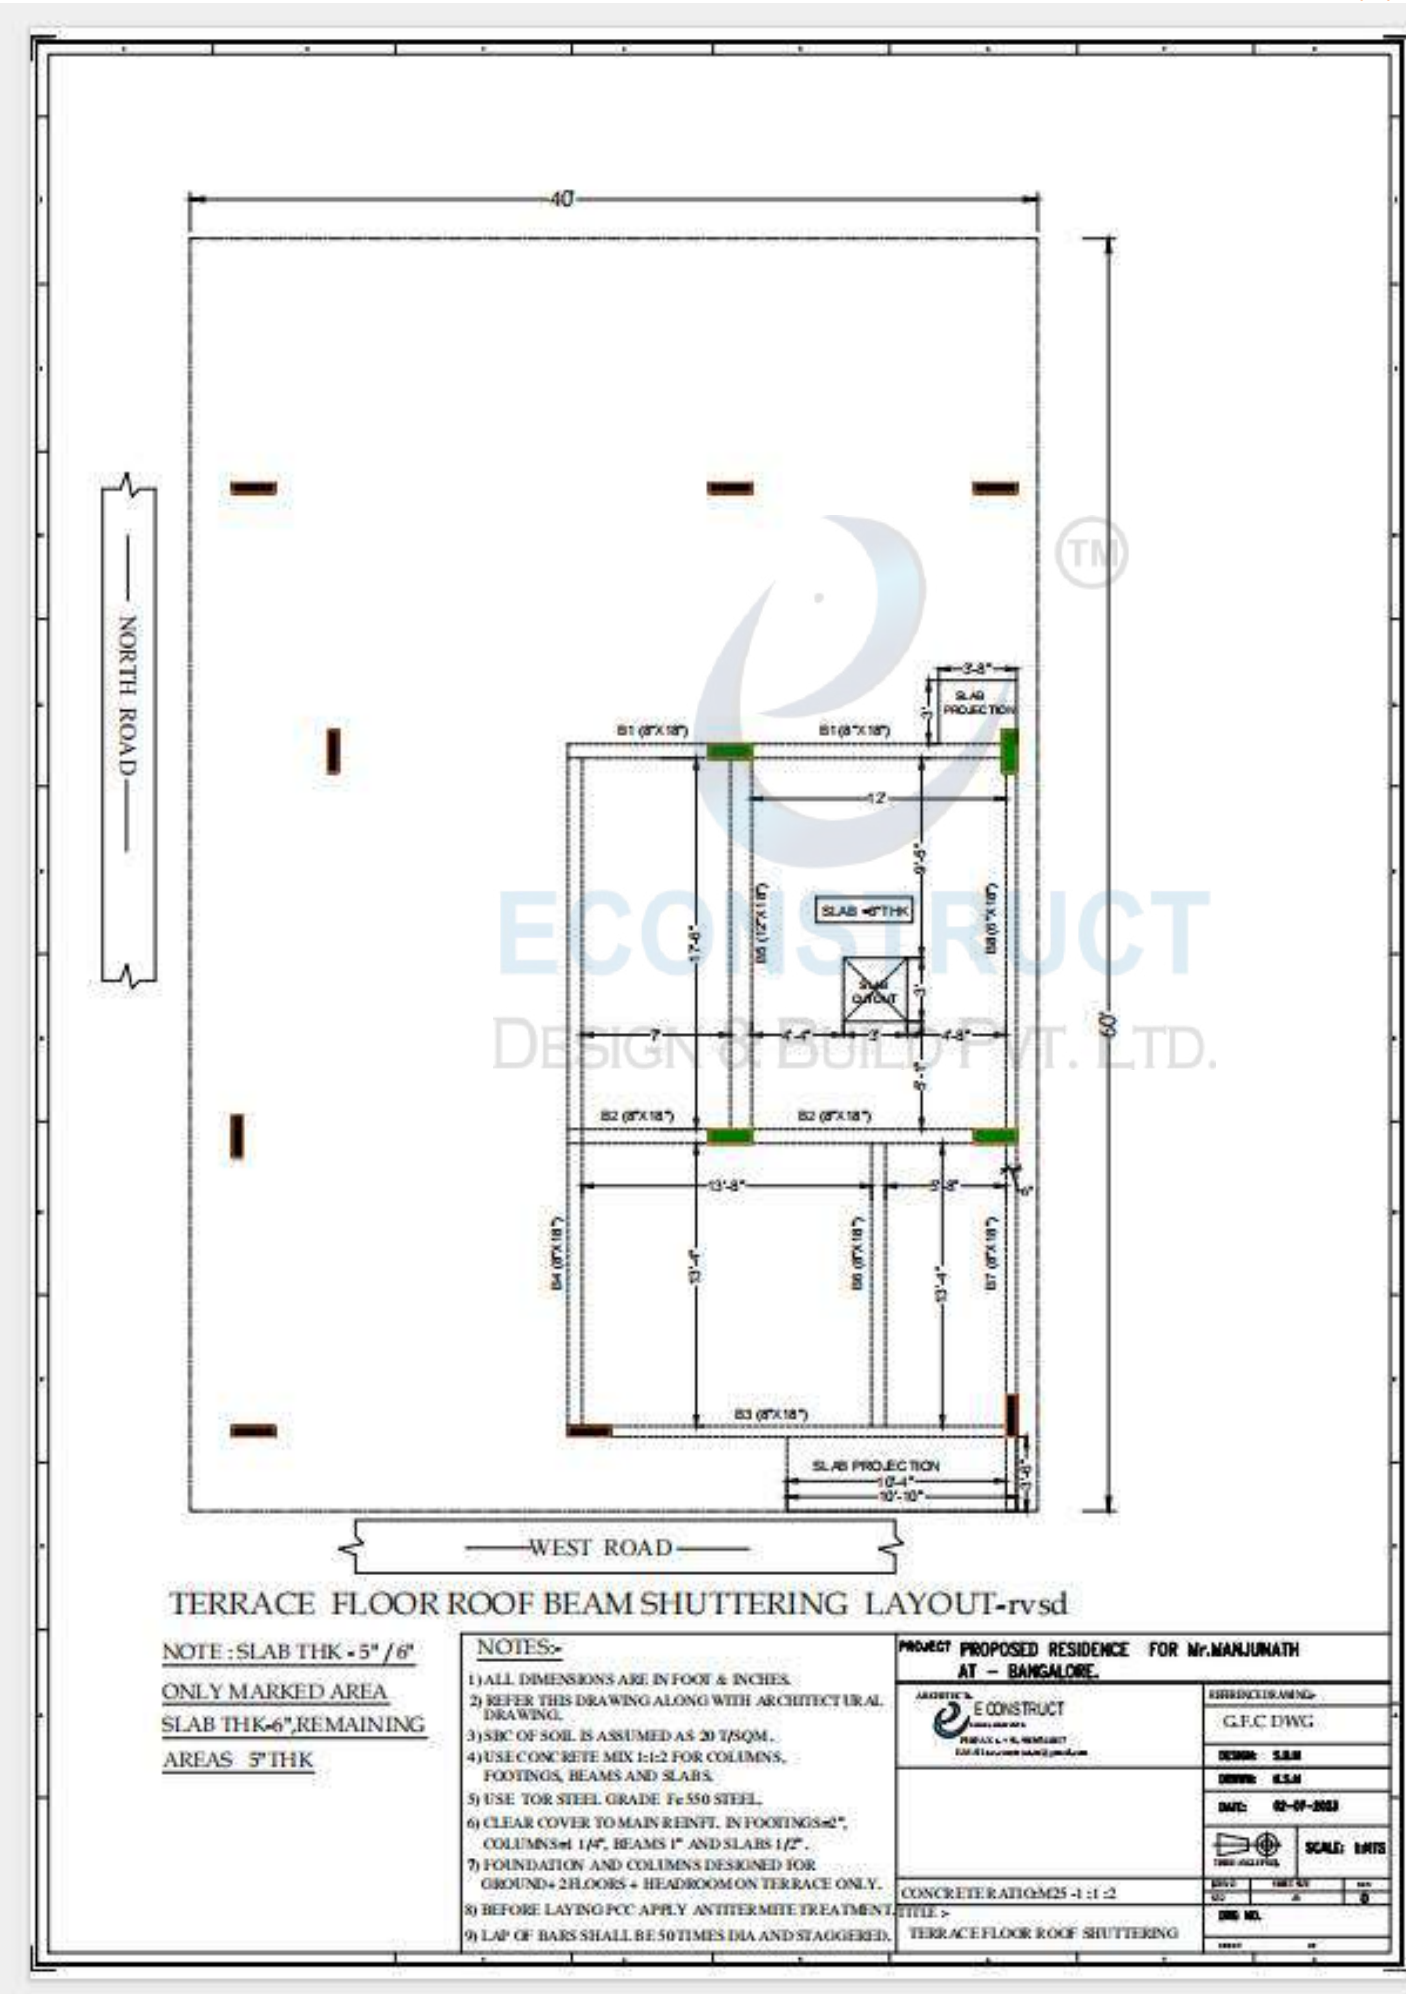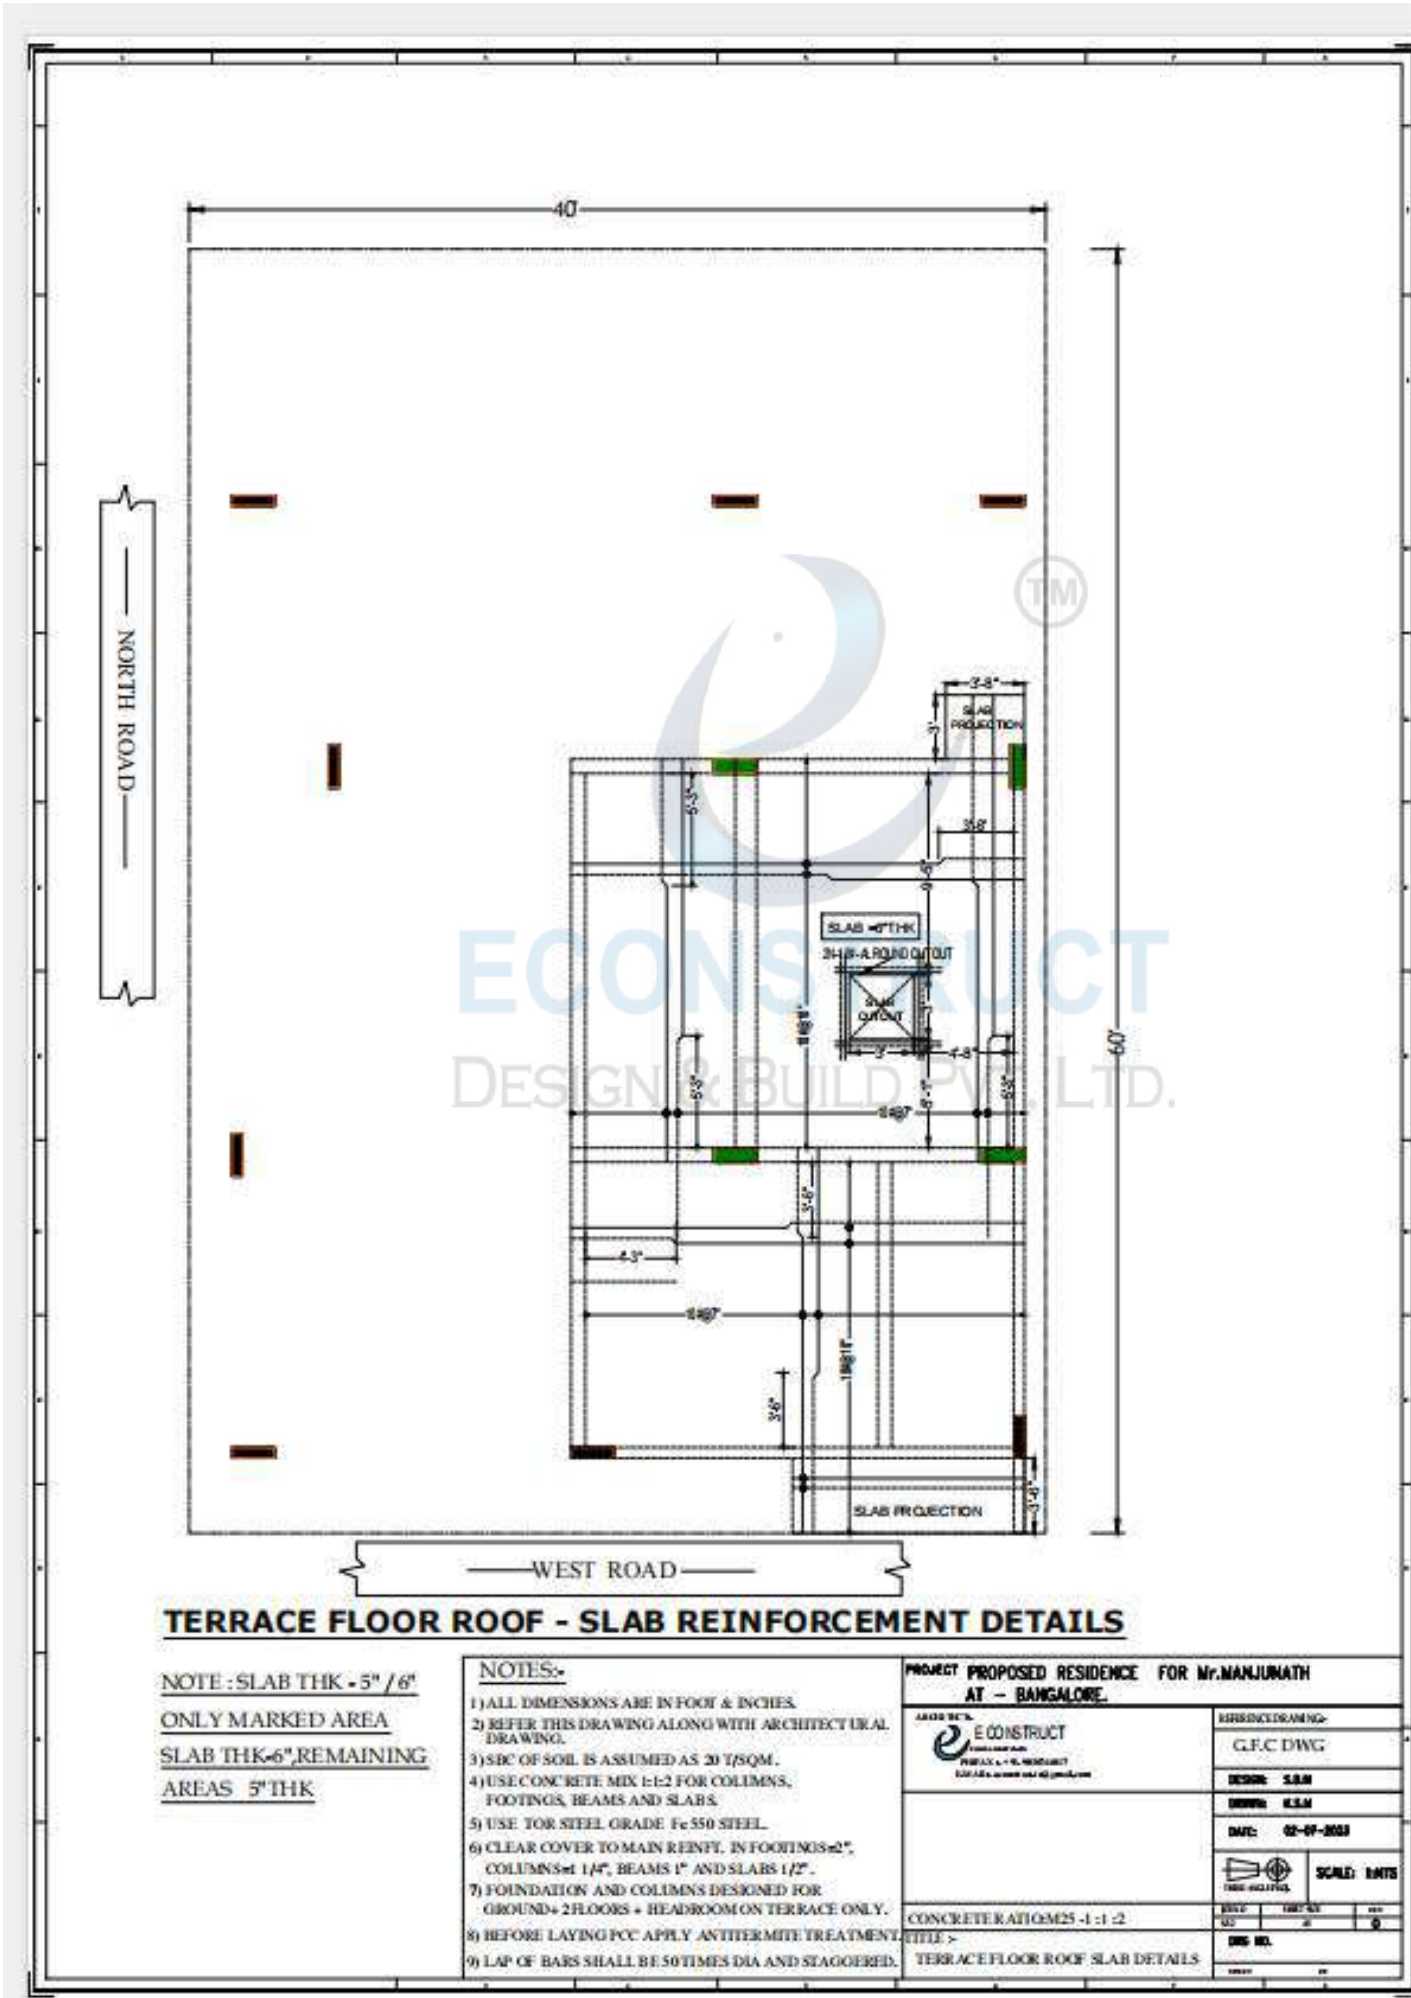


Architectural Drawings Included

- Ground Floor Plan (37' x 45')
- First, Second & Terrace Floor Plans (Triplex Layout)
- Working Plans (Second & Terrace Floor)
- Doors & Windows Schedule
- Total Doors – 20 Nos
- Staircase Plans (External + Internal Duplex)
- Loft & Chajja Details (All Floors)
- Electrical Ceiling Layout (All Floors)
- Solar Water Provision for Toilets
- Kitchen & Utility Planning
- Compound Details
- Kitchen Detailed Plan
- Bedroom Wardrobe Designs (5 Types)

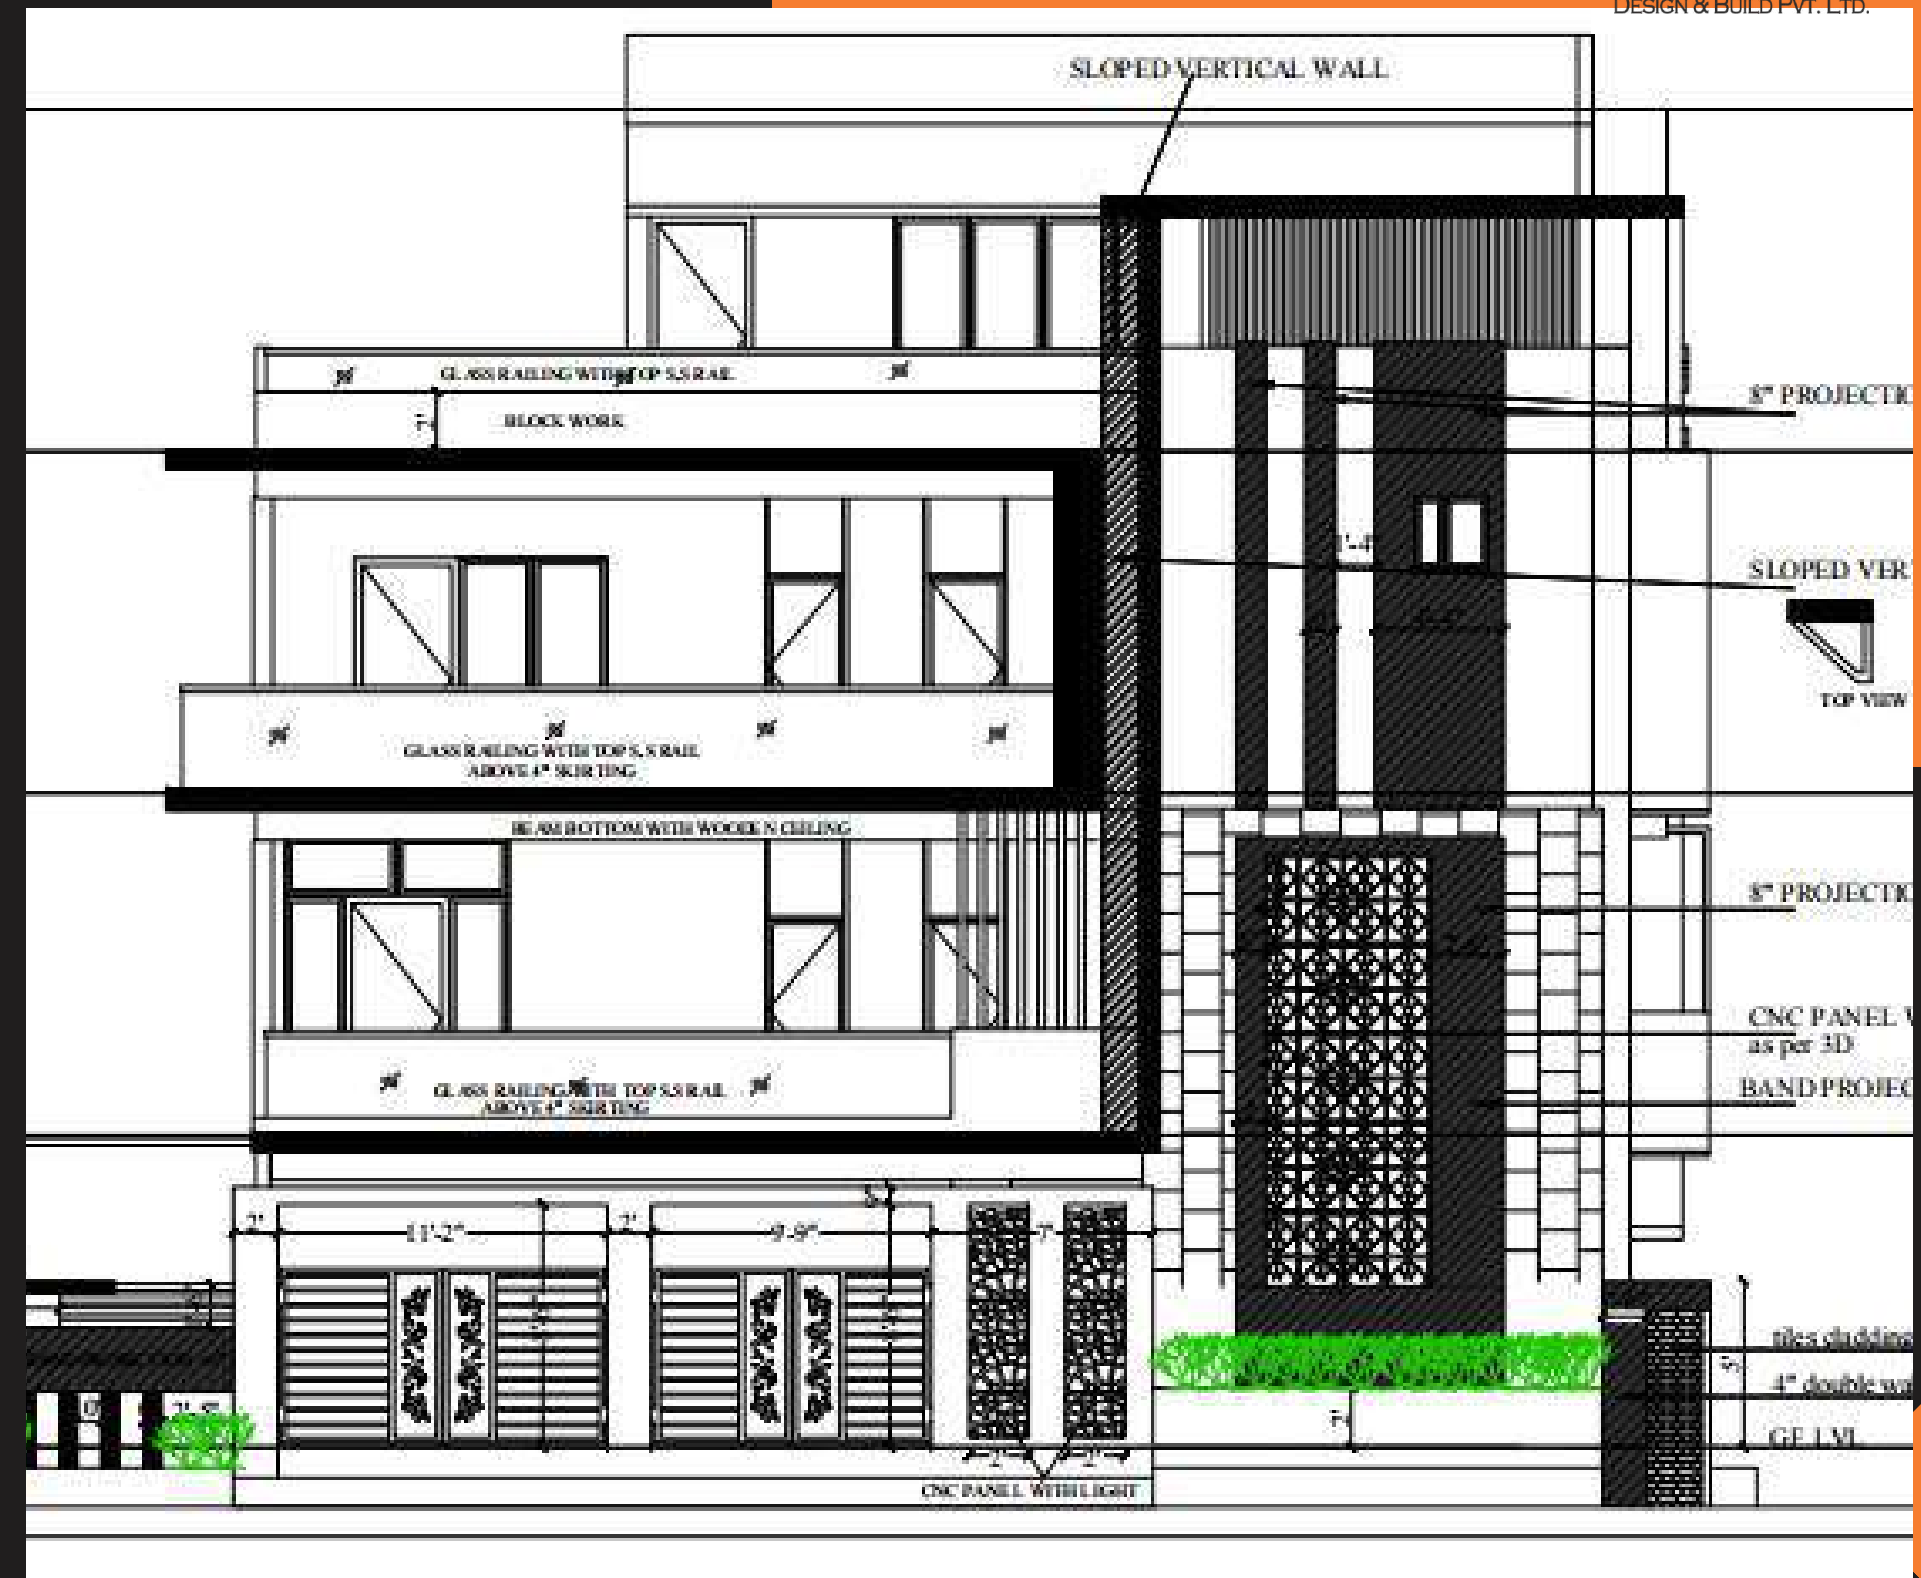


01

GROUND FLOOR PLAN
BUILDING SIZE (37' X 45')

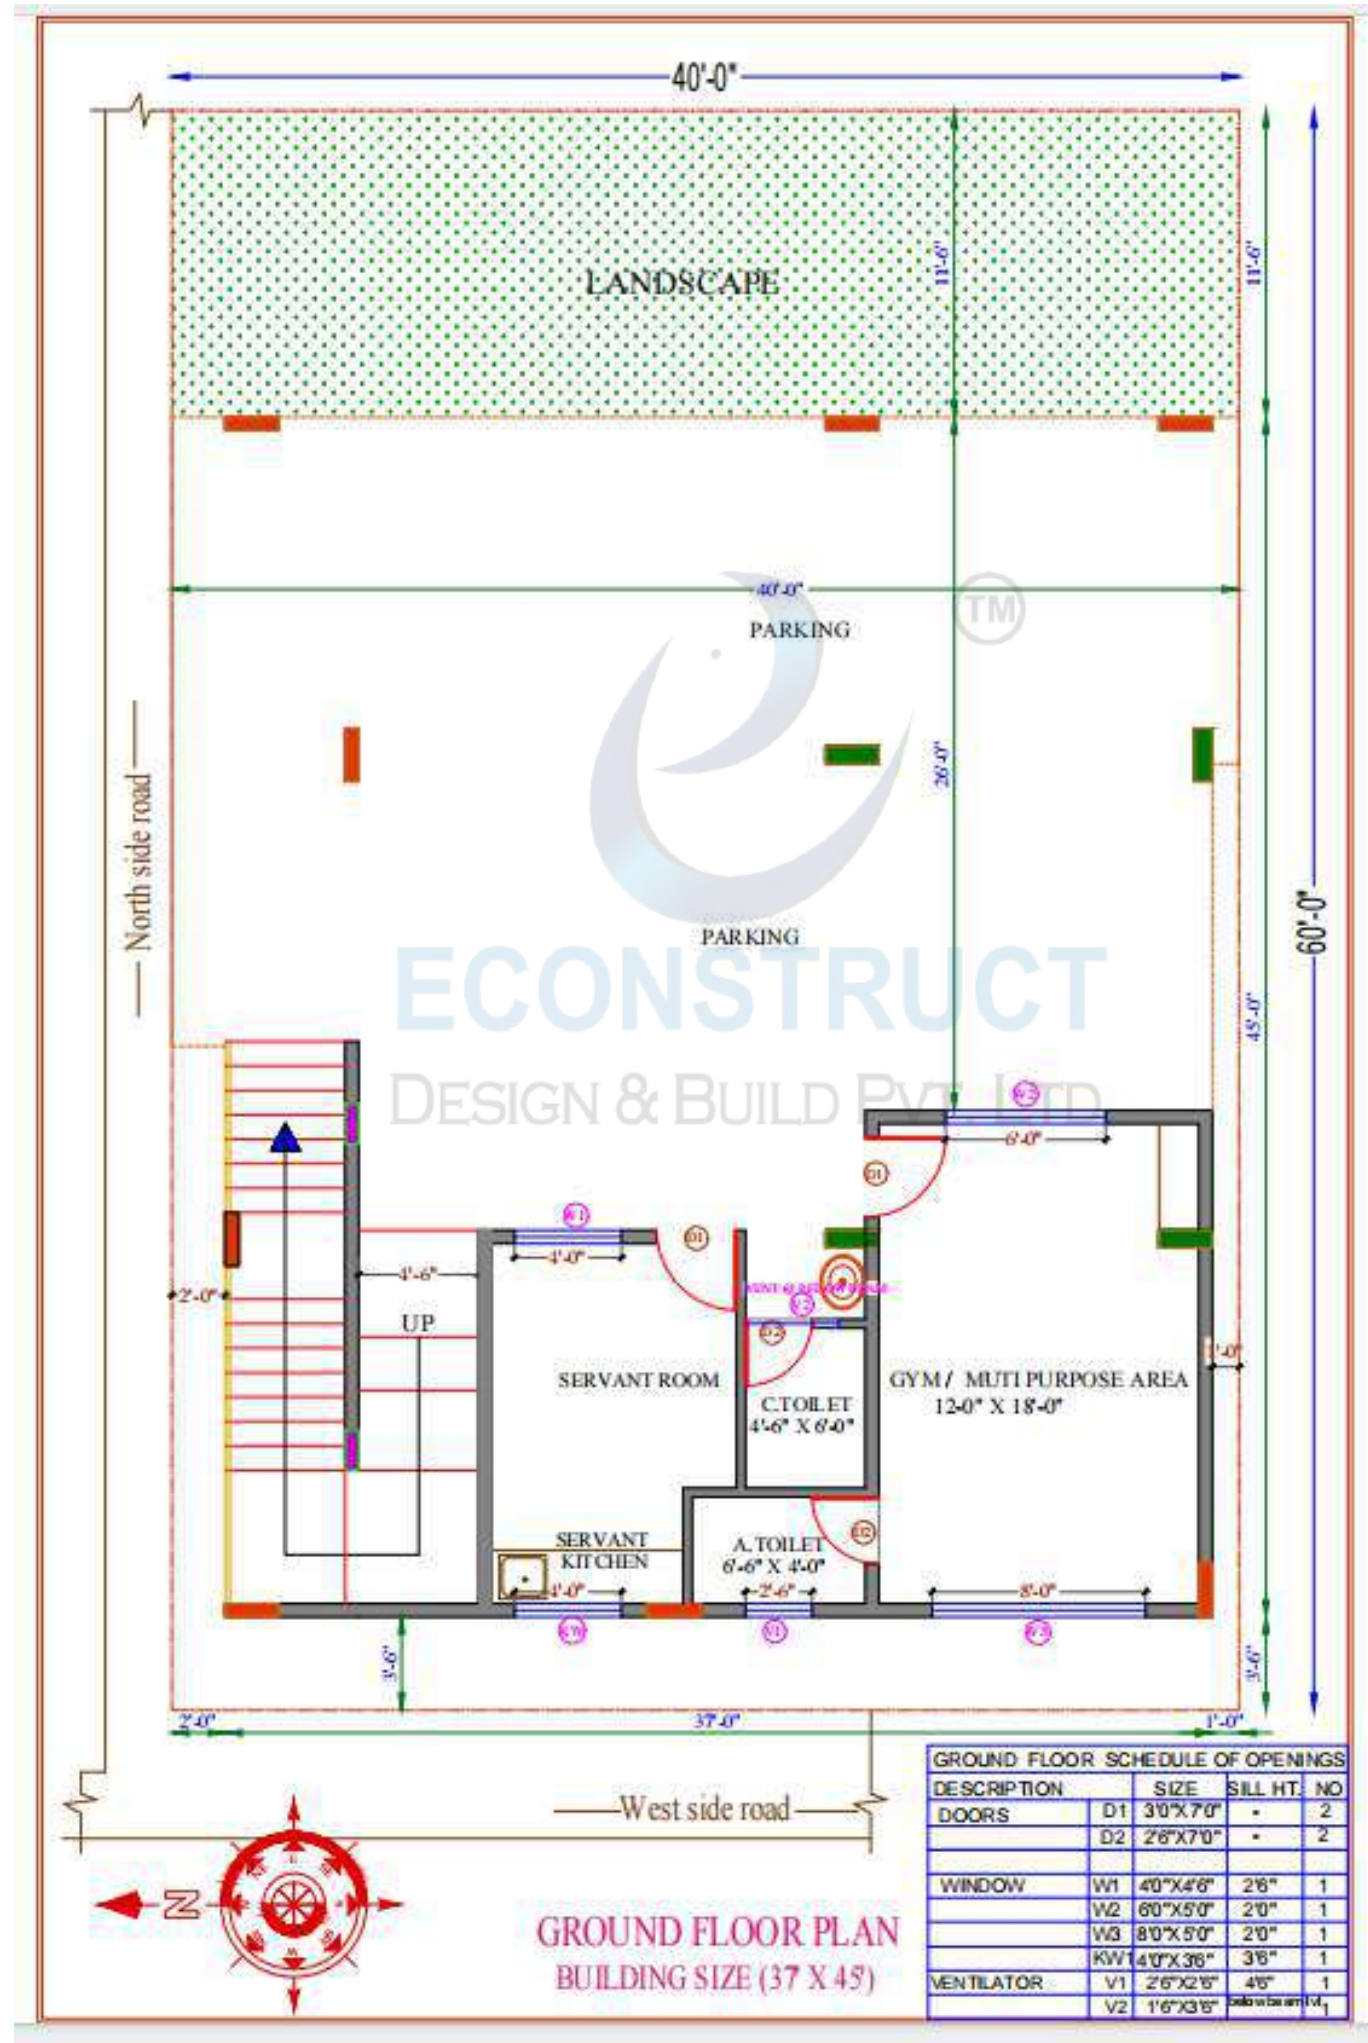


02

FIRST FLOOR PLAN - DUPLEX
HOUSE BUILDING SIZE (37' X 45')

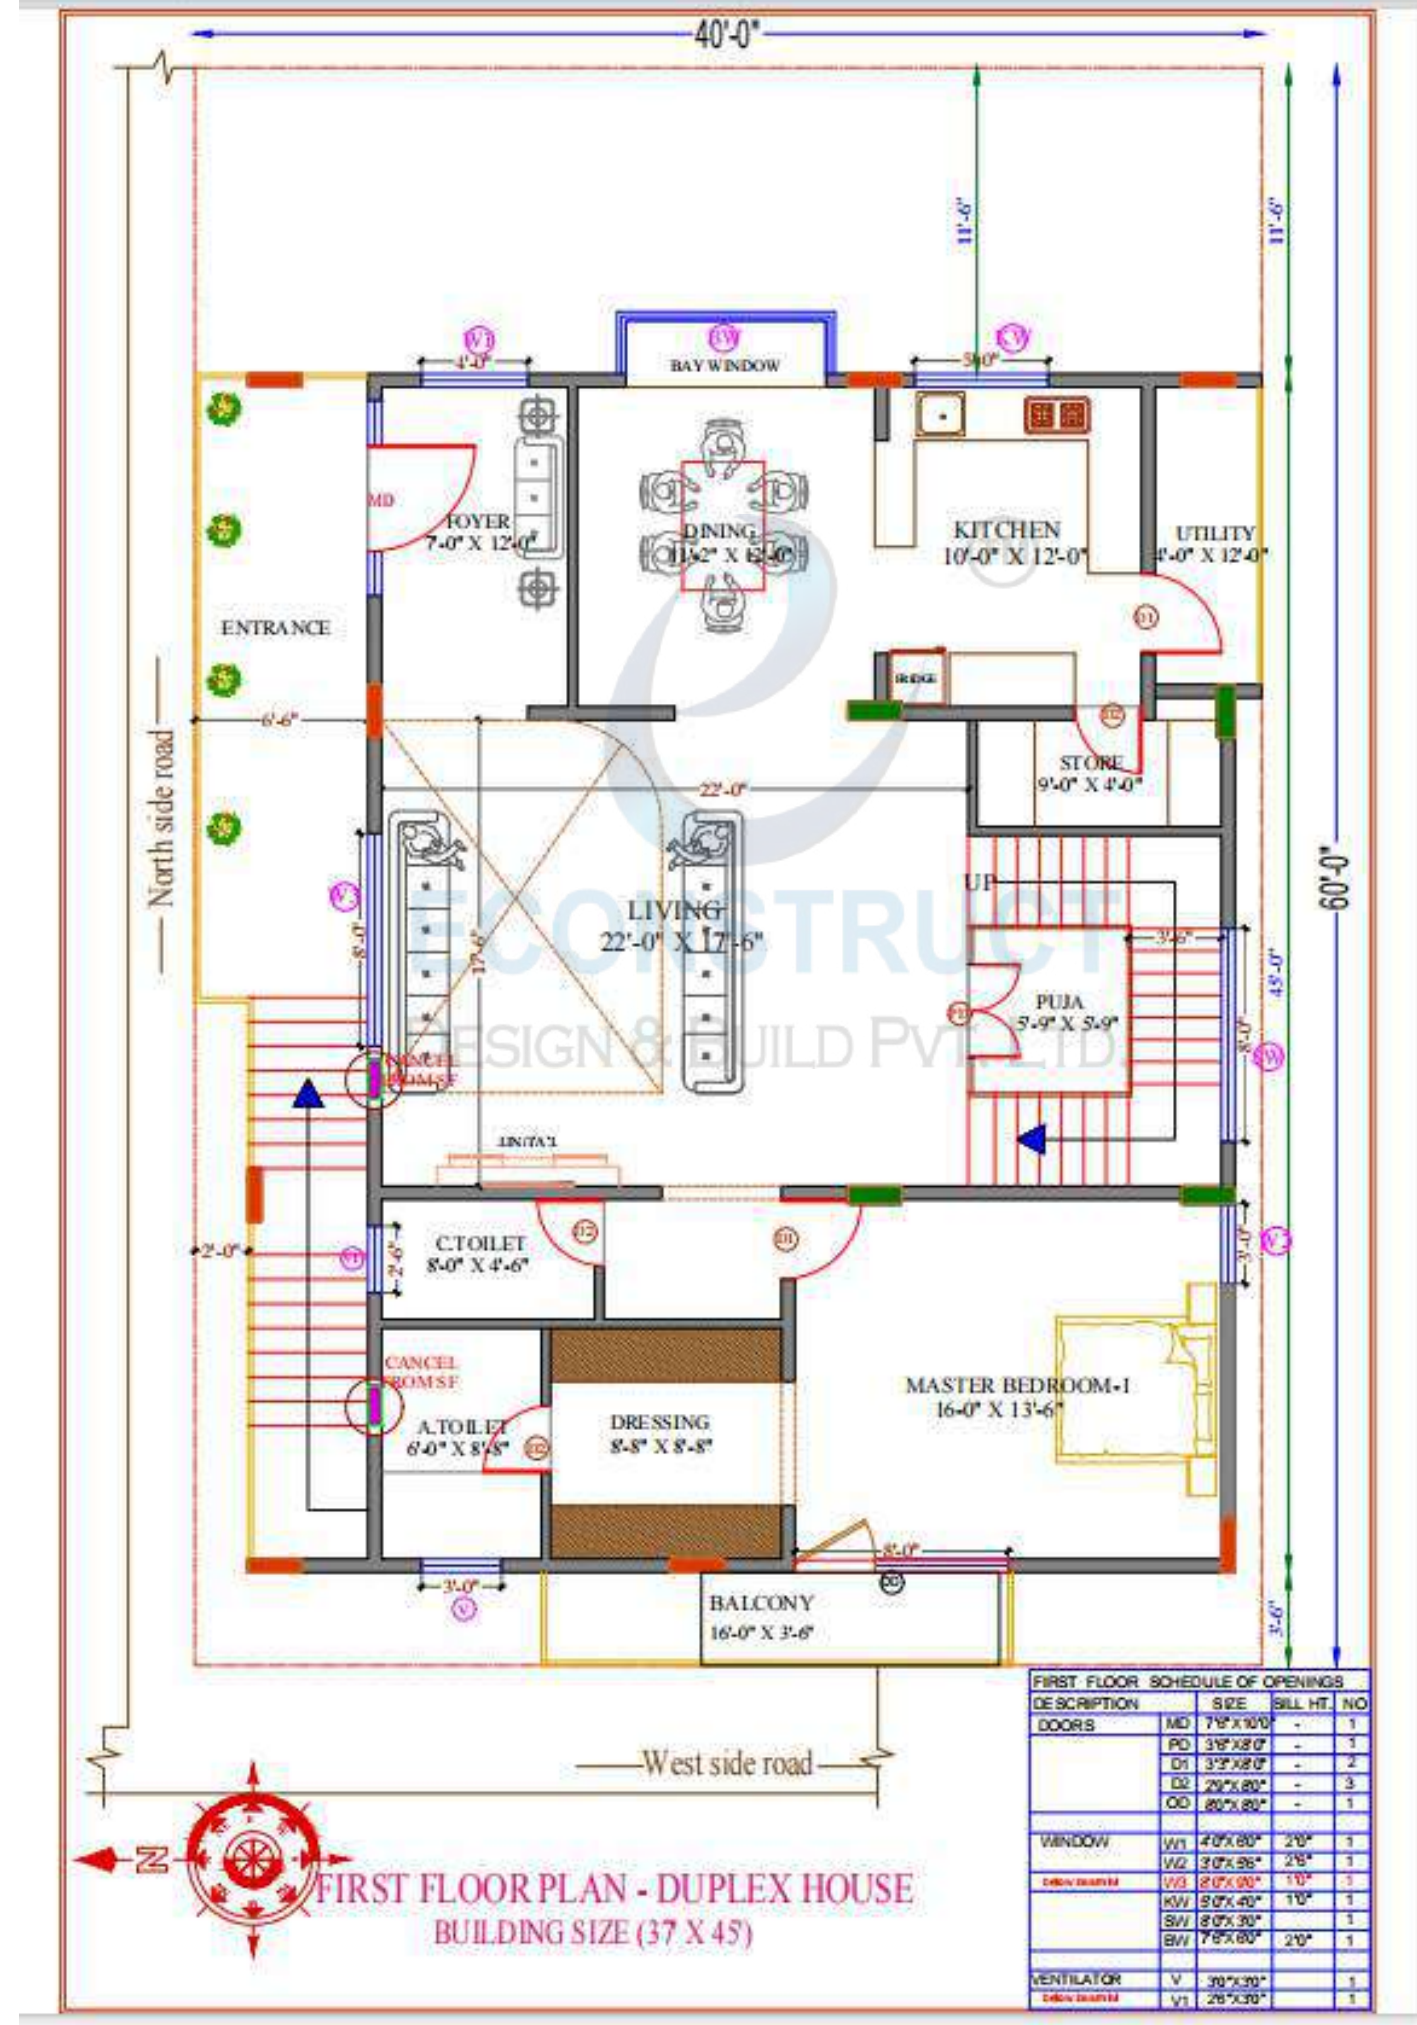


03

SECOND FLOOR PLAN - DUPLEX HOUSE BUILDING SIZE (37' X 45')

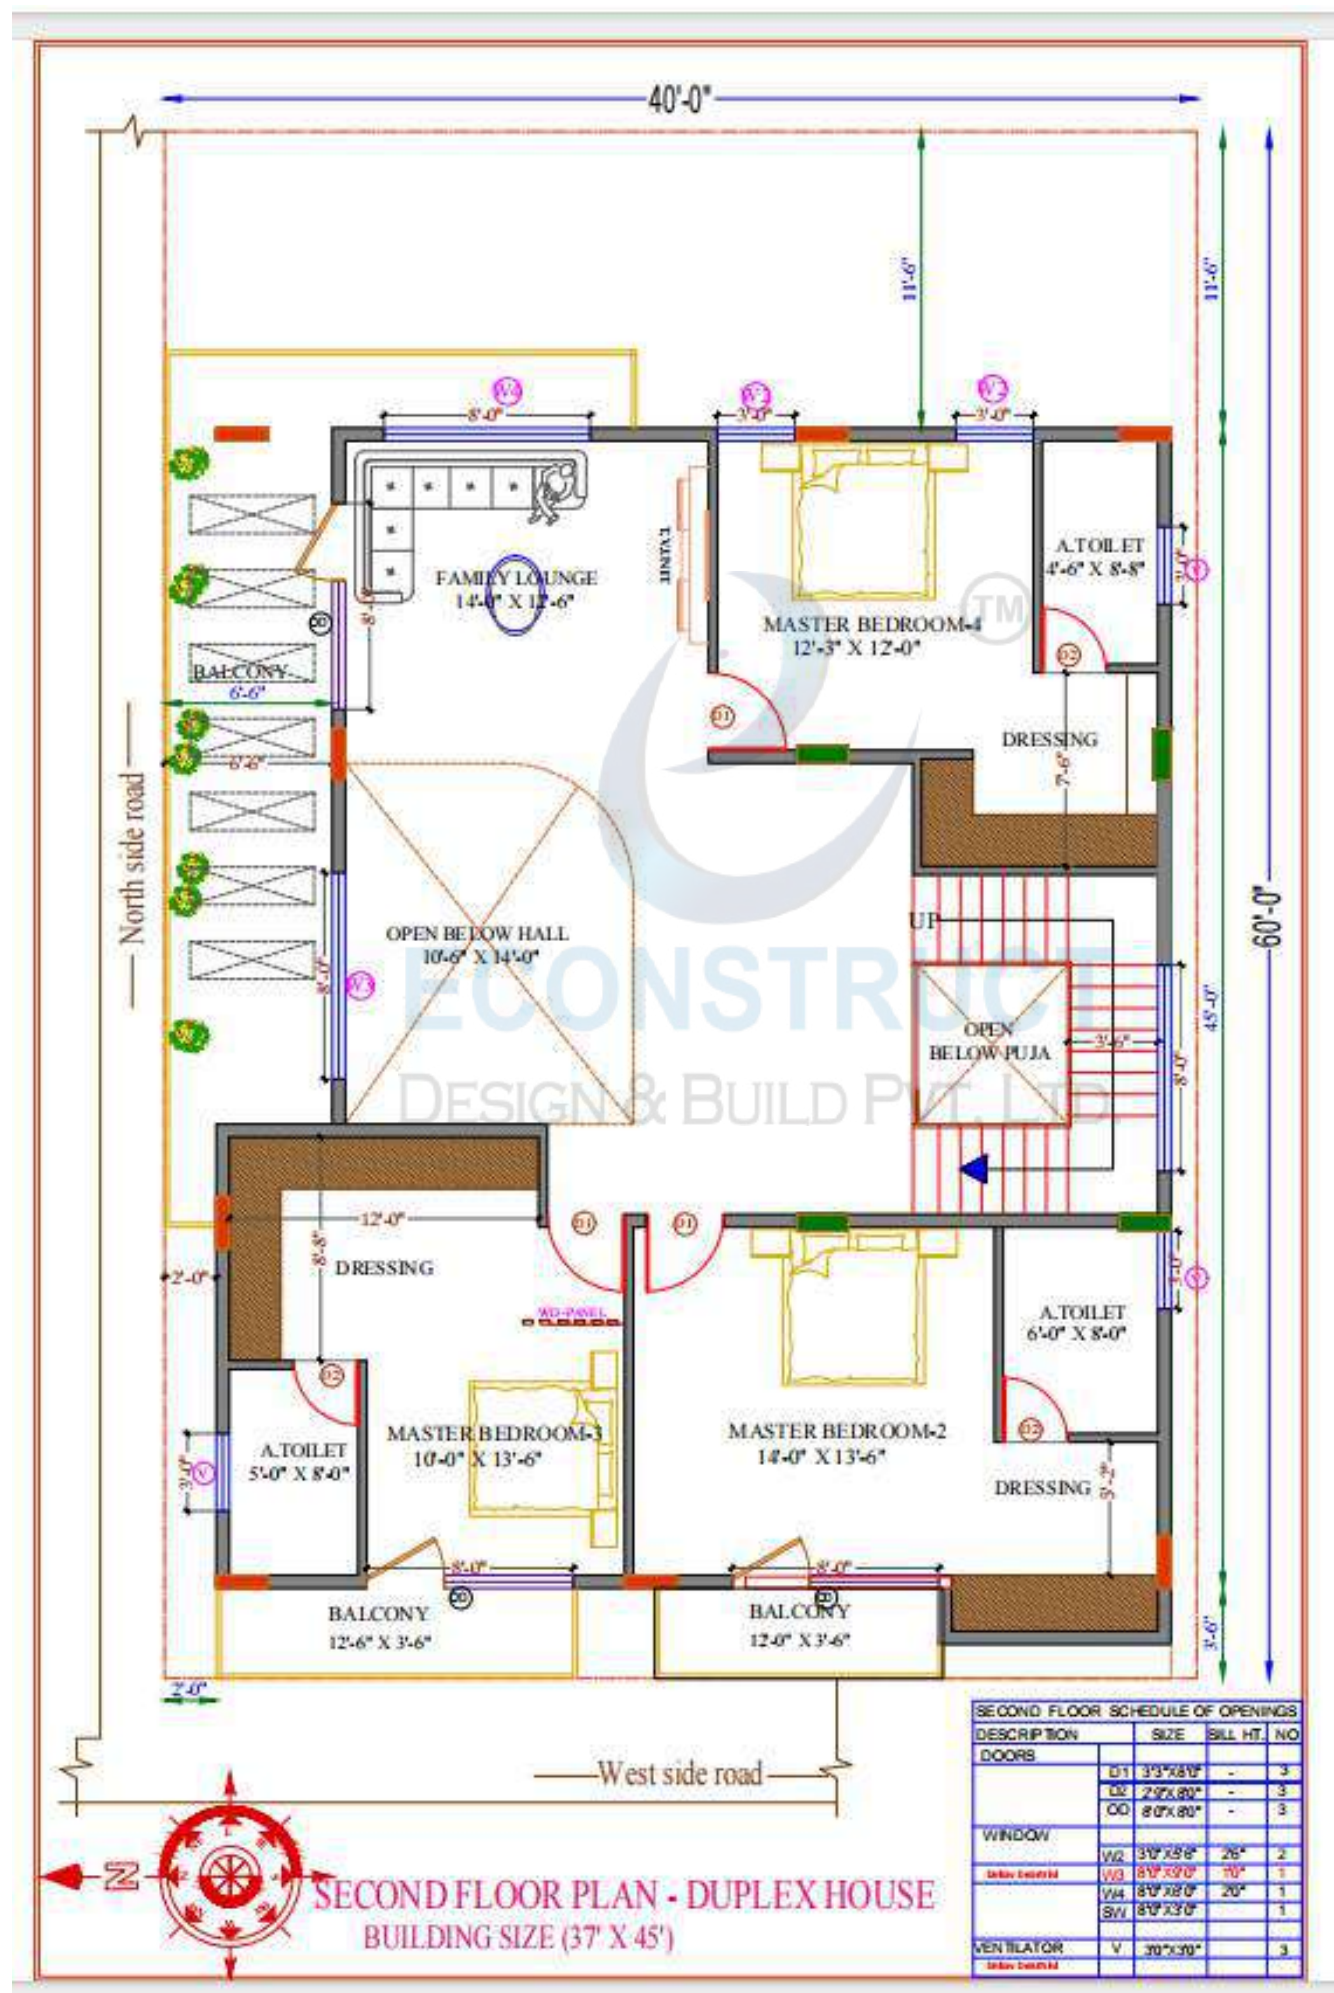


04

TERRACE FLOOR PLAN - DUPLEX HOUSE BUILDING SIZE (37' X 45')

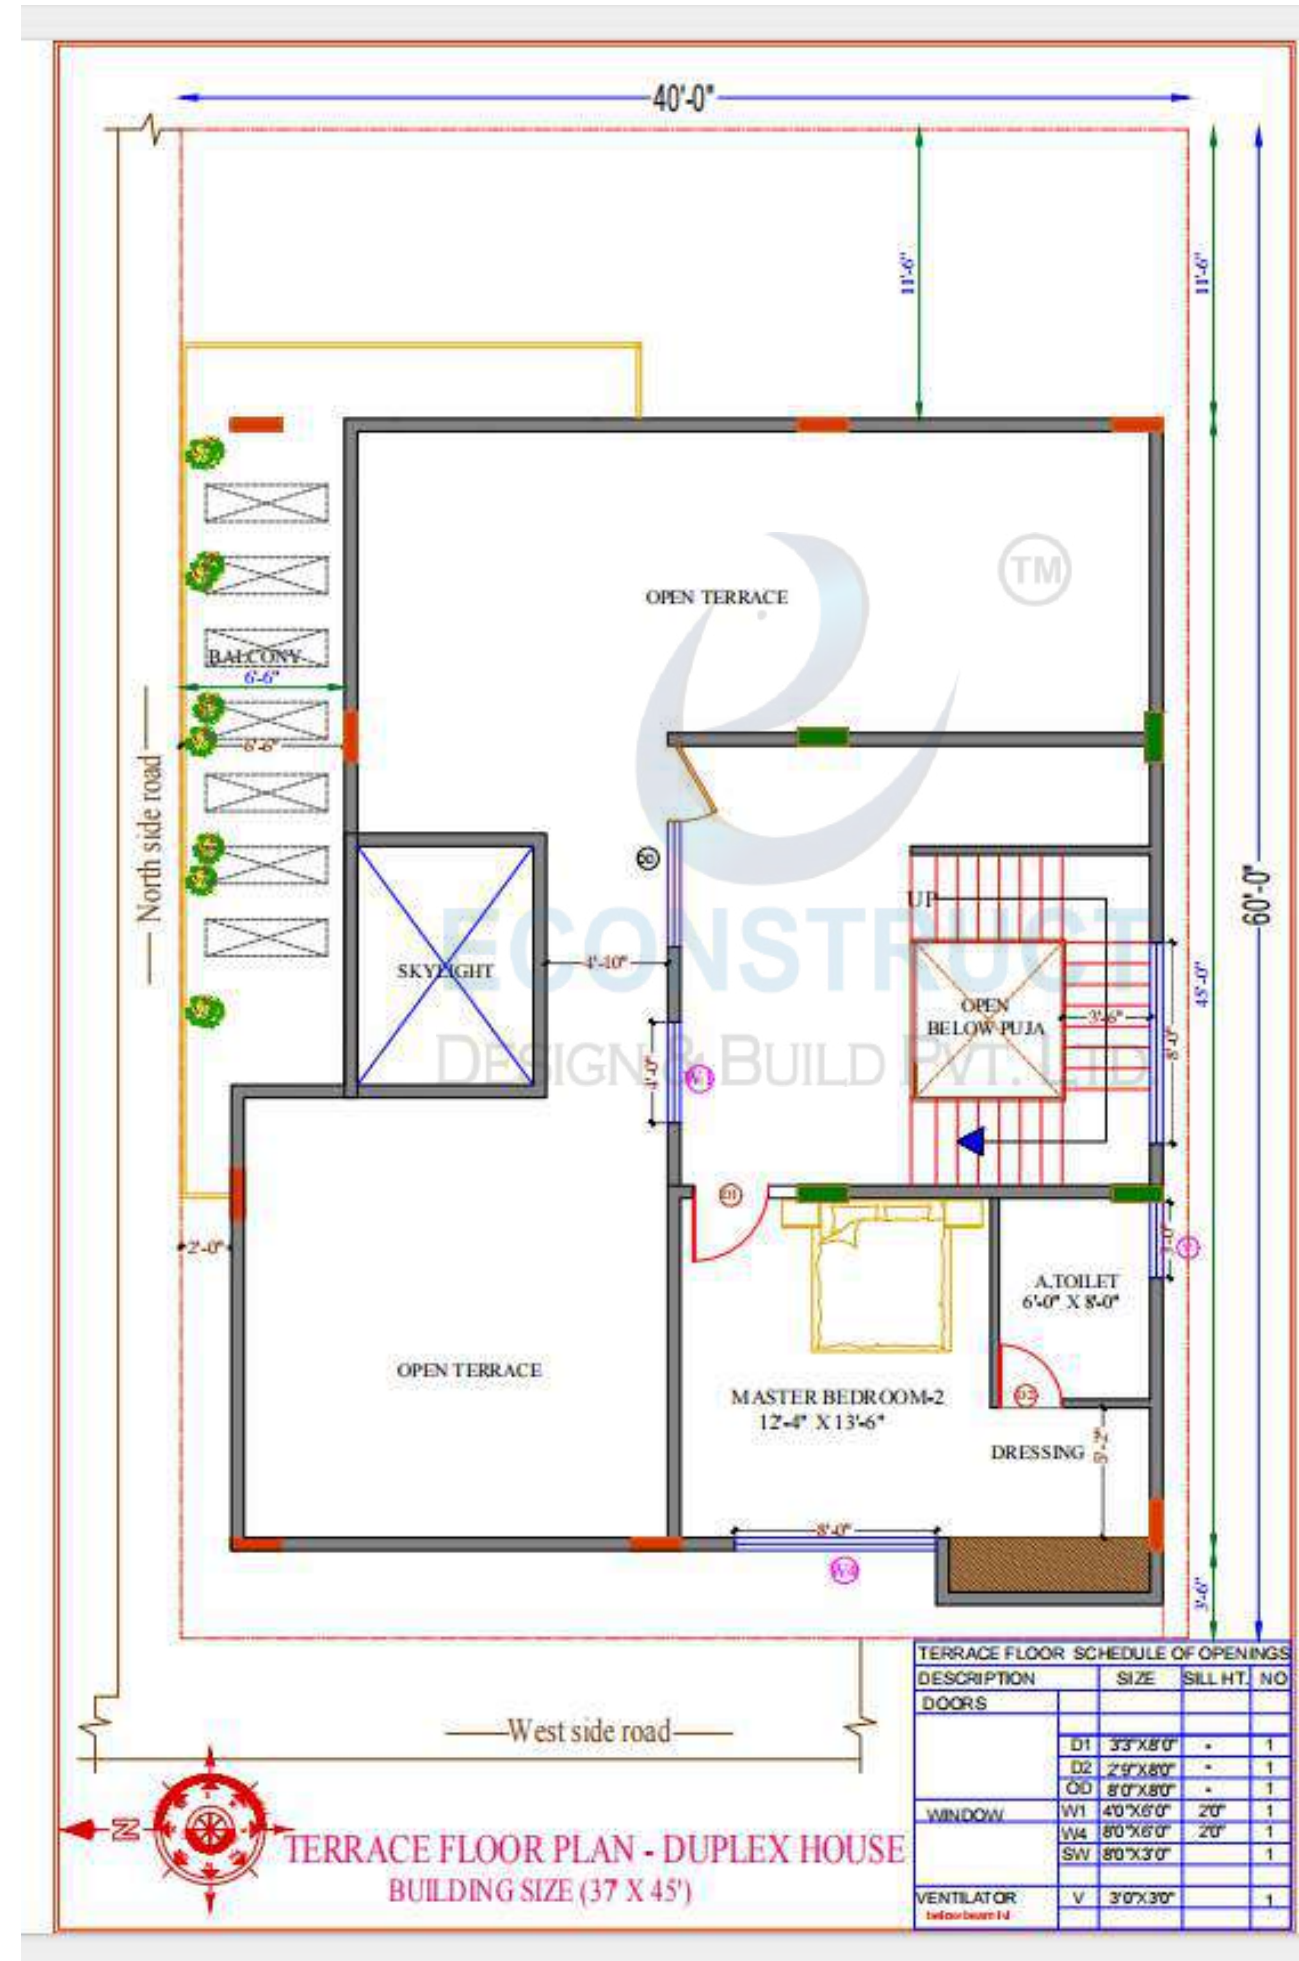


05



SECOND FLOOR WORKING PLAN

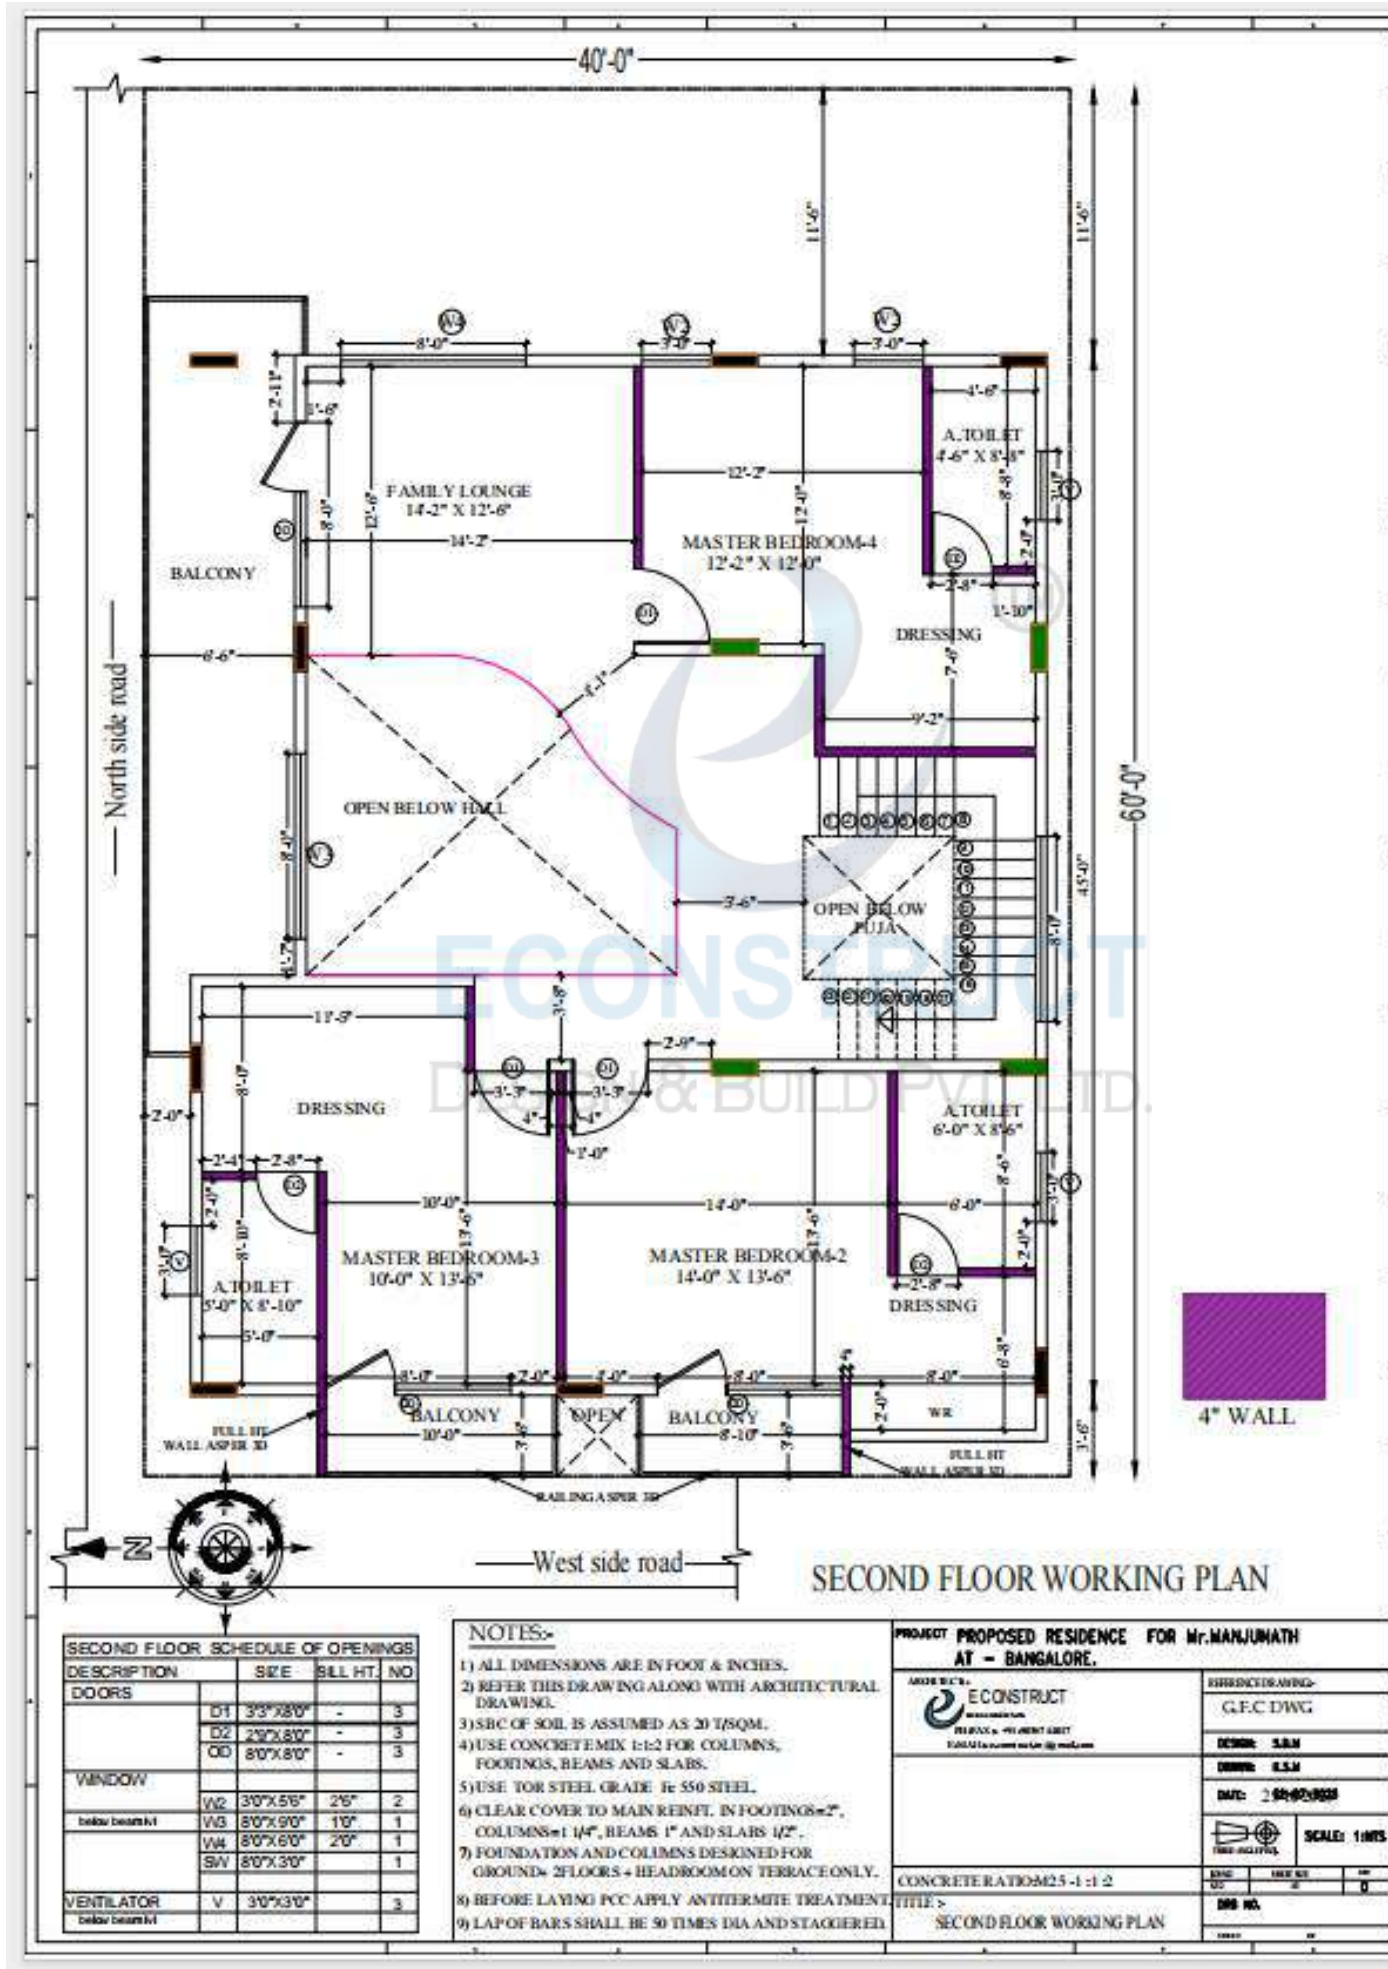

06



TERRACE FLOOR WORKING PLAN

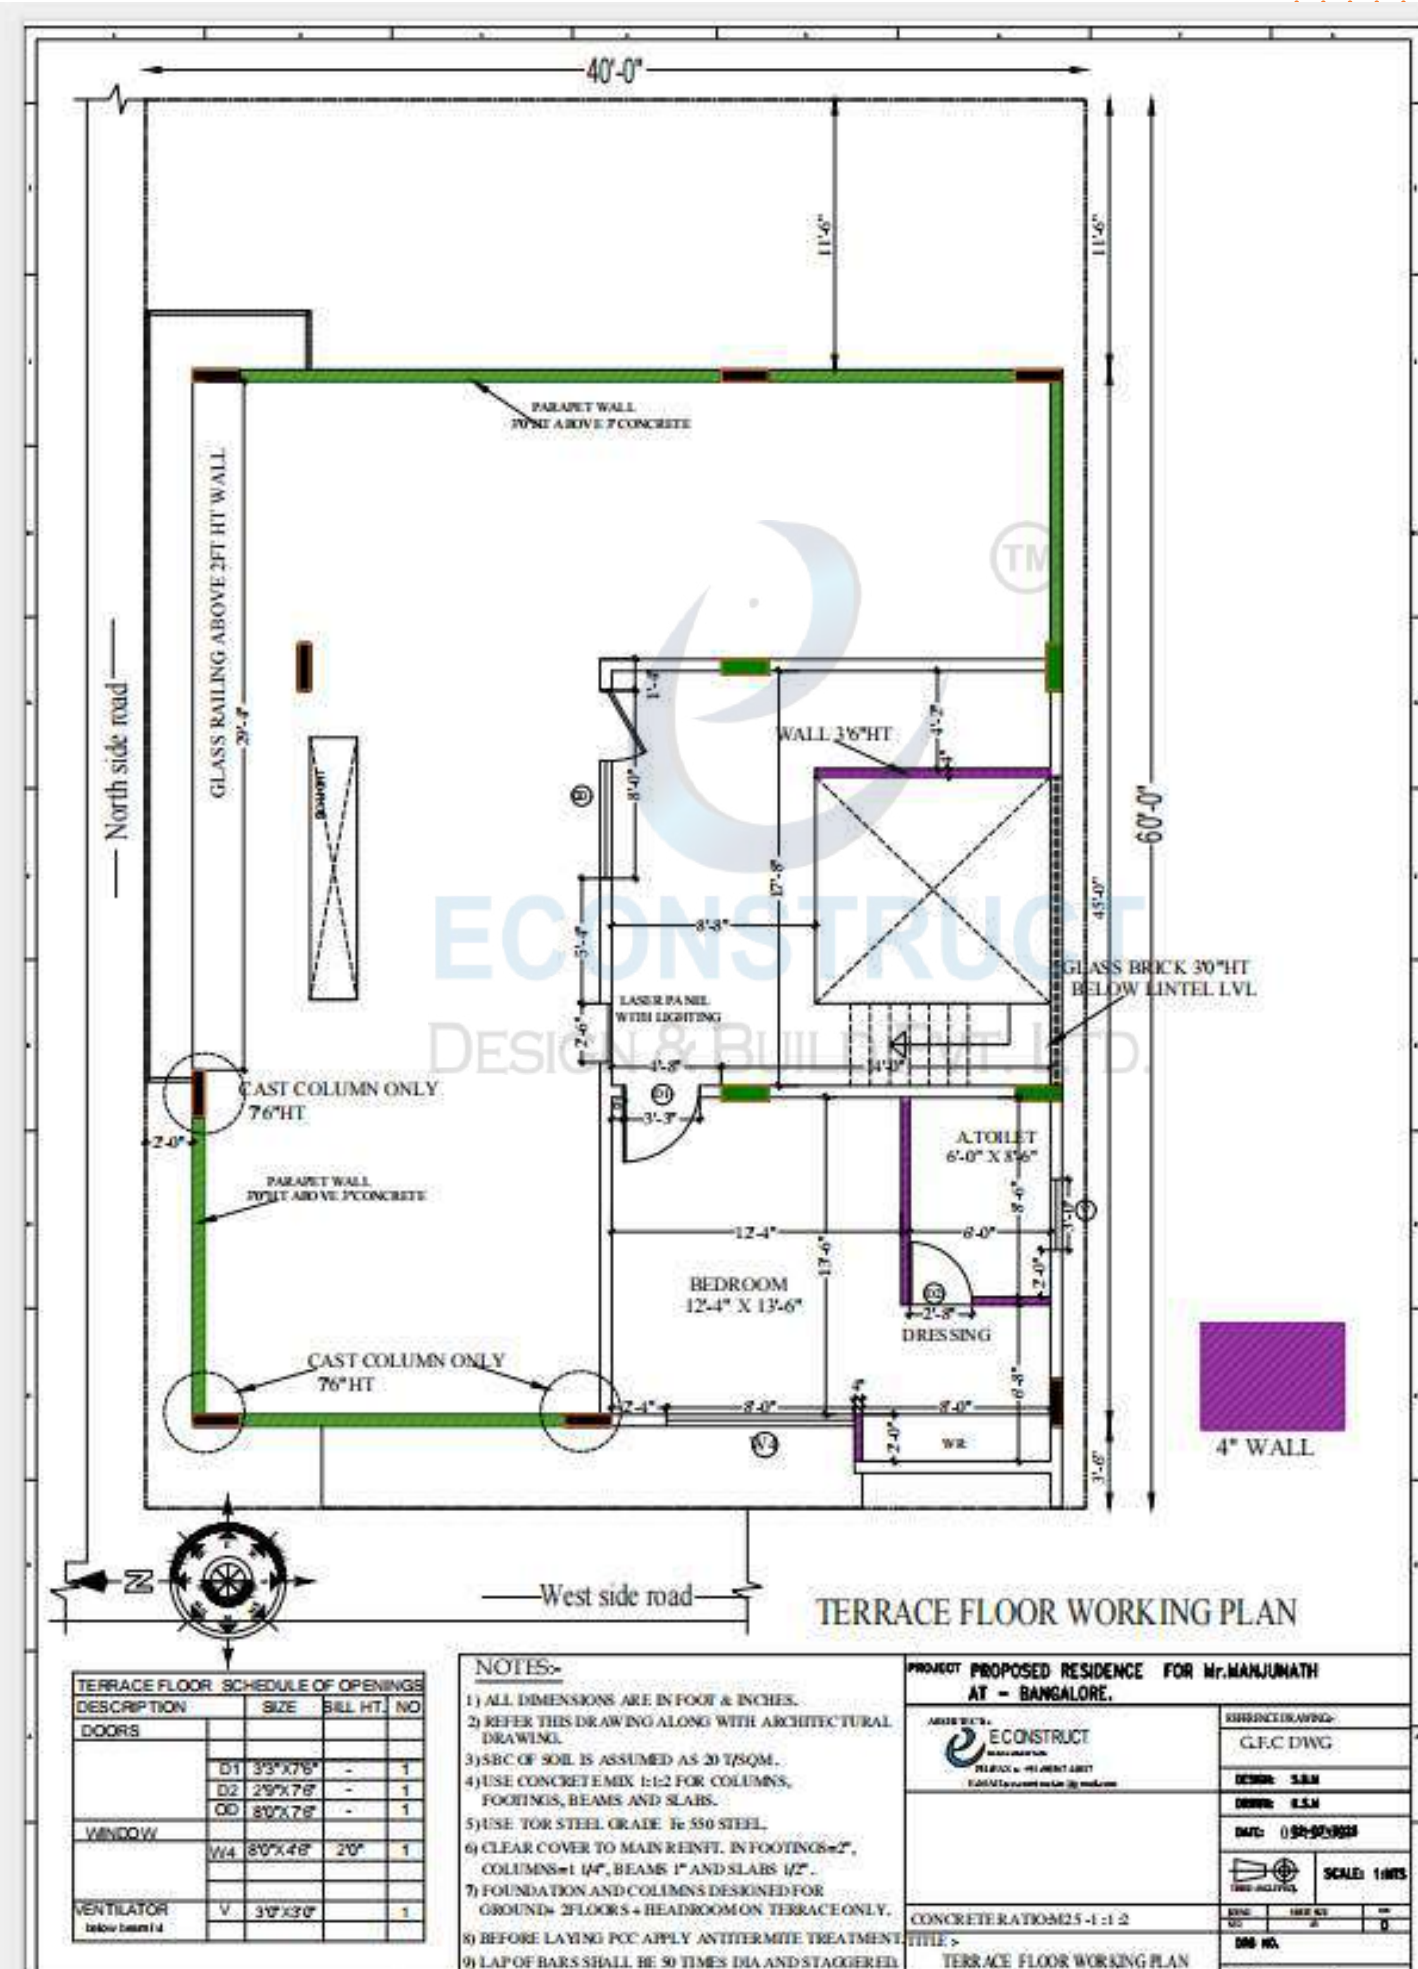

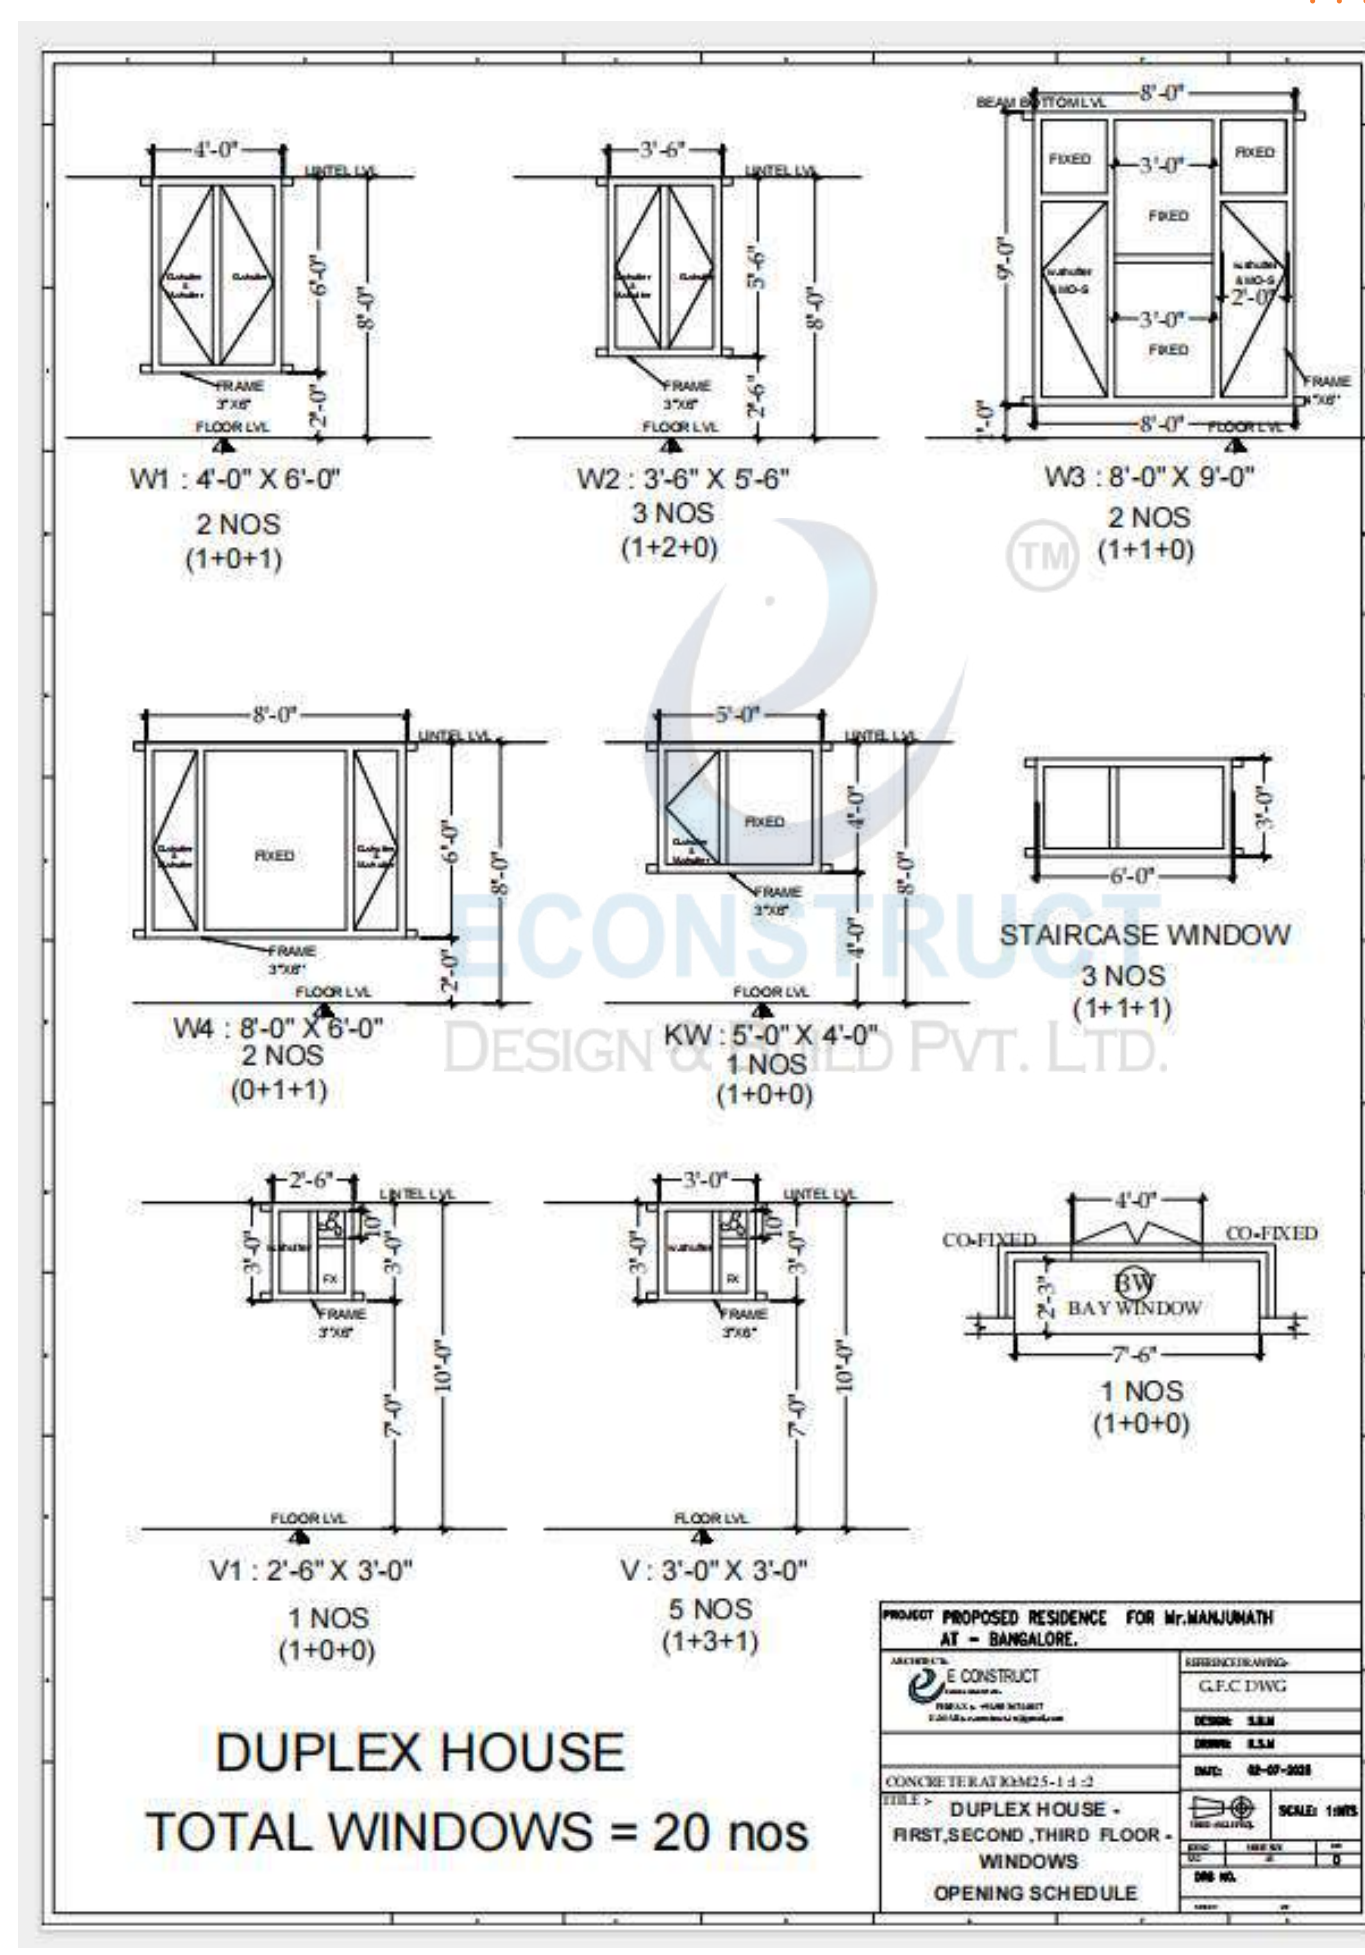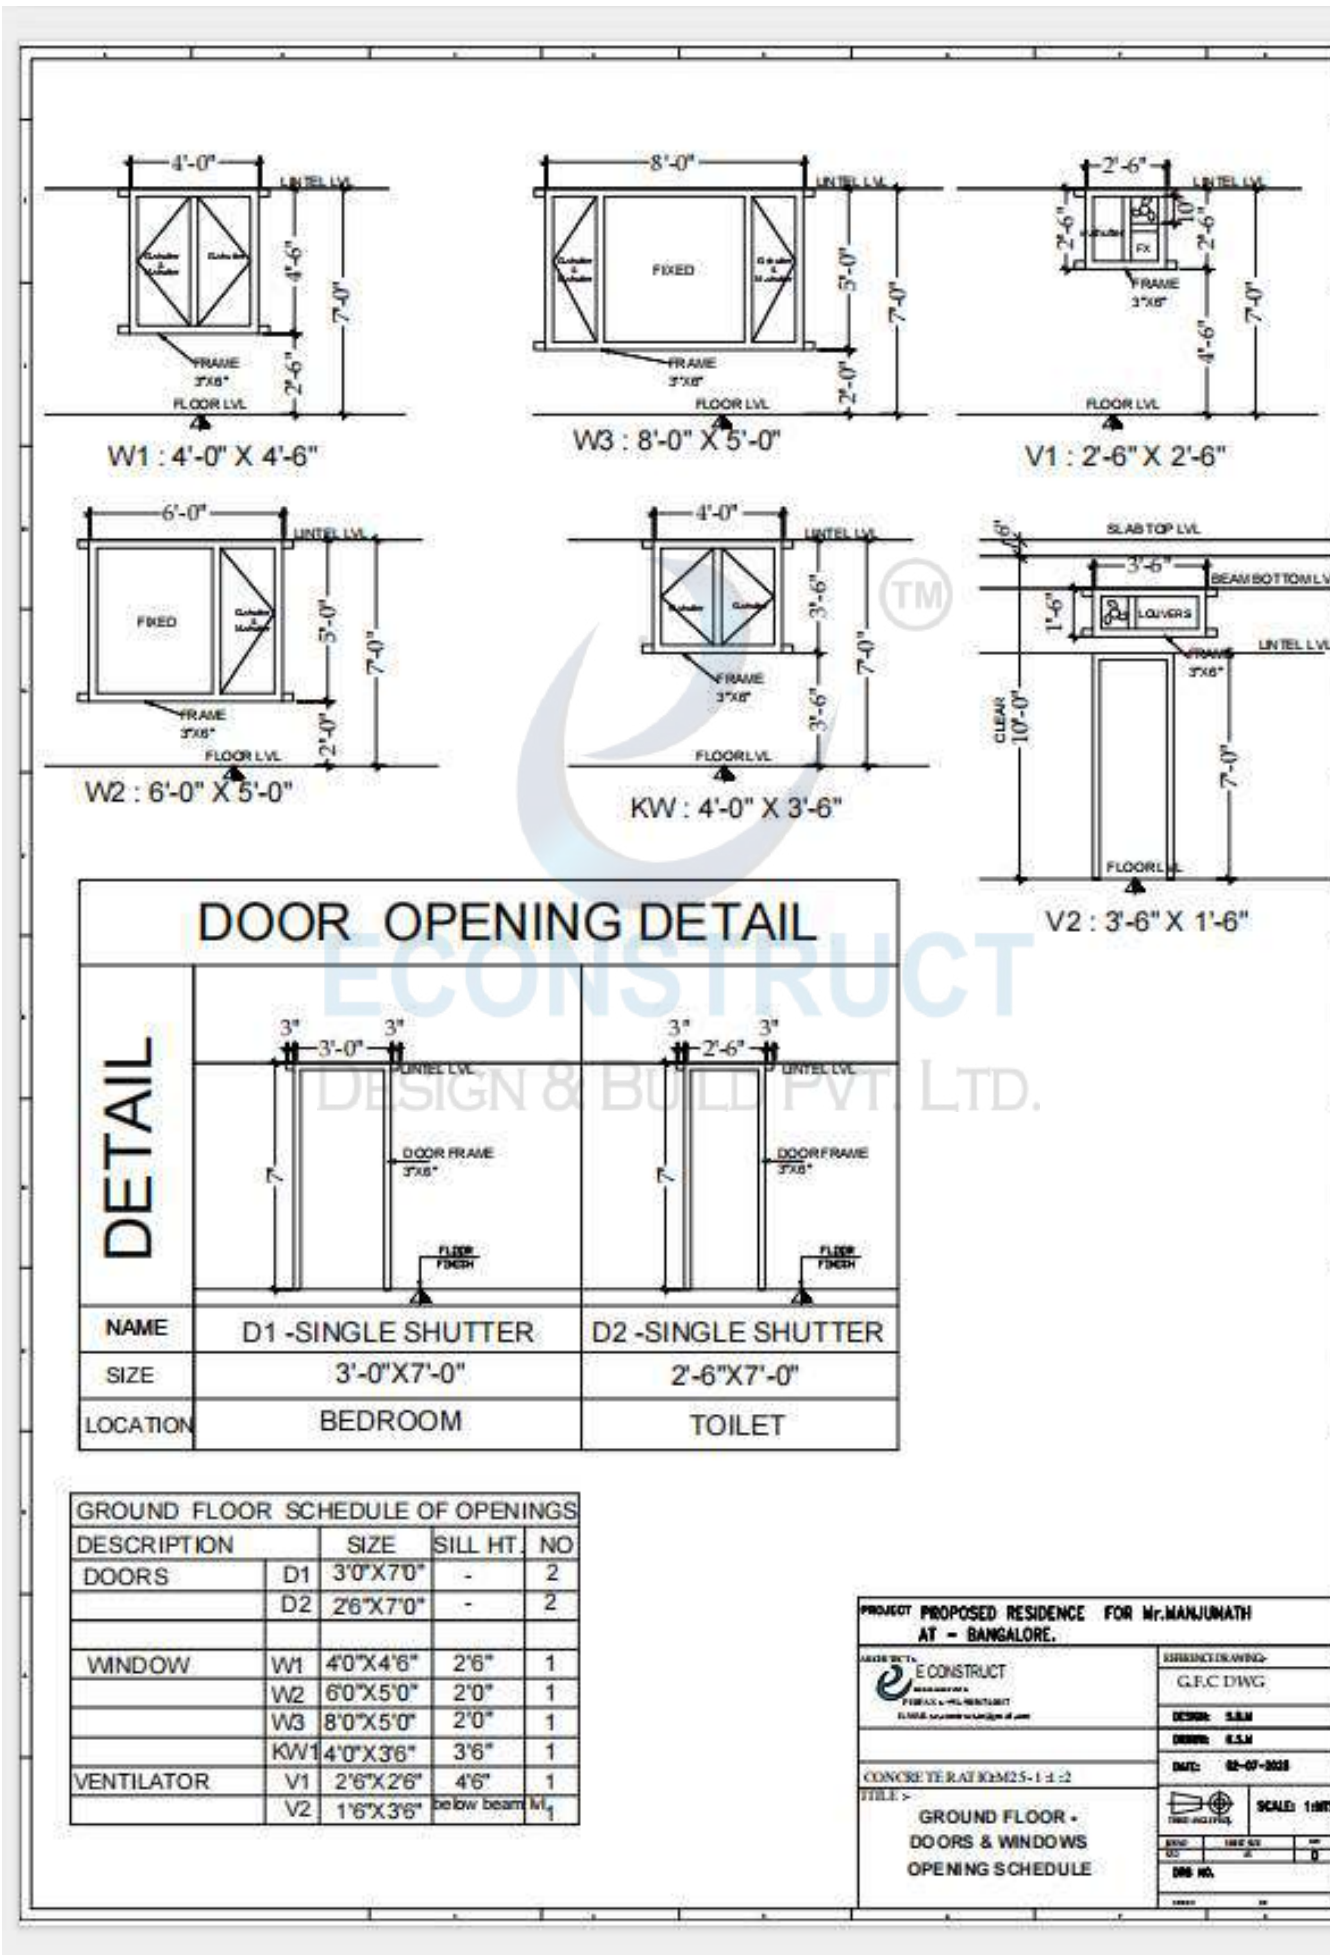


DUPLEX HOUSE
TOTAL DOORS = 20 nos

[illegible]

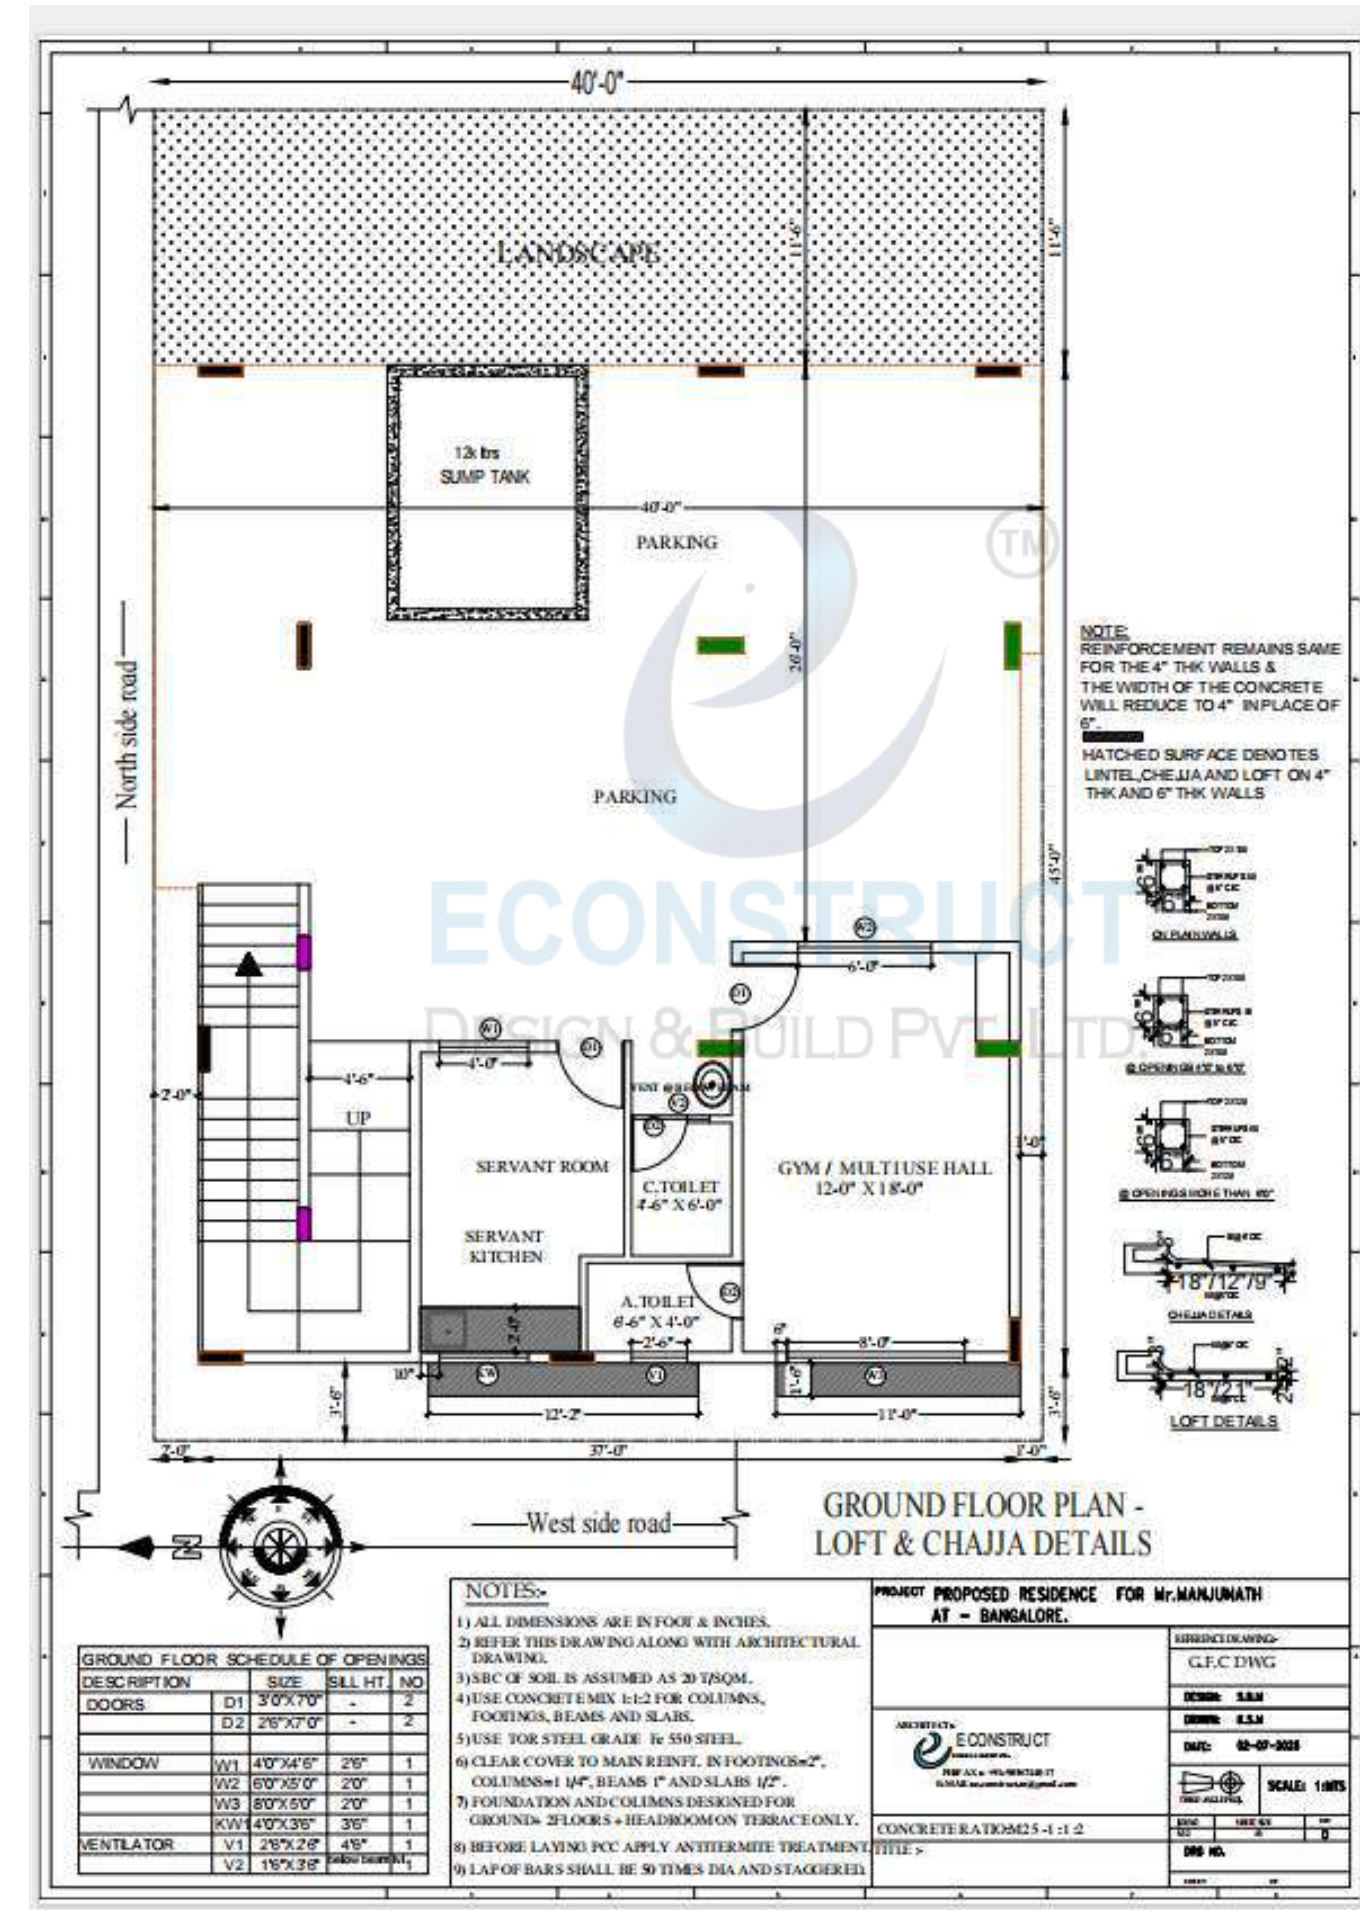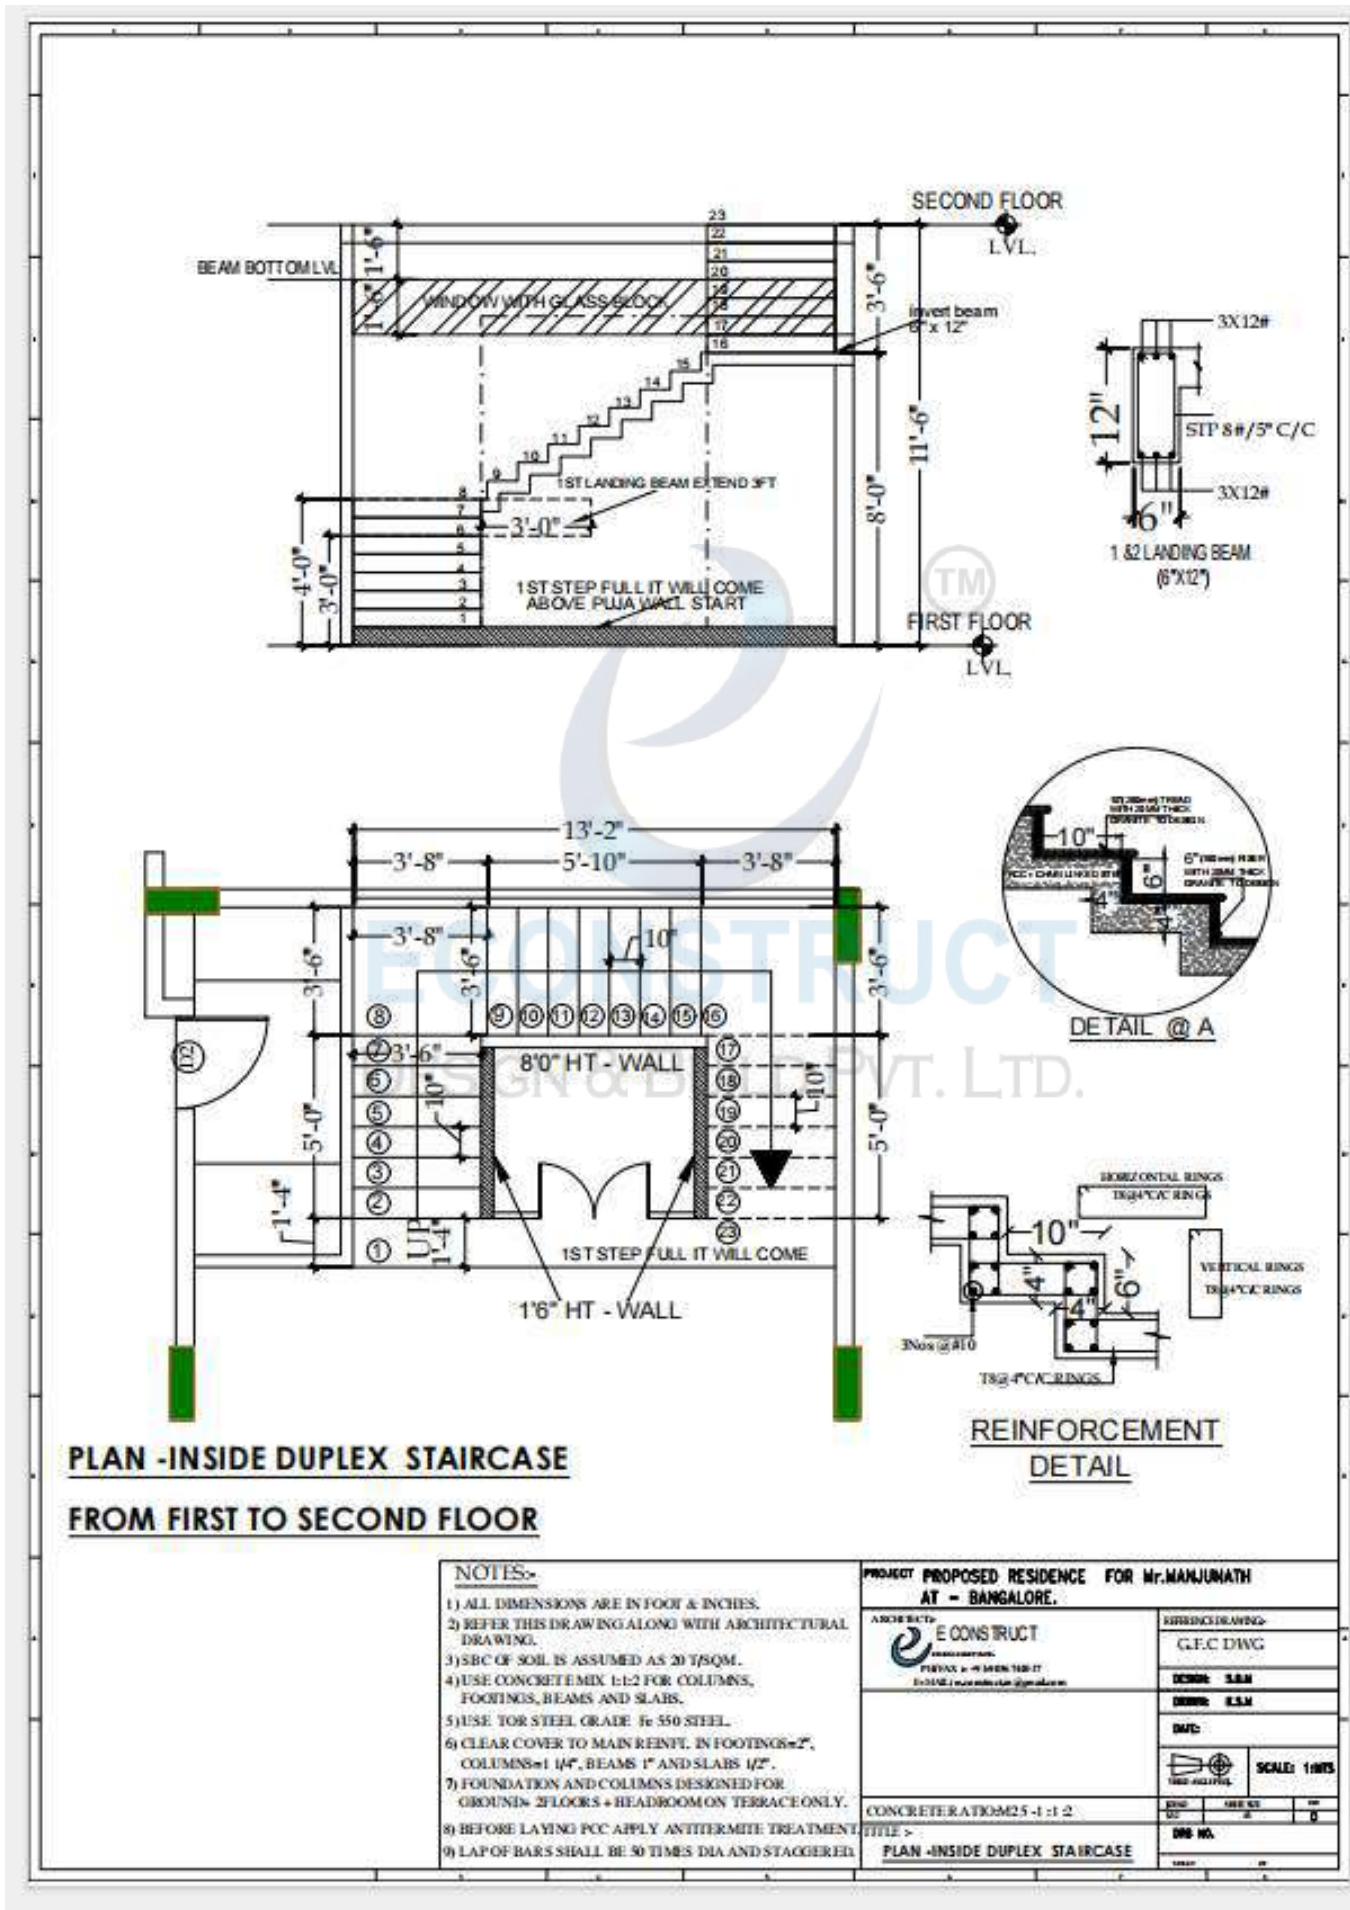


13

FIRST FLOOR PLAN - LOFT & CHAJJA DETAILS

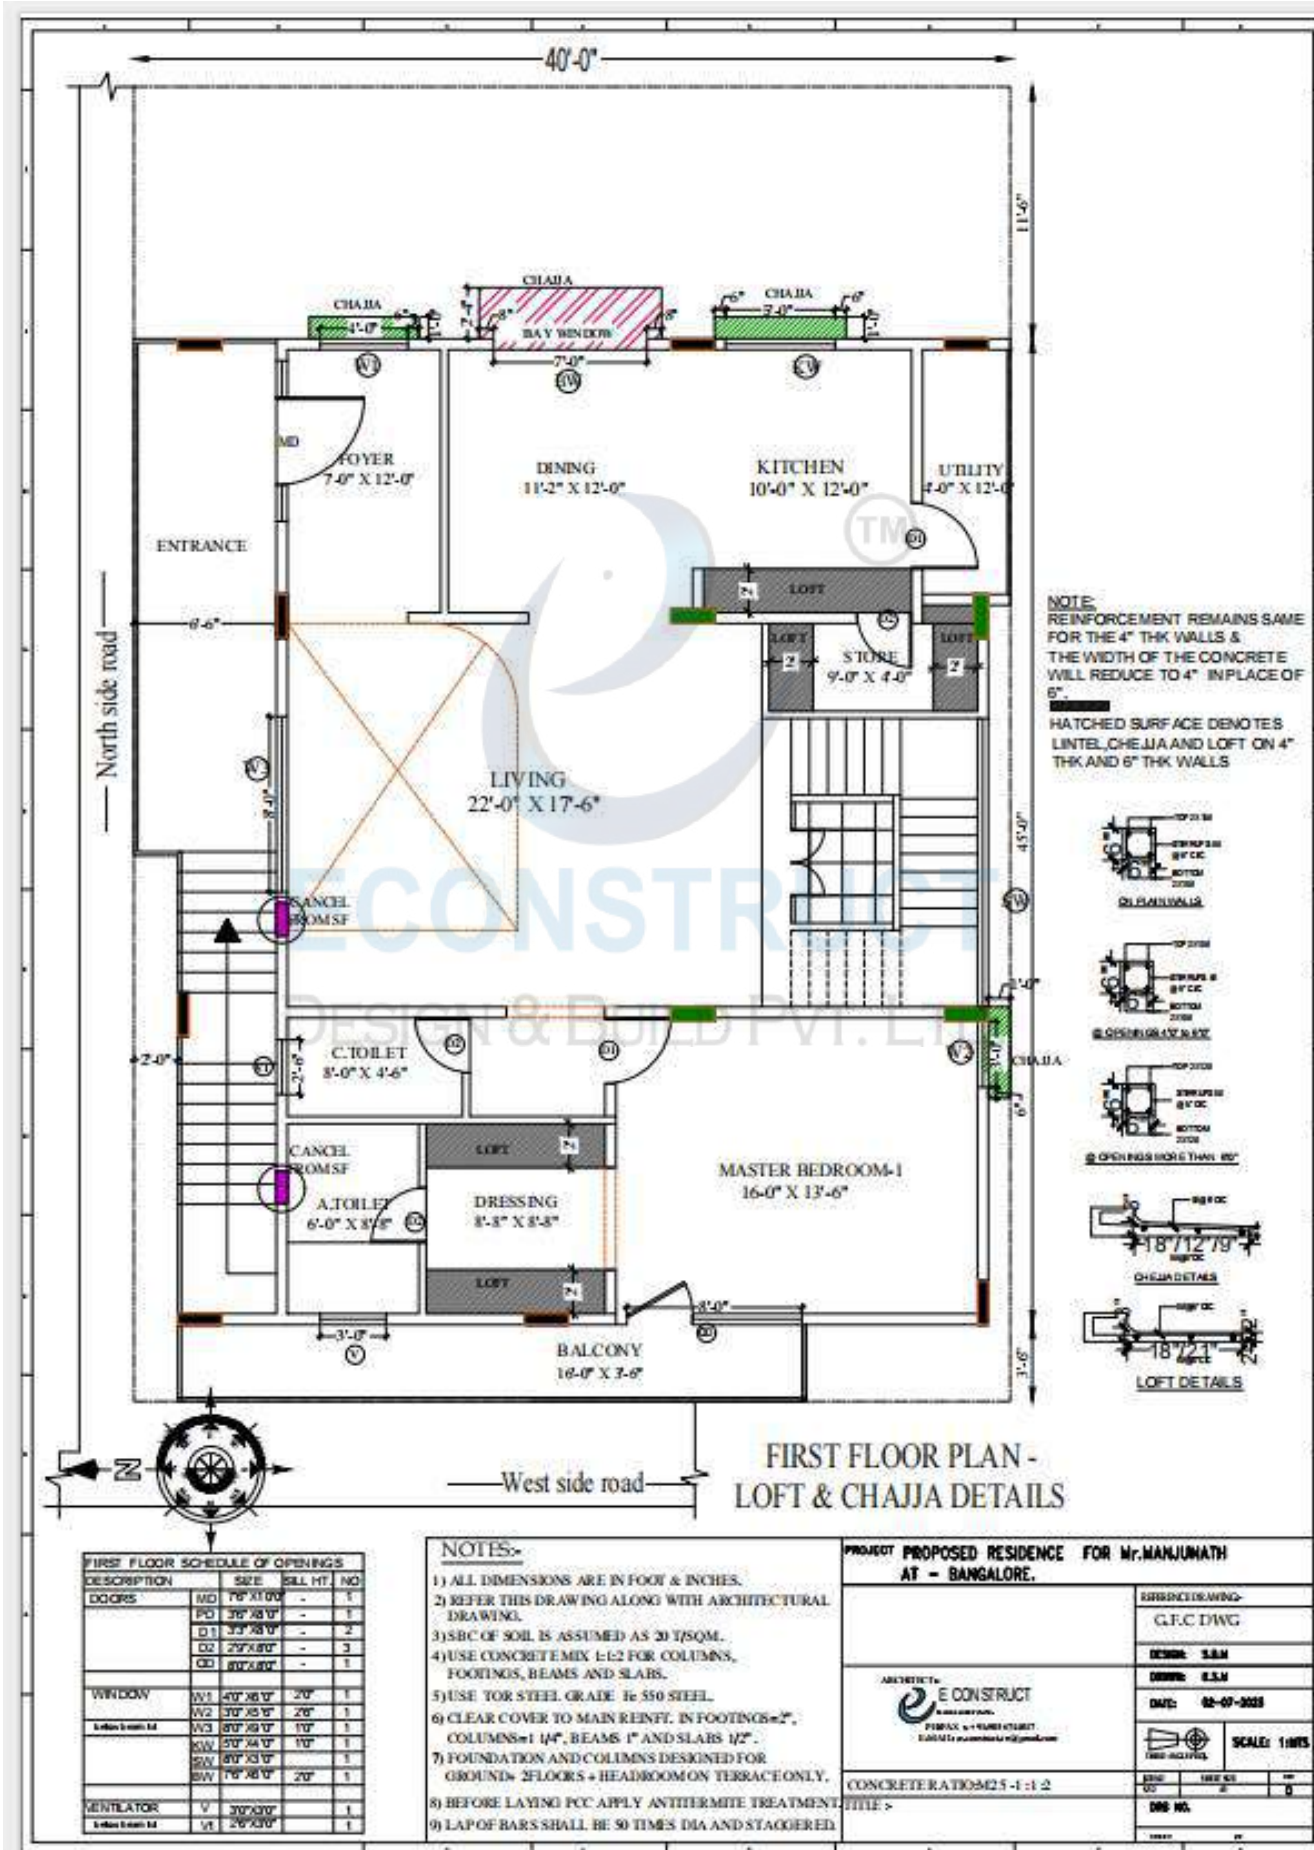


14


SECOND FLOOR PLAN - LOFT & CHAJJA DETAILS

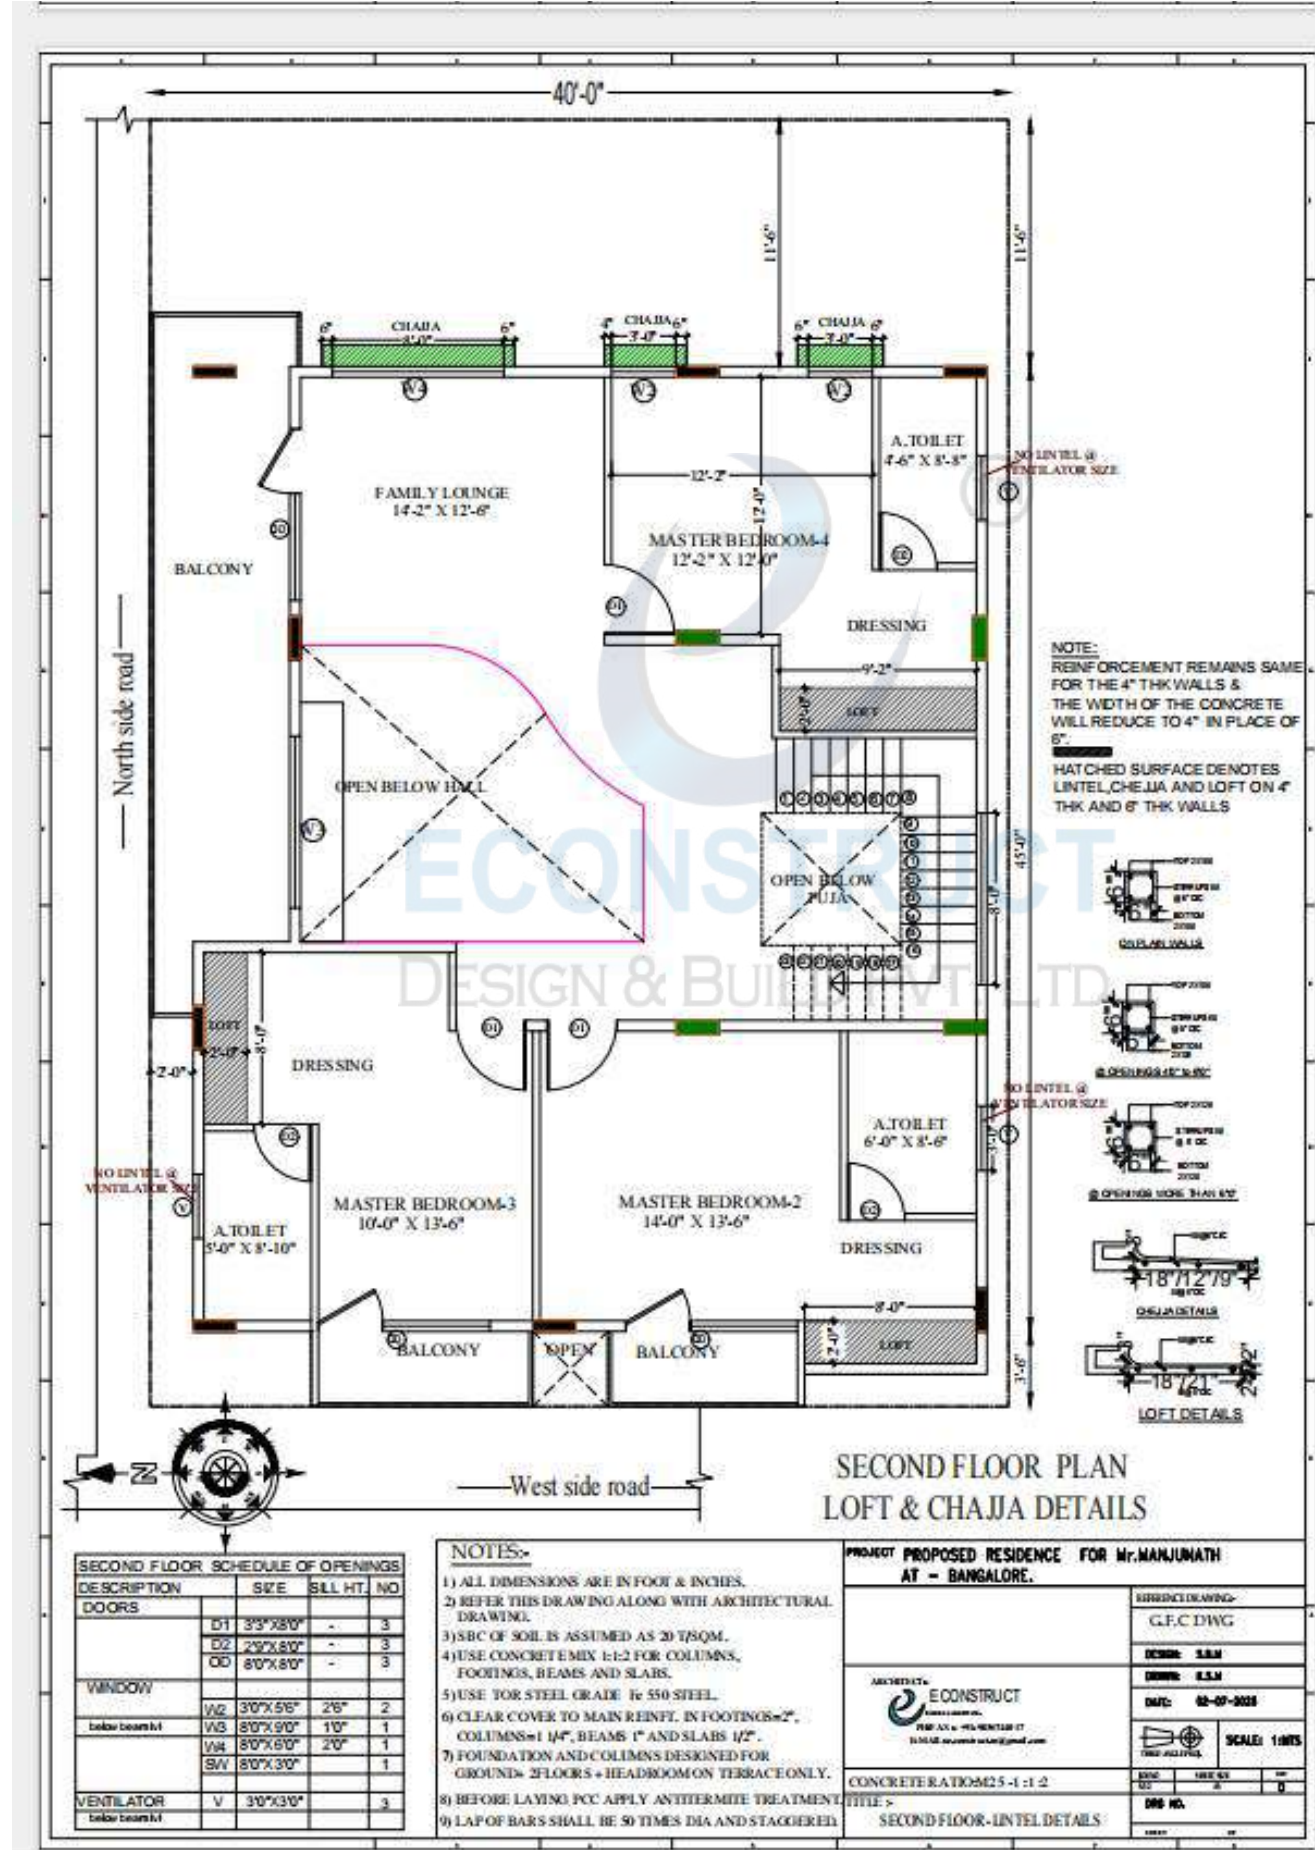


GROUND FLOOR PLAN (RVSD) (ELECTRICAL CEILING FIXTURE LAYOUT)

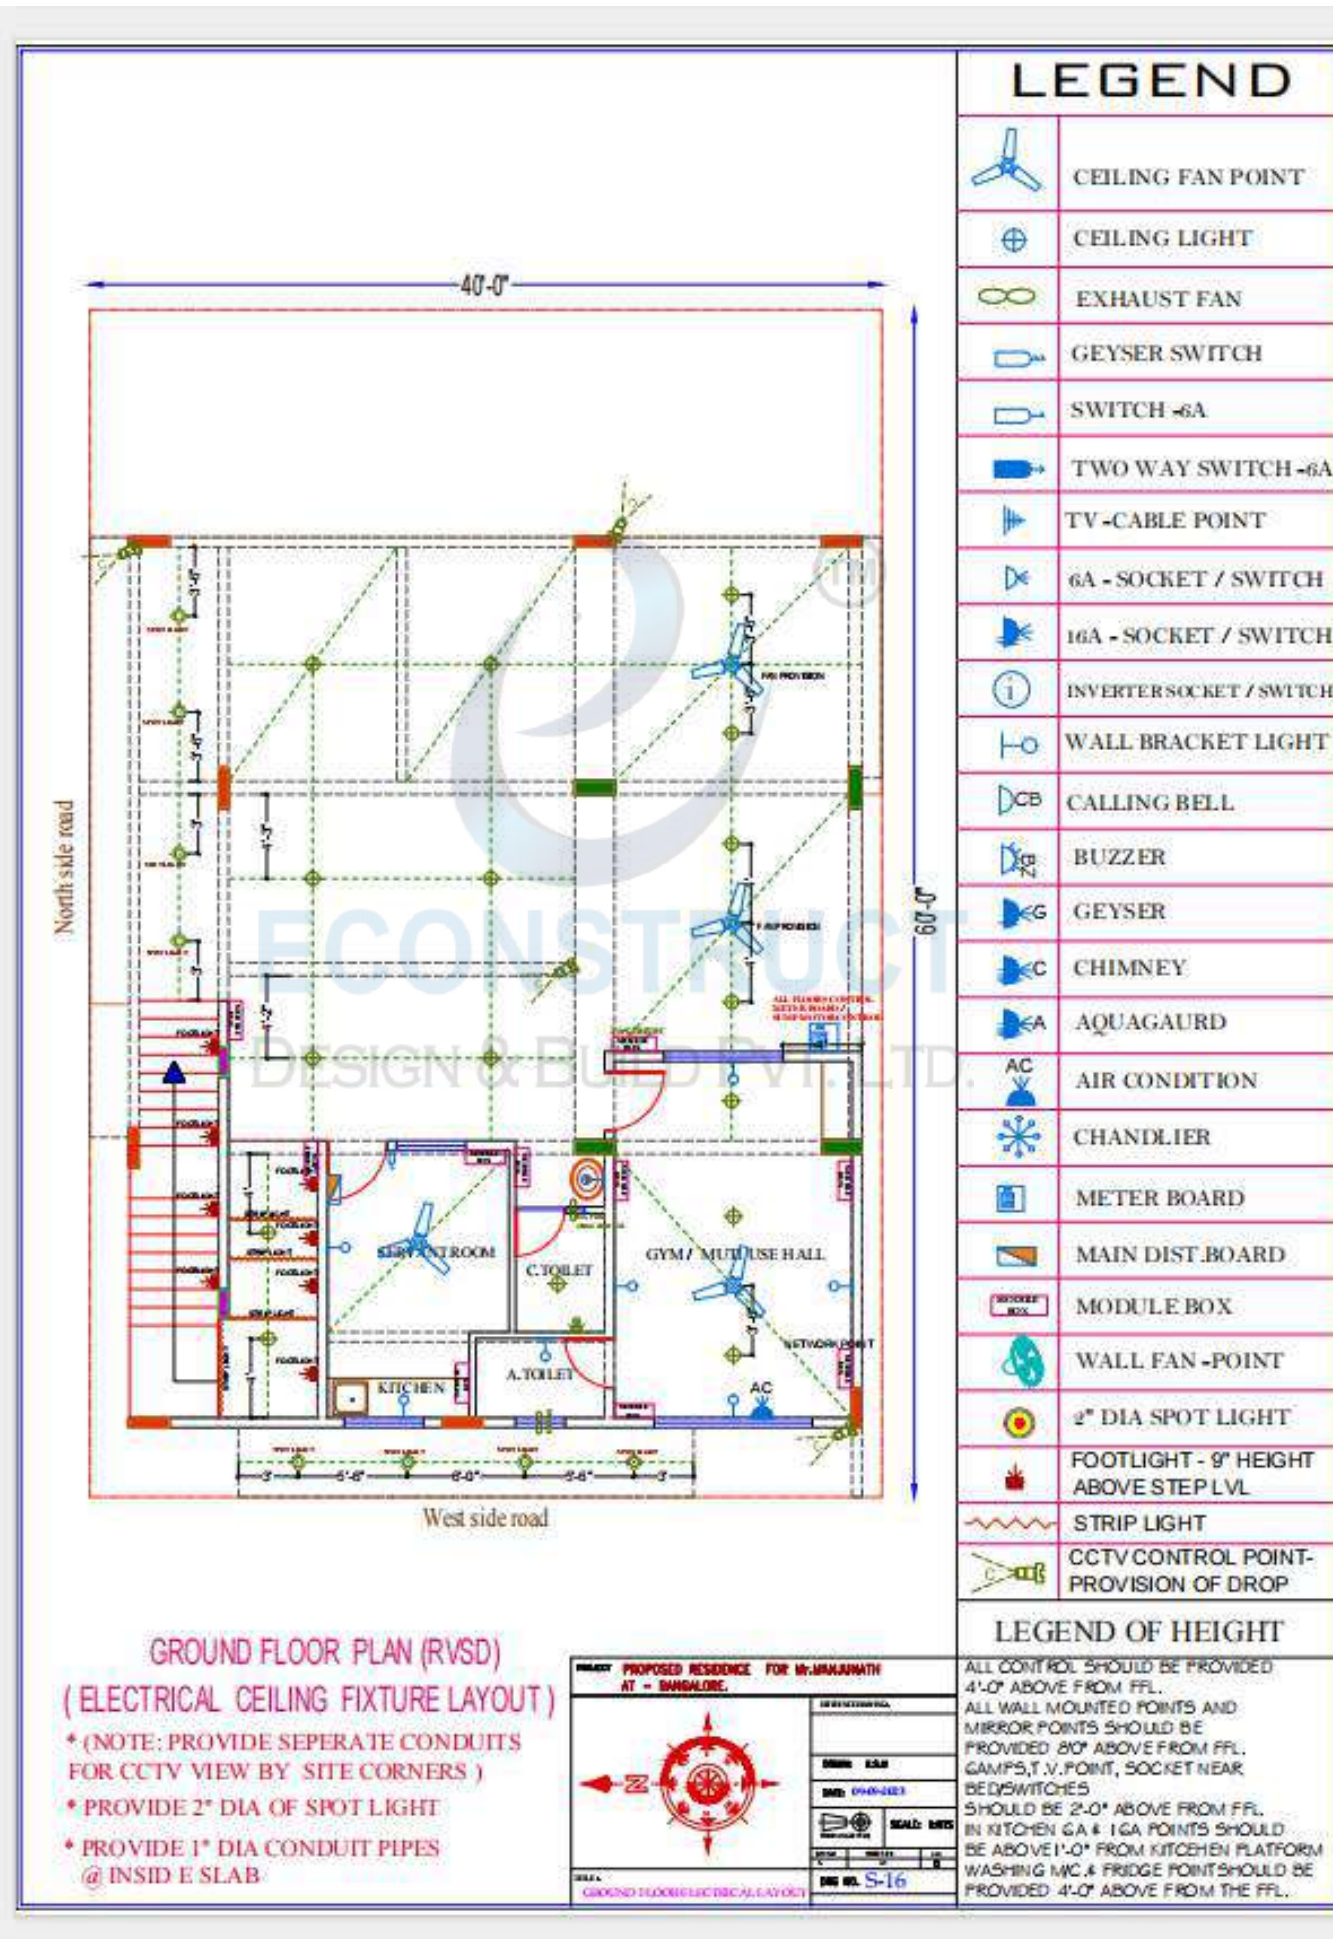


FIRST FLOOR PLAN PROVISION OF DROP (ELECTRICAL CEILING FIXTURE LAYOUT)


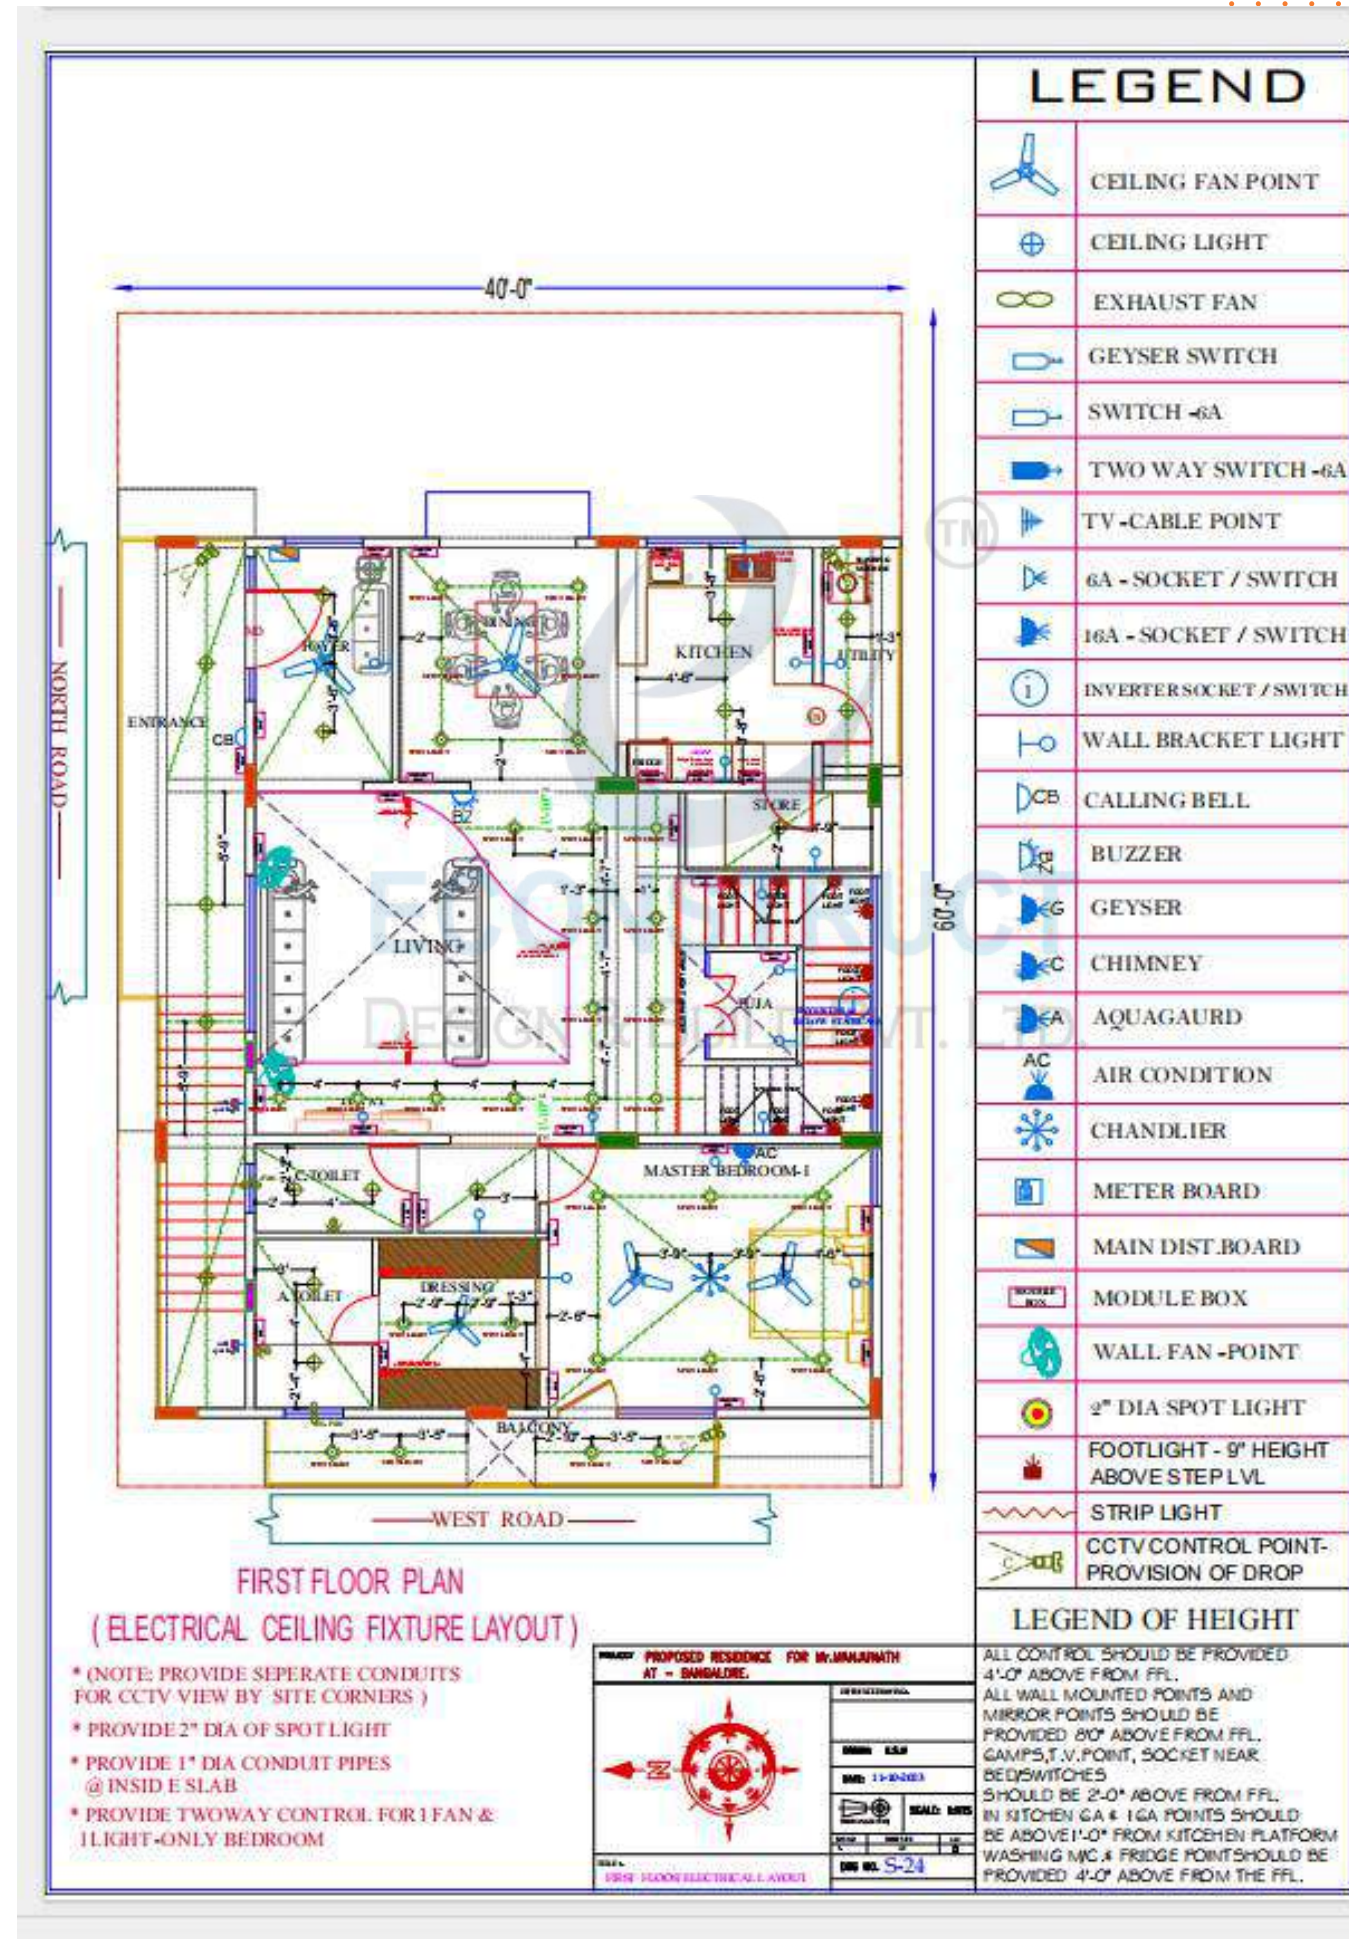


SECOND FLOOR PLAN PROVISION OF DROP (ELECTRICAL CEILING FIXTURE LAYOUT)

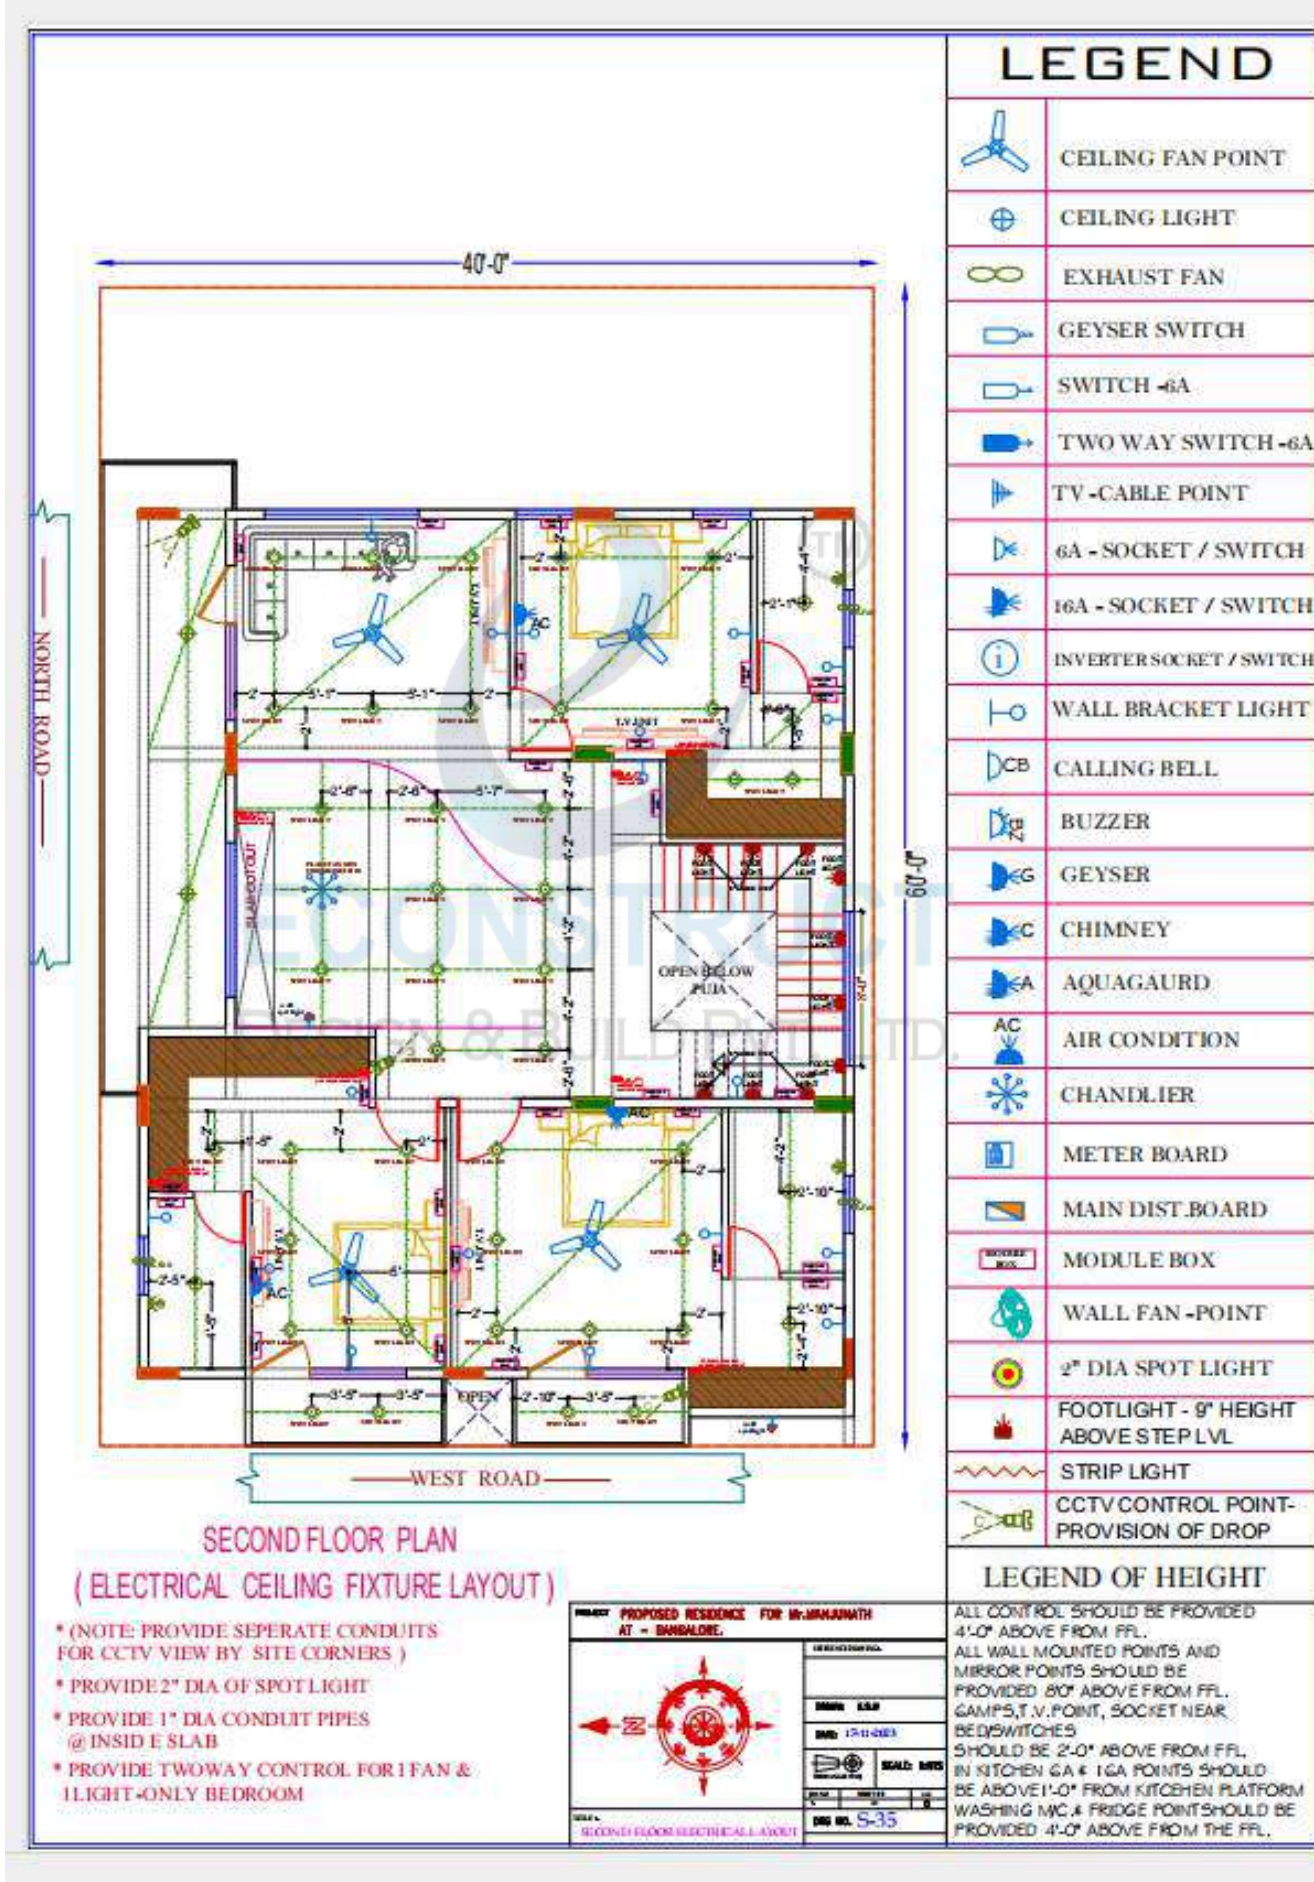


TERRACE FLOOR PLAN - (ELECTRICAL CEILING FIXTURE LAYOUT)

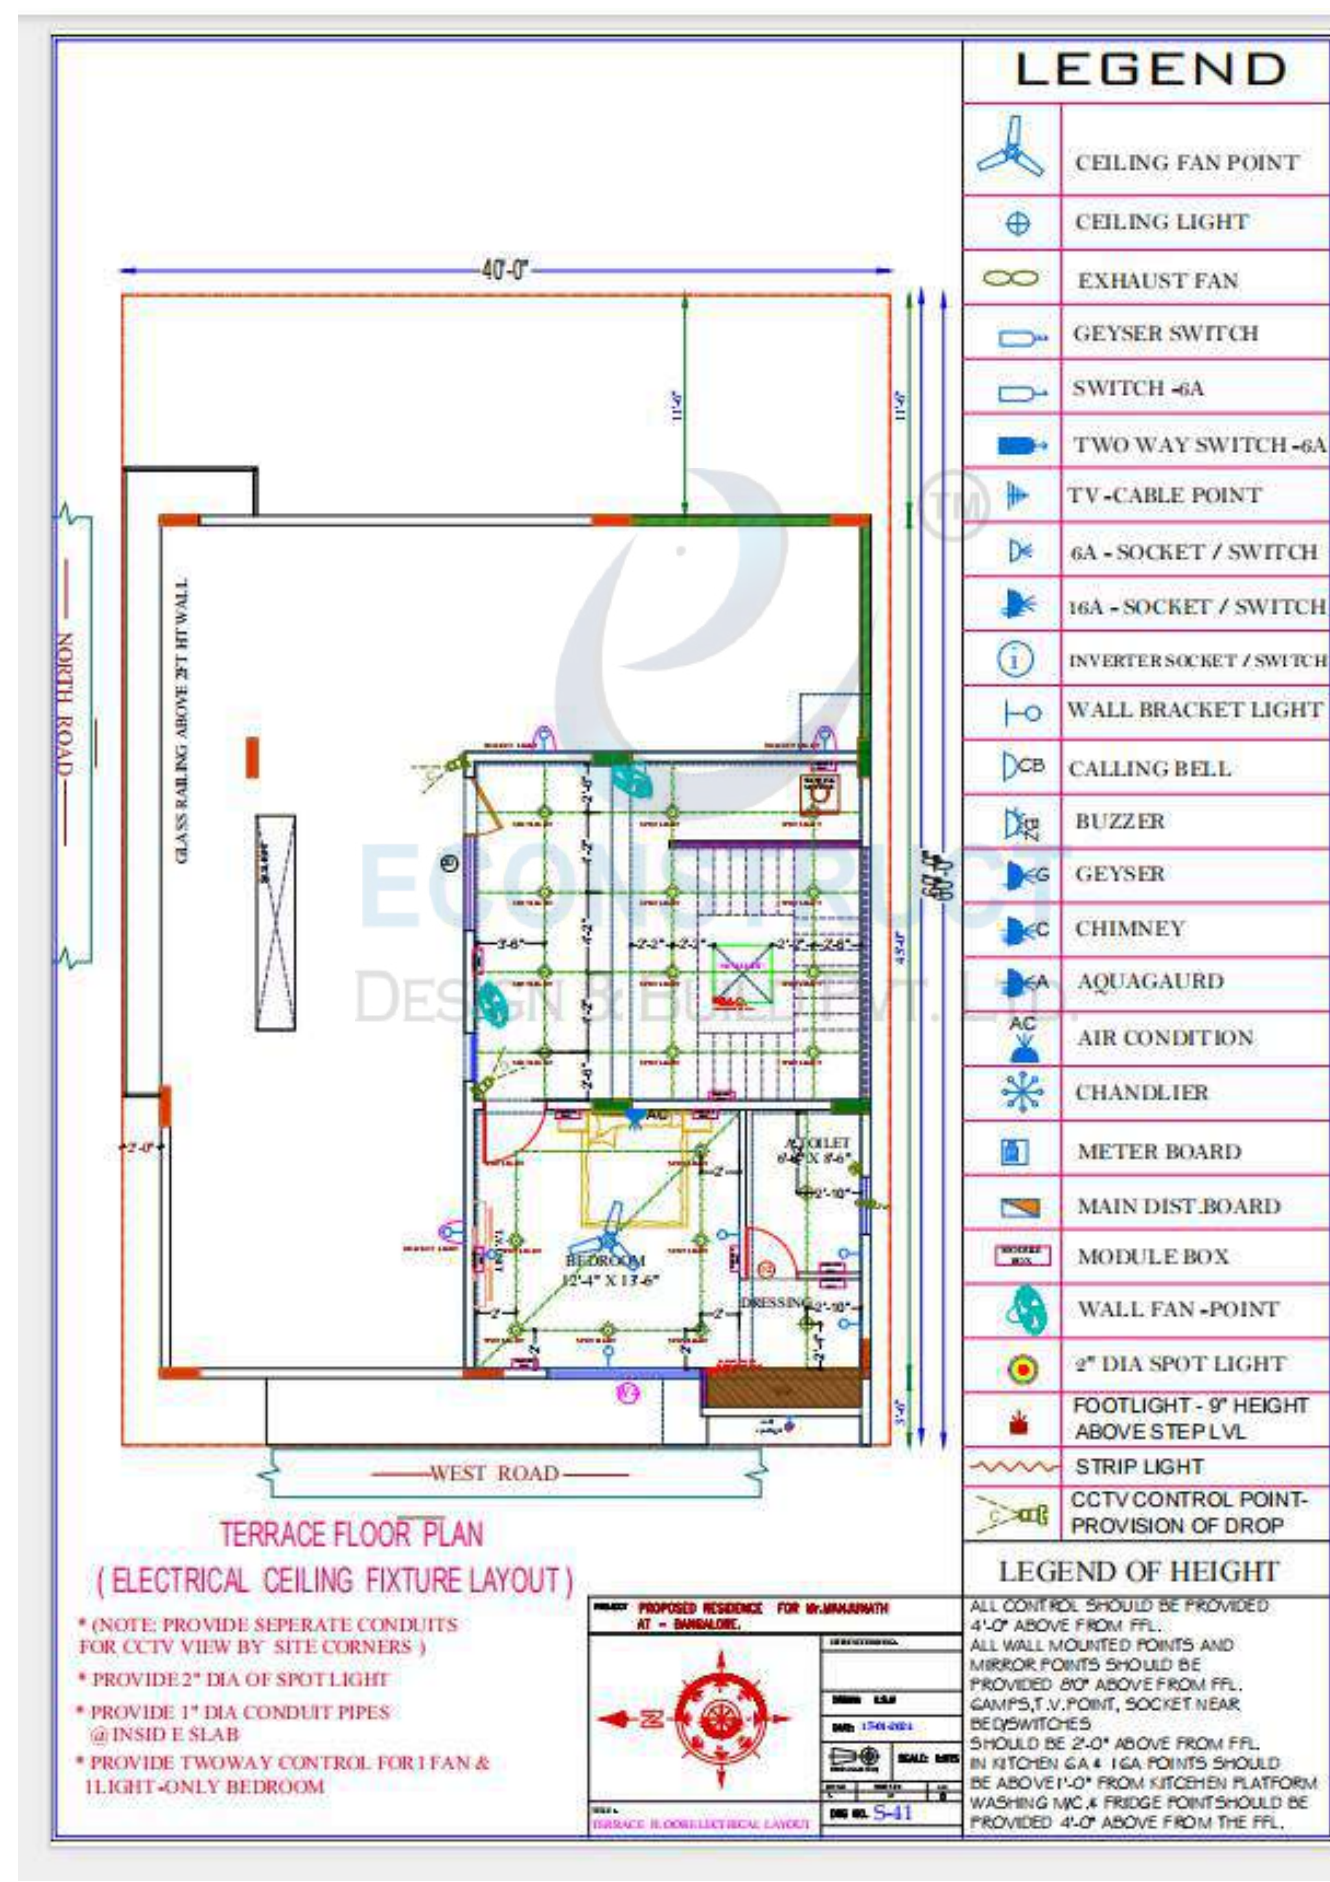

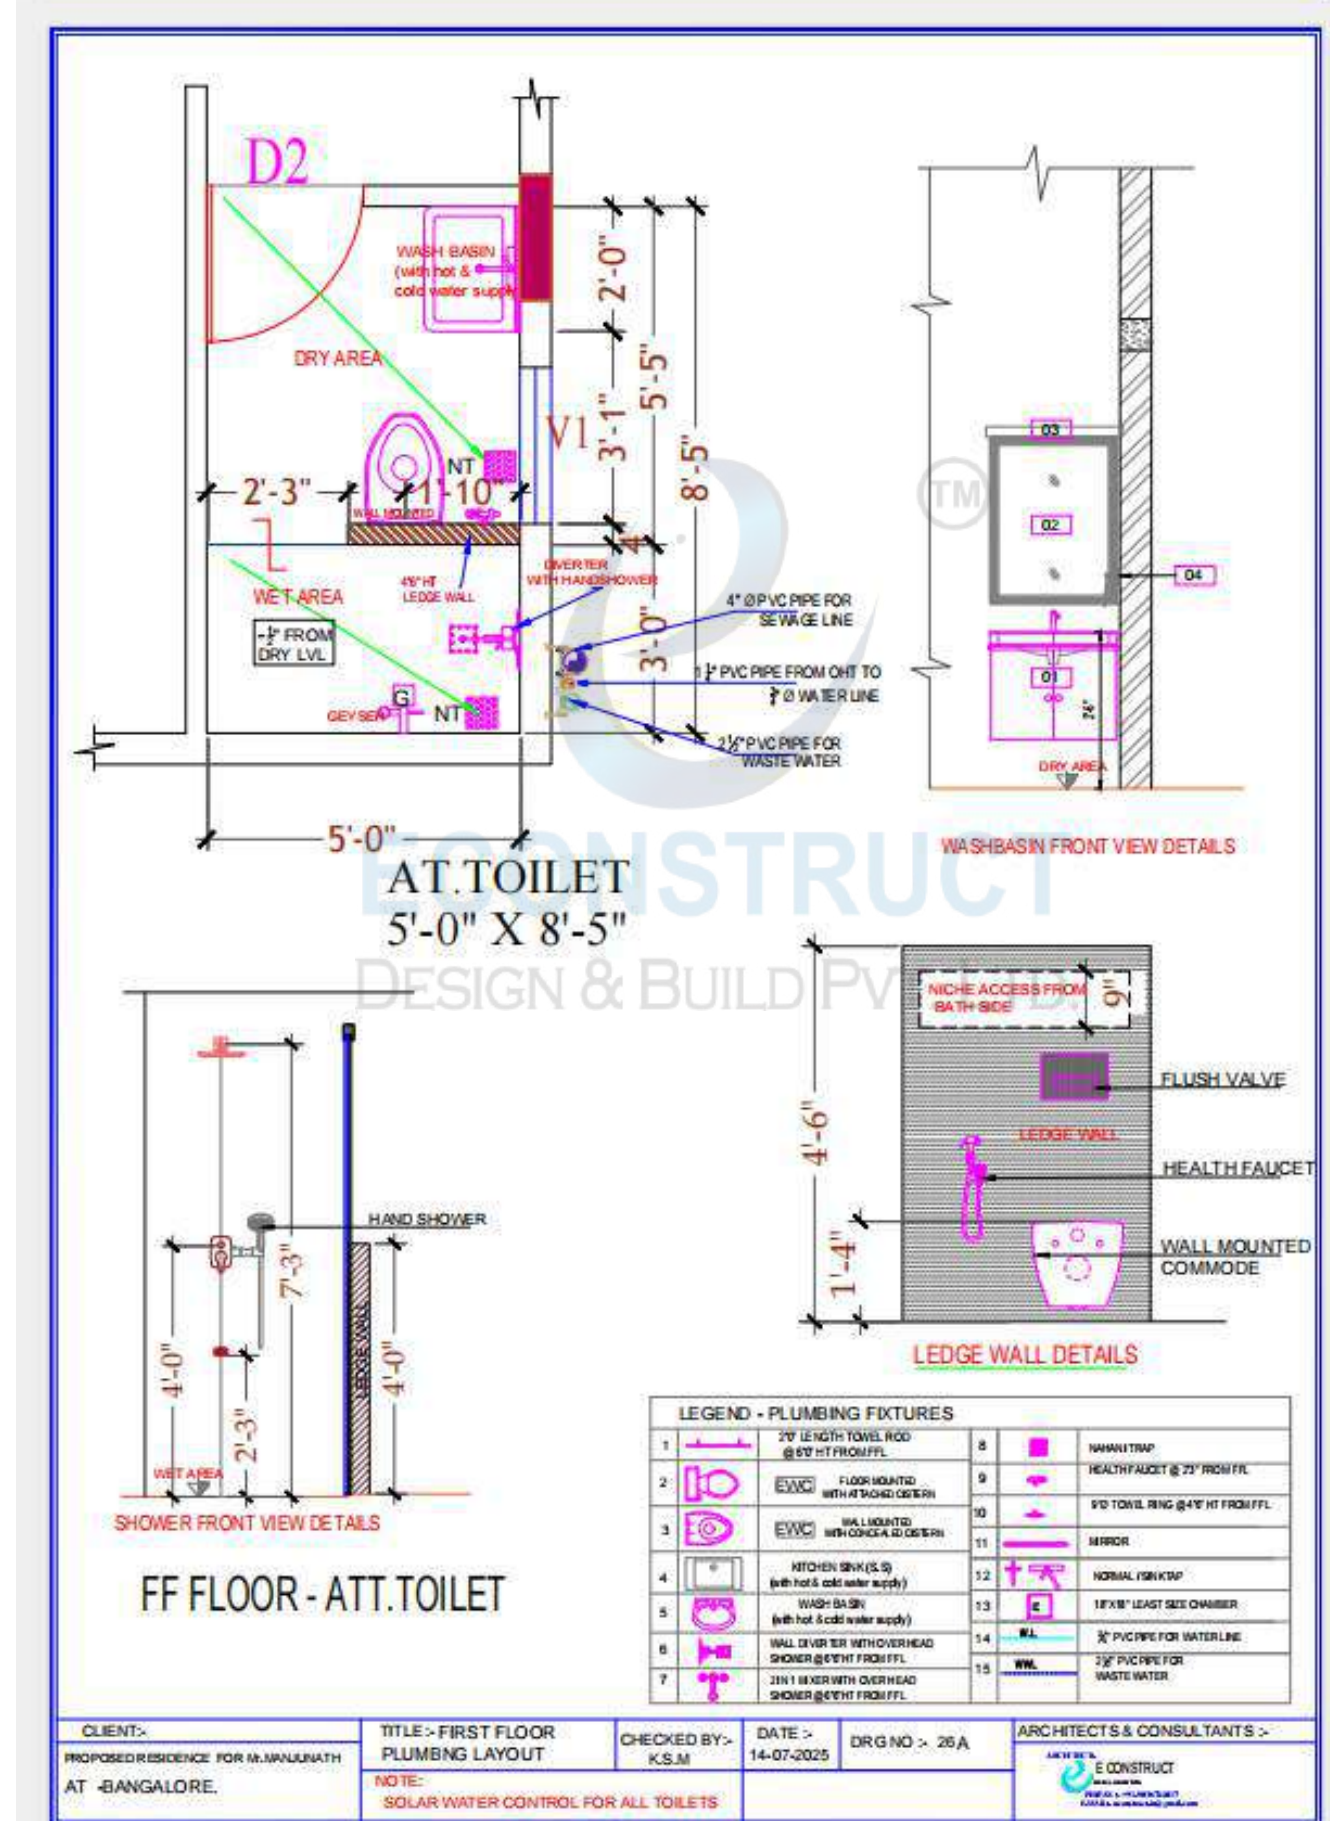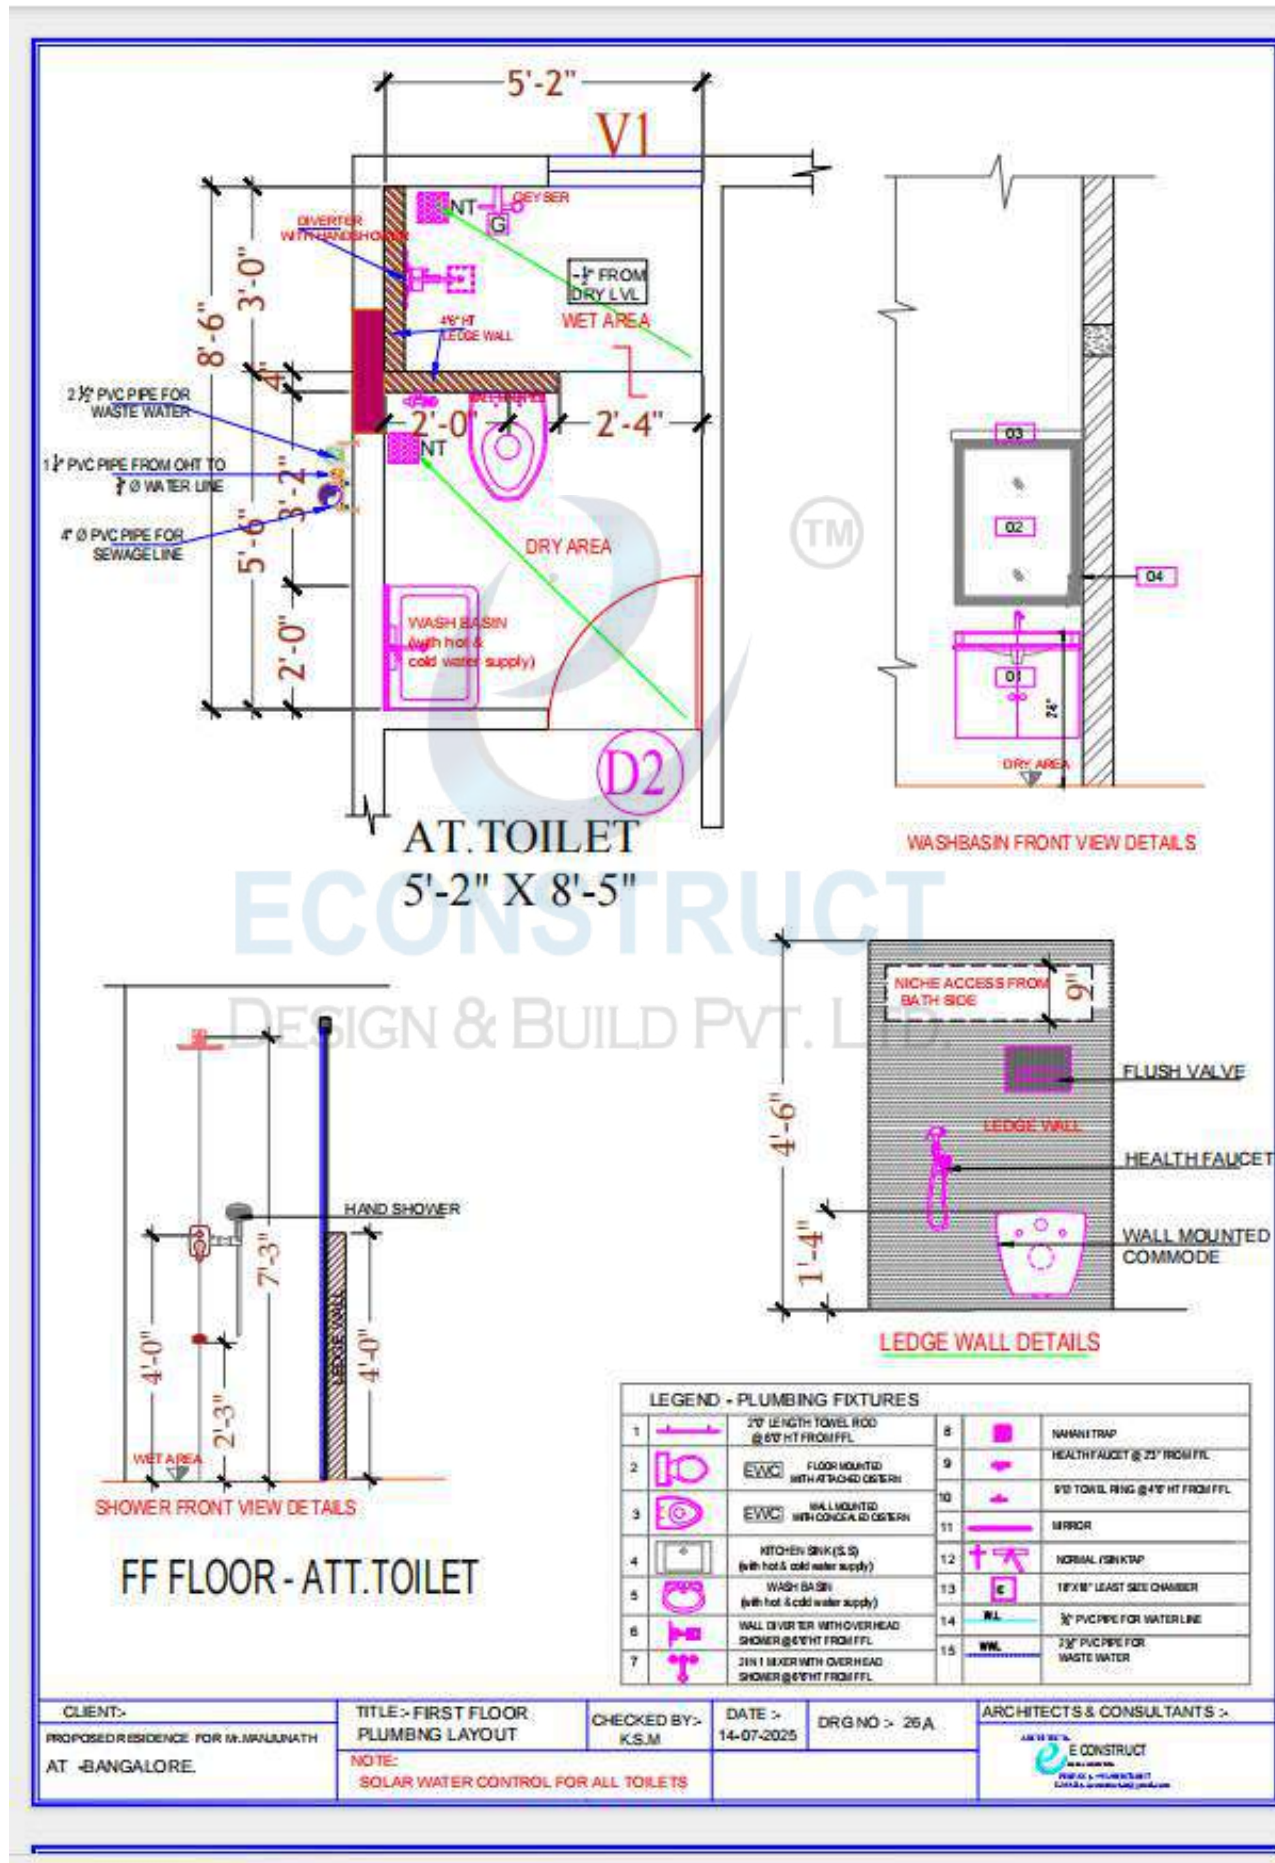


21


FF - KITCHEN / UTILITY

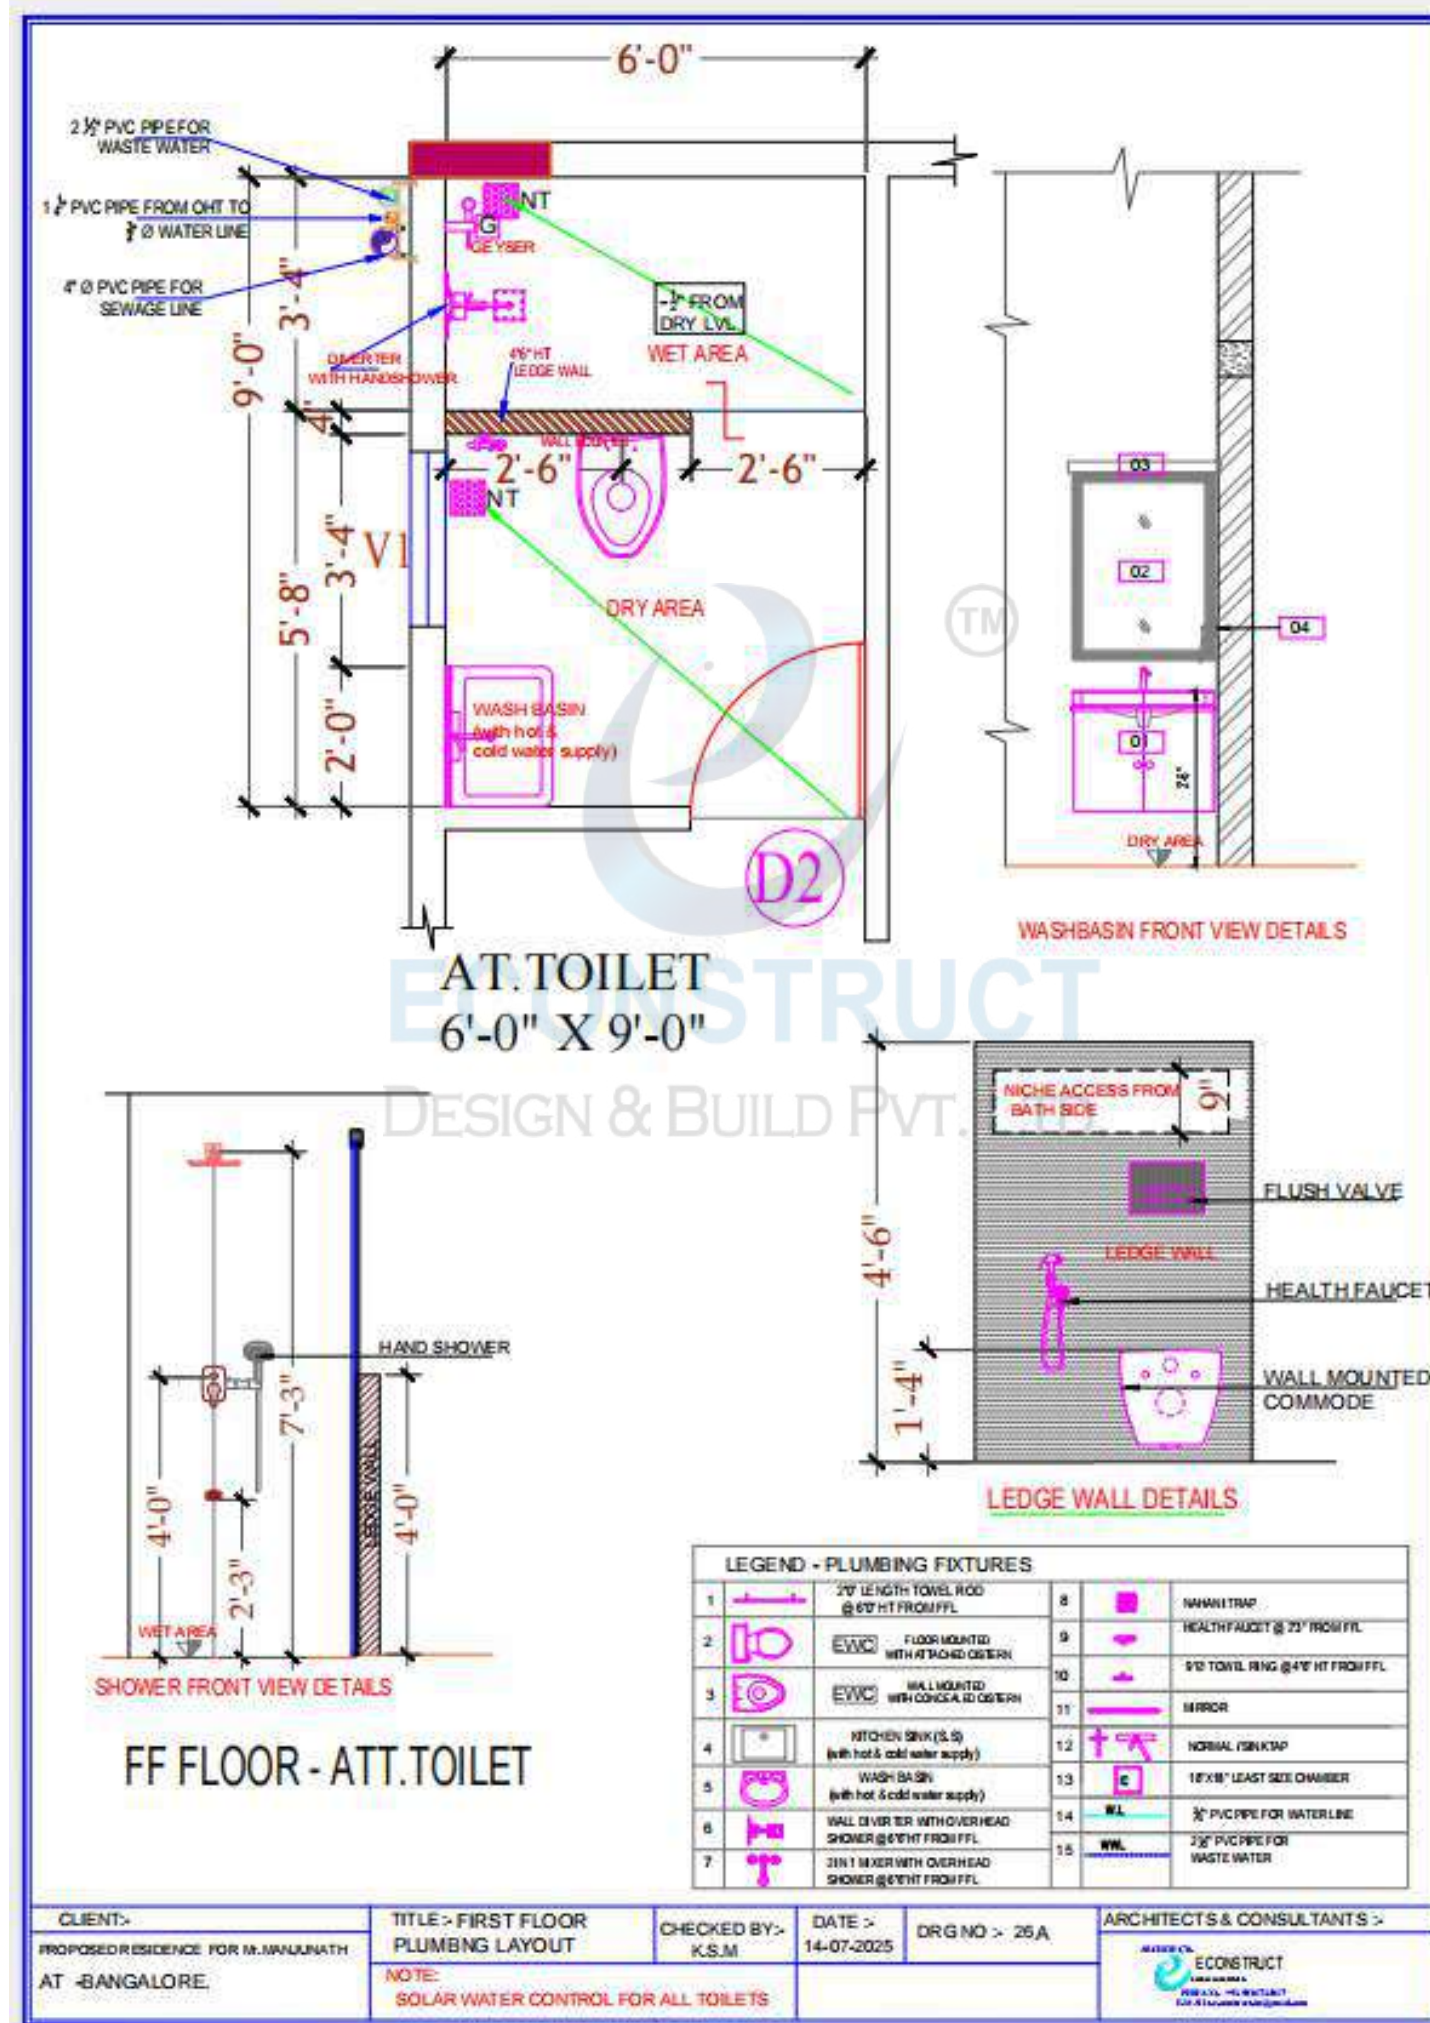


22

COMPOUND DETAILS

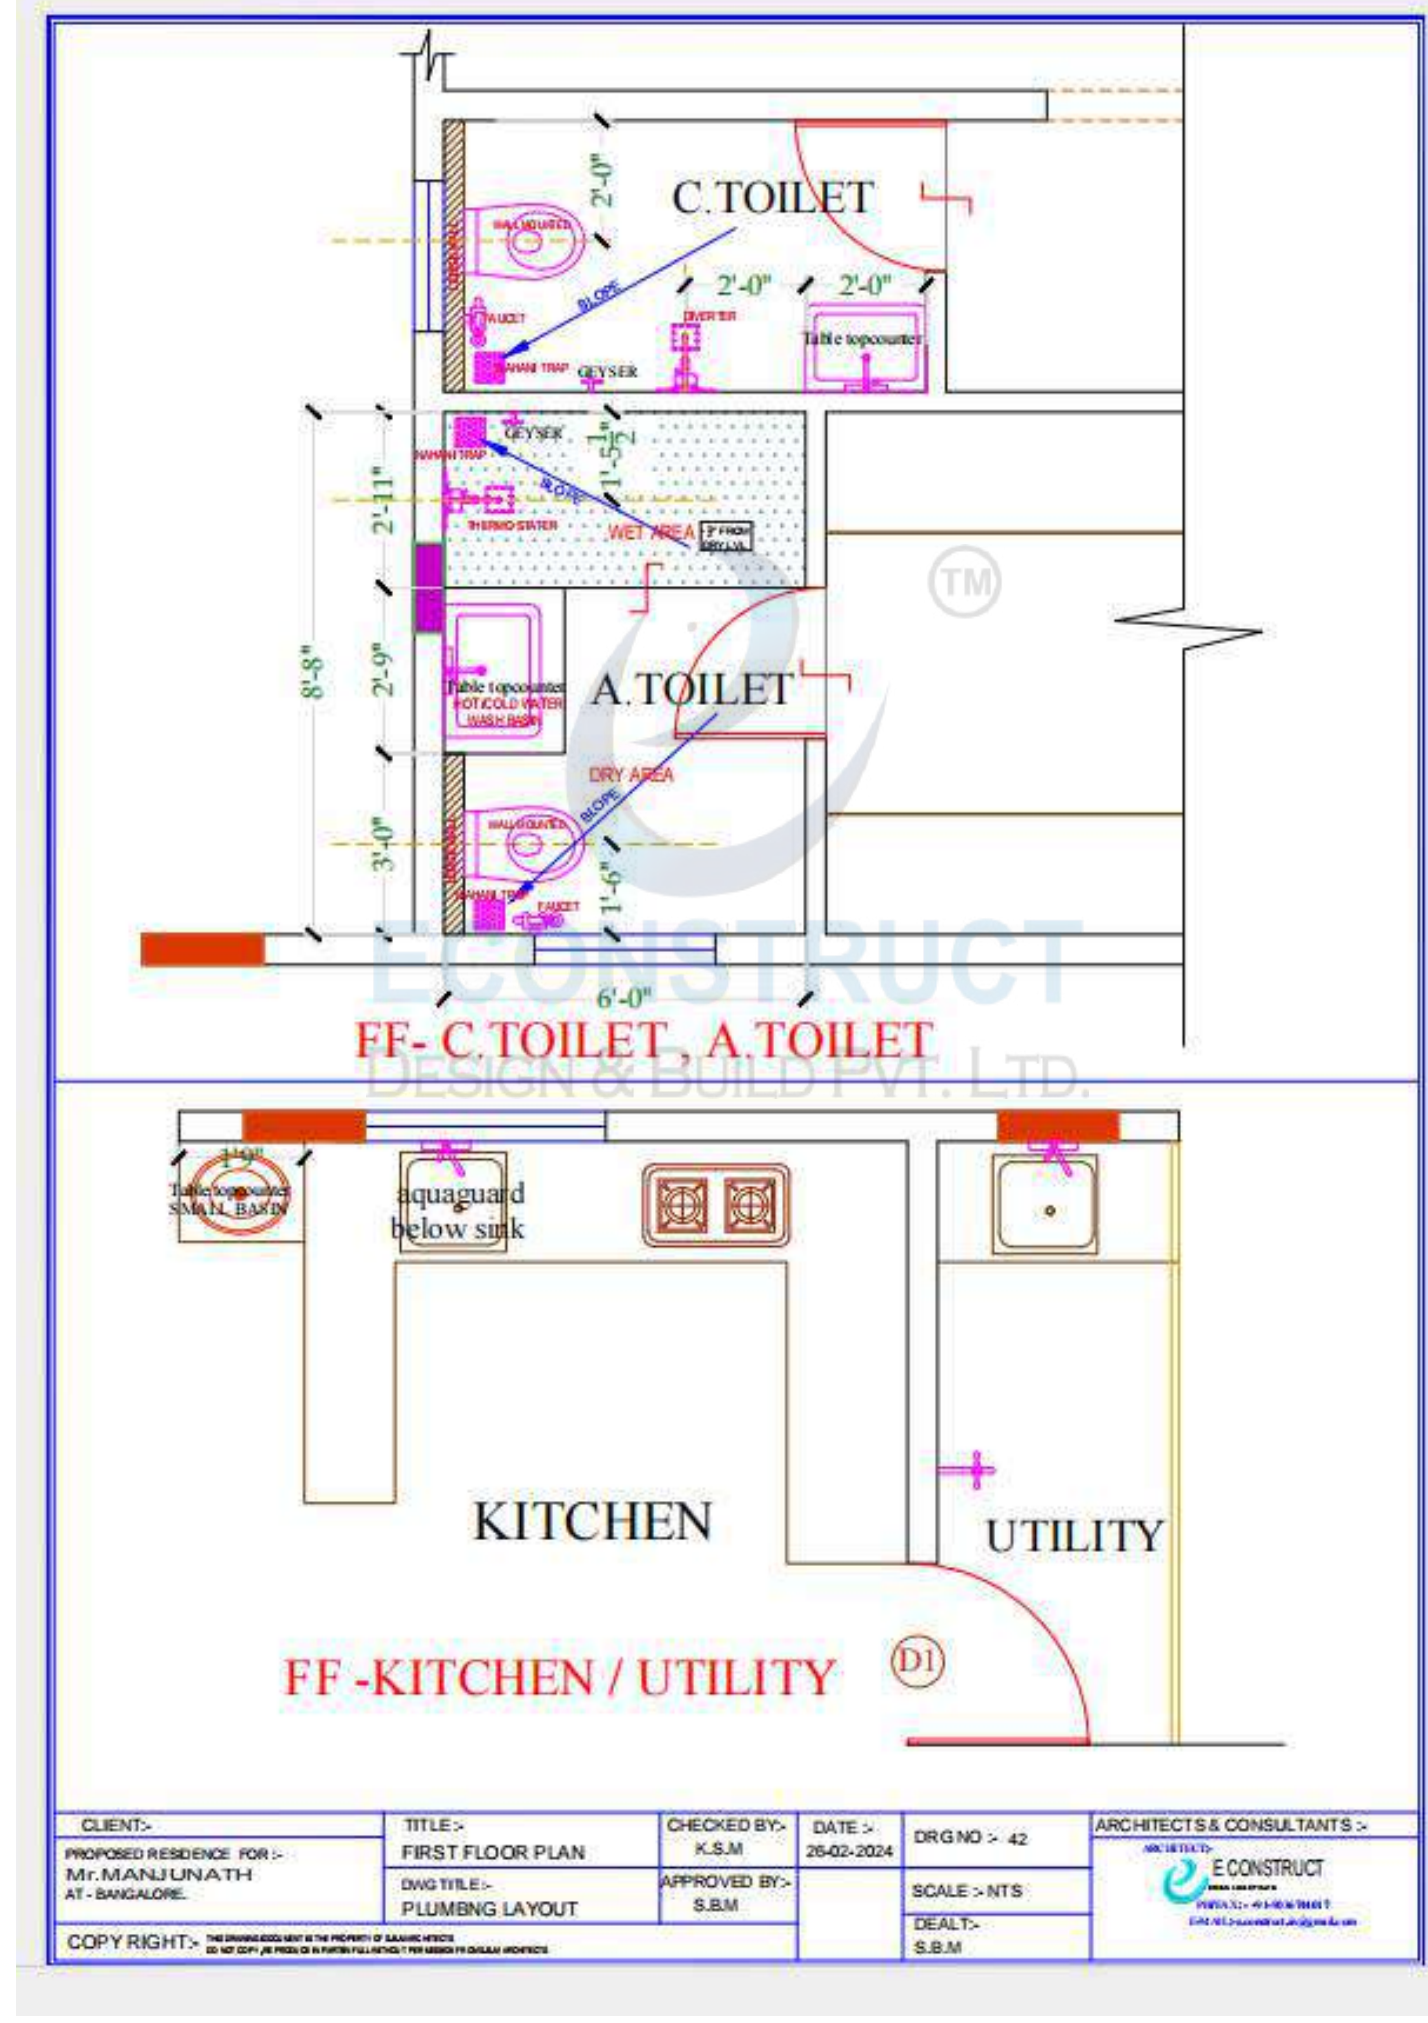


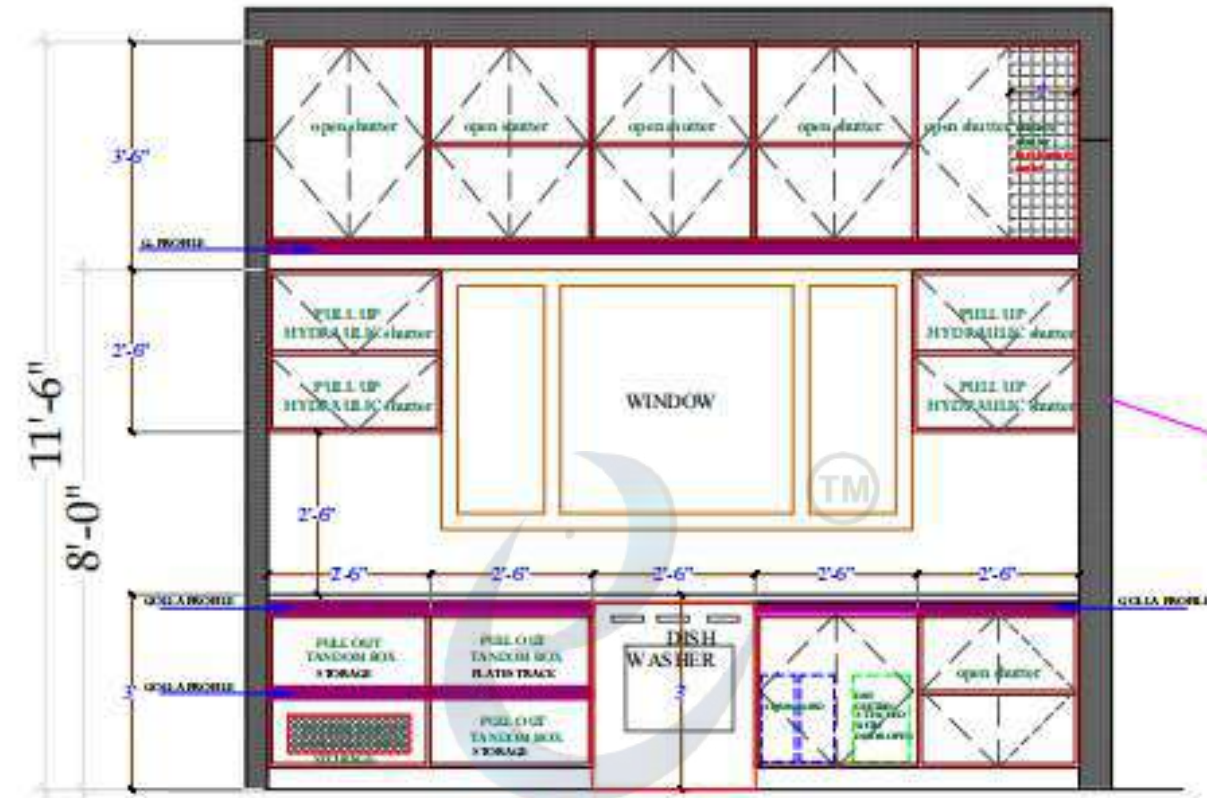

NORTH WALL

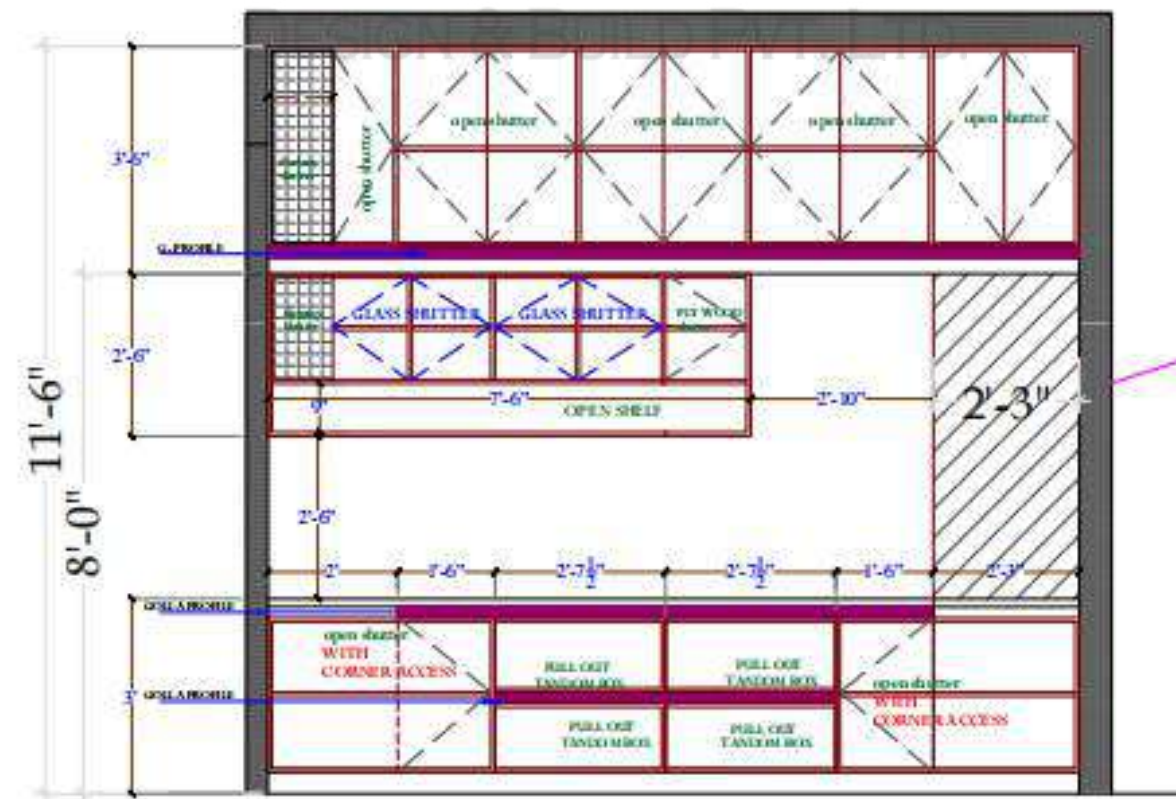




SOUTH WALL

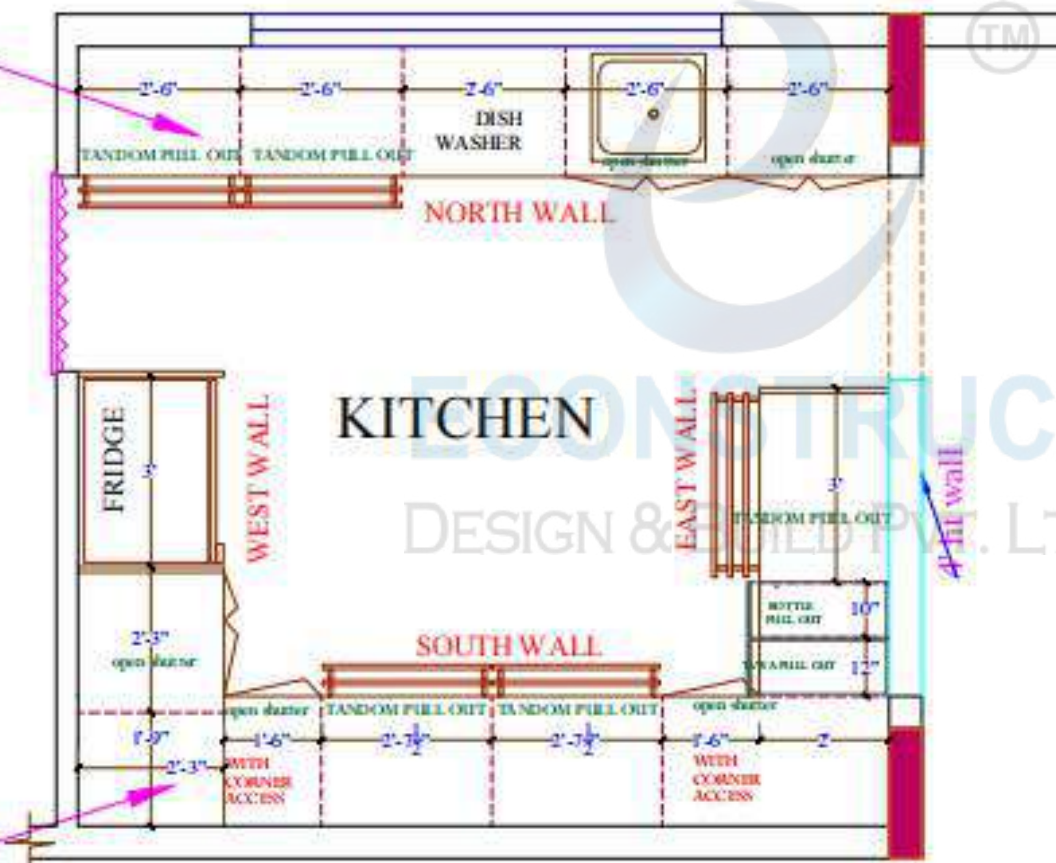

KITCHEN PLAN

REVISION -1

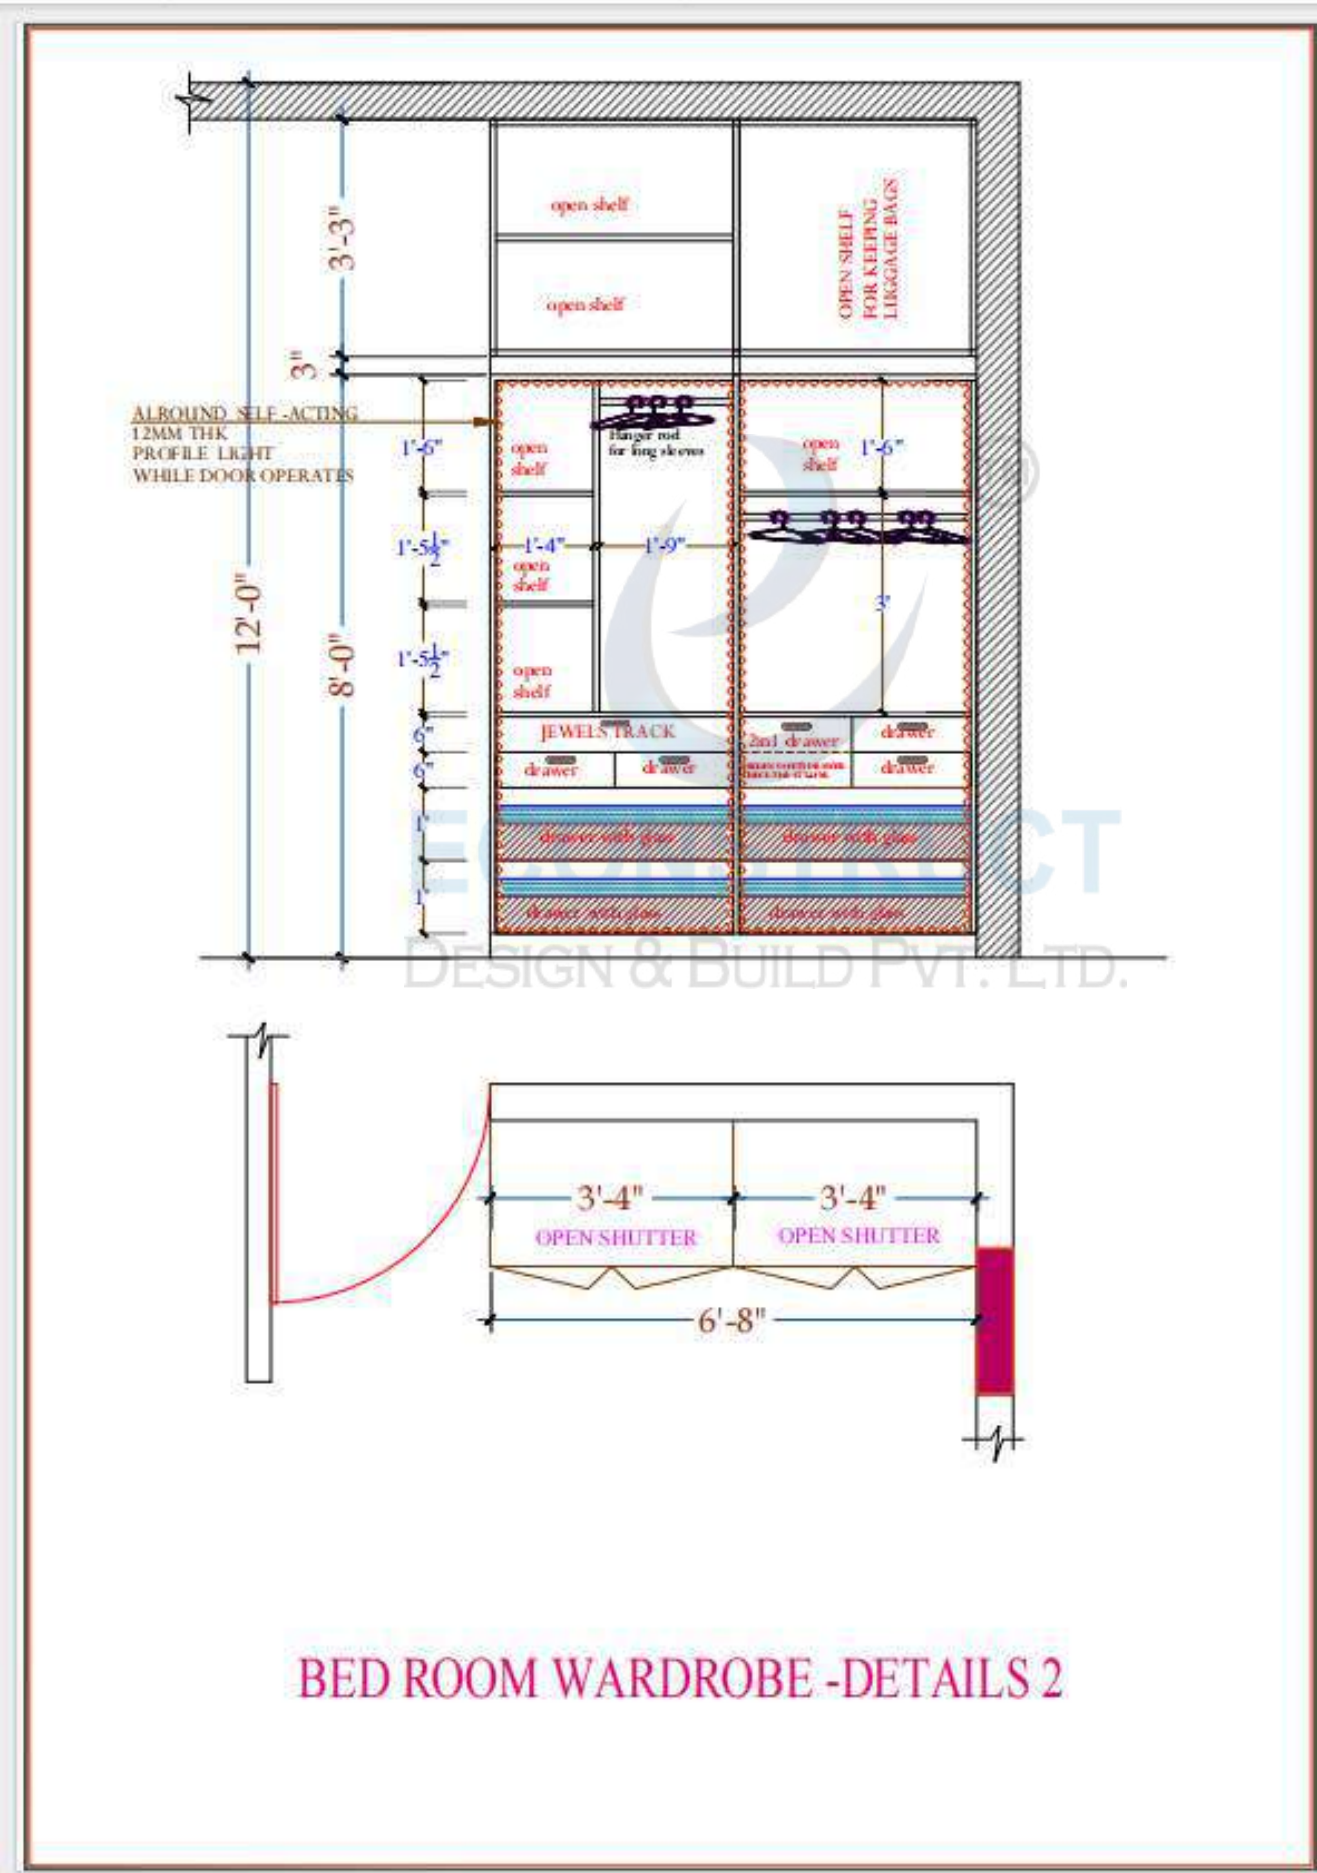

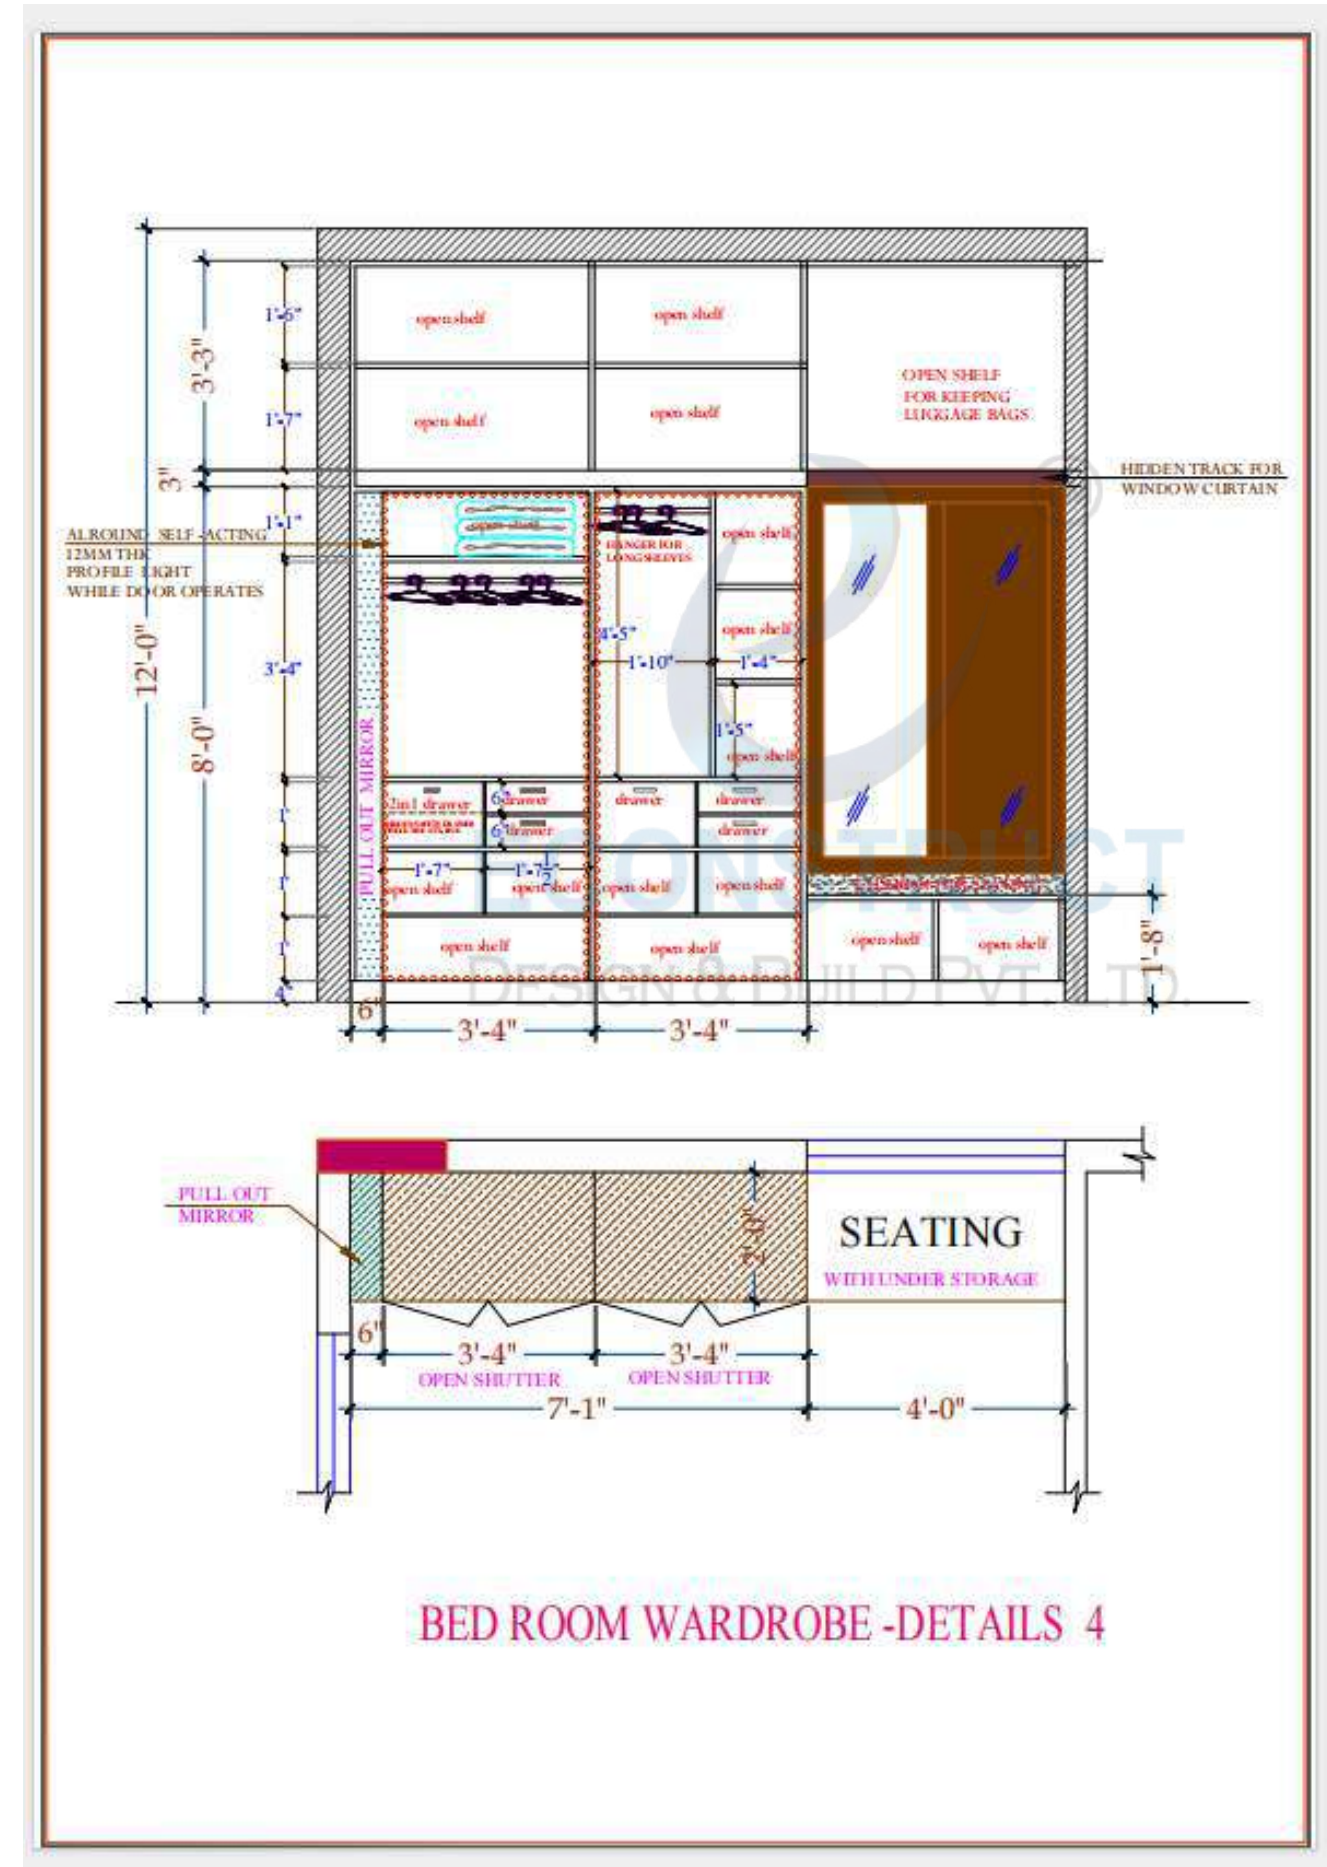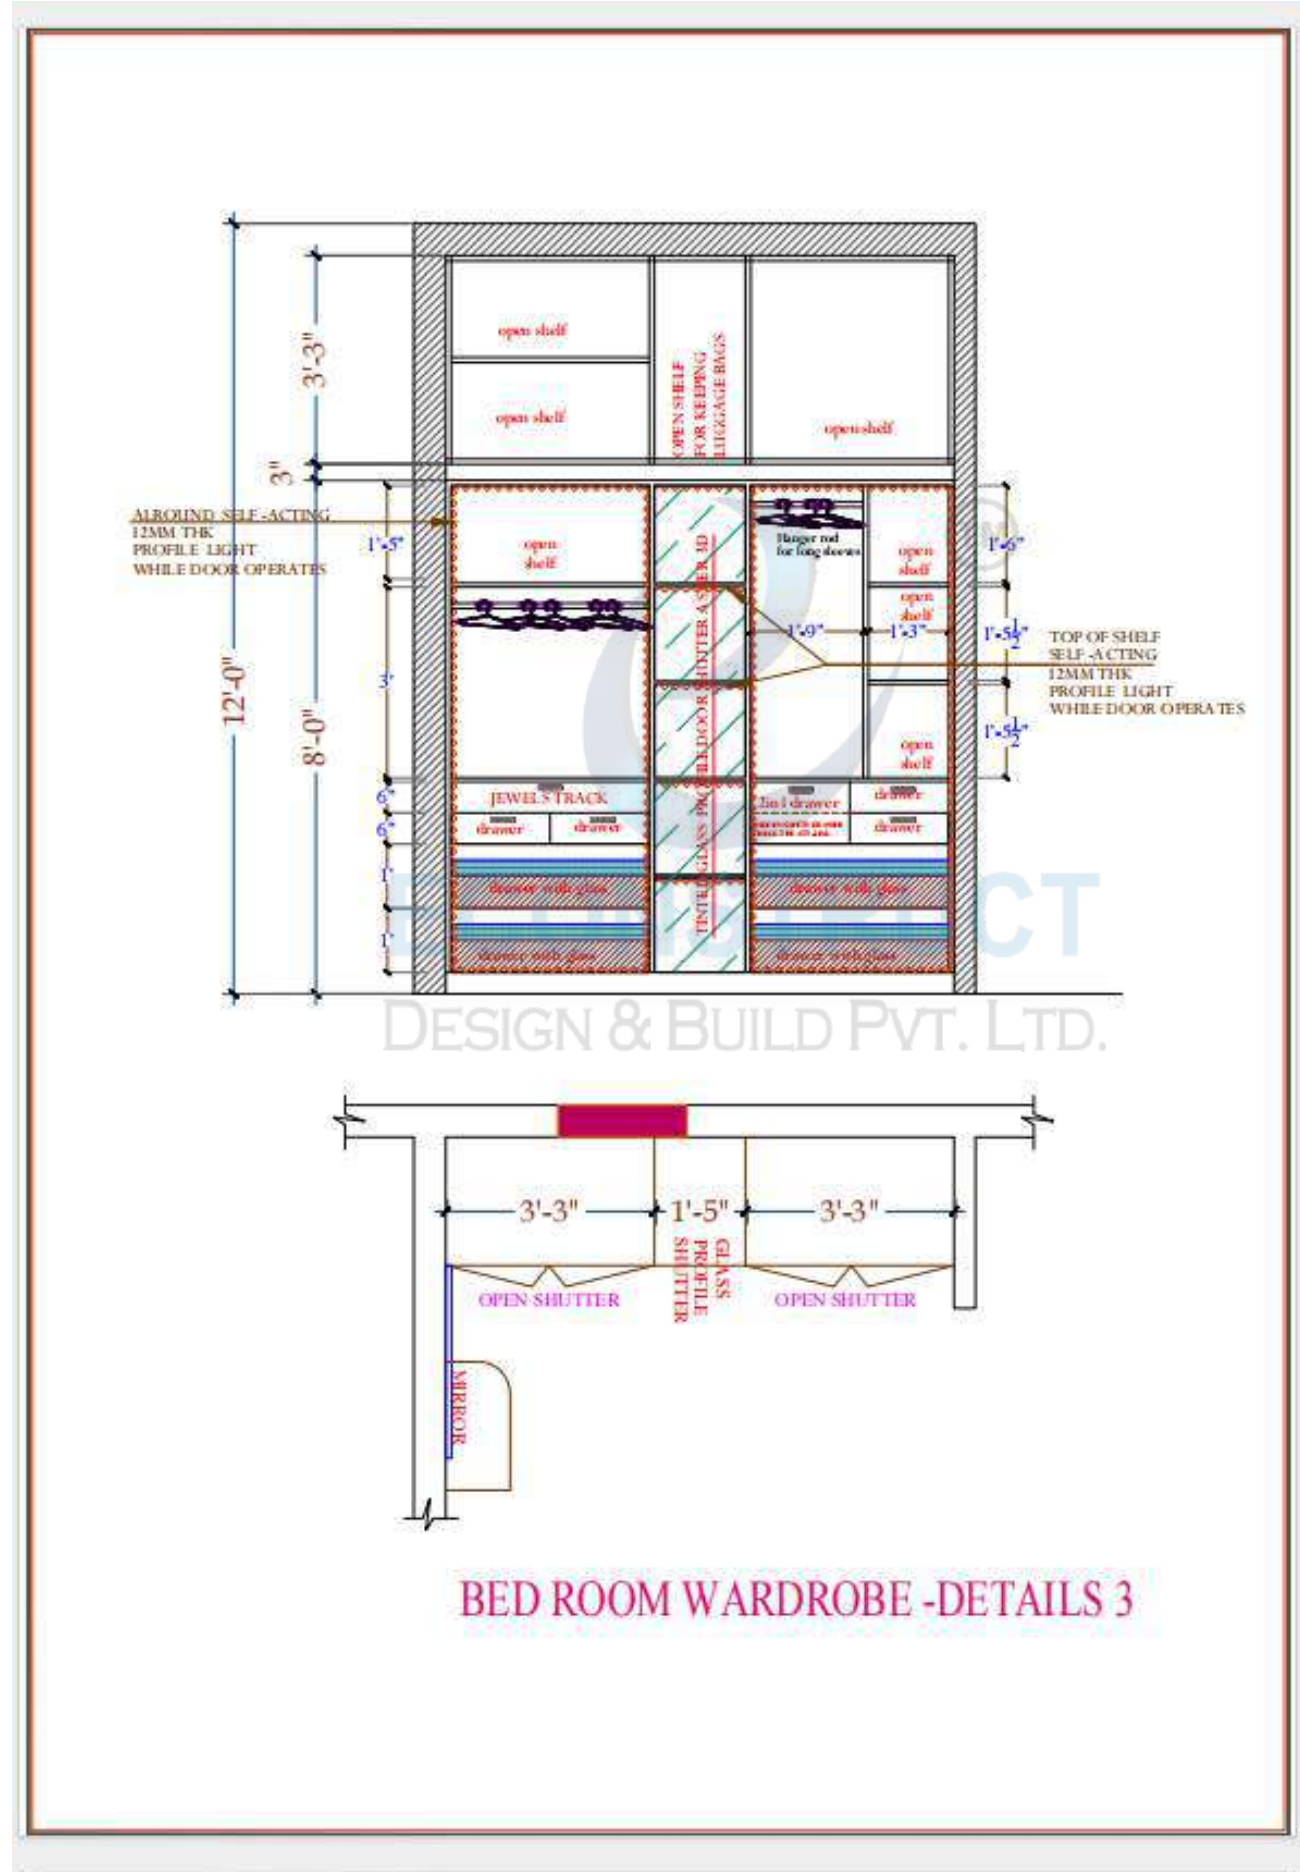



WEST SIDE COMPOUND DETAILS


- **3D
Elevation**



- **Home Interior Entrance**



- Home Interior - Devghar

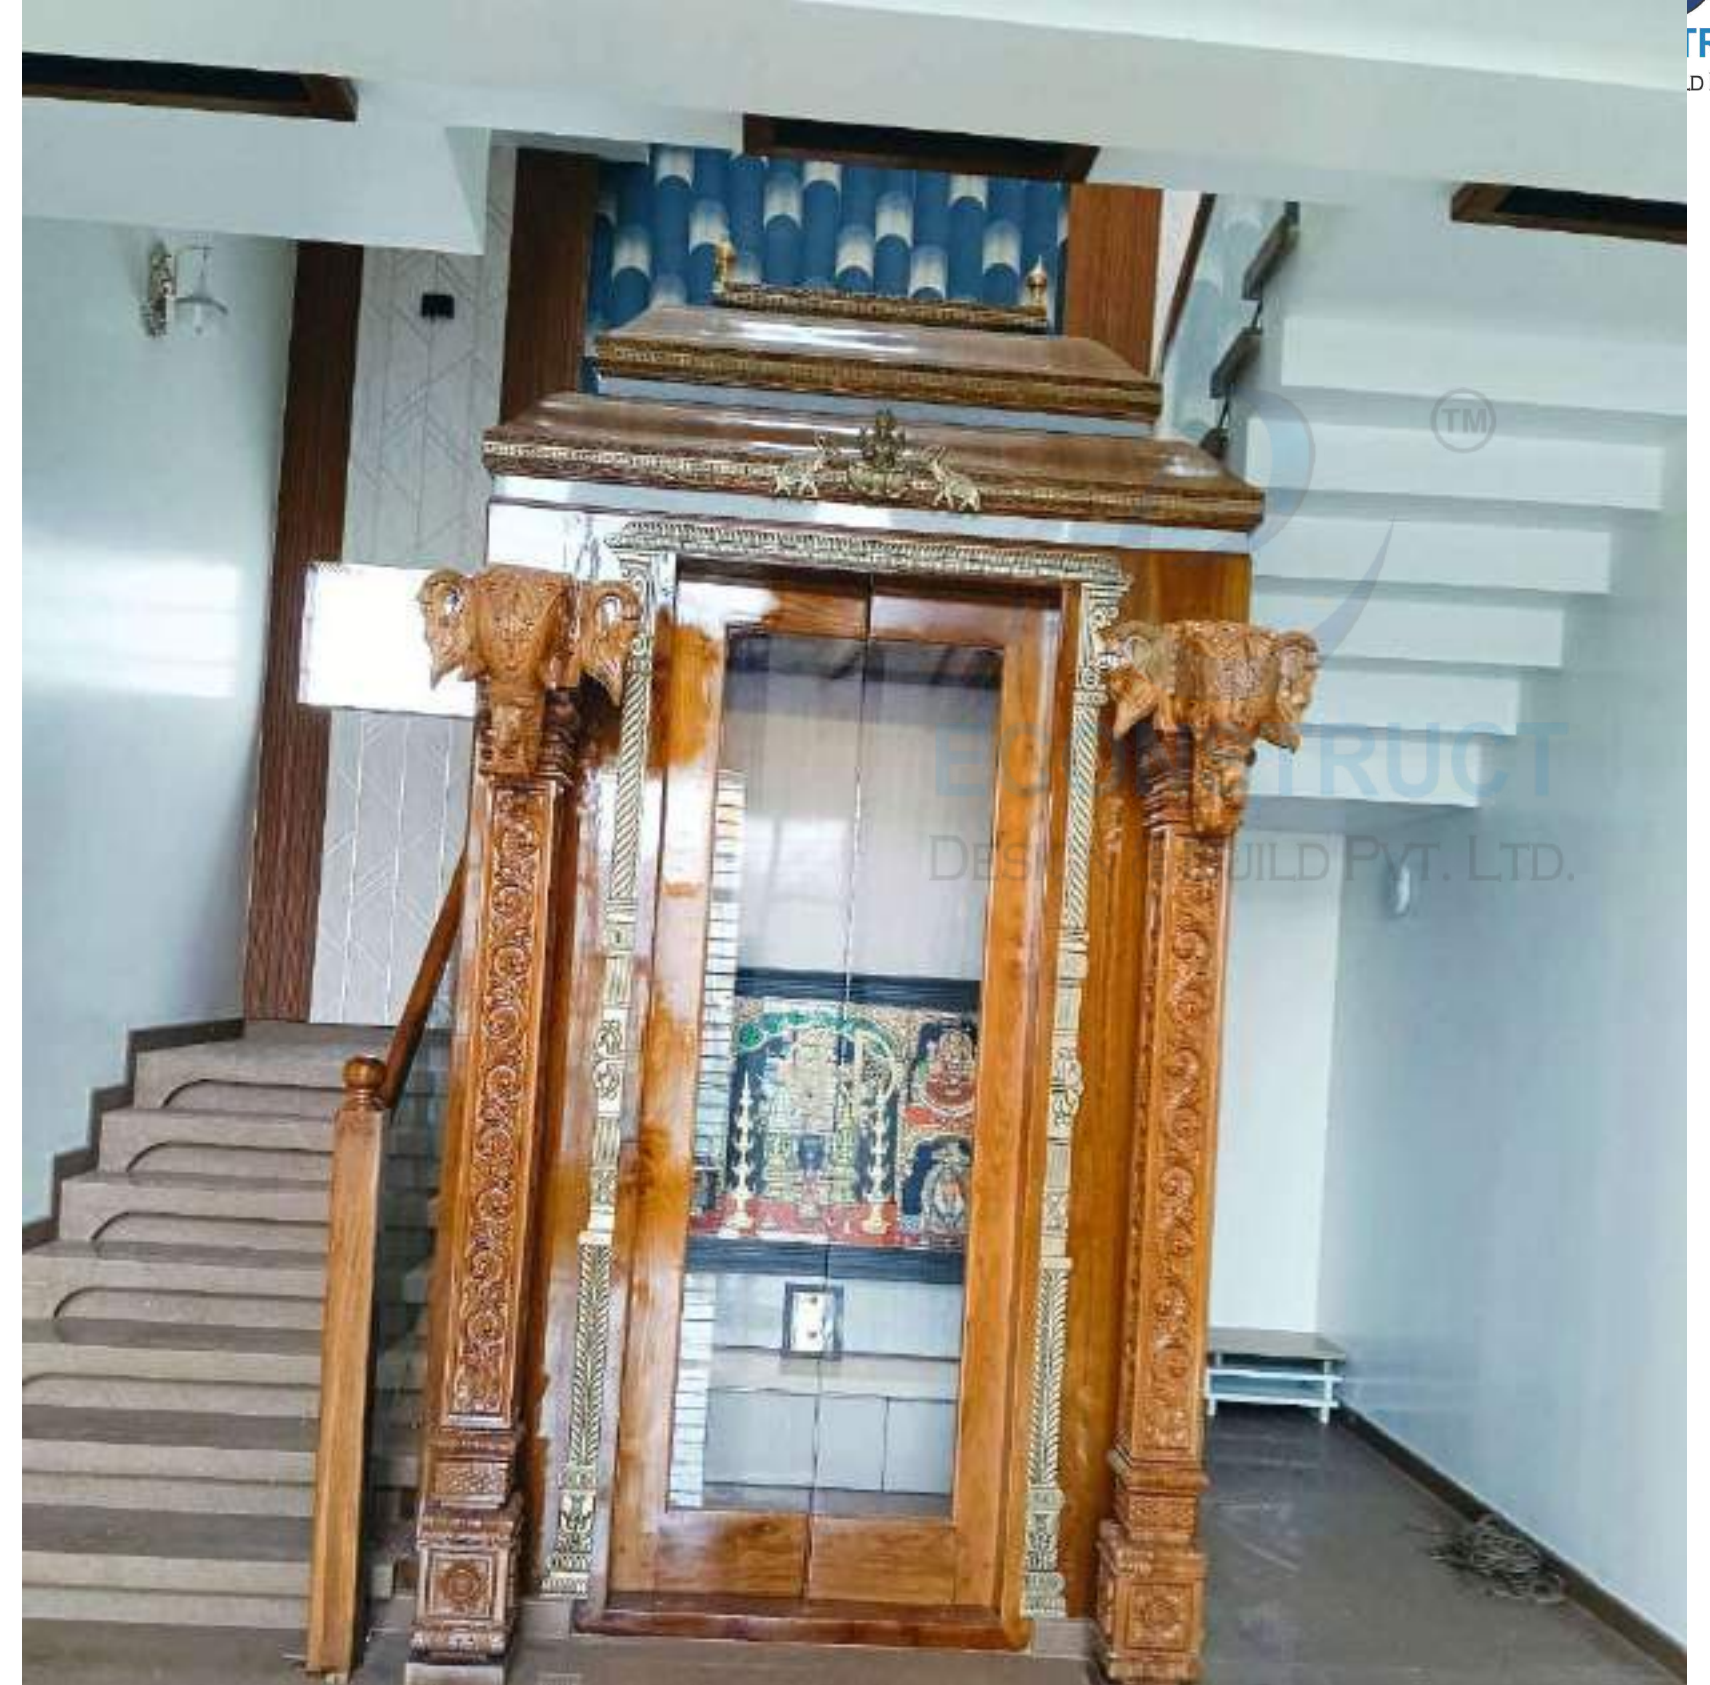

- Home Interior



- Home Interior



- Home Interior



• Turning Vision into Reality



Some images of our projects.



Some images of our projects.



www.e-construct.in

THANK YOU



Build Smart. Build Strong. Build with E-Construct
Don't just build a house — build a home that lasts for generations.

Contact Us: +91 9036744017 / +91 7259921111 / +91 7259222888