

www.e-construct.in

Construct Your Dream Home with **E-CONSTRUCT**

 +91 9036744017


ECONSTRUCT
DESIGN & BUILD PVT. LTD.





ECONSTRUCT Design & Build Pvt Ltd is a leading consultancy and contracting company in India that has executed construction work for some of the most significant projects in the country. We continue to alter the structural landscape through several other prestigious projects in the residential, commercial, and Institutional space.

We believe in exceeding clients' expectations by operating at par with global benchmarks for transparency, reliability and integrity. A commitment to sustainable development, safety and environment protection forms the genesis of our culture. Our clients value our allegiance to quality, timely deliveries, superior customer service and the experience of engaging in business with a highly qualified and experienced management. After creating our mark on the Mumbai landscape, we expanded to Bangalore, Tumkur, Mysore.

ECONSTRUCT is committed to maintaining the highest standards of business conduct and corporate governance. We believe this is essential for operating a successful business, serving our shareholders and maintaining our integrity in the marketplace. We look at each project as a mission our team has to achieve, for the sake of the client's dreams, pride of our shareholders and ultimately, self-satisfaction.

www.e-construct.in



FOUNDER'S INTRODUCTION

Sandeep Pingale Founder & MD

He has over 20+ years of experience in Civil & Structural engineering. International experience in structural analysis, Design, Execution and Management of up to G+81 story structure in Dubai.

He has worked with a various Multidisciplinary organization that has given him "State of Art" in providing the services with International quality standards.

He has worked by considering various International codes like ACI, CEBFIP, BS codes, IS codes that gave him the excellent exposure and immense knowledge about the civil engineering area.



FOUNDER'S INTRODUCTION

Shraddha Pingale Jt. Managing Director

M.Tech Graduate from a recognized university who co-founded ECONSTRUCT Design & Build Pvt Ltd. Well-known for her innovative techniques in Business Development, Creative Strategies, Brand Building, Corporate Trainings for Entrepreneurship. She is young, dynamic, self-motivated and she knows how to build the building blocks of the foundation of any company. She is the backbone of the company that stands straight in every challenging situation.



OUR HISTORY

2010

Establishment

ECONSTRUCT Design & Build Pvt. Ltd. was founded with a vision to deliver high-quality engineering, construction, and consultancy services, setting strong foundations in the residential, commercial, and institutional sectors.

2015

Growth & Expansion

After establishing a strong presence in Mumbai, the company expanded operations to Bangalore, Tumkur, and Mysore, executing multiple prestigious projects and strengthening its reputation for quality, transparency, and timely delivery.

2019

Leadership & Excellence

Emerged as a trusted industry leader, operating at global standards with a focus on sustainability, safety, corporate governance, and client satisfaction, while delivering complex, high-value projects across India and Abroad.





**we ensure every detail is handled with perfection,
so you can enjoy a stress-free construction journey.**

From planning to execution,





WHAT WE PROVIDE

- **Architectural Planning**
(Smart & Space-Optimized Designs)
- **Complete Structural Drawings**
(Safe & Strong Design)
- **3D Elevation**
(Visualize Before Construction)
- **Construction Services**
(Quality Execution)
- **Site Visit Support**
(Start to End Guidance)
- **Budget Planning**
(Cost-Controlled Solutions)

We provide 50+ detailed drawings for every project, including Architectural, Structural, and MEP designs.

Why? Because we truly care about your safety, budget, and long-term satisfaction.

With proper planning and complete drawings, you clearly understand every aspect of your home construction. This helps you make informed decisions and avoid costly mistakes.

Even if you want to make changes later, it won't lead to major expenses, because everything is already well-planned in advance.

We Provide 50+ Detailed Drawings for Every Project

Including Architectural, Structural & MEP Designs

Why?

Because we truly care about your
Safety, Budget, and Long-Term Satisfaction.



Safety



Budget





Satisfaction

See Our Completed Project – Understand Our Perfection

Go through our completed project drawings and plans to clearly understand what we deliver with accuracy and detailing.


Project Details

- **Client:** Manjunath
- **Location:** Battarahalli, KR Puram
- **Plot Size:** 60' x 40'
- **Status:** Completed & Client Staying
- **Ground Floor –** Parking + Servant Room
- **1st, 2nd & 3rd Floor –** Triplex House
- **Project Timeline:** 14 Months (Including Interior Work)

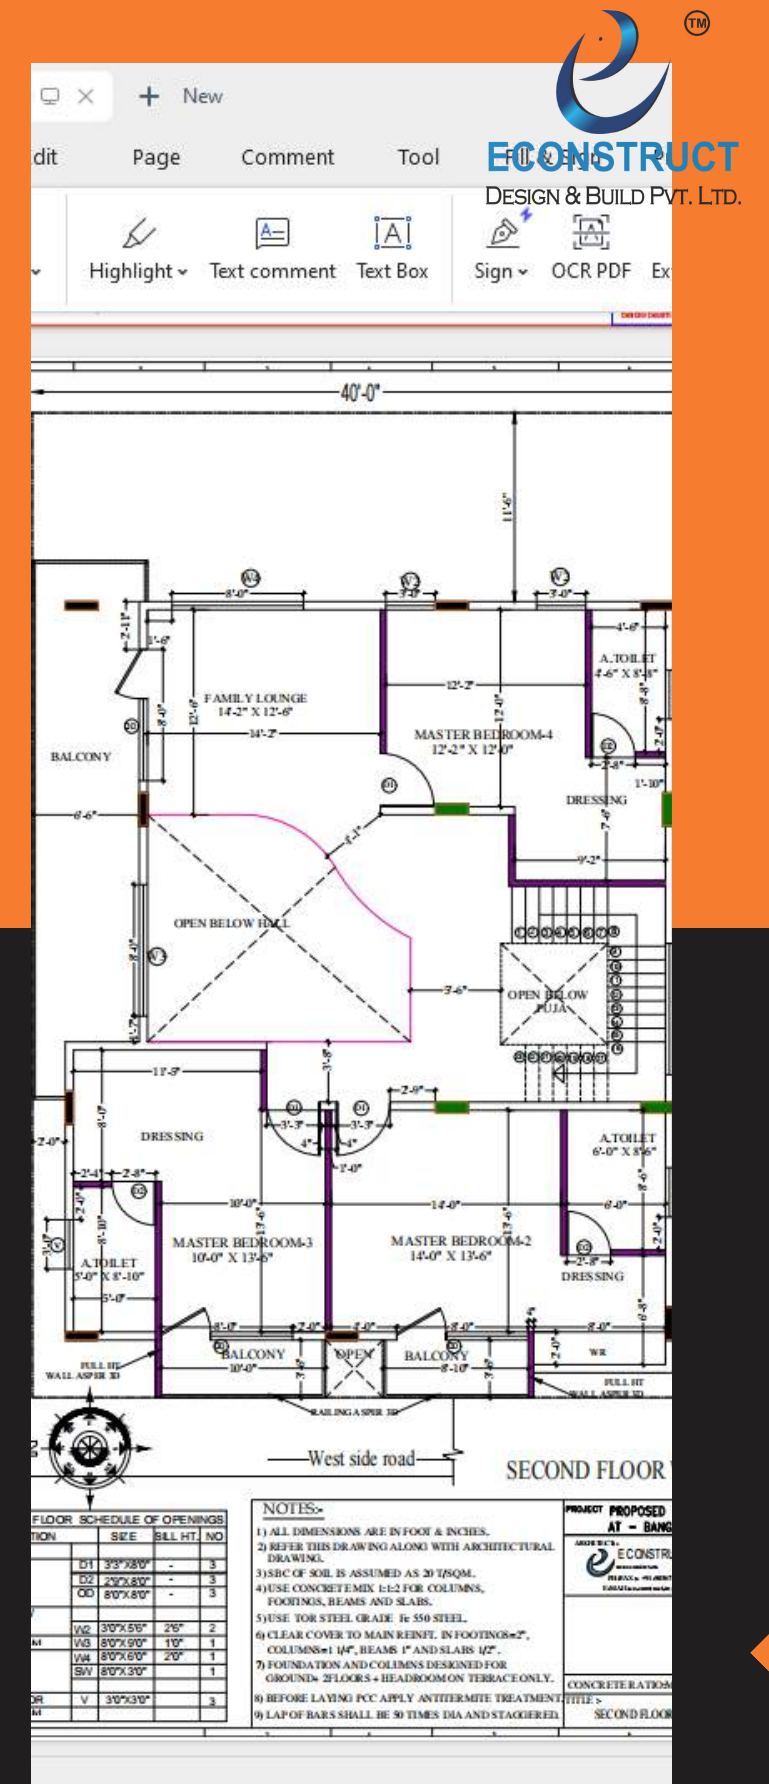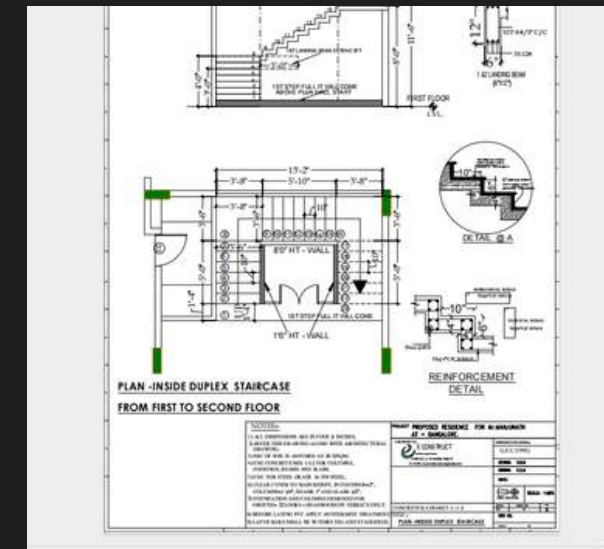


Structural Drawings Included

- Column Marking Layout
- Footing Marking Layout
- Column & Footing RC Details
- Pedestal Reinforcement
- Plinth Beam Layout & Reinforcement
- Ground Floor Beam & Slab Details
- First Floor Beam & Slab Details (Revised)
- Second Floor Beam & Slab Details
- Terrace Beam & Slab Details
- Beam Shuttering Layouts (All Floors)
- Complete Reinforcement Detailing

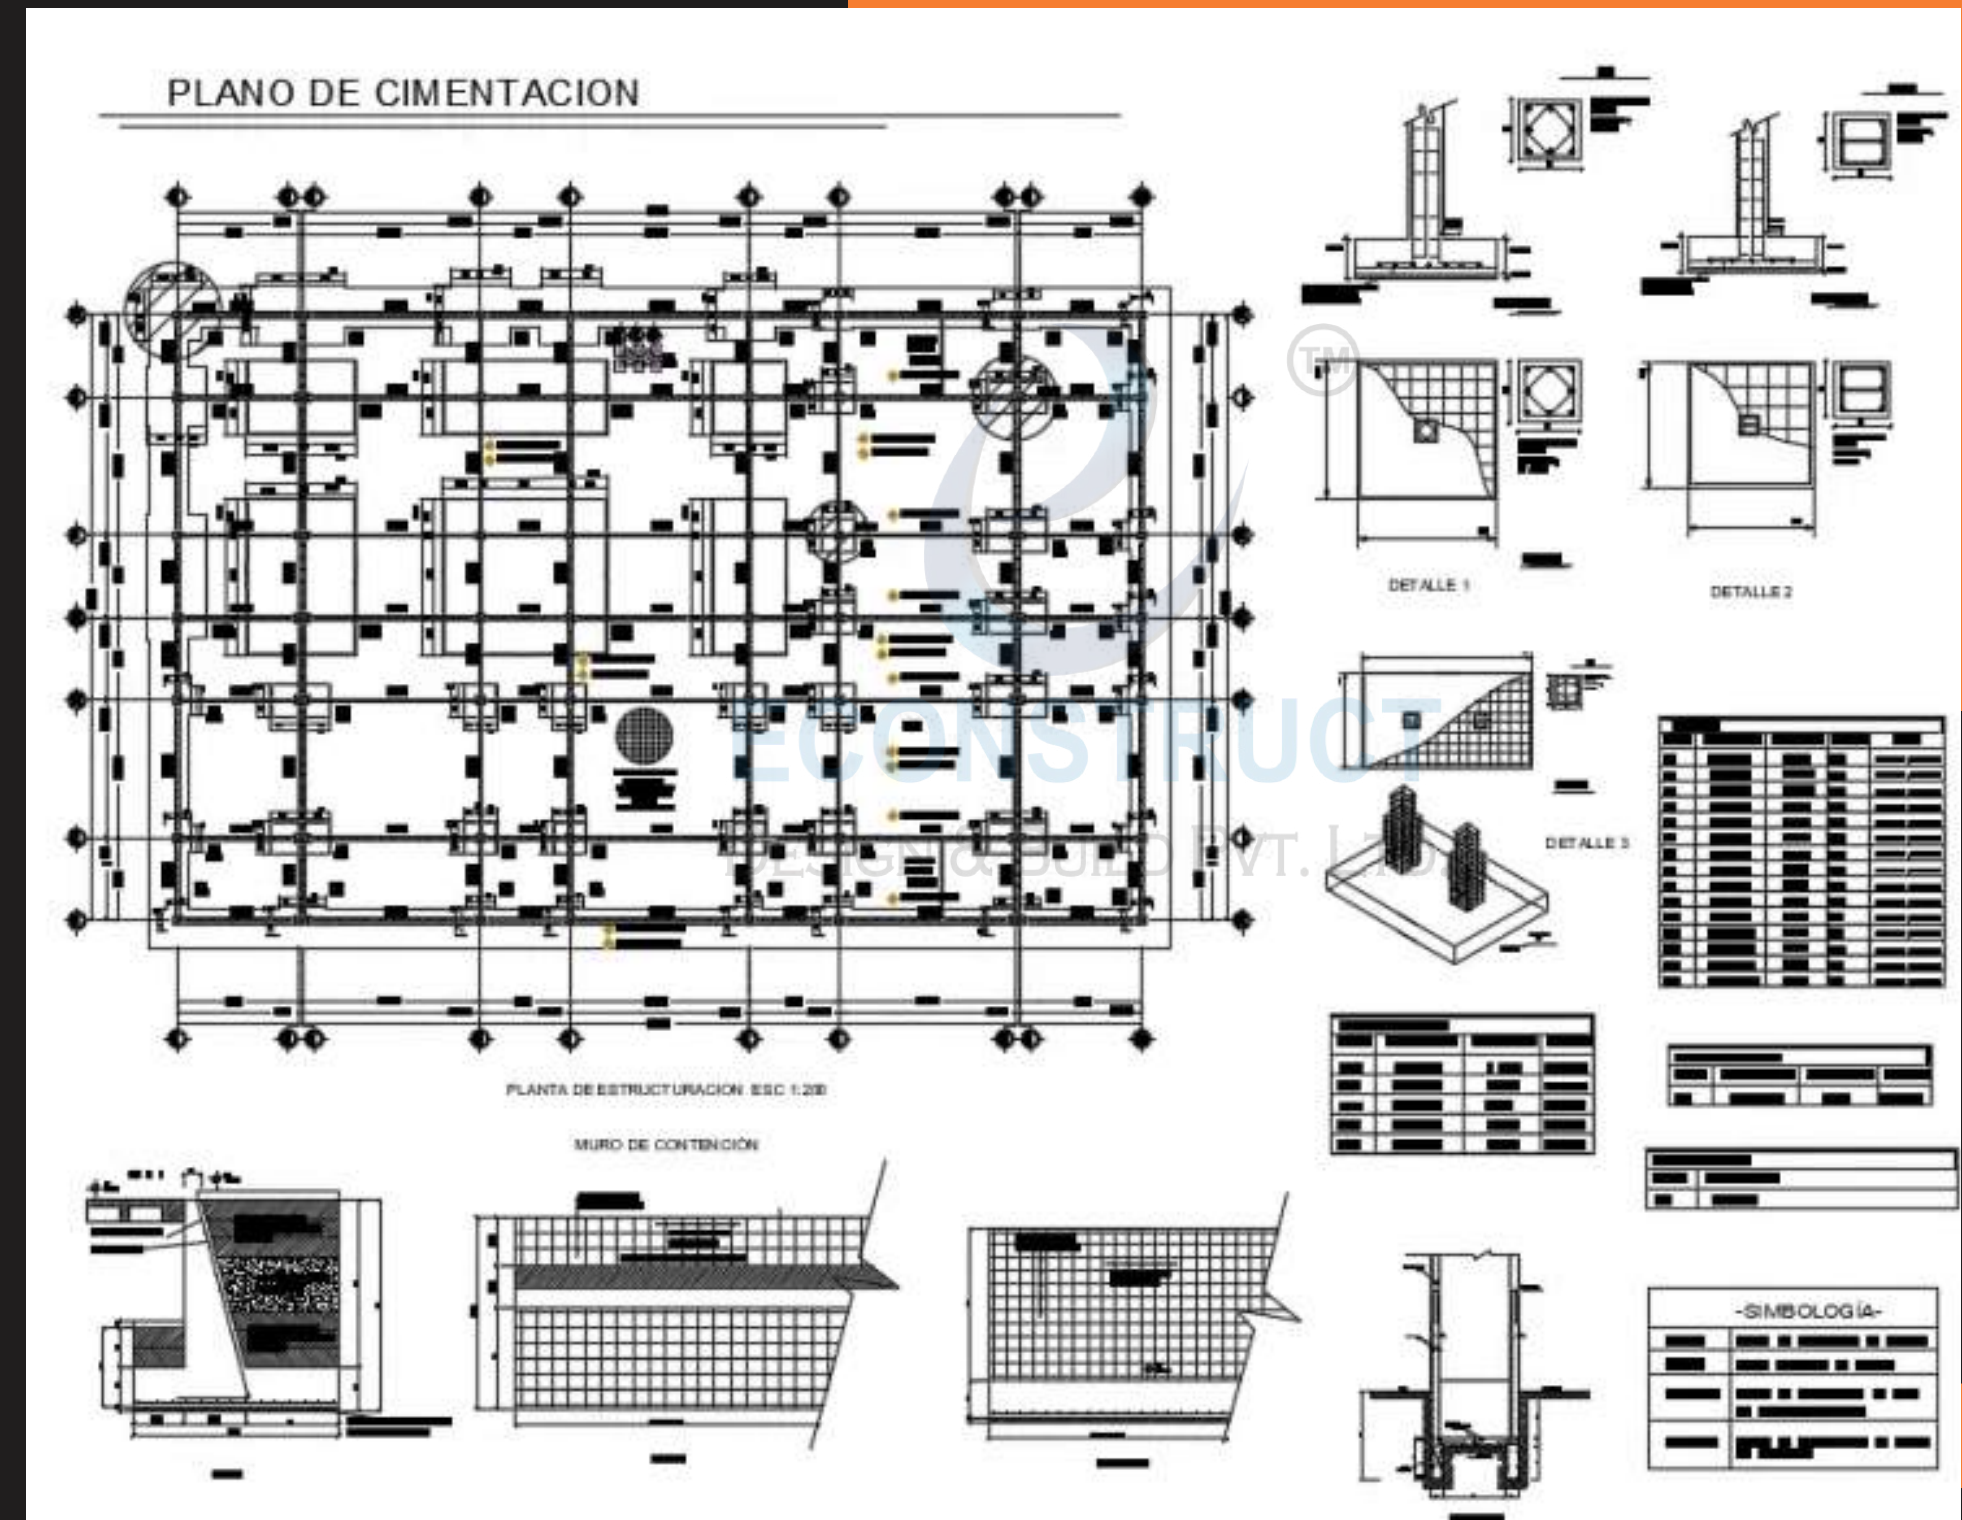


01

COLUMN MARKING LAYOUT

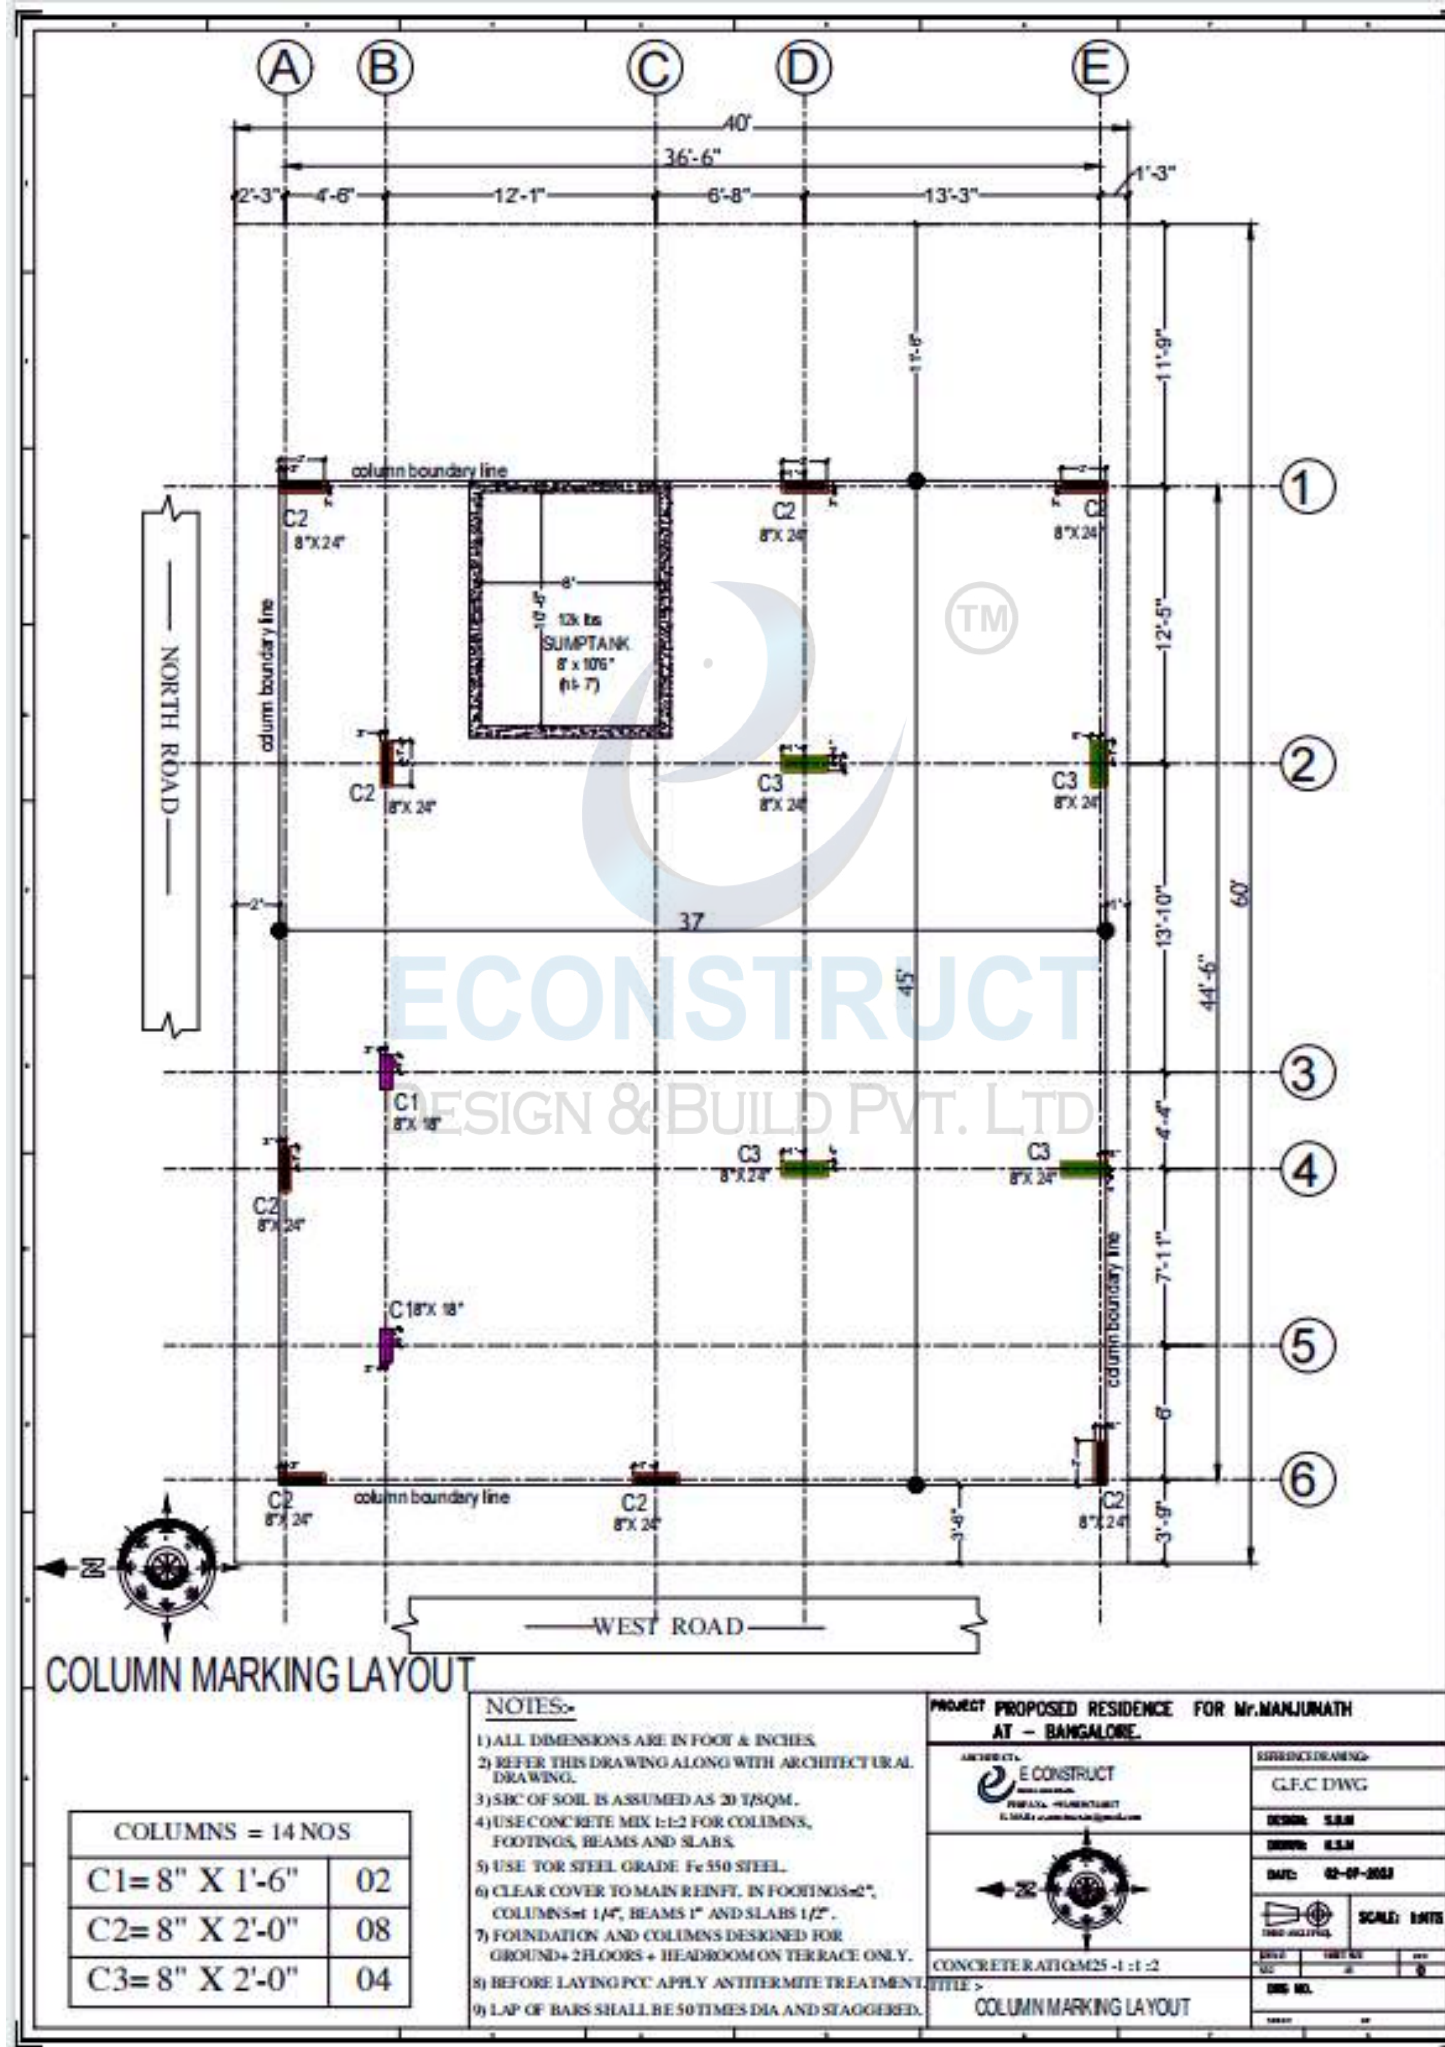


02

FOOTING MARKING LAYOUT

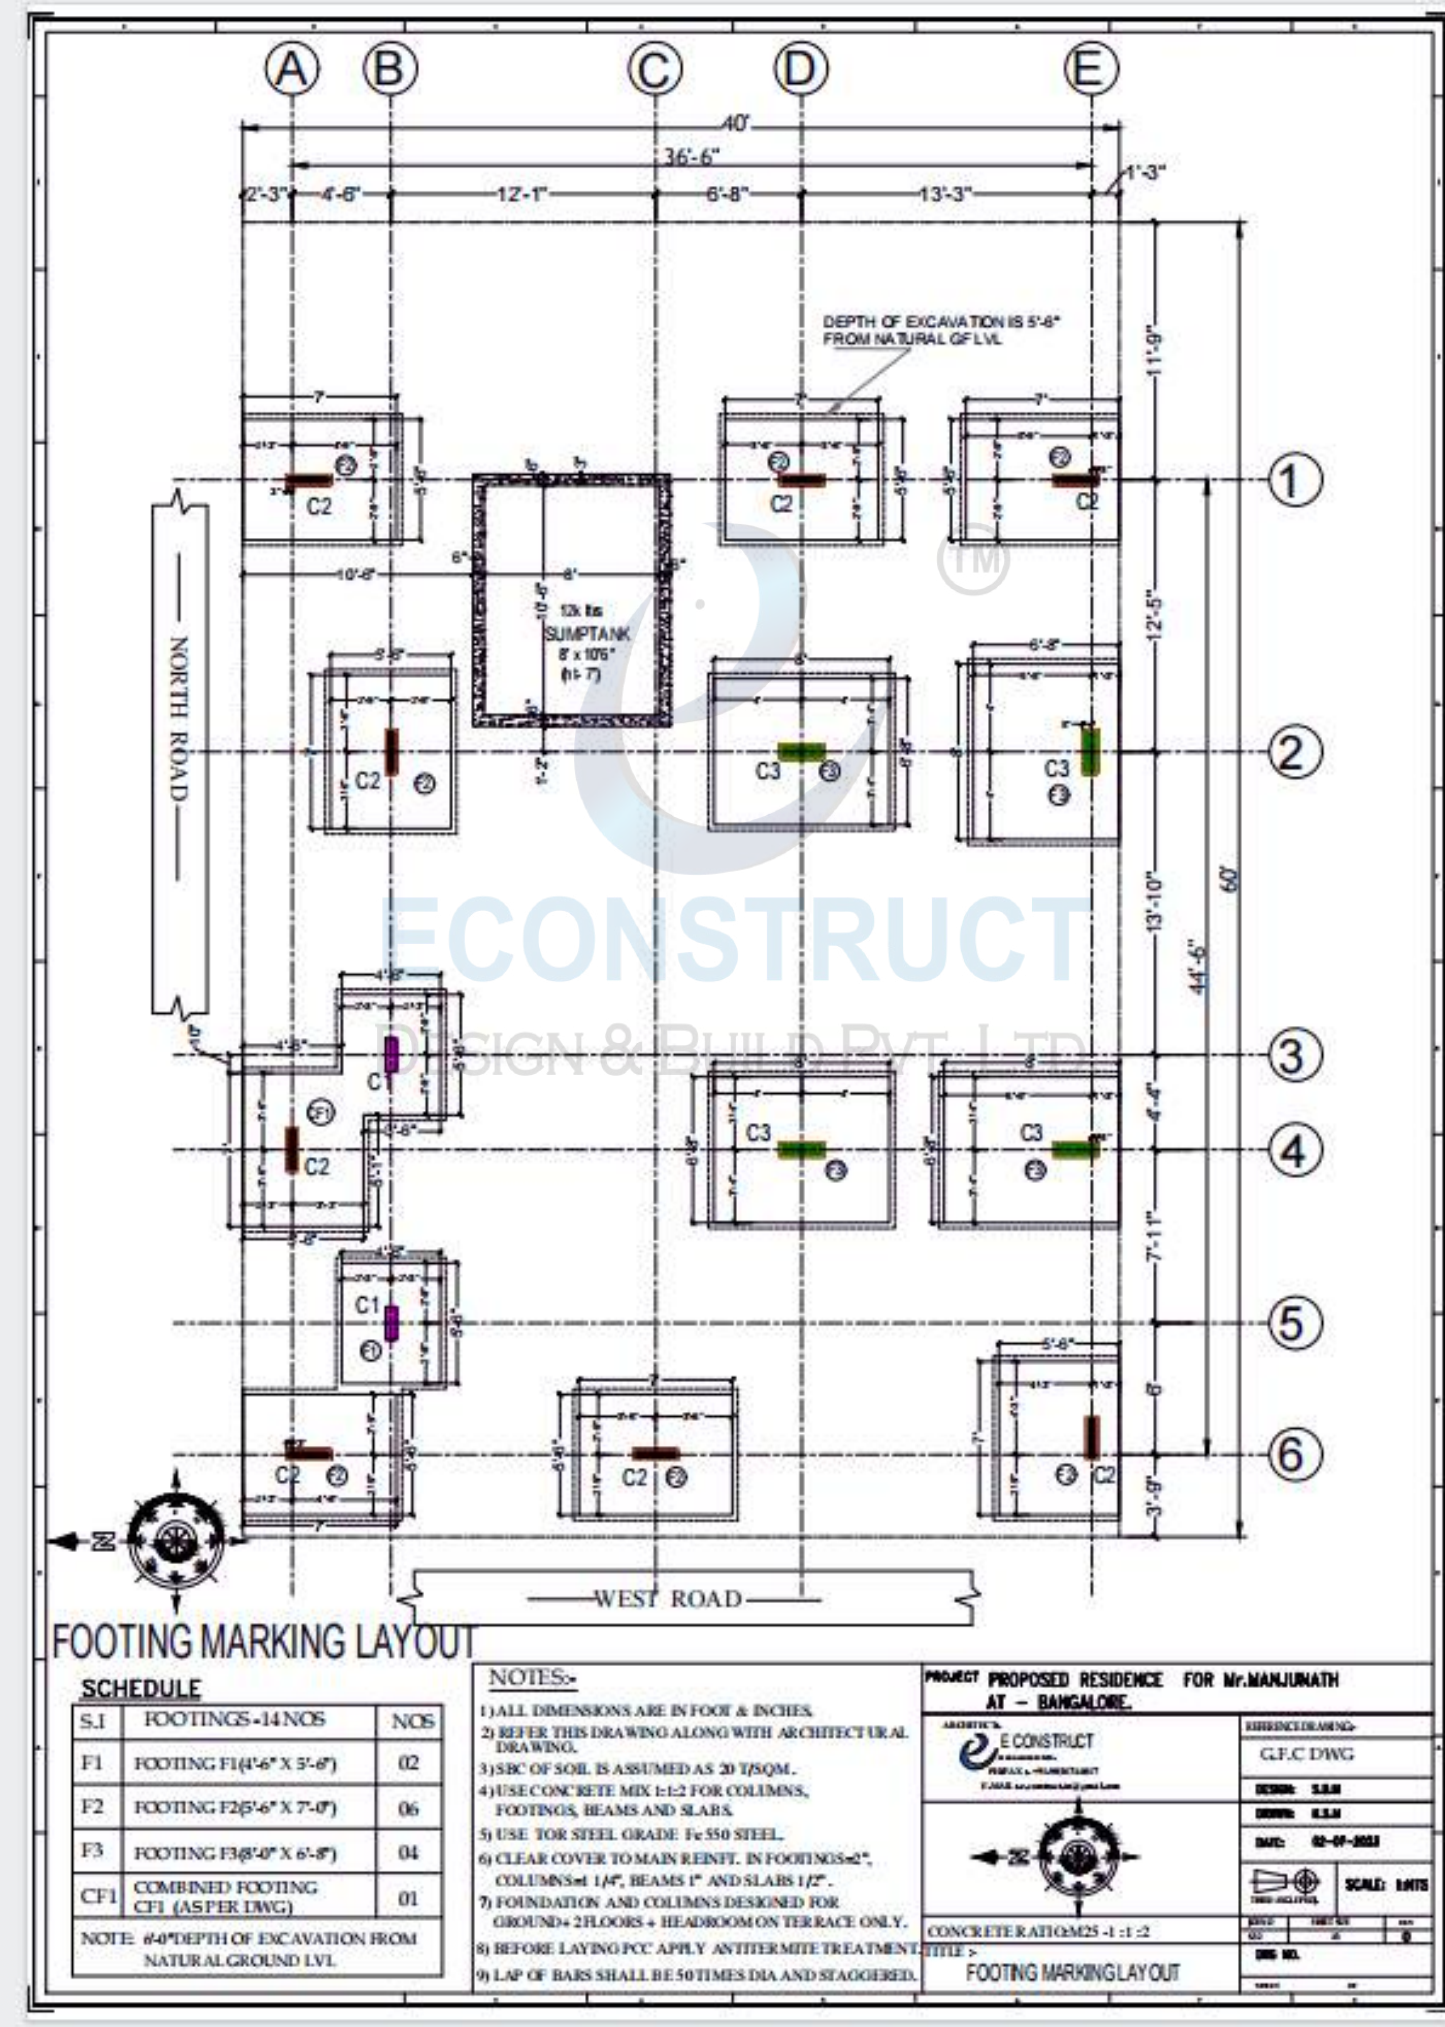


PROJECT PROPOSED RESIDENCE FOR Mr.MANJUNATH AT - BANGALORE.		
ARCHITECT  ECONSTRUCT CORPORATION PLOT NO - 49 SASETHARI 5th STAGE, 4th CROSS, 4th MAIN ROAD	REFERENCE DRAWING:-	
	G.F.C DWG	
	DESIGN: S.R.M	
	DRAWING: S.R.M	
	DATE: 02-07-2003	
	 SCALE: 1:100	
CONCRETE: RAJQM25-1 : 1 : 2	DATE: 02-07-2003 BY: [Signature] (SIN. NO.	DATE: 02-07-2003 BY: [Signature] (SIN. NO.


PROJECT PROPOSED RESIDENCE FOR Mr.MANJUNATH AT - BANGALORE.		
E CONSTRUCT PROFESSIONAL CONSULTANTS P.O BOX 809070 CHENNAI-600 090 E MAIL : econstruct@gmail.com	RESIDENCE DRAWING:-	
	G.F.C DWG	
	SECTION: S.S.W	
	DRAWN: S.S.W	
	DATE: 02-09-2023	
	SCALE: 1/100	
CONCRETE RATIO M25 :- 1 : 1 : 2 TITLE > PEDESTAL DETAILS		

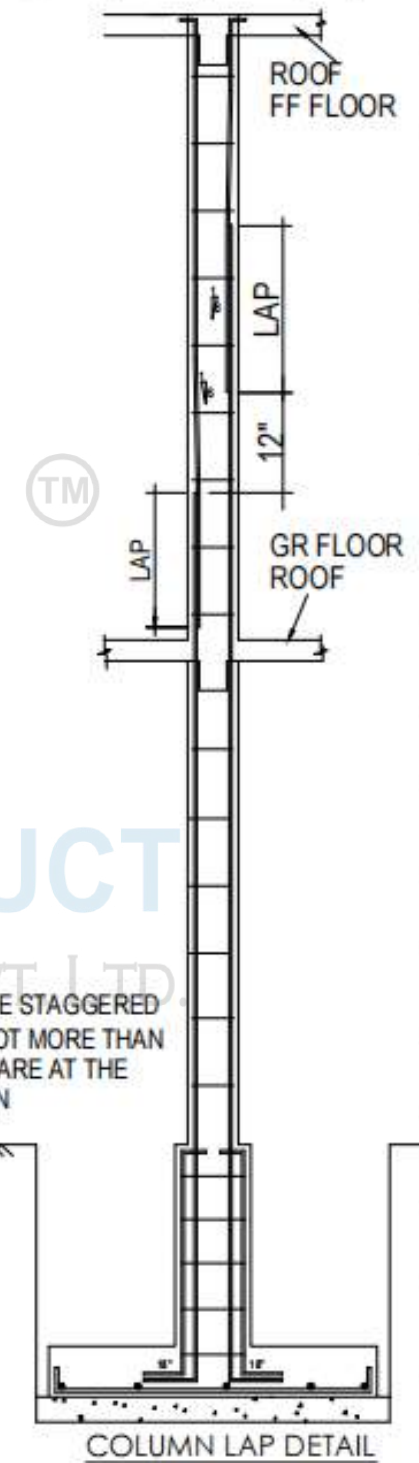

05

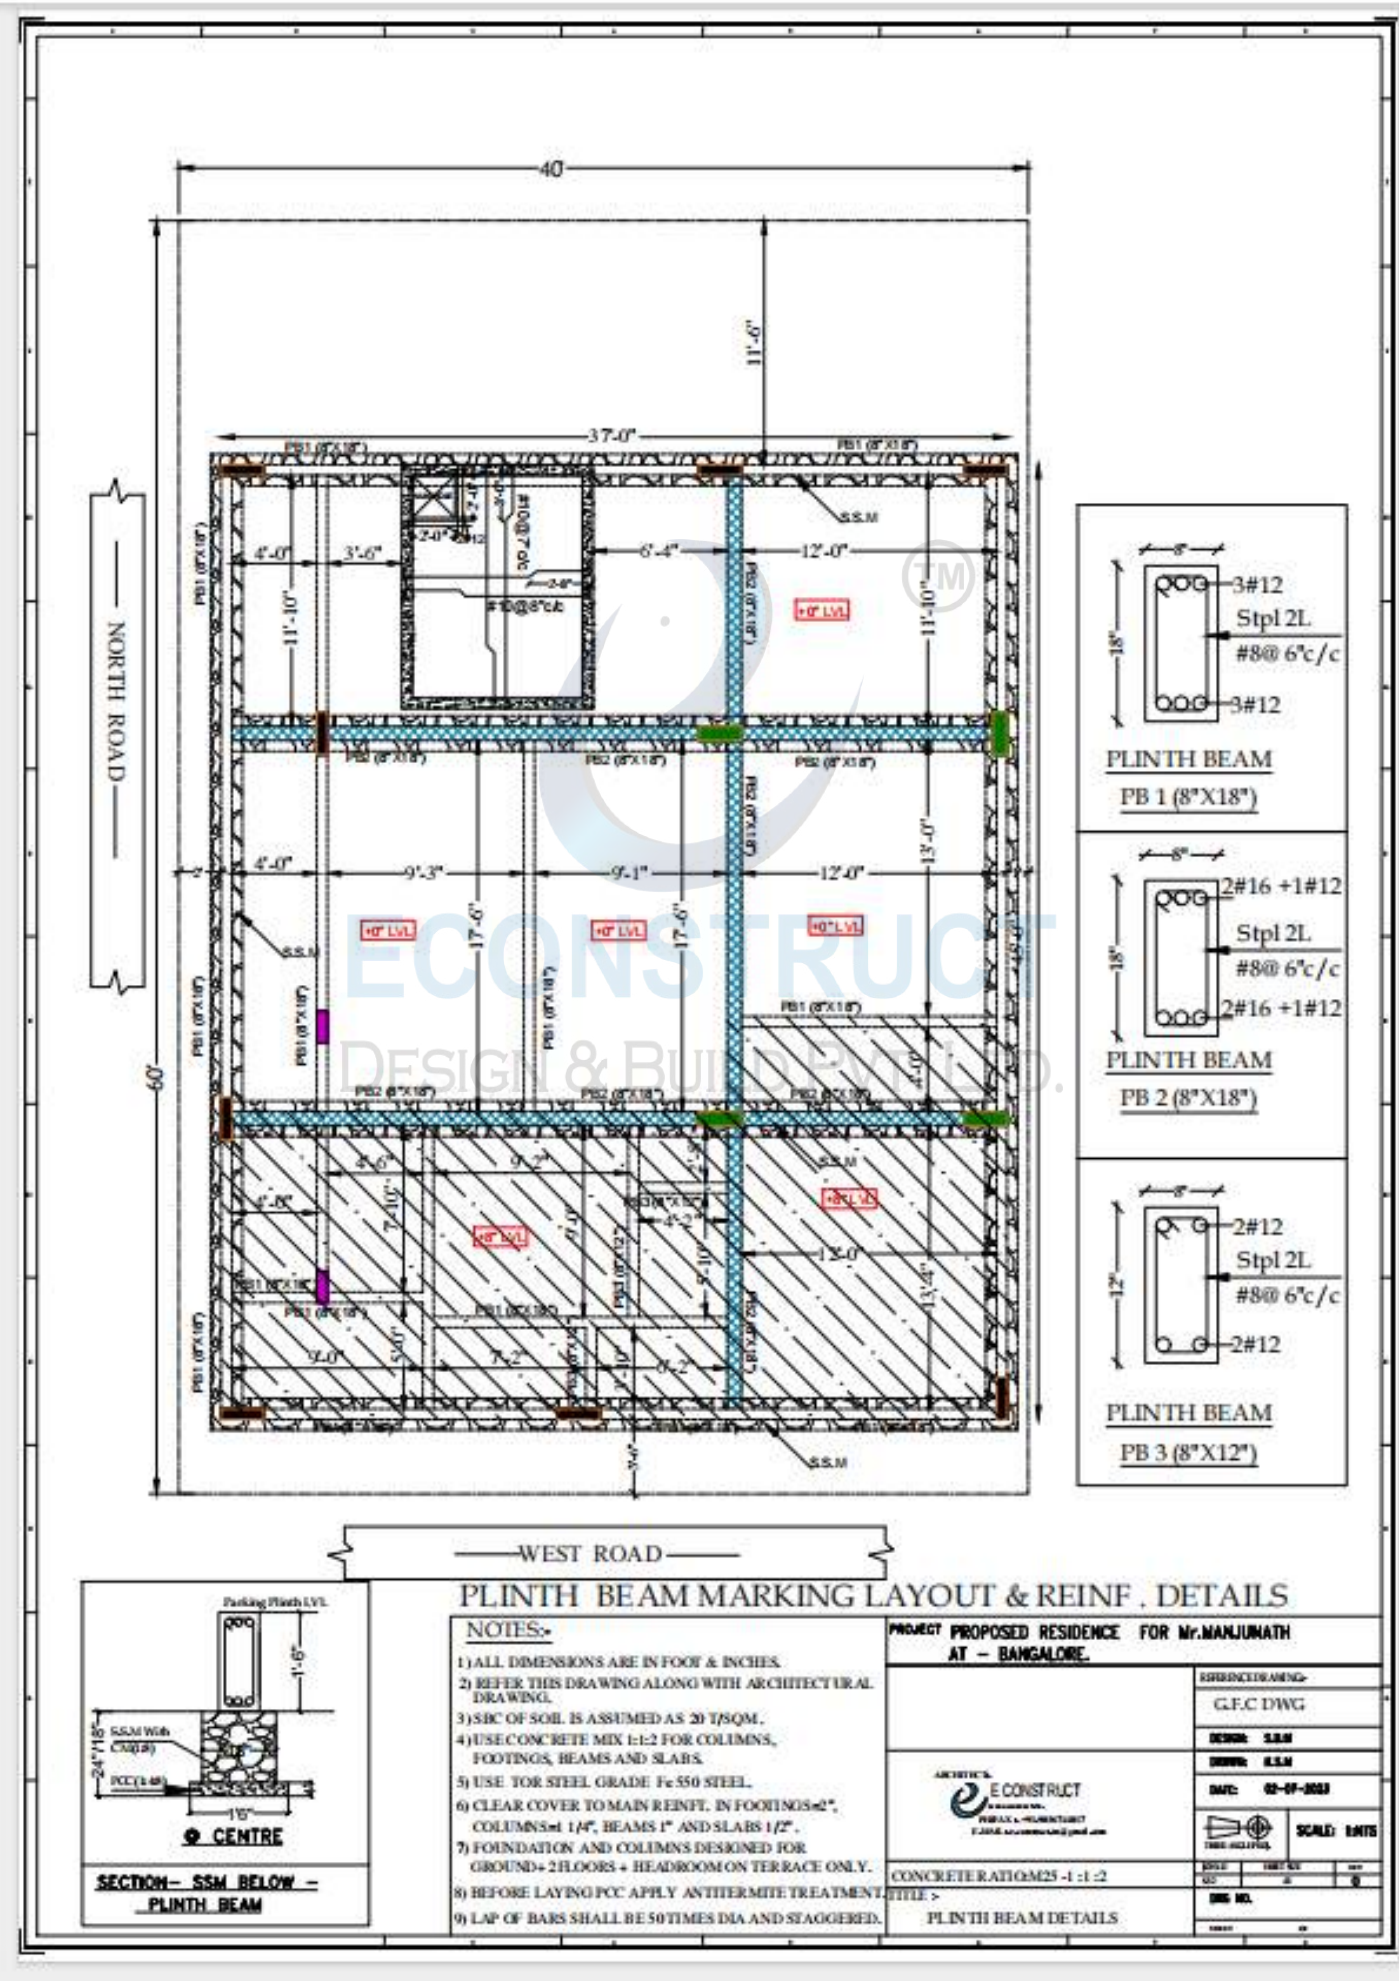PLINTH BEAM MARKING LAYOUT
& REINF. DETAILS


06


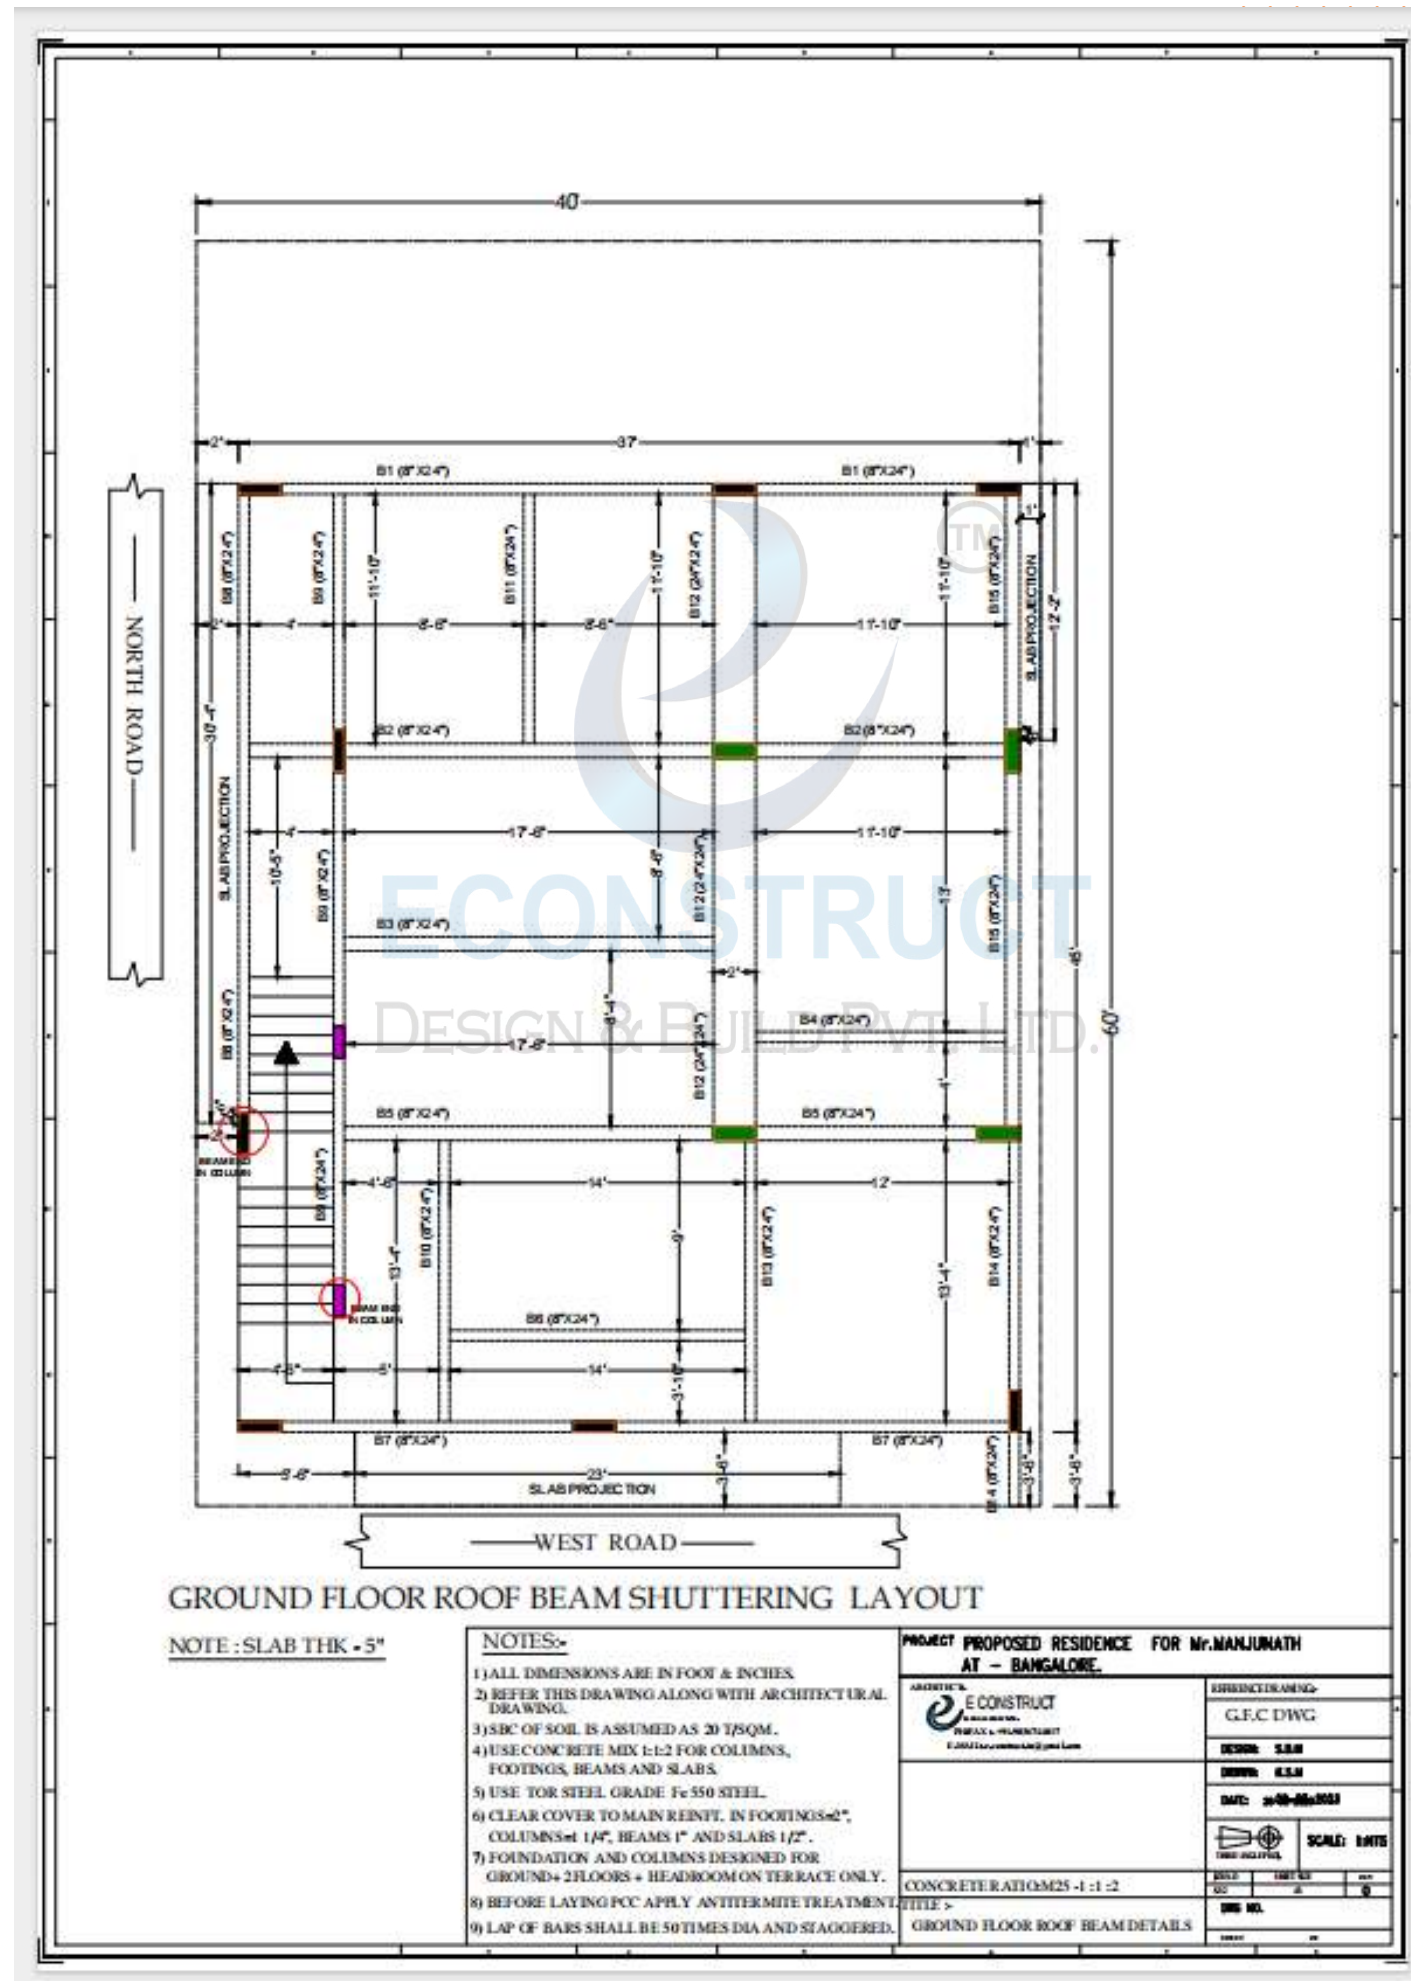
GROUND FLOOR ROOF BEAM
SHUTTERING LAYOUT



GROUND FLOOR - ROOF BEAM REINFORCEMENT DETAILS



GROUND FLOOR - ROOF BEAM REINFORCEMENT DETAILS

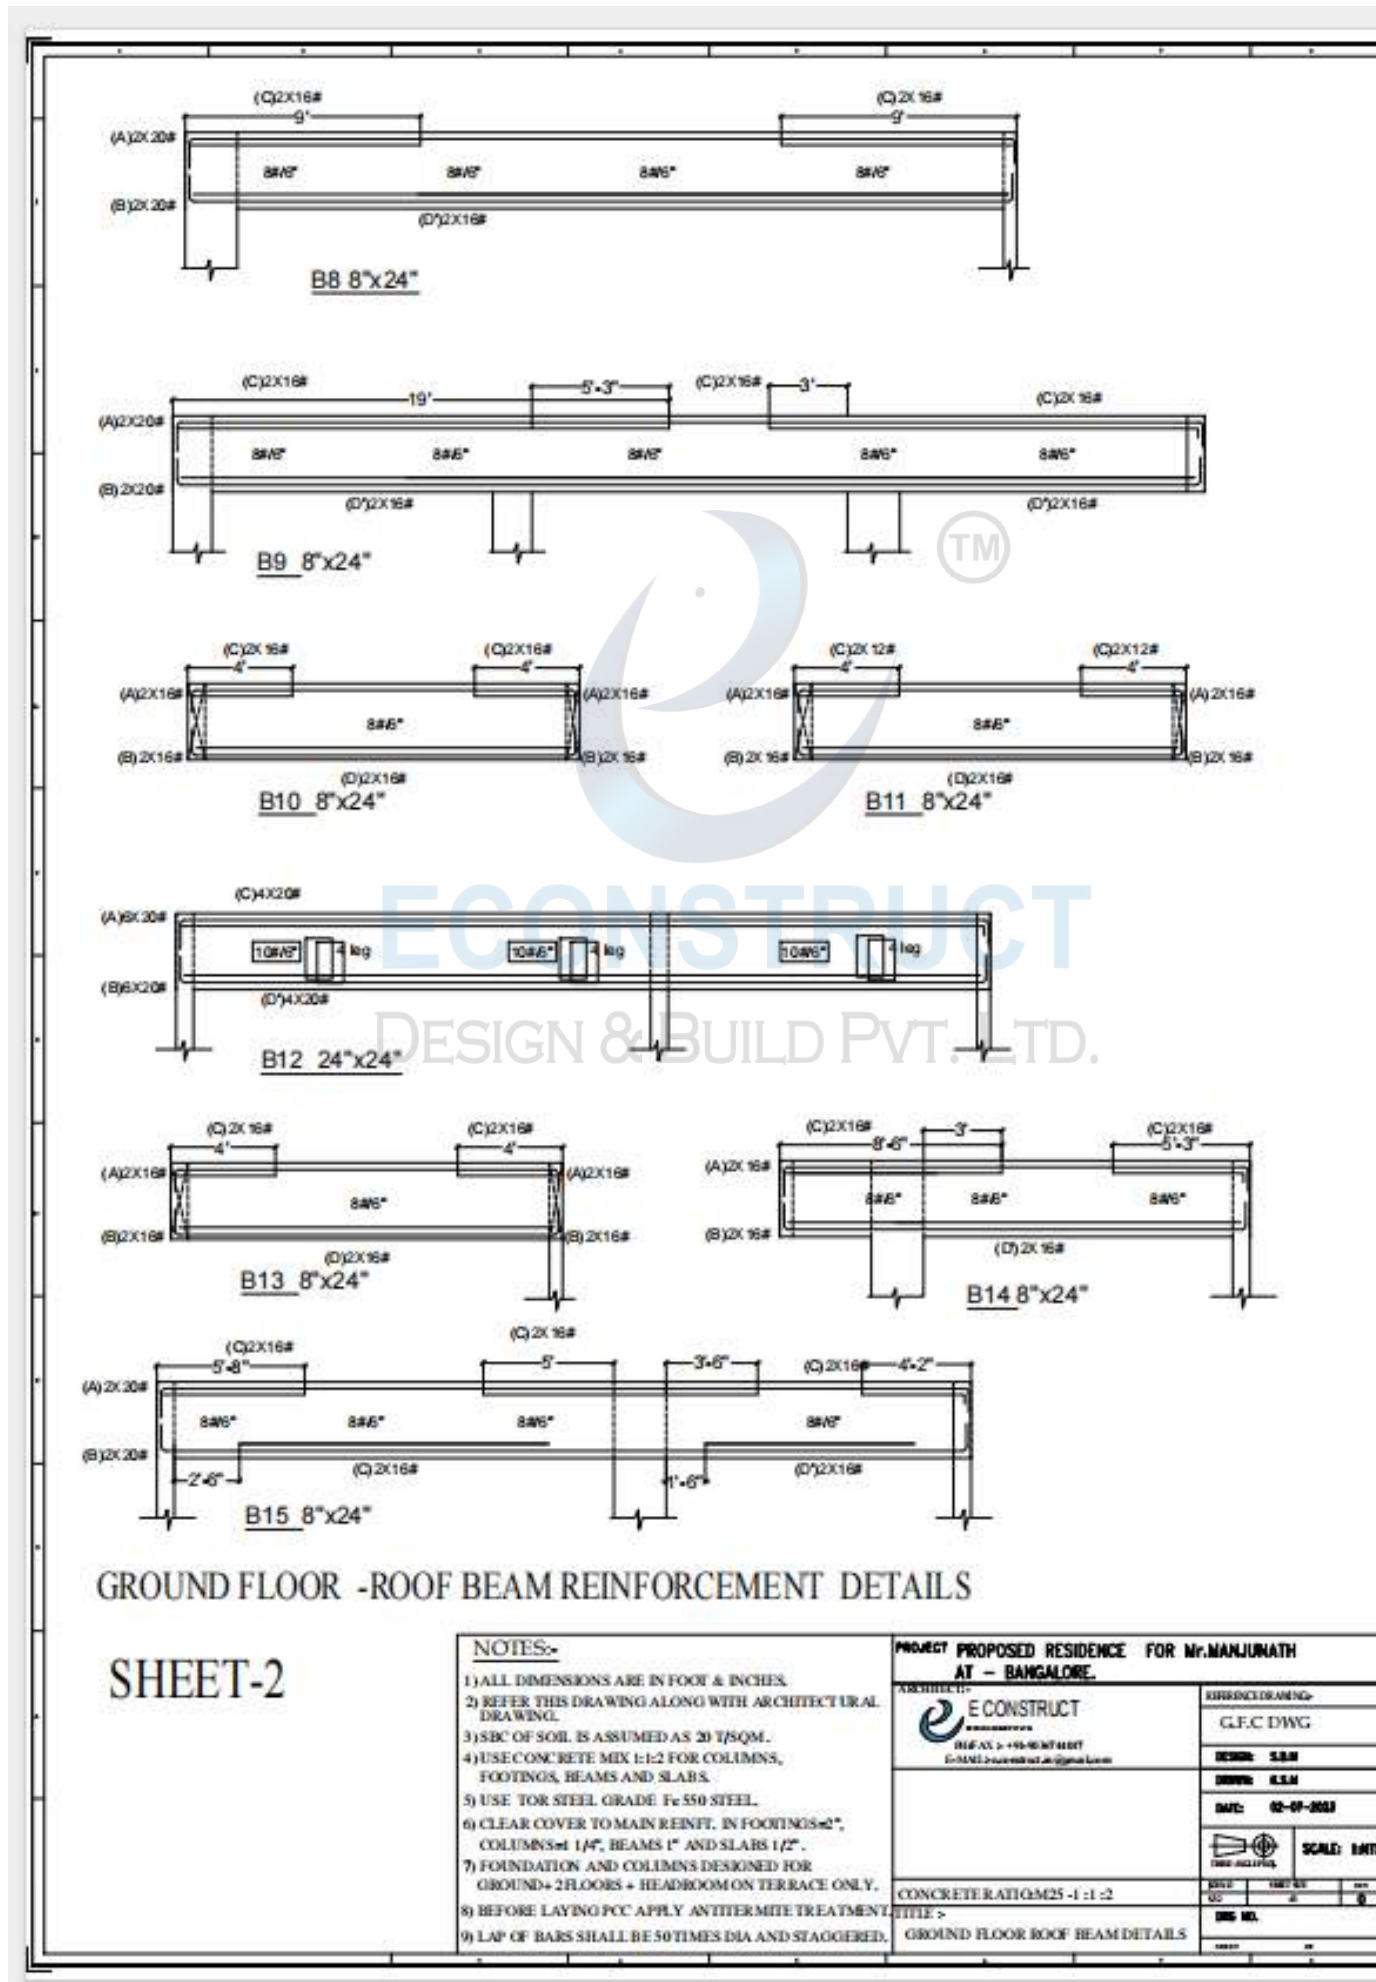


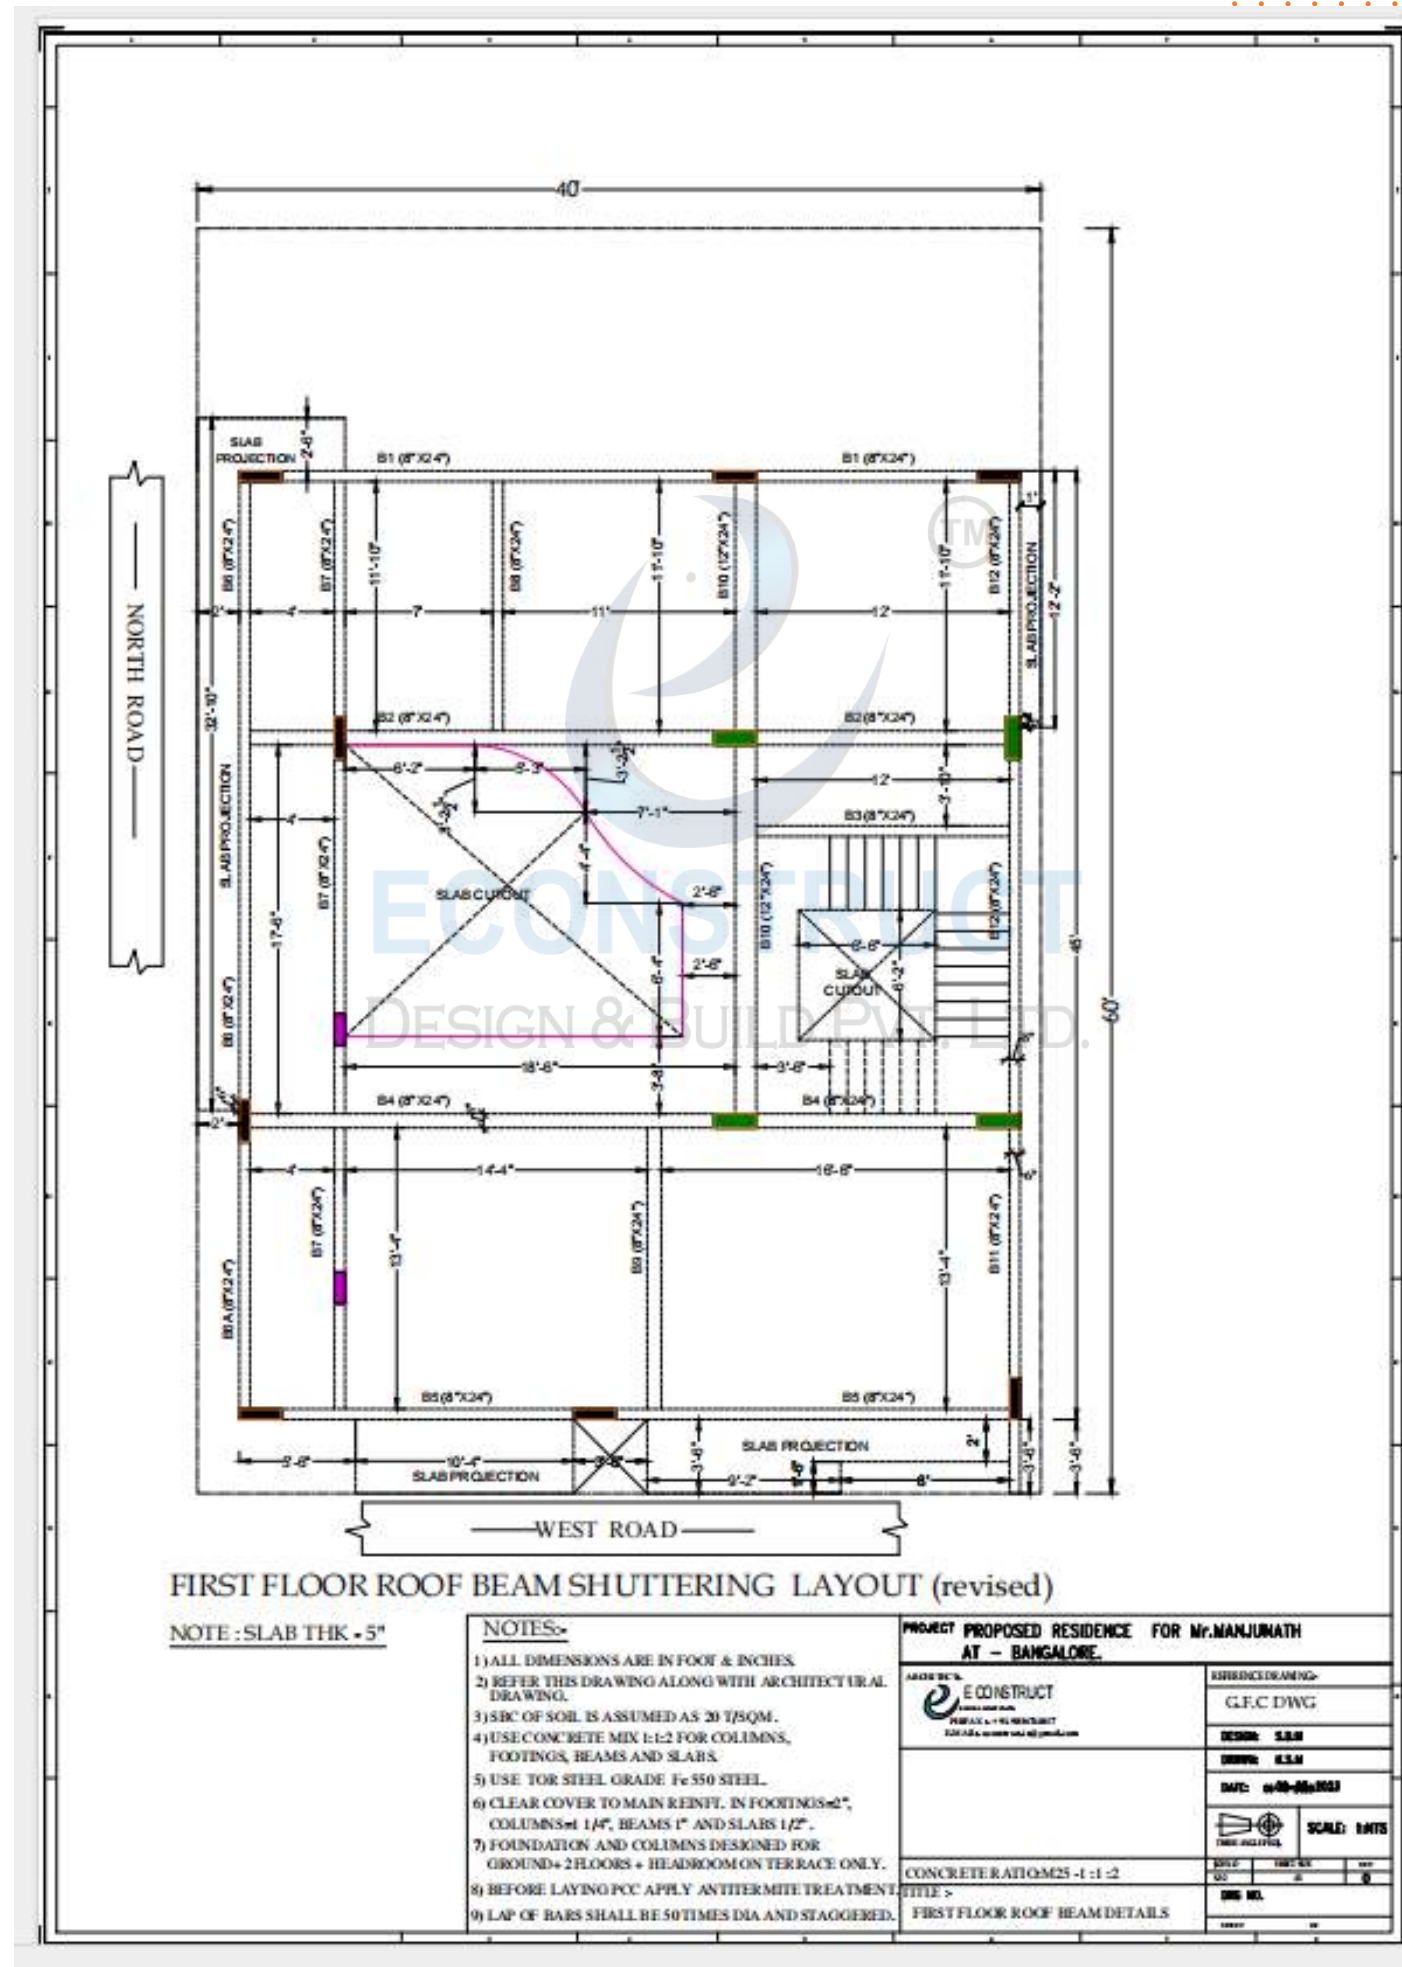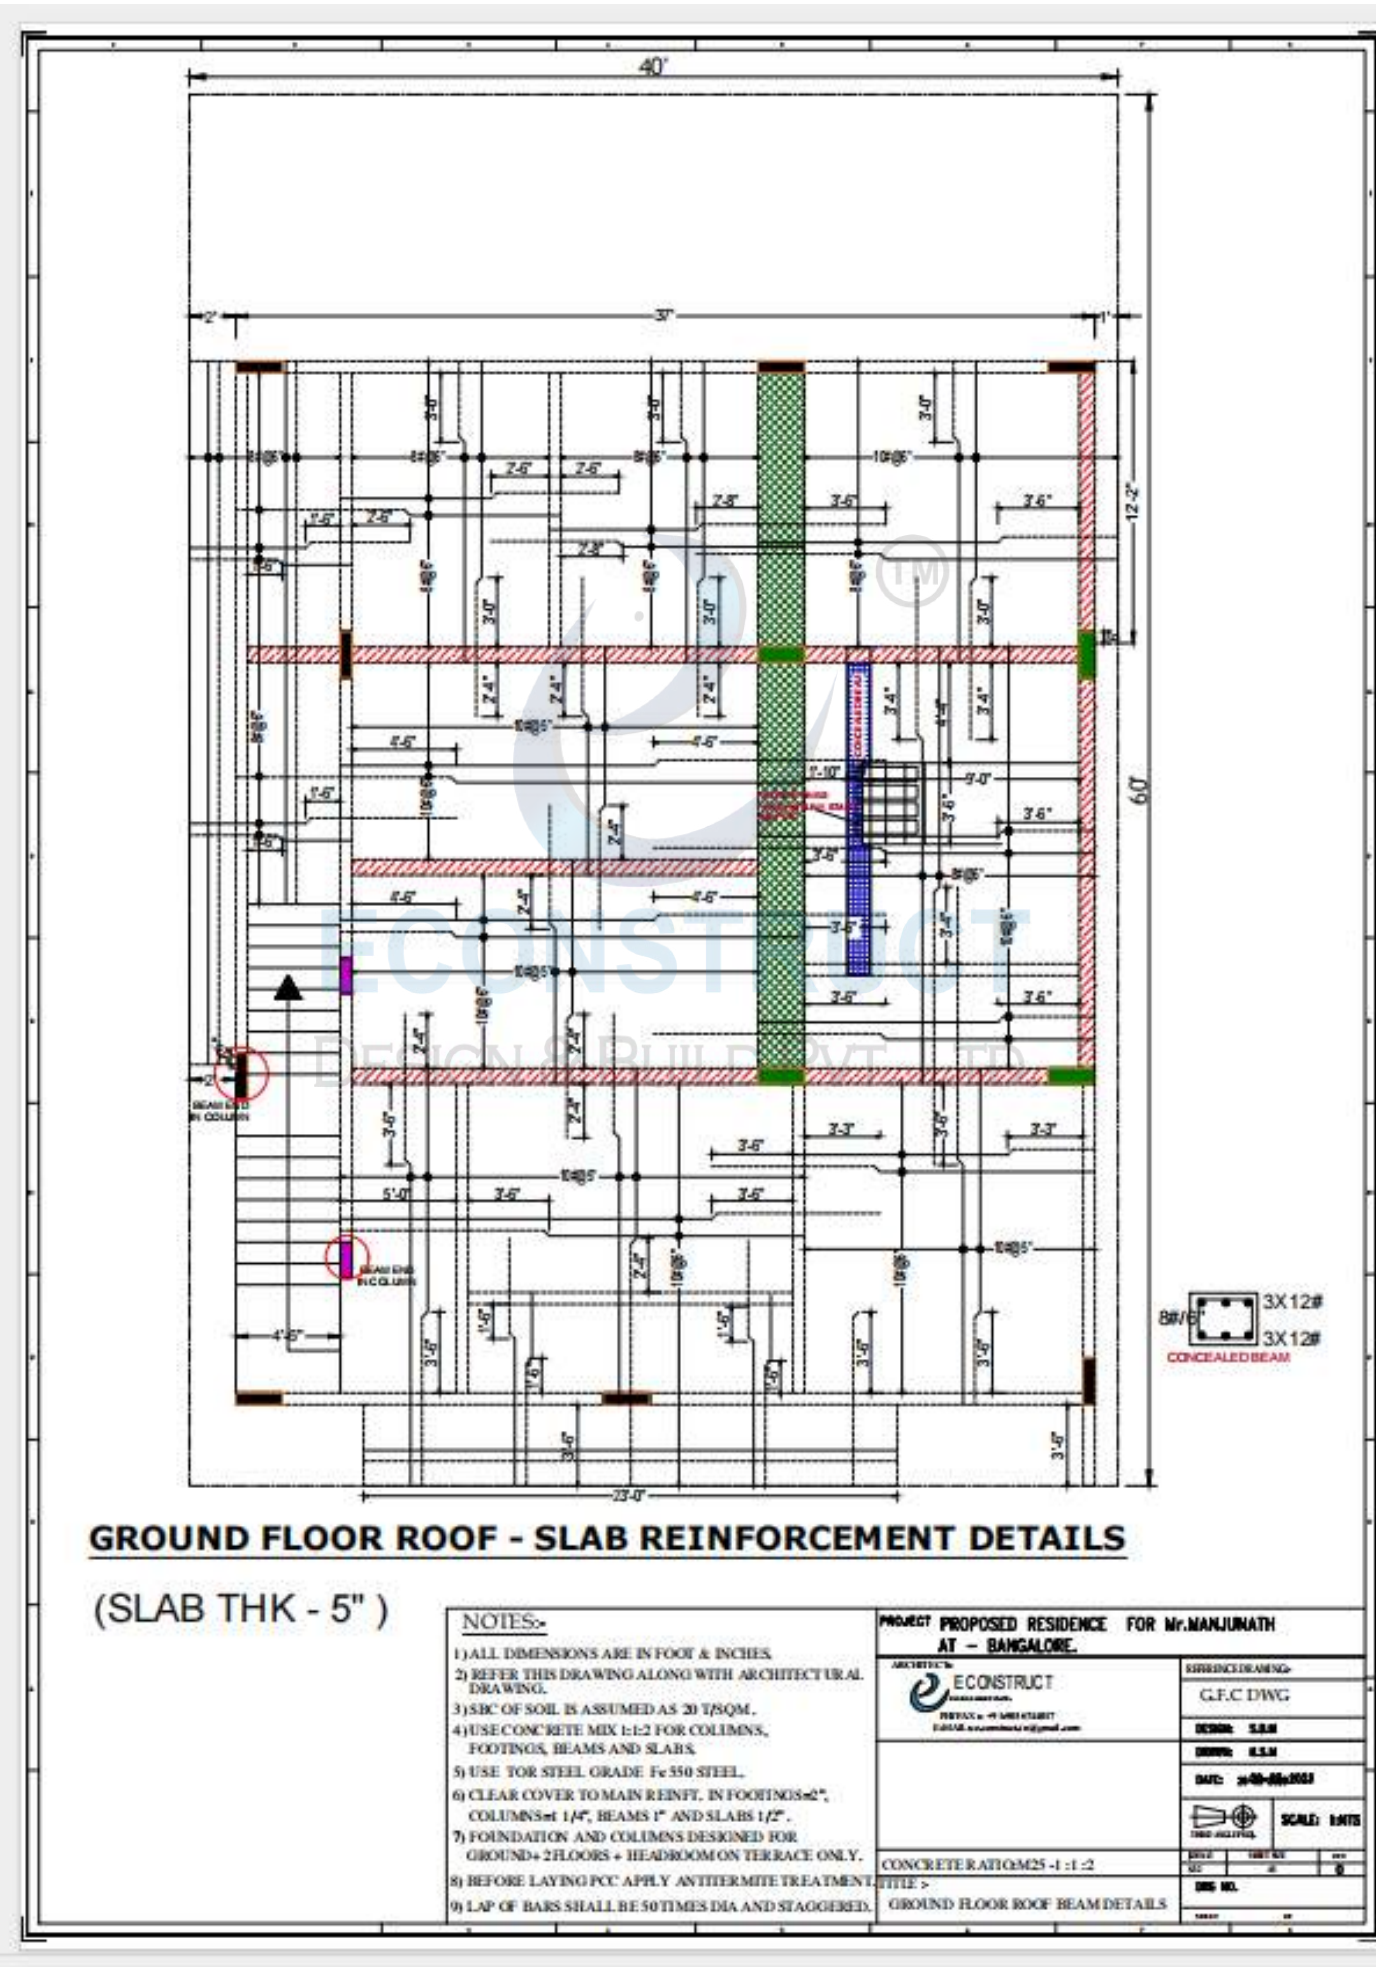

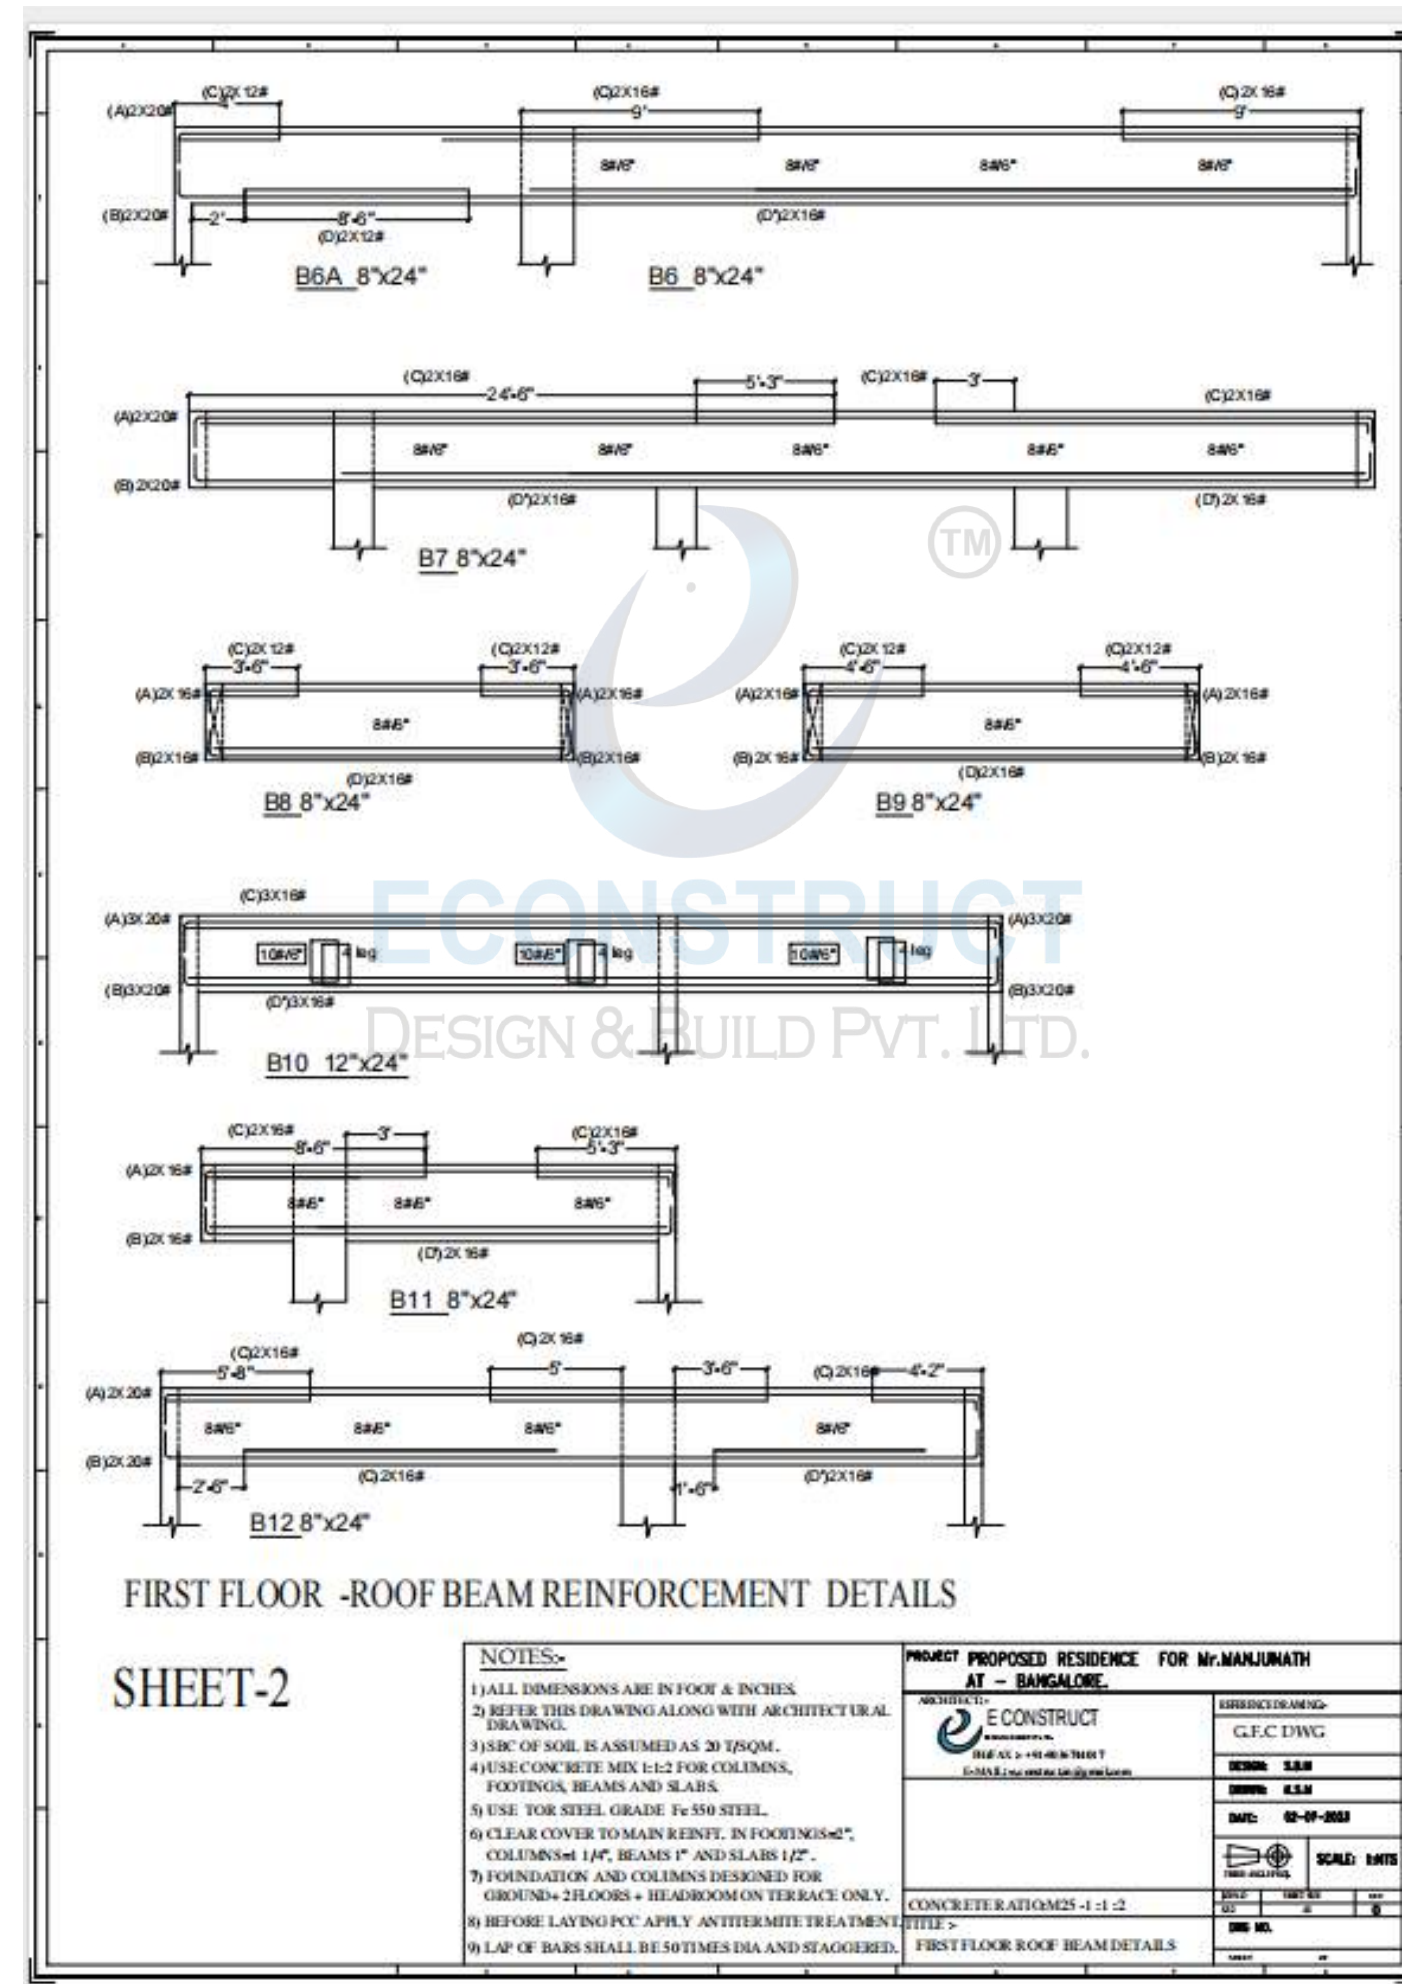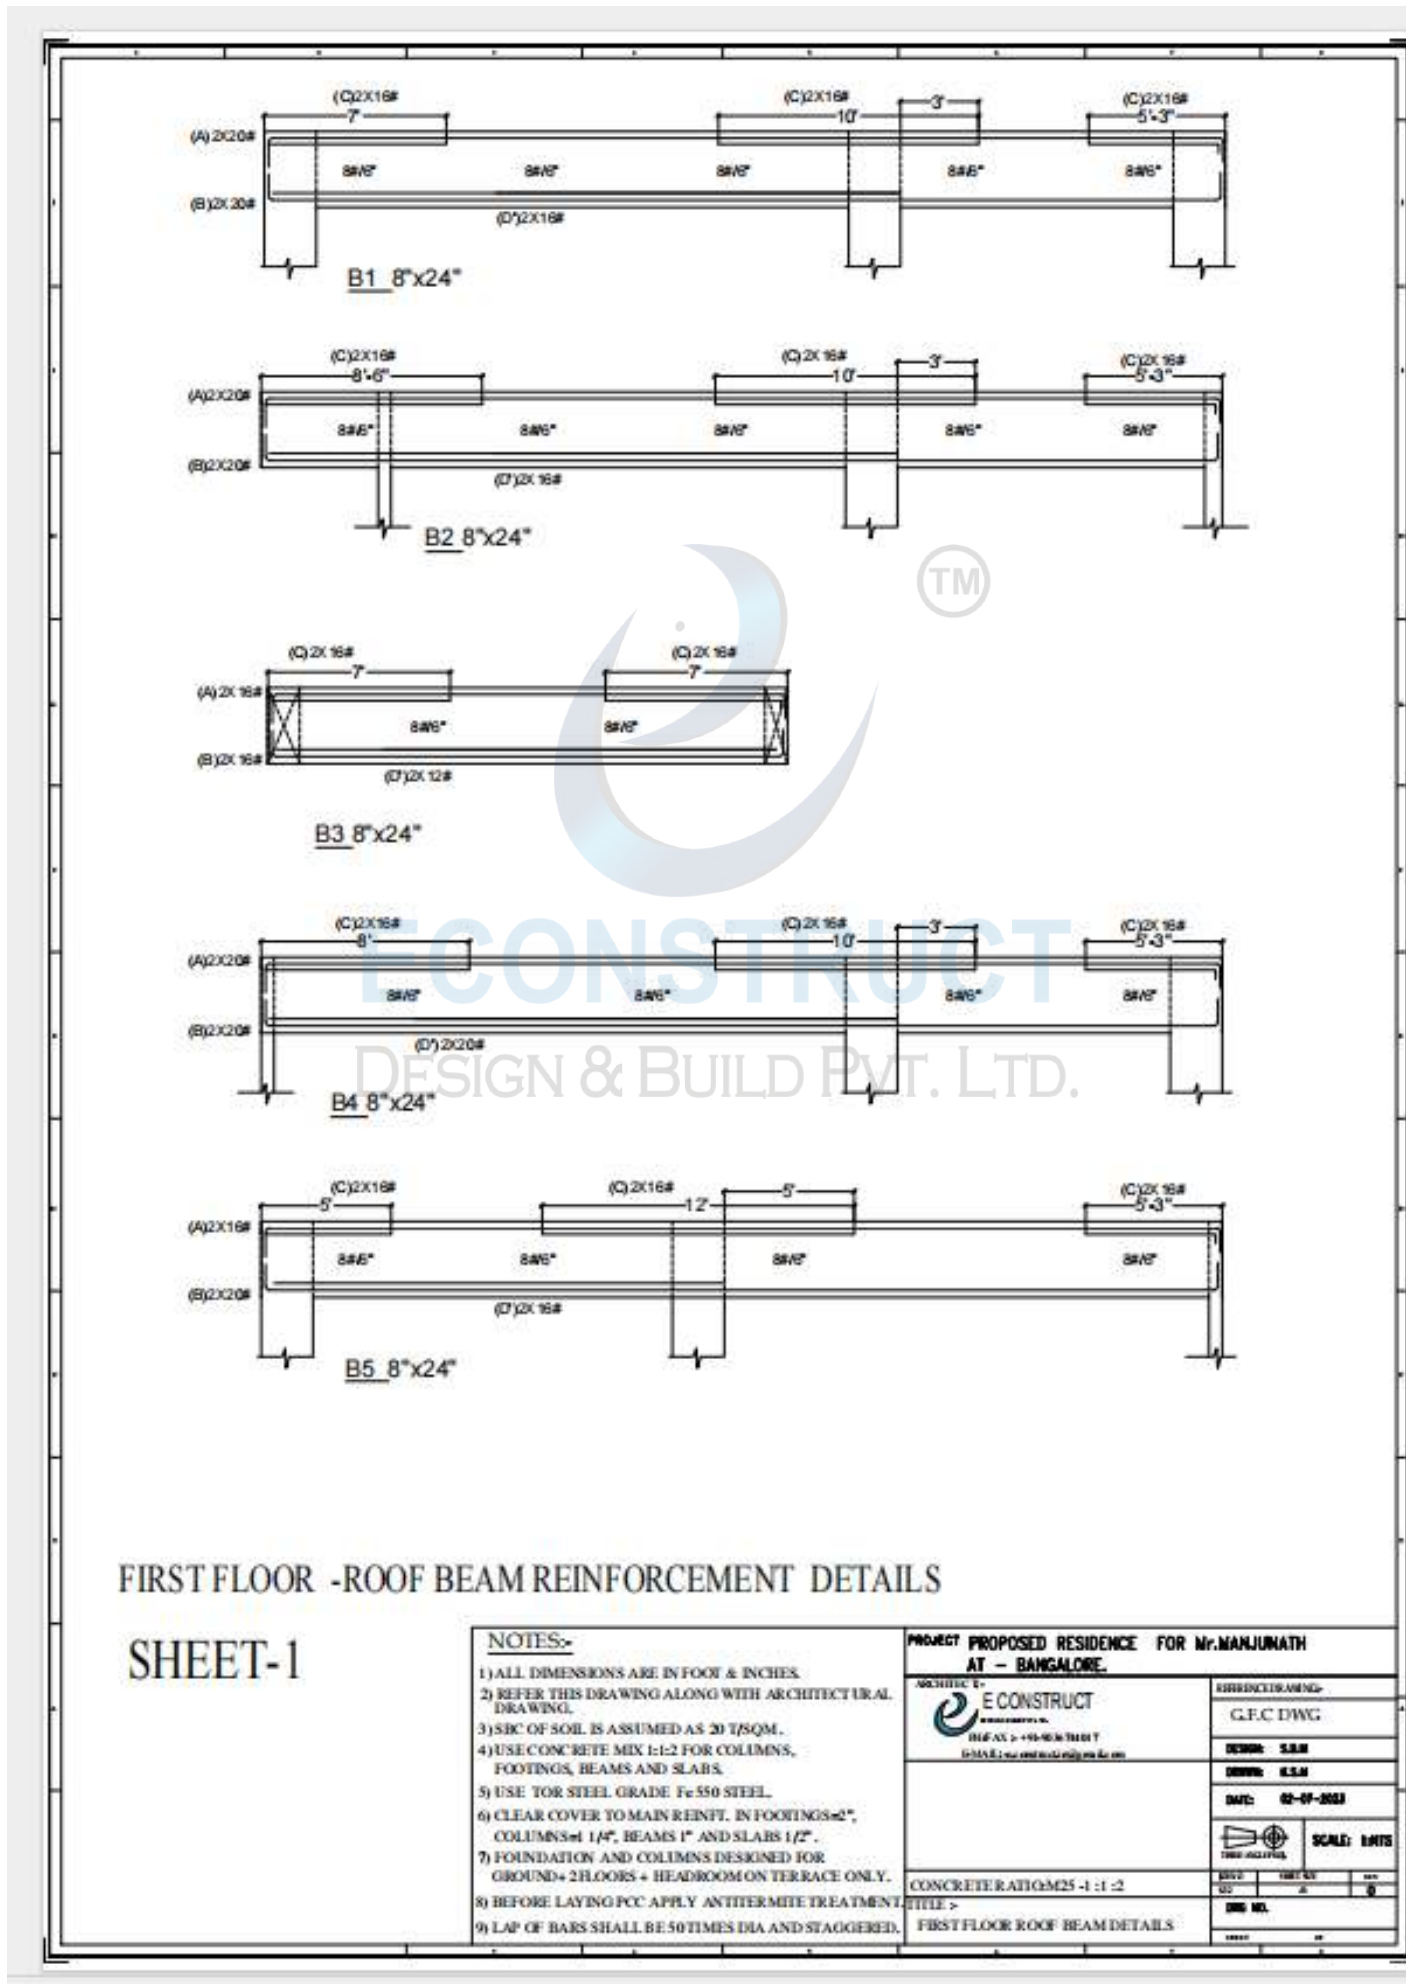


13

FIRST FLOOR ROOF - SLAB
REINFORCEMENT DETAILS (REVISED)

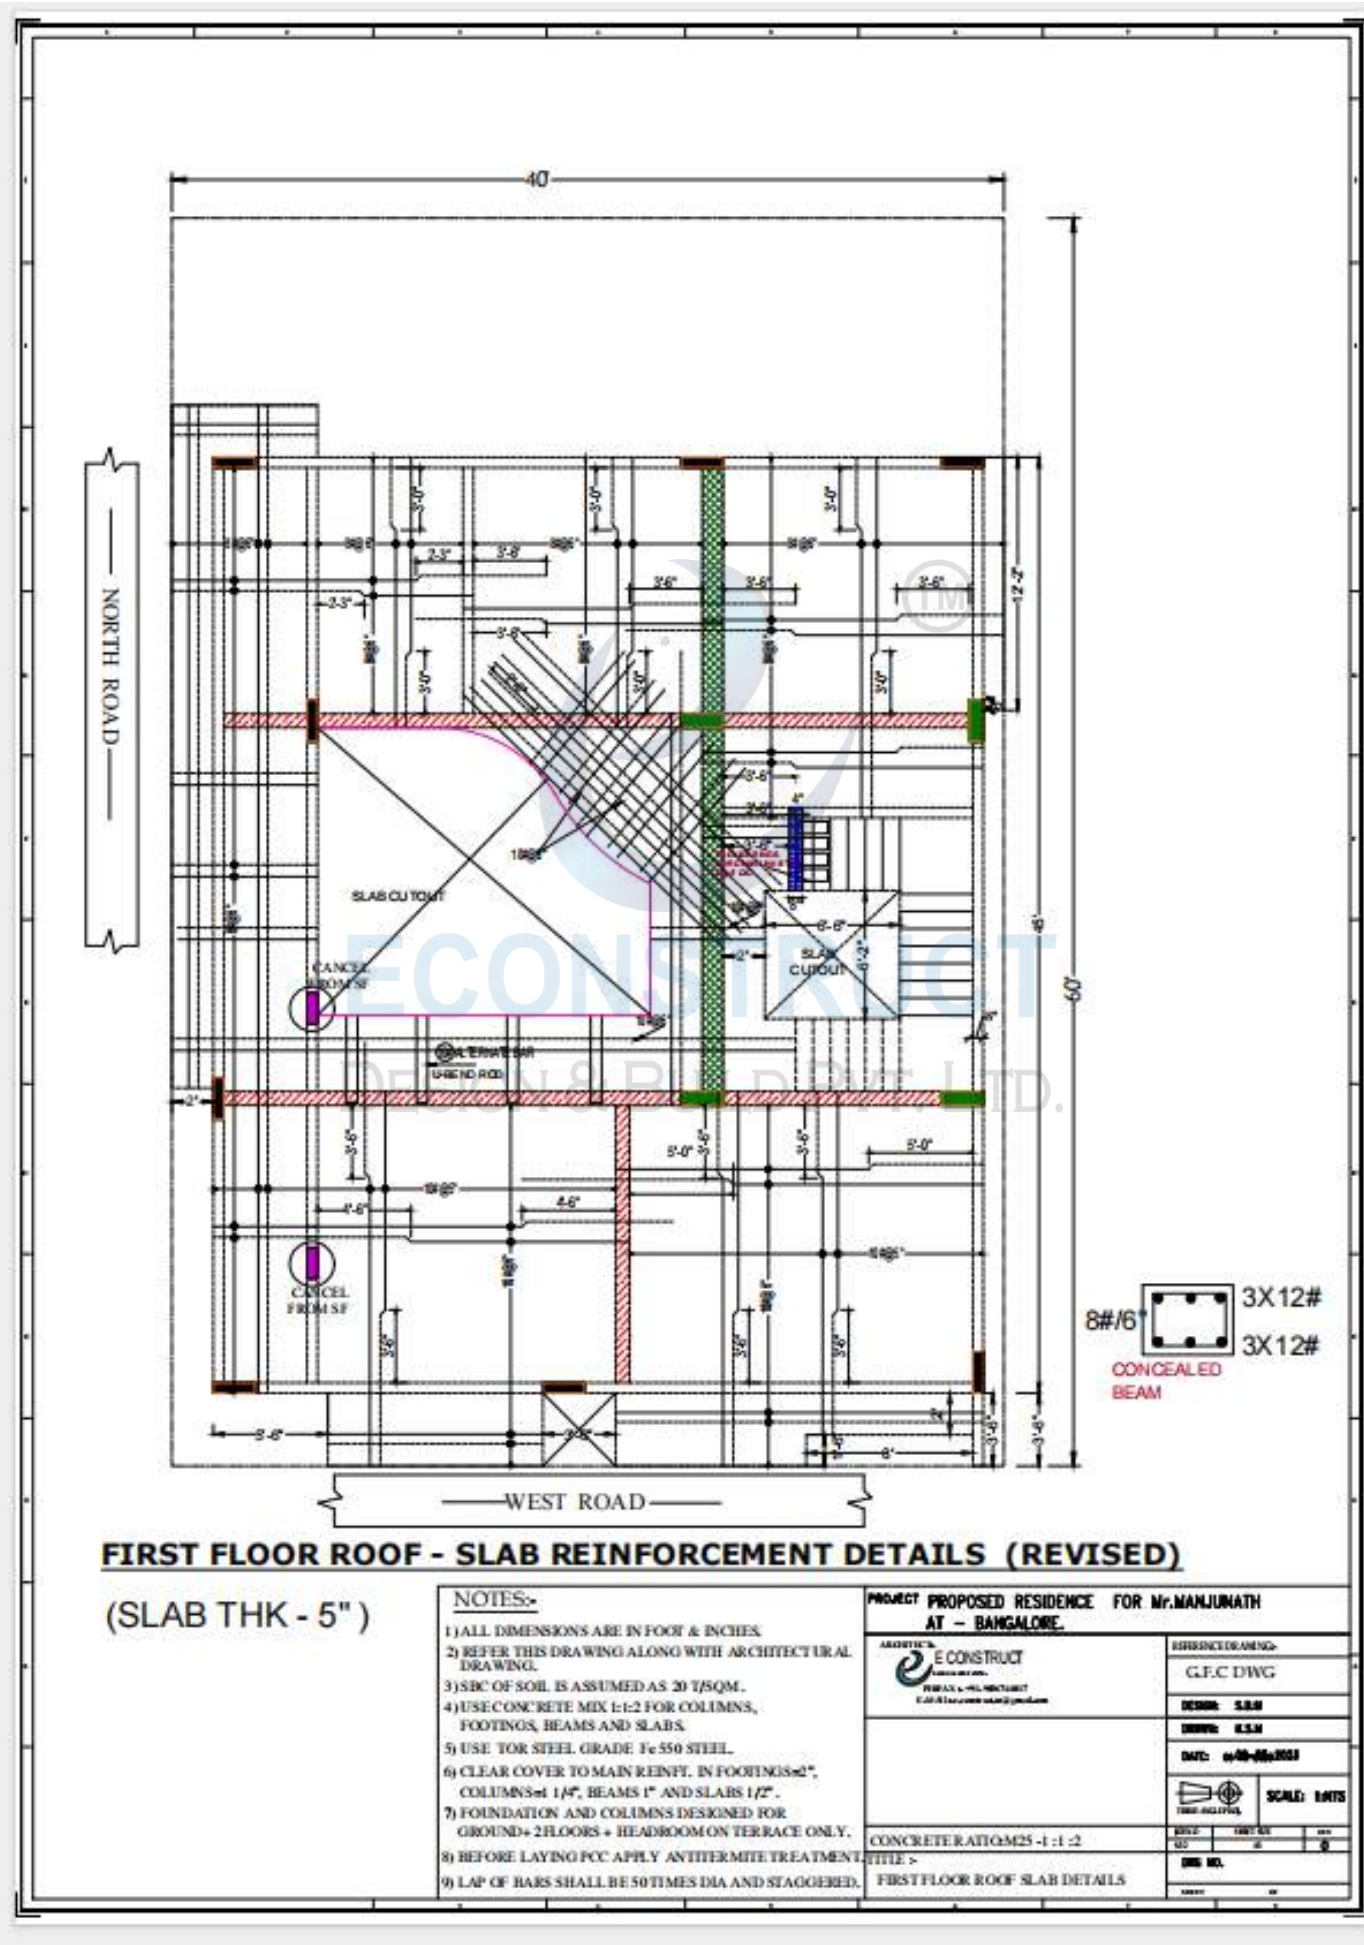


14


SECOND FLOOR ROOF BEAM
SHUTTERING LAYOUT-rvsd

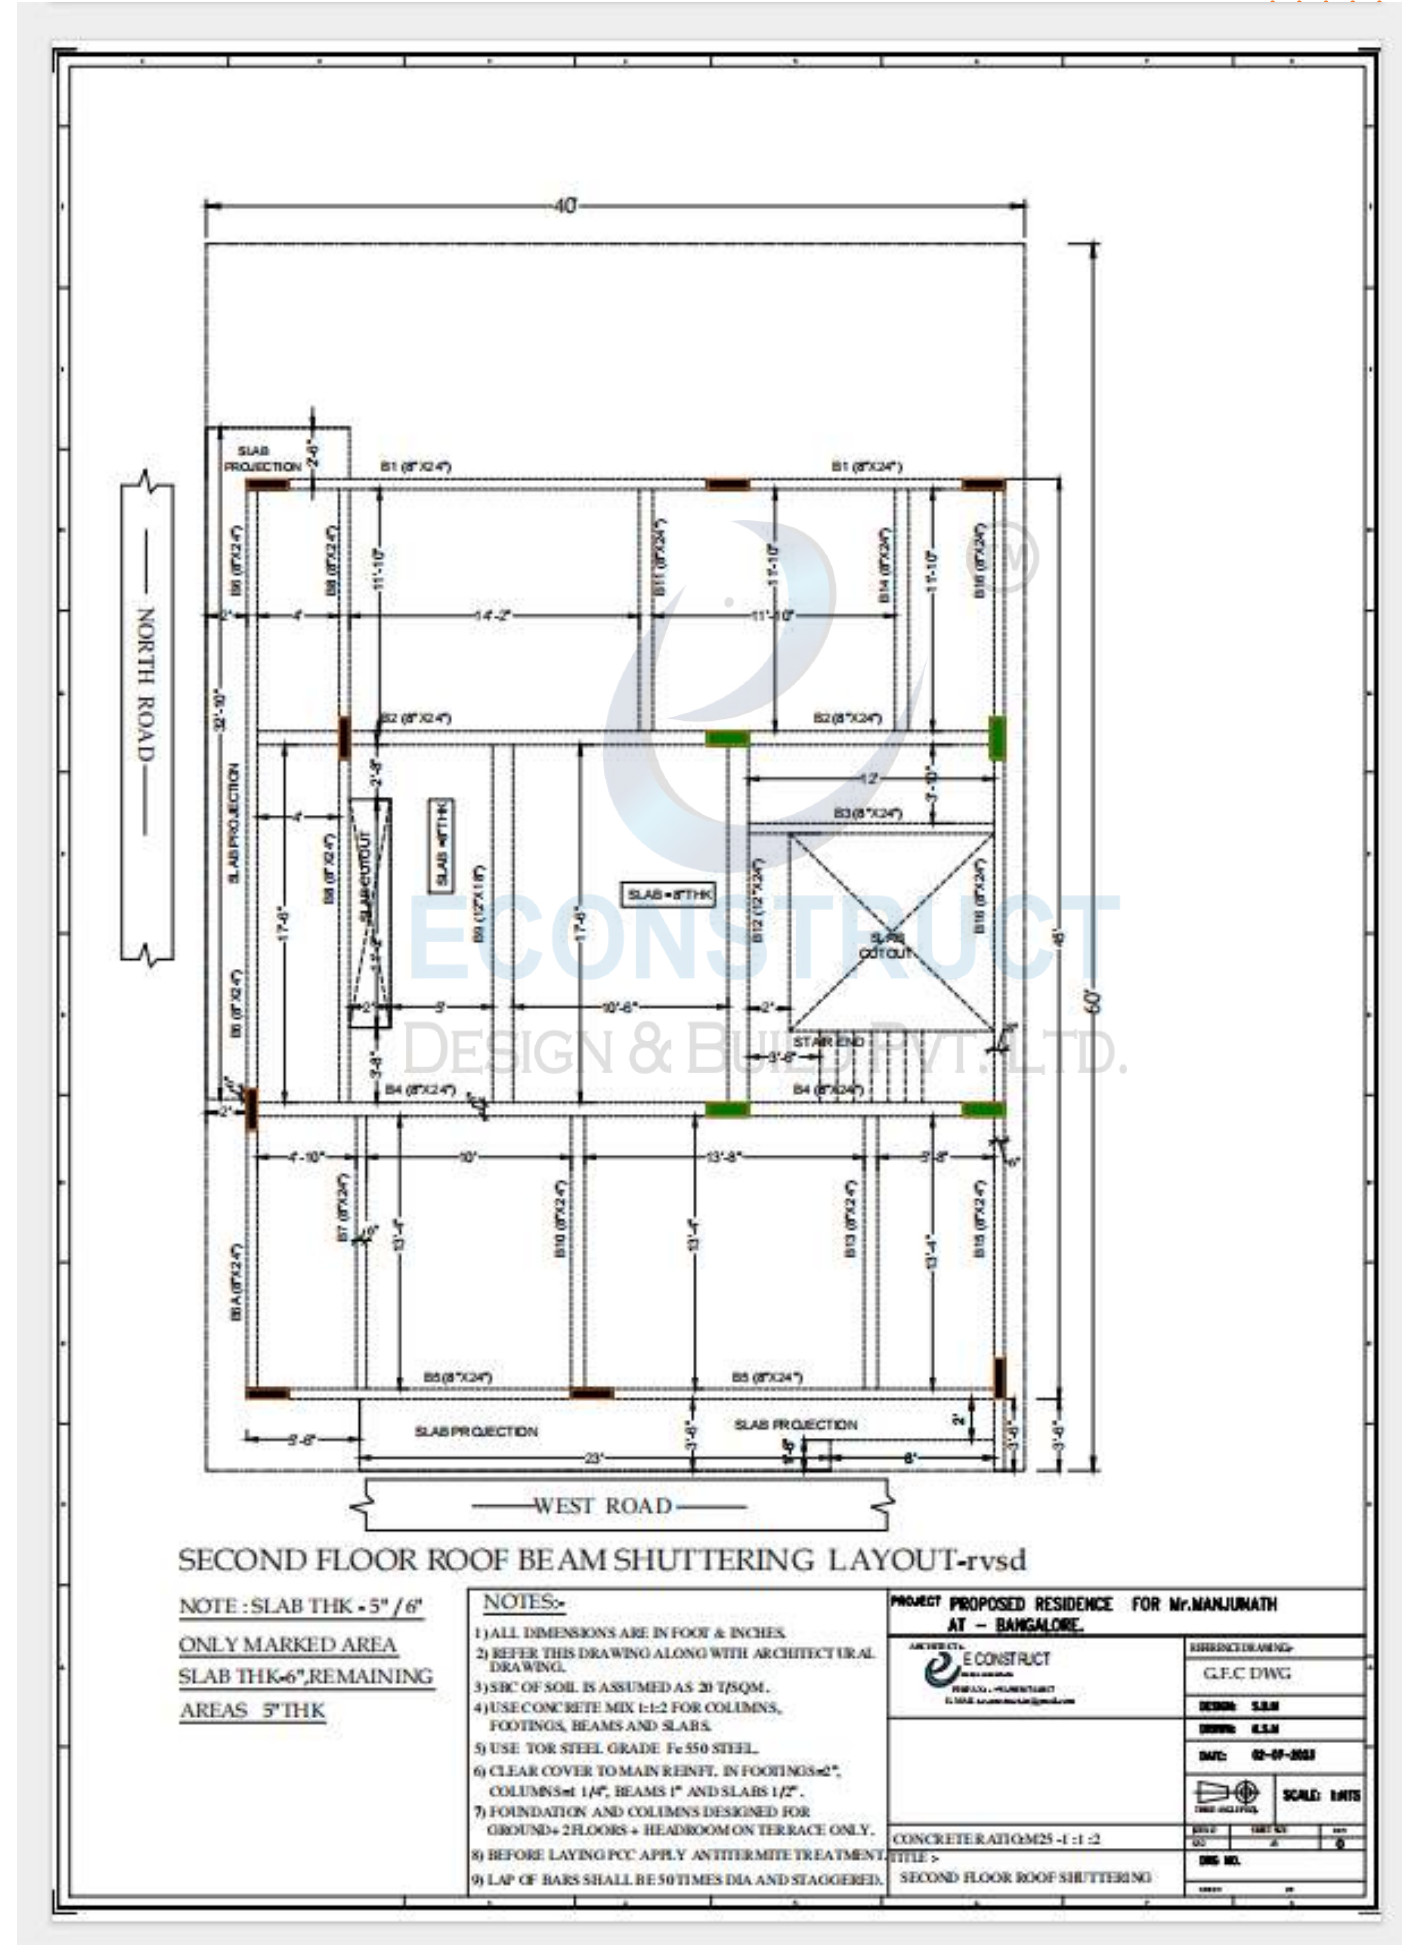

15. SECOND FLOOR - ROOF BEAM REINFORCEMENT DETAILS - SHEET-1

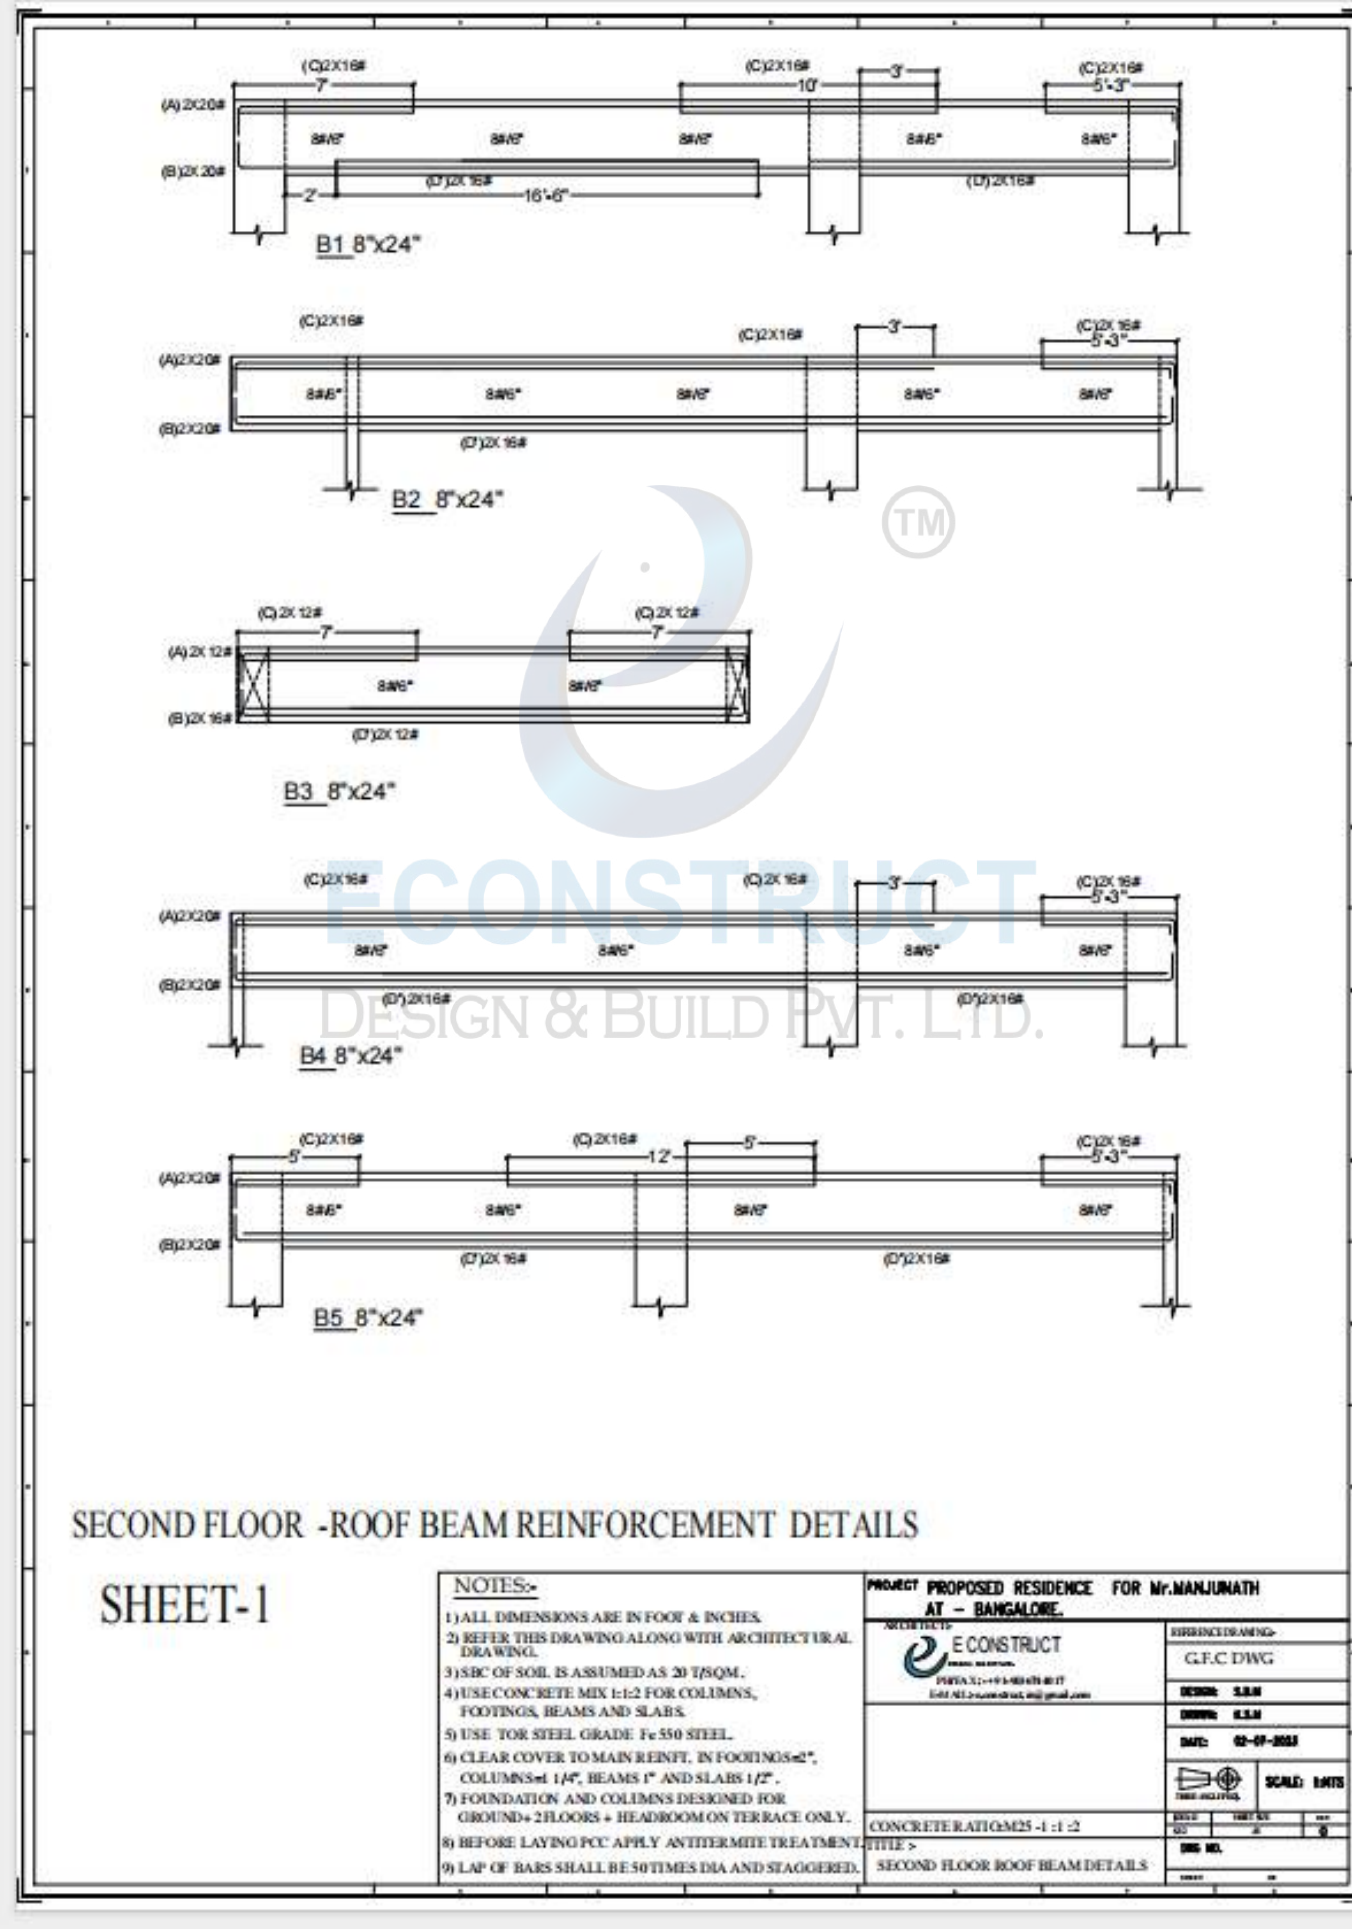


SECOND FLOOR - ROOF BEAM REINFORCEMENT DETAILS - SHEET-2

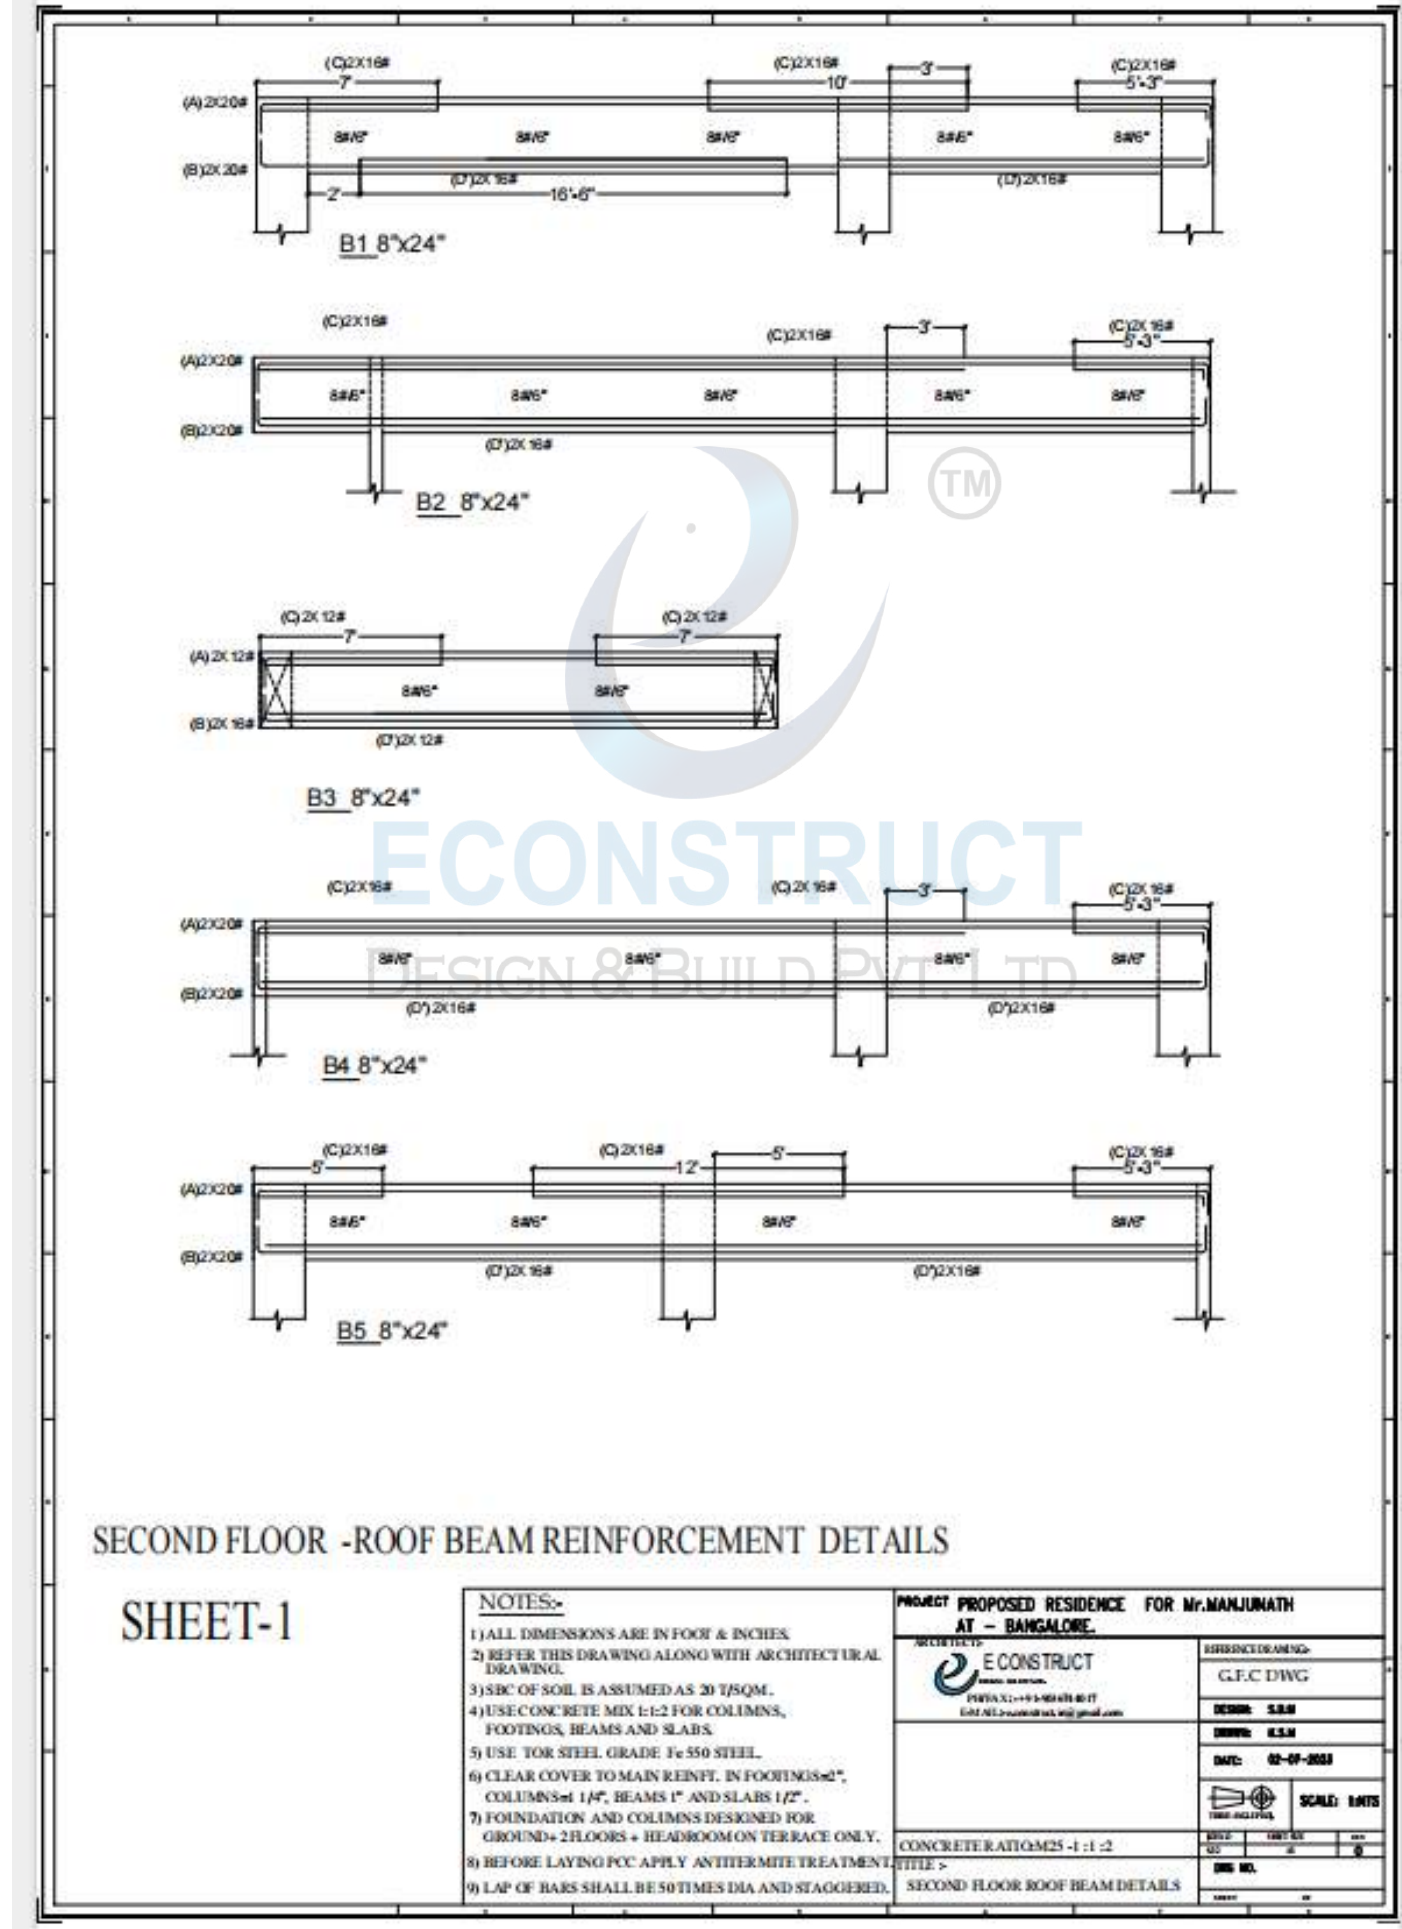


17

SECOND FLOOR ROOF - SLAB REINFORCEMENT DETAILS

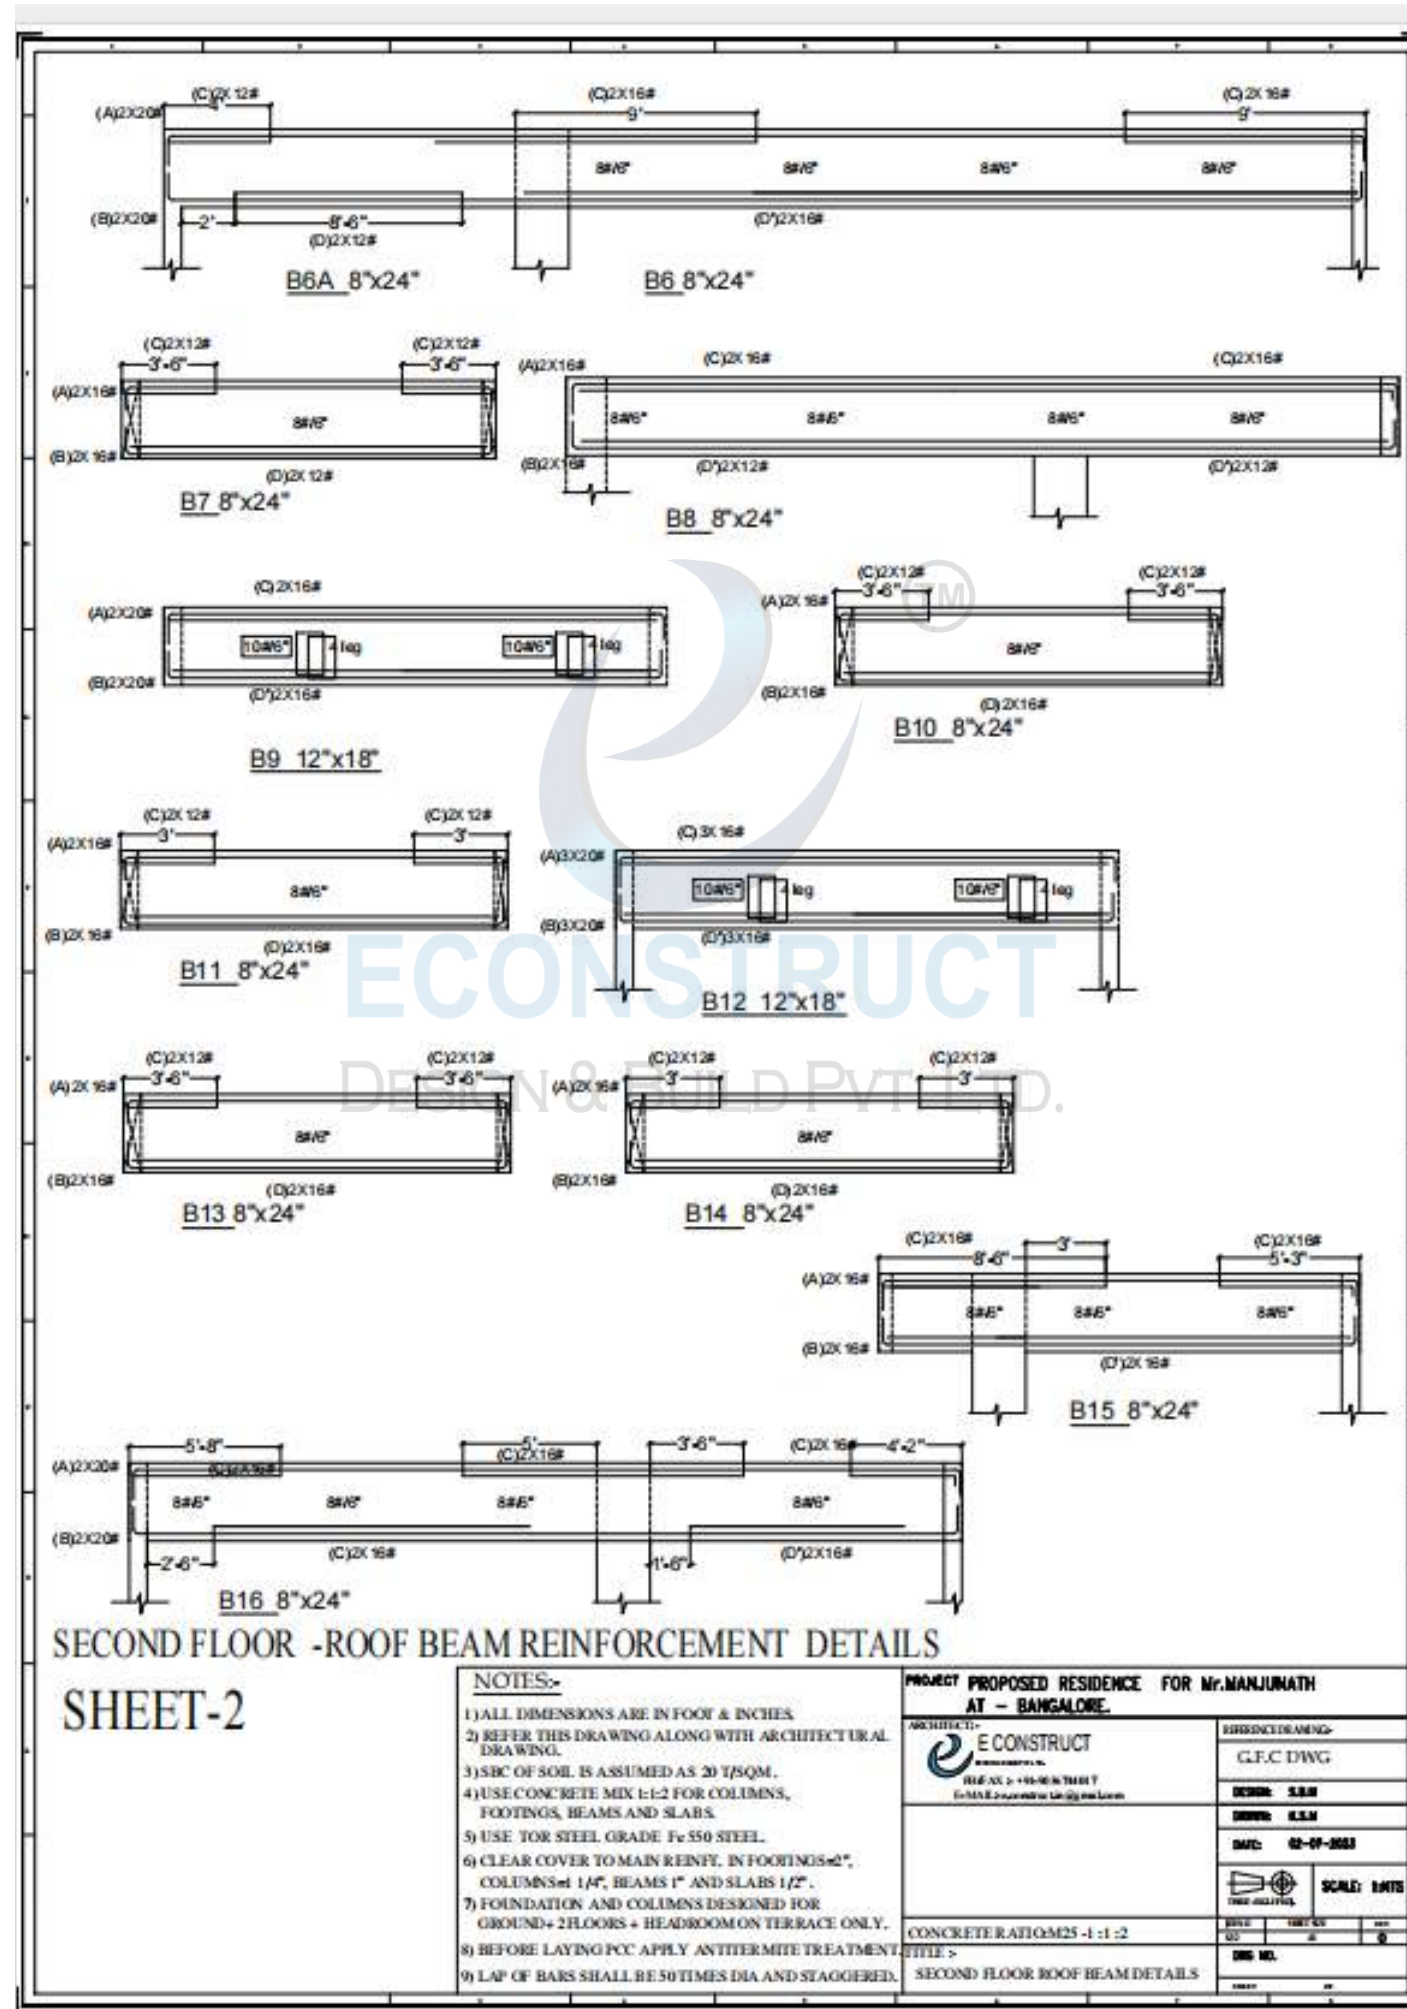


18


TERRACE FLOOR ROOF - SLAB REINFORCEMENT DETAILS

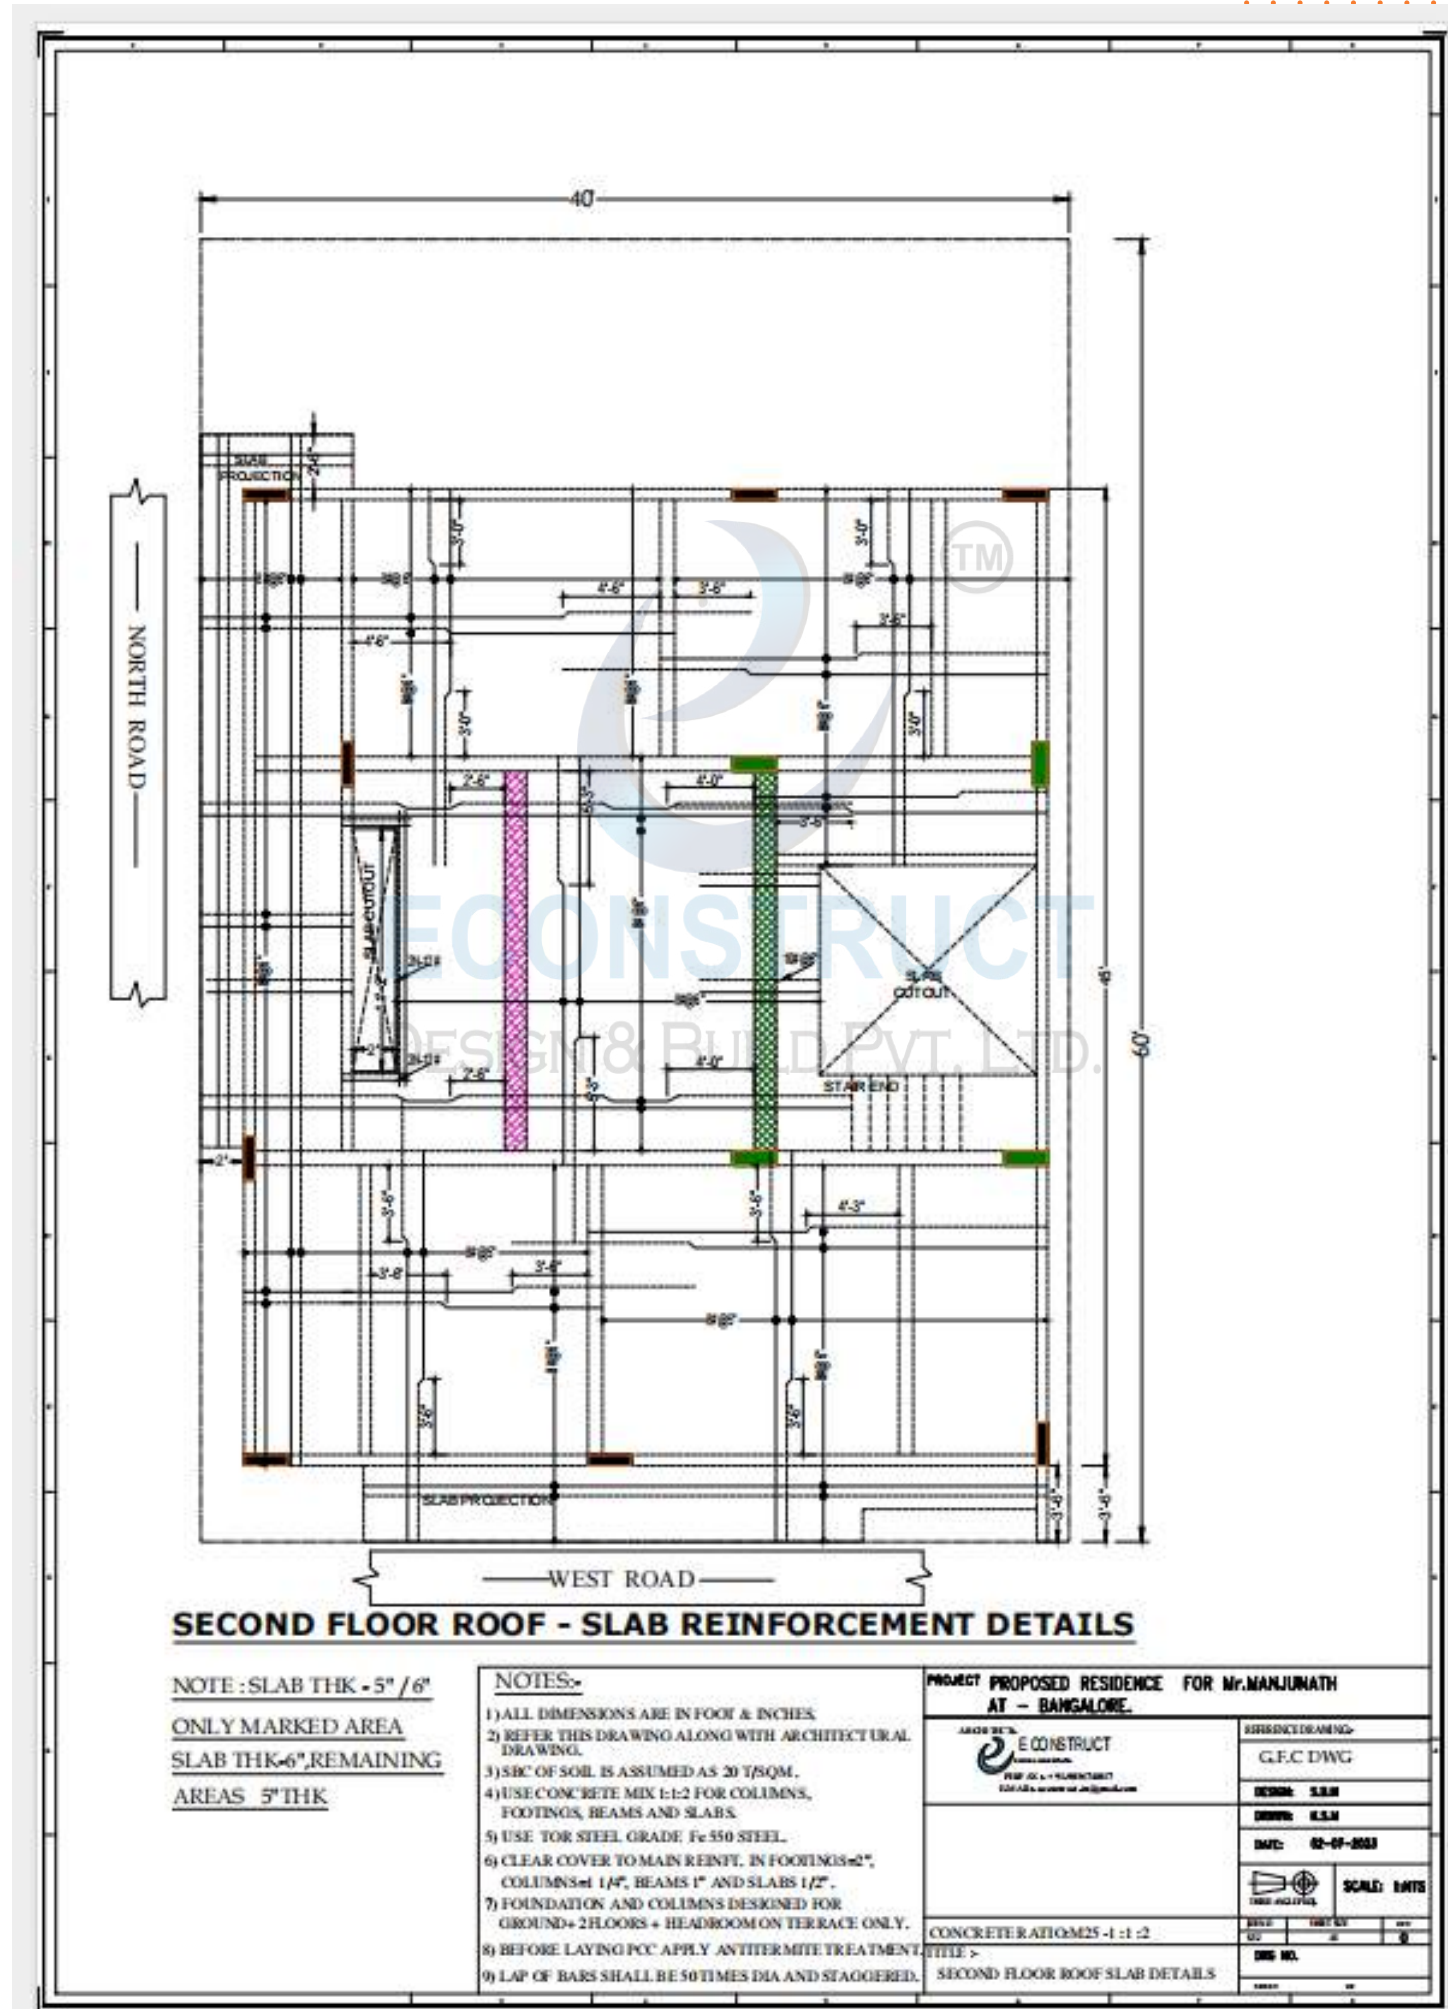

19

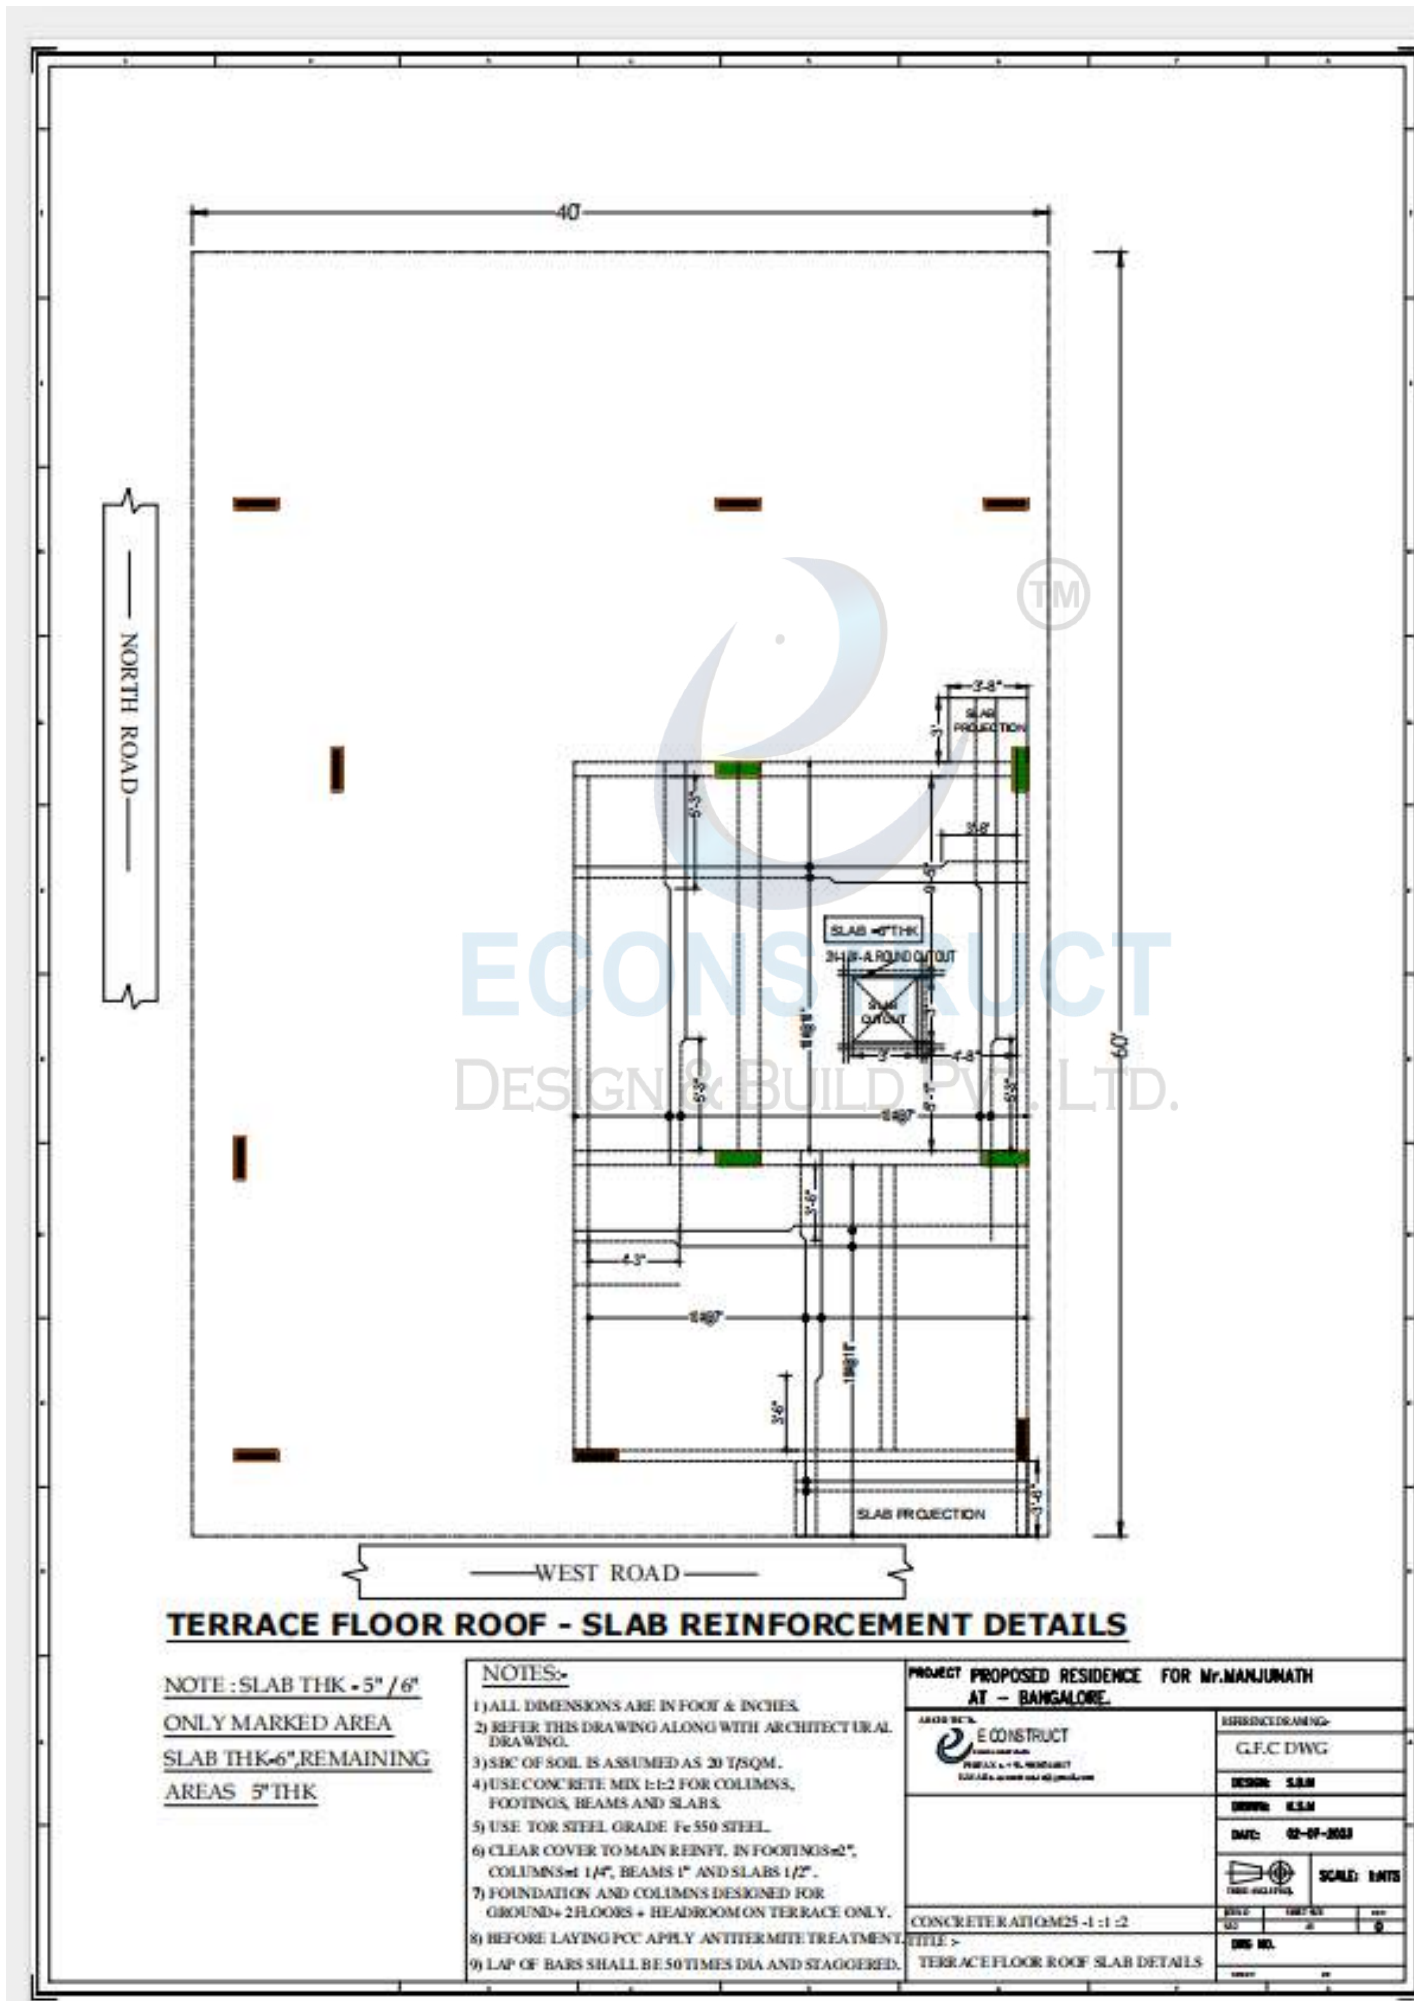
TERRACE FLOOR - ROOF BEAM
REINFORCEMENT DETAILS

20

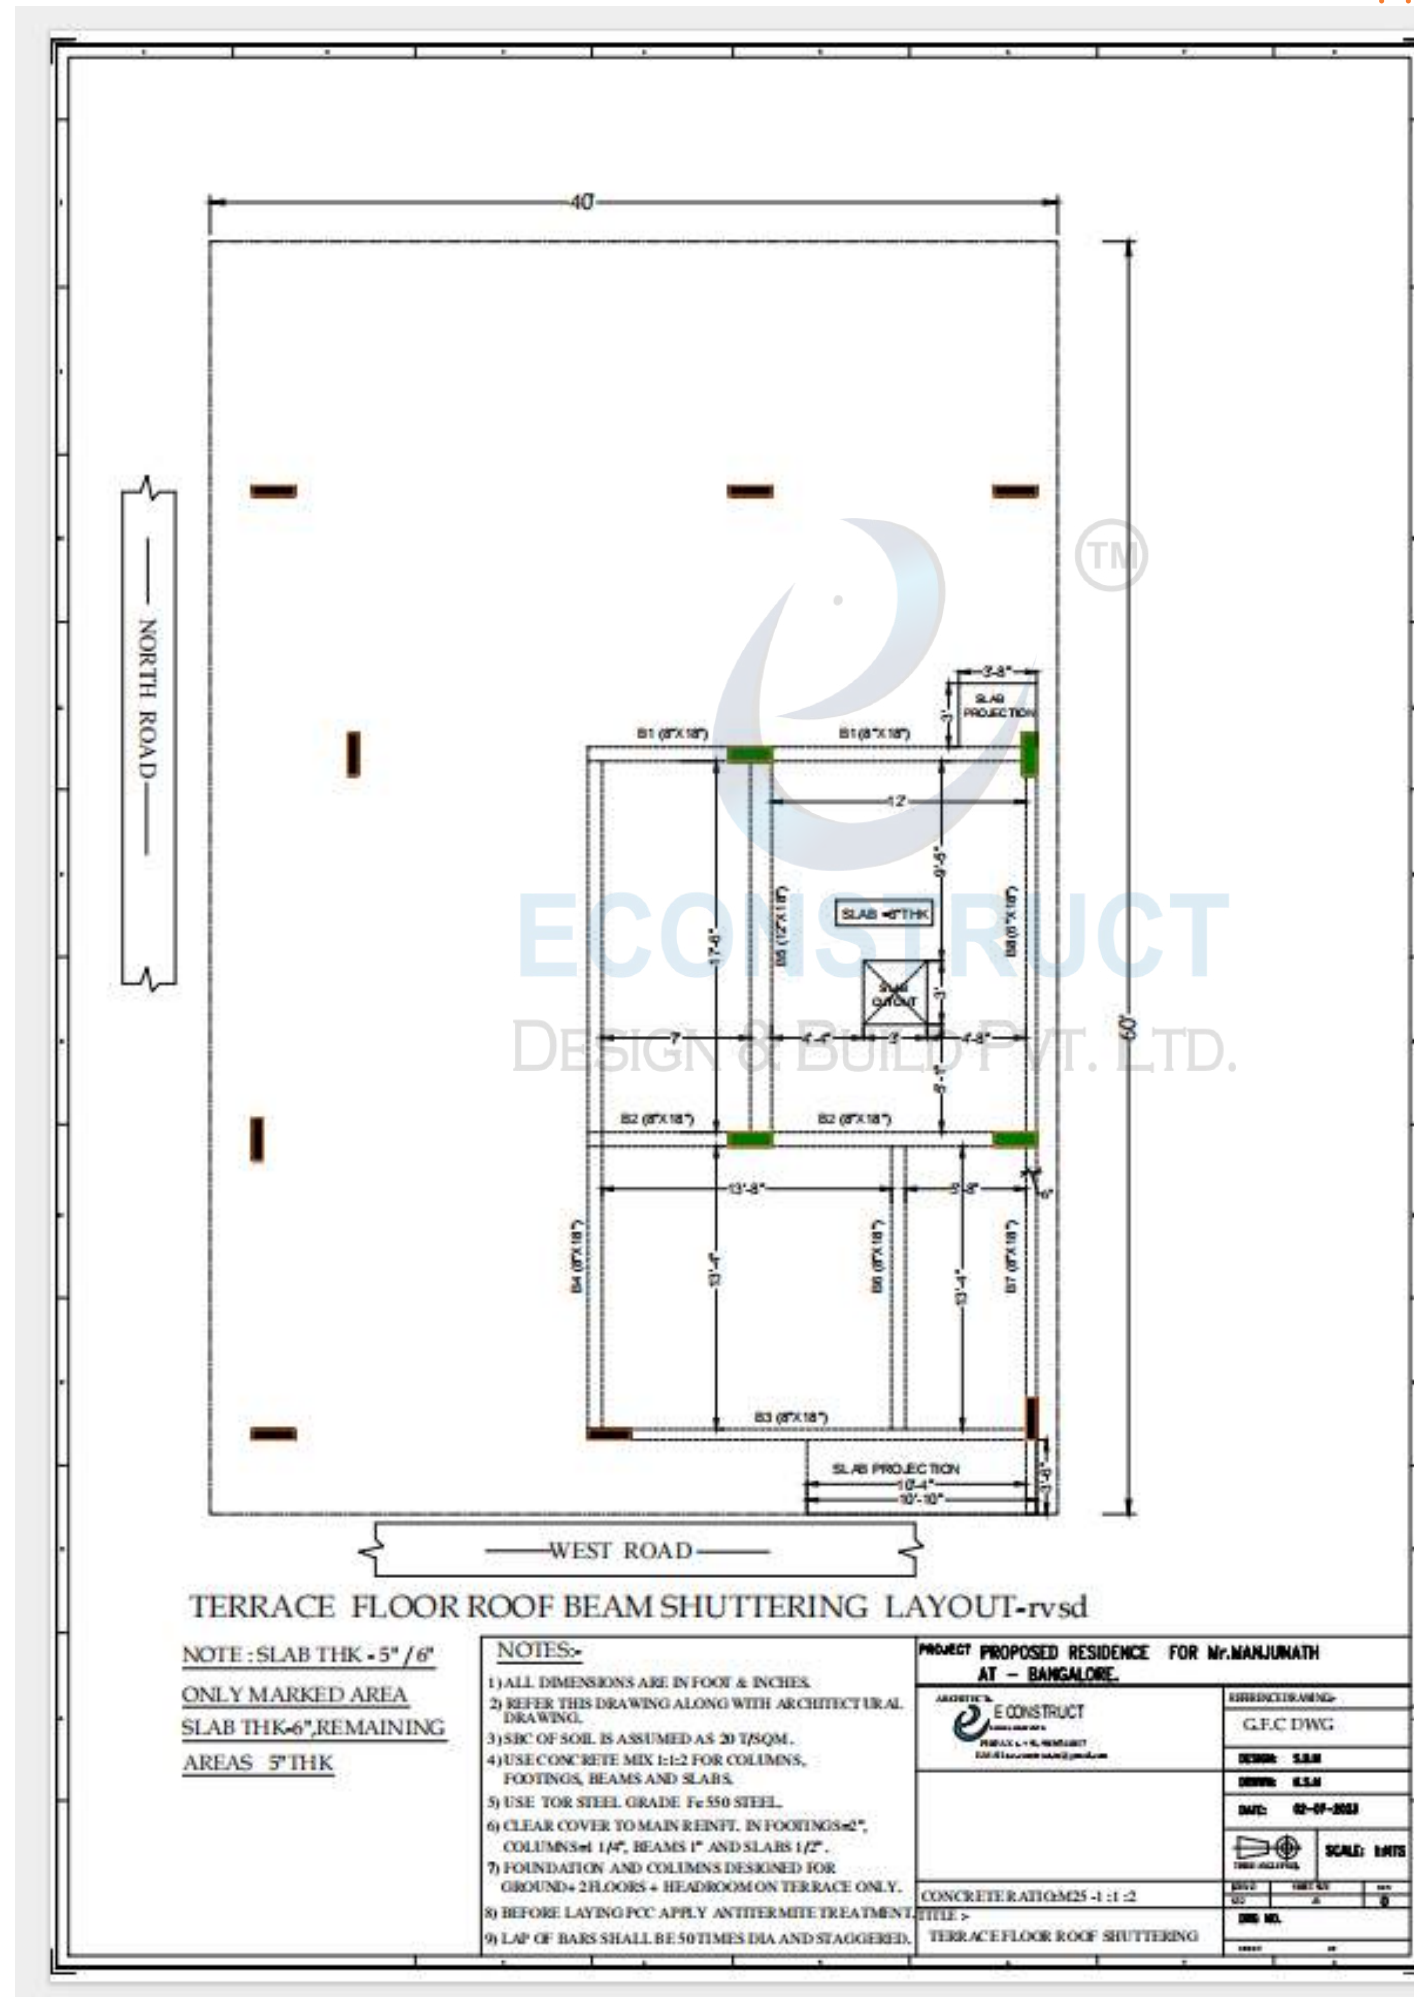TERRACE FLOOR ROOF BEAM
SHUTTERING LAYOUT-rv


Architectural Drawings Included

- Ground Floor Plan (37' x 45')
- First, Second & Terrace Floor Plans (Triplex Layout)
- Working Plans (Second & Terrace Floor)
- Doors & Windows Schedule
- Total Doors – 20 Nos
- Staircase Plans (External + Internal Duplex)
- Loft & Chajja Details (All Floors)
- Electrical Ceiling Layout (All Floors)
- Solar Water Provision for Toilets
- Kitchen & Utility Planning
- Compound Details
- Kitchen Detailed Plan
- Bedroom Wardrobe Designs (5 Types)

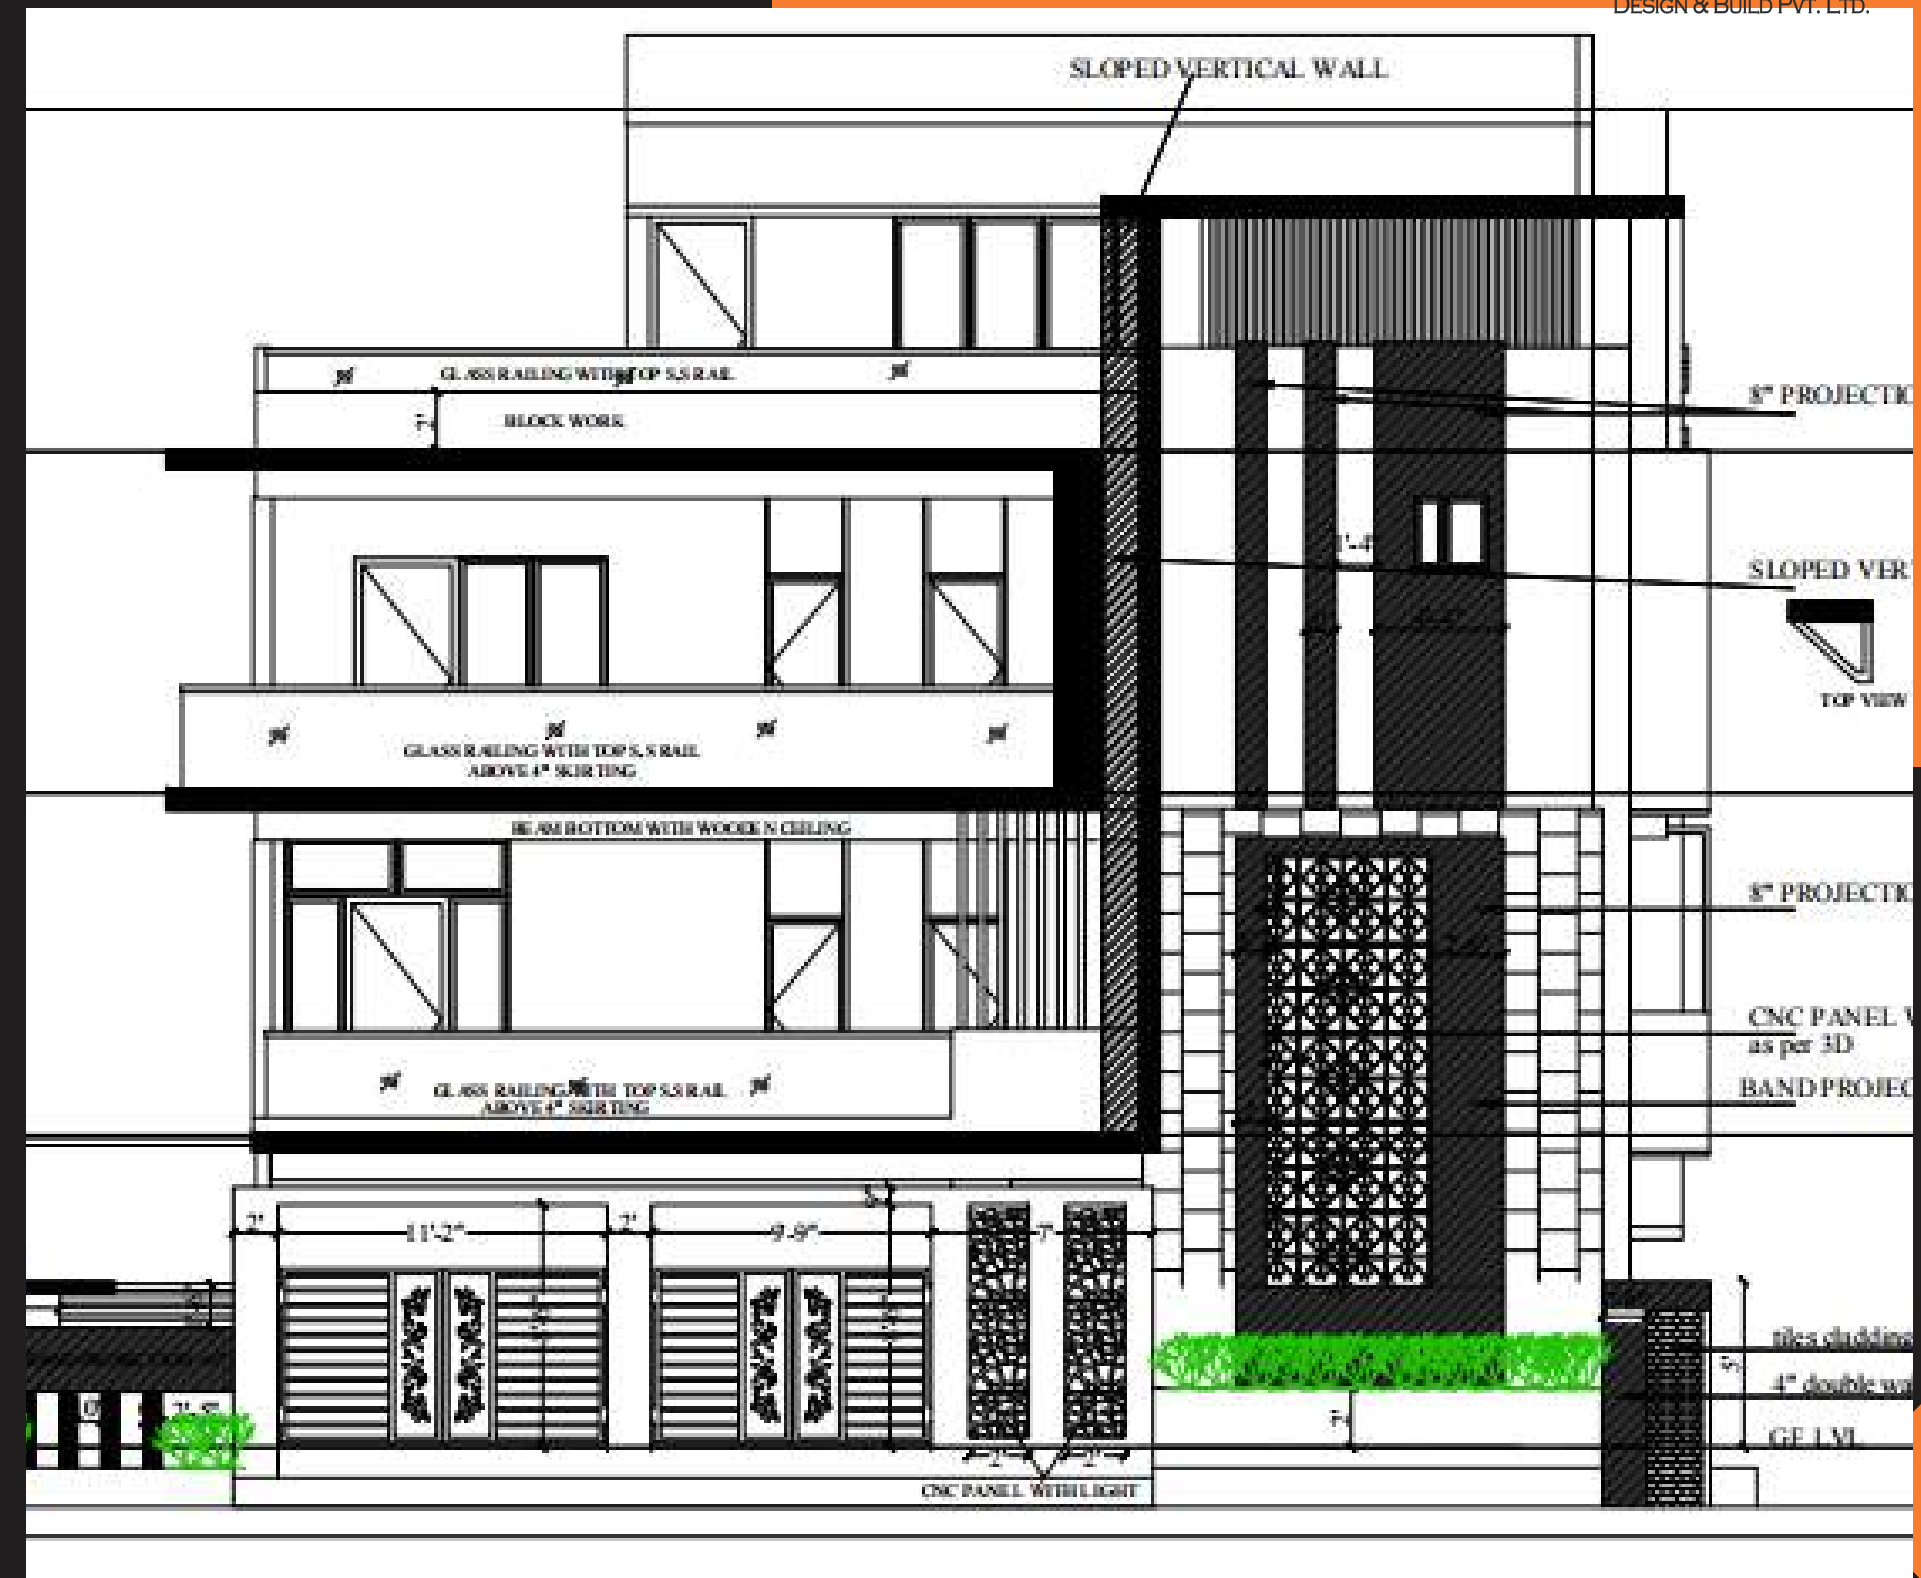


01

GROUND FLOOR PLAN
BUILDING SIZE (37' X 45')

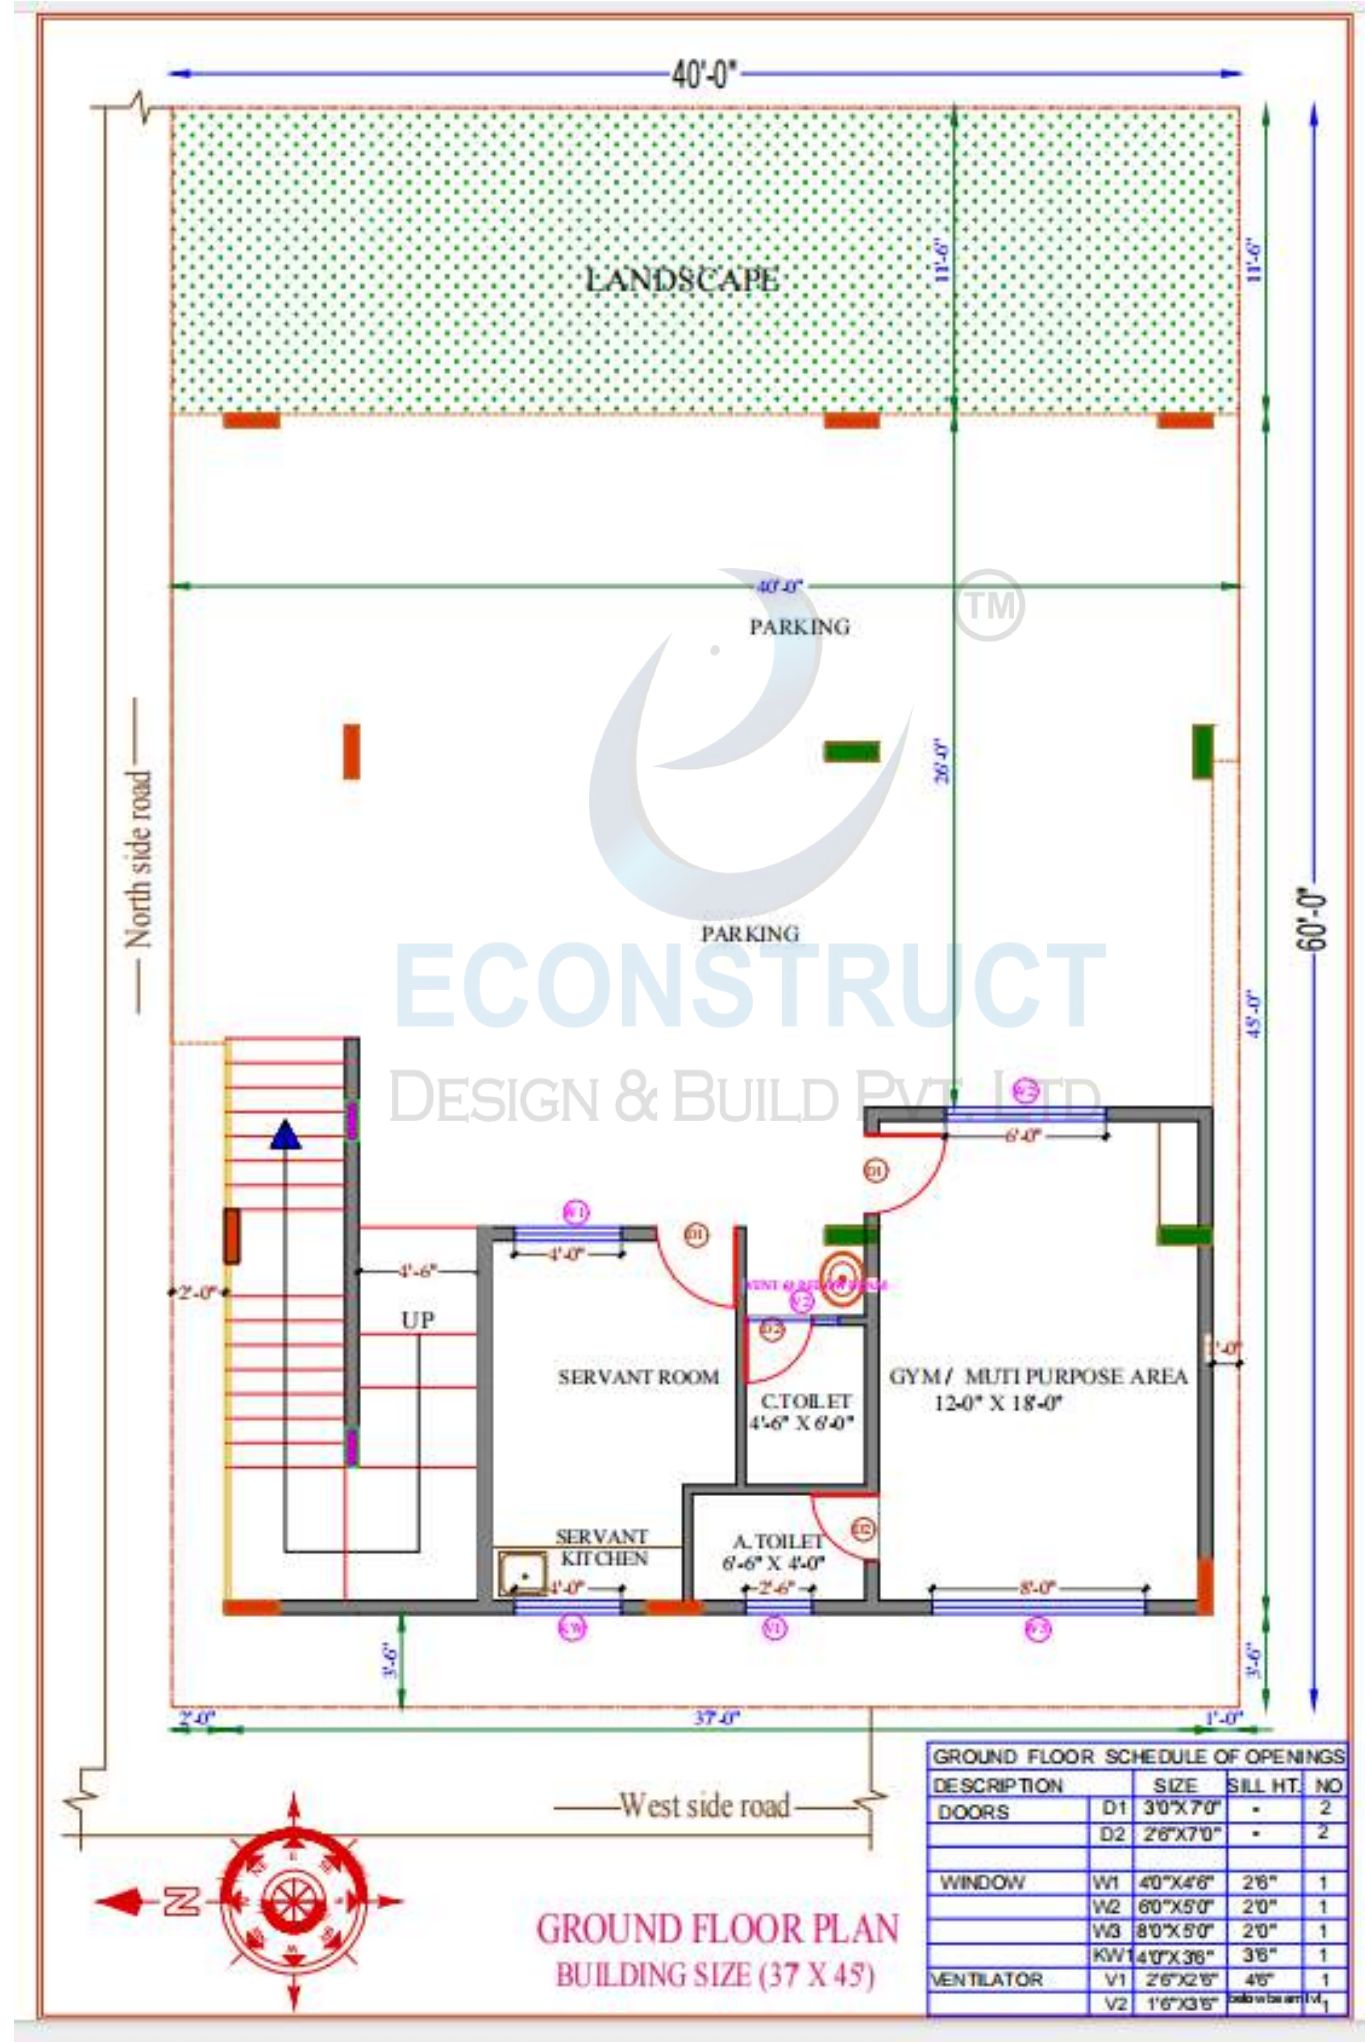


02

FIRST FLOOR PLAN - DUPLEX
HOUSE BUILDING SIZE (37' X 45')

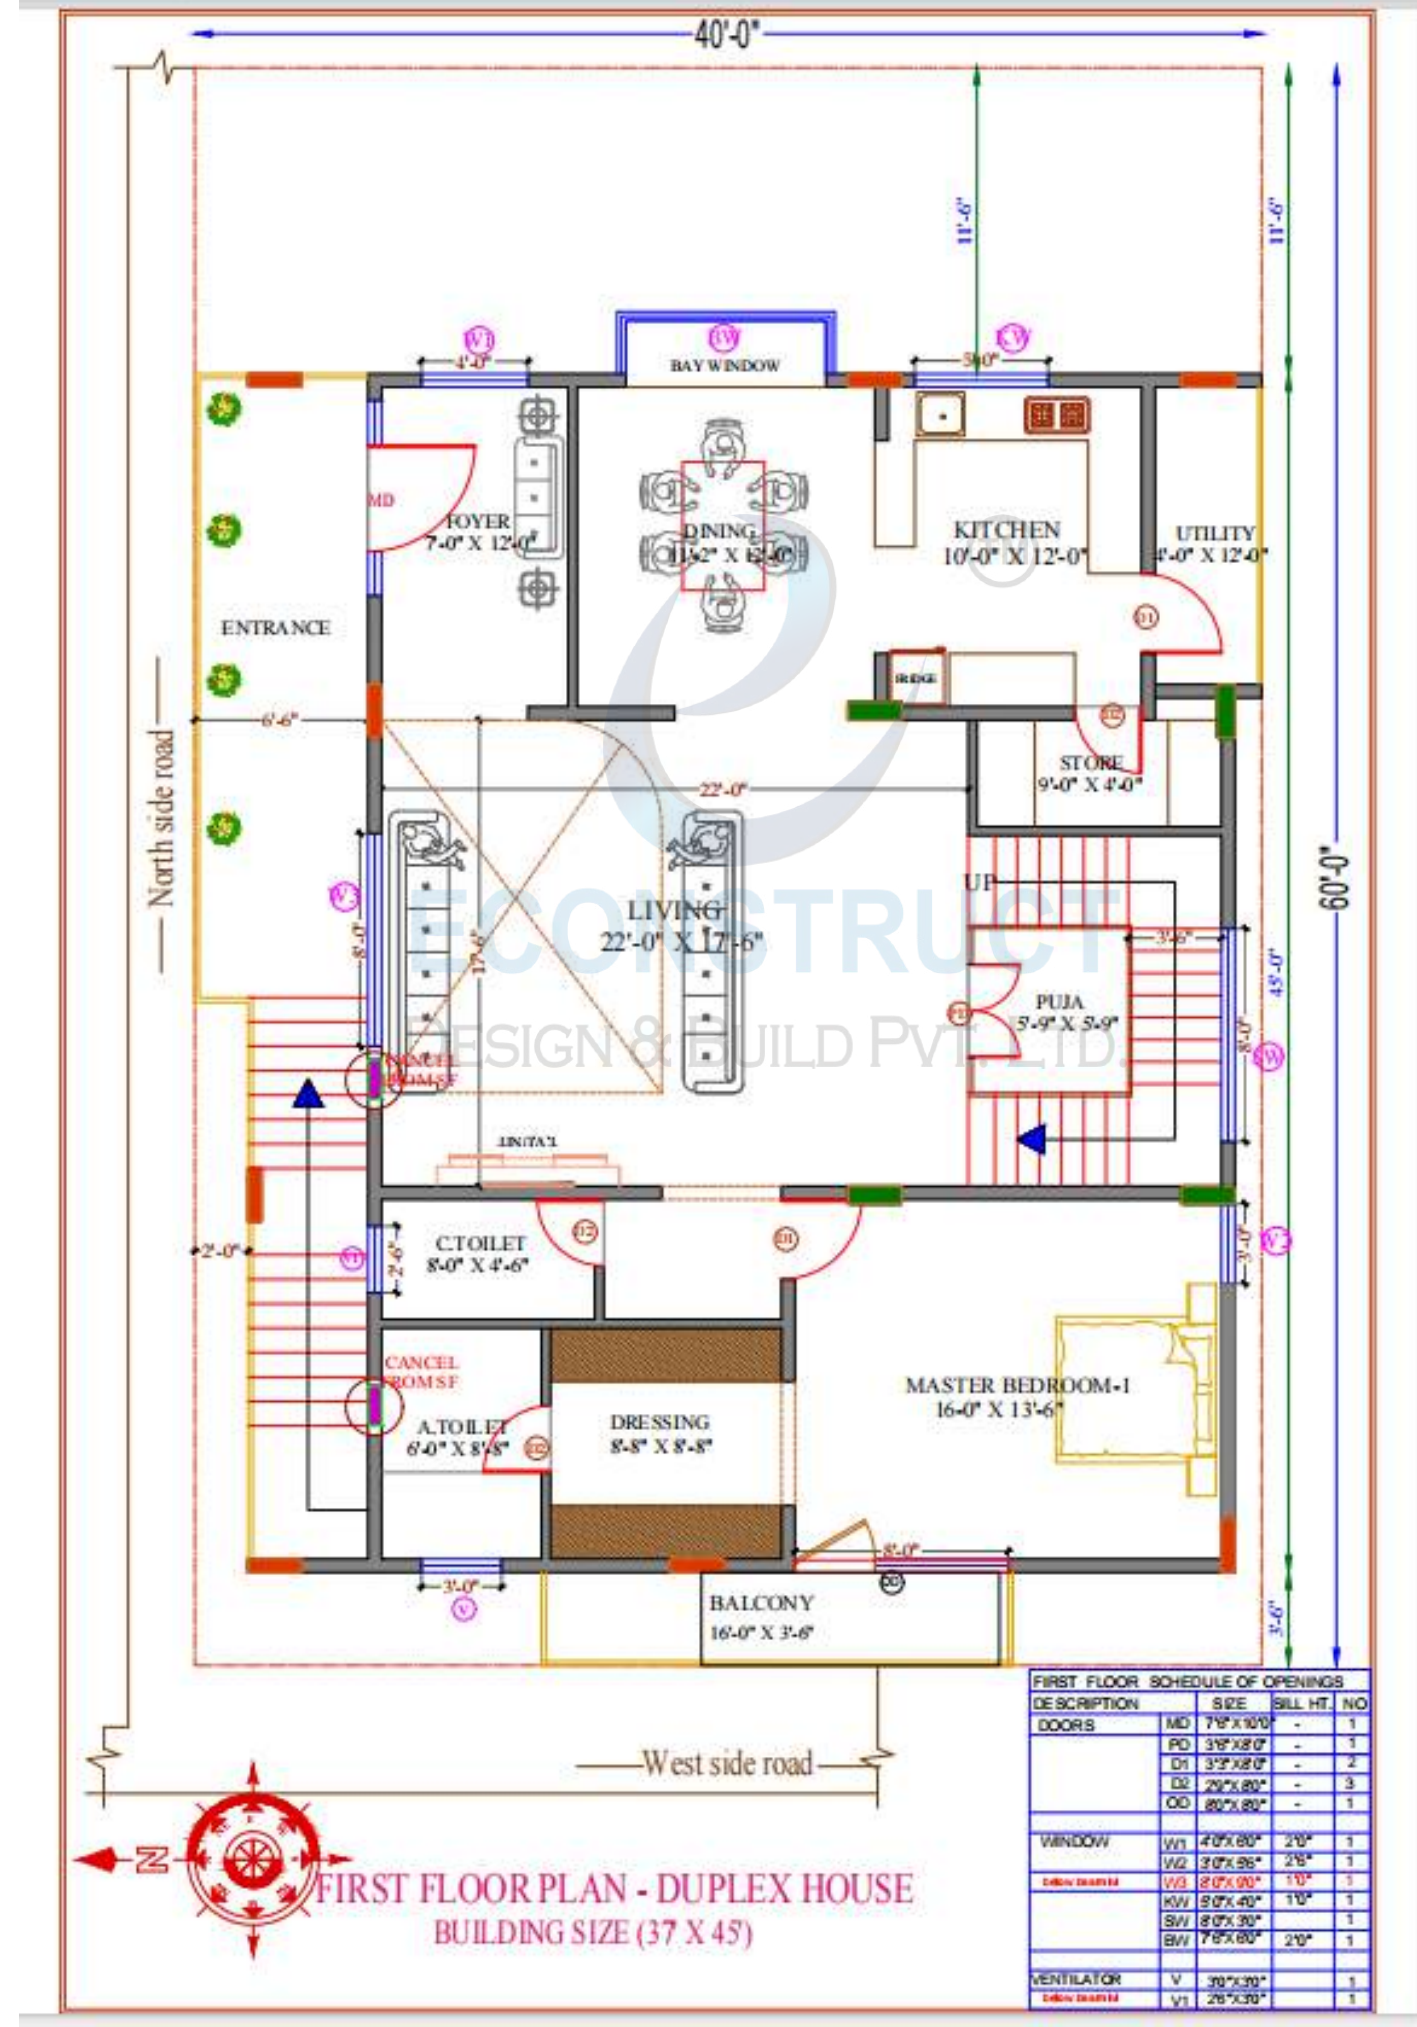


03

SECOND FLOOR PLAN - DUPLEX HOUSE BUILDING SIZE (37' X 45')

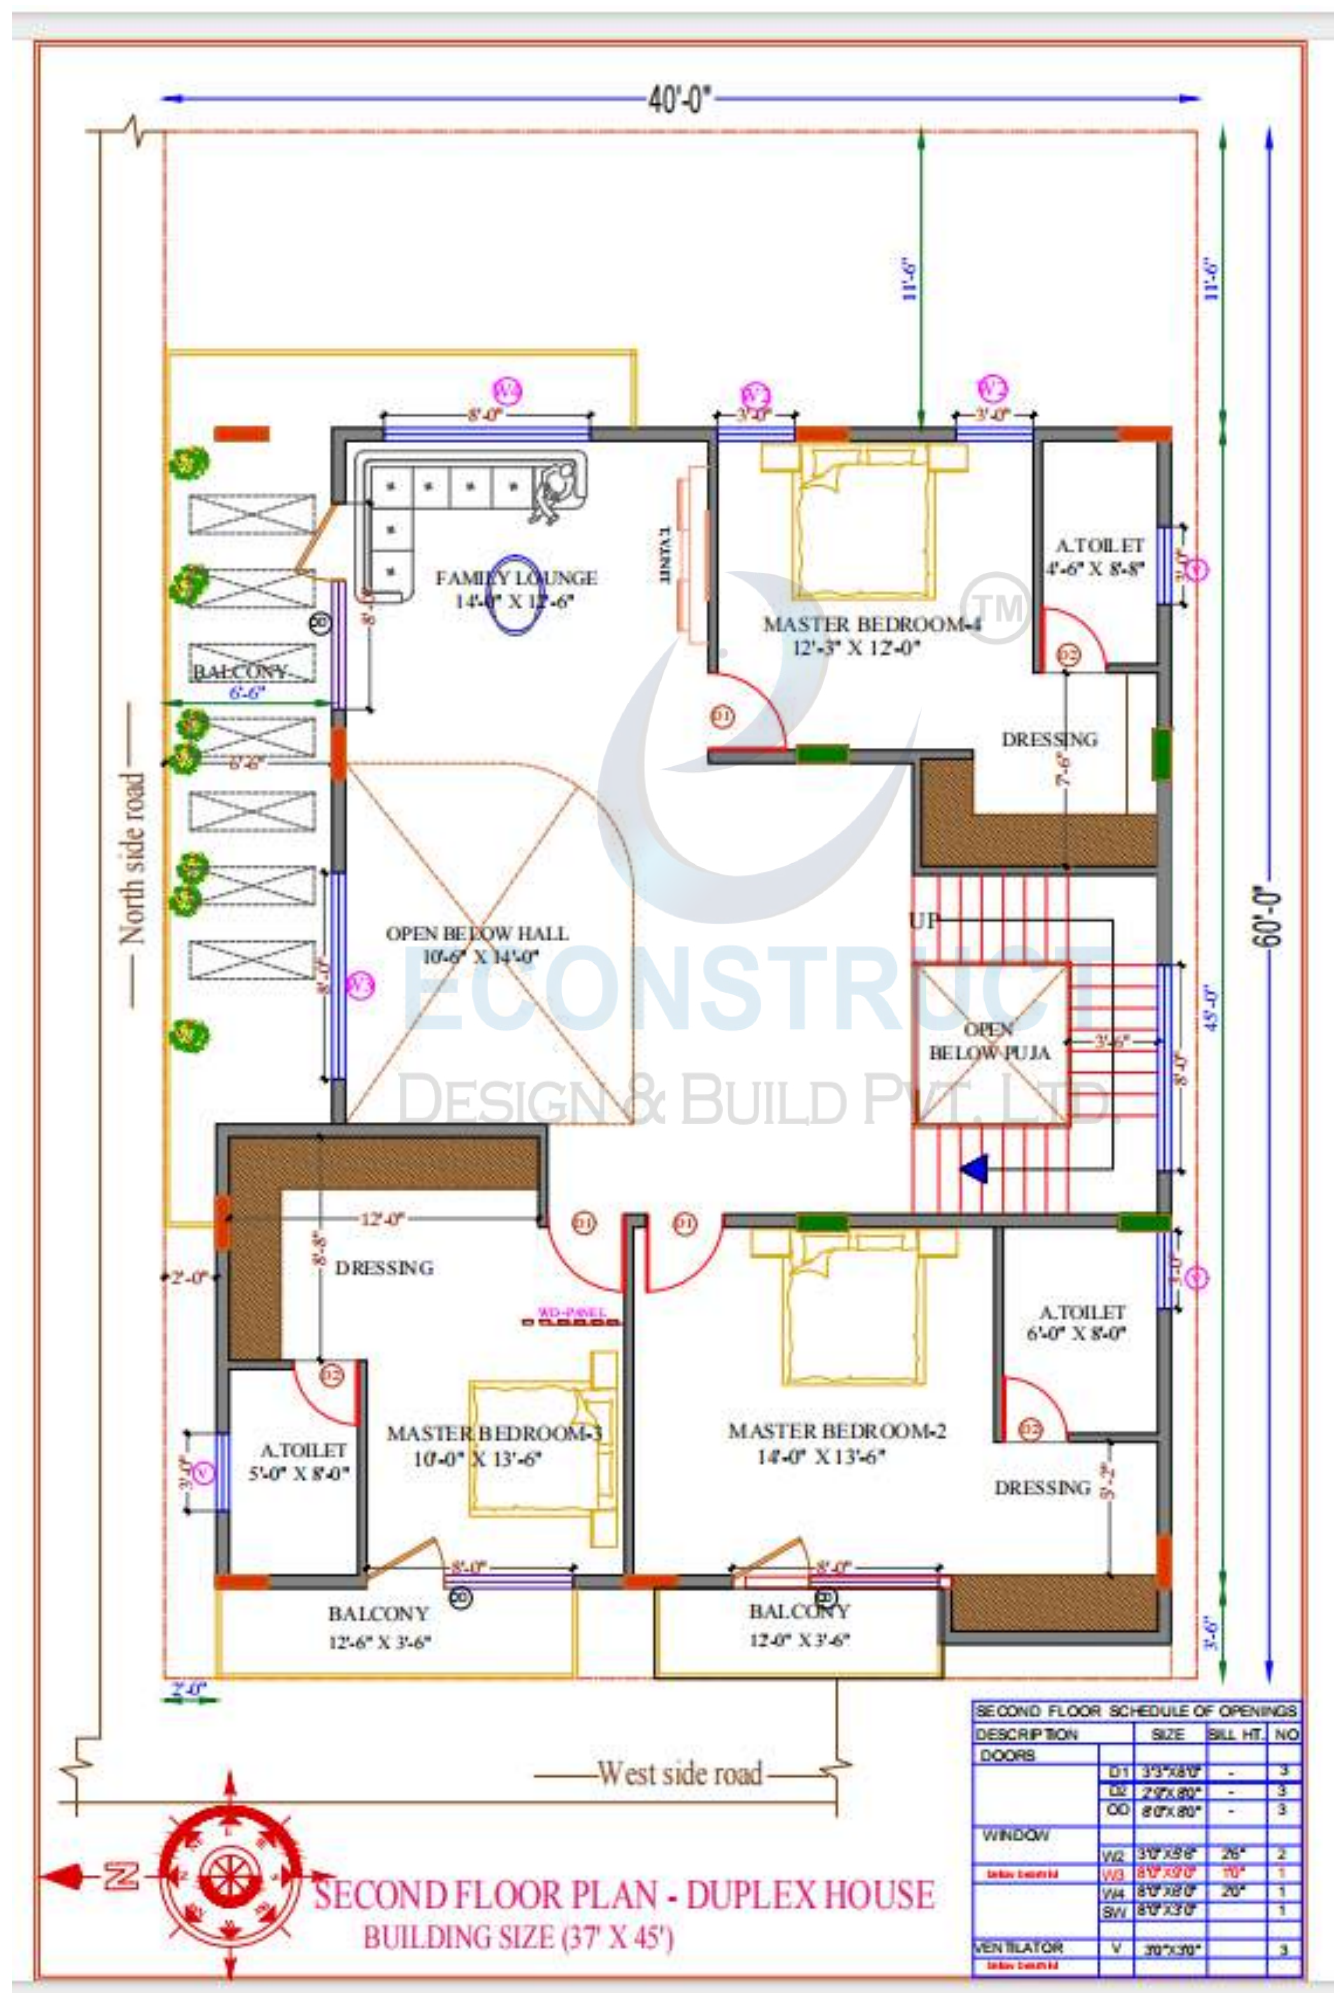


04

TERRACE FLOOR PLAN - DUPLEX HOUSE BUILDING SIZE (37' X 45')

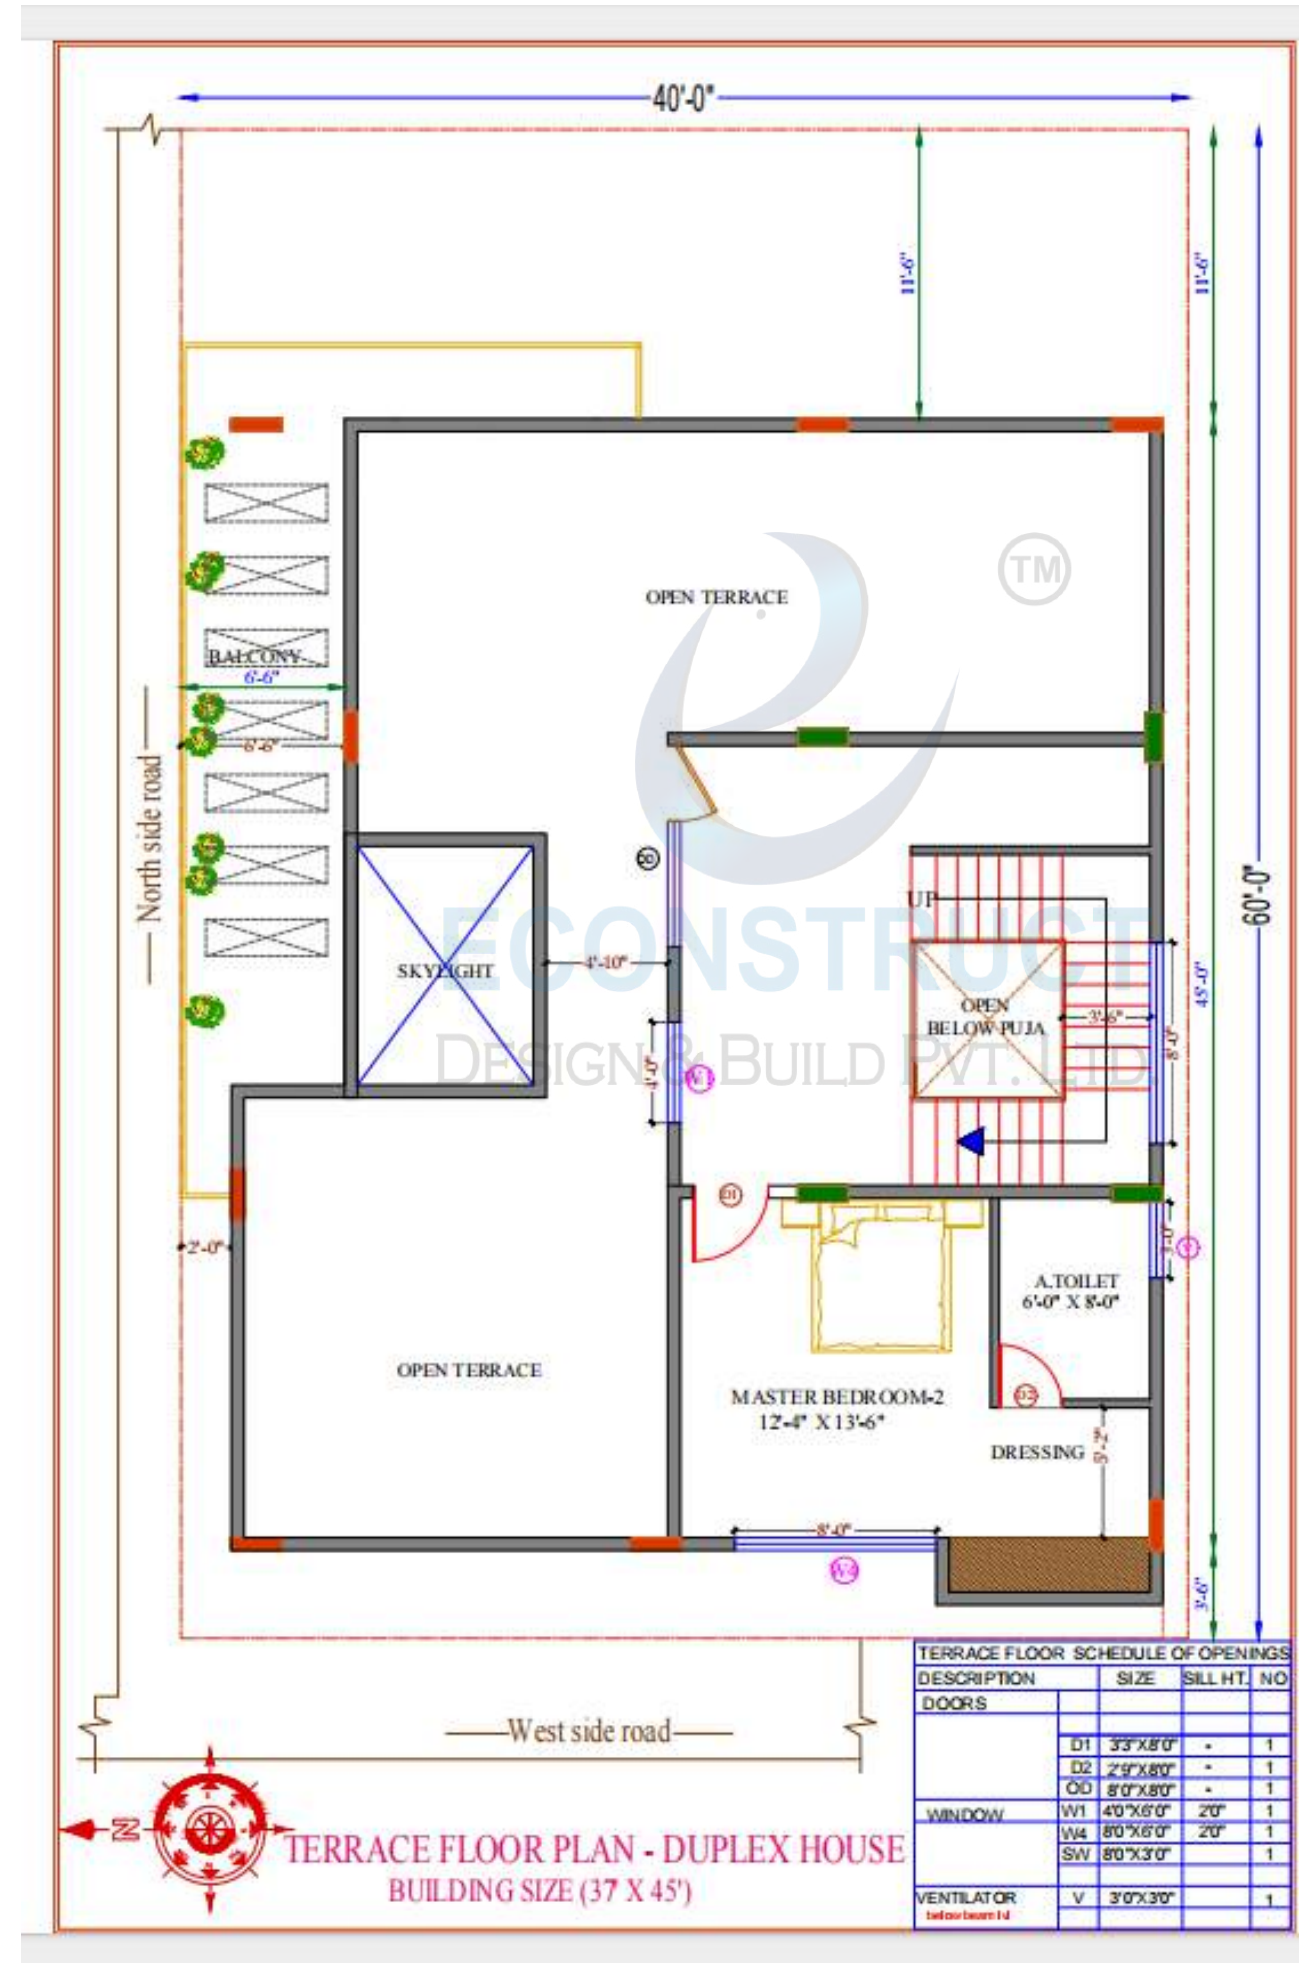


05

SECOND FLOOR WORKING PLAN

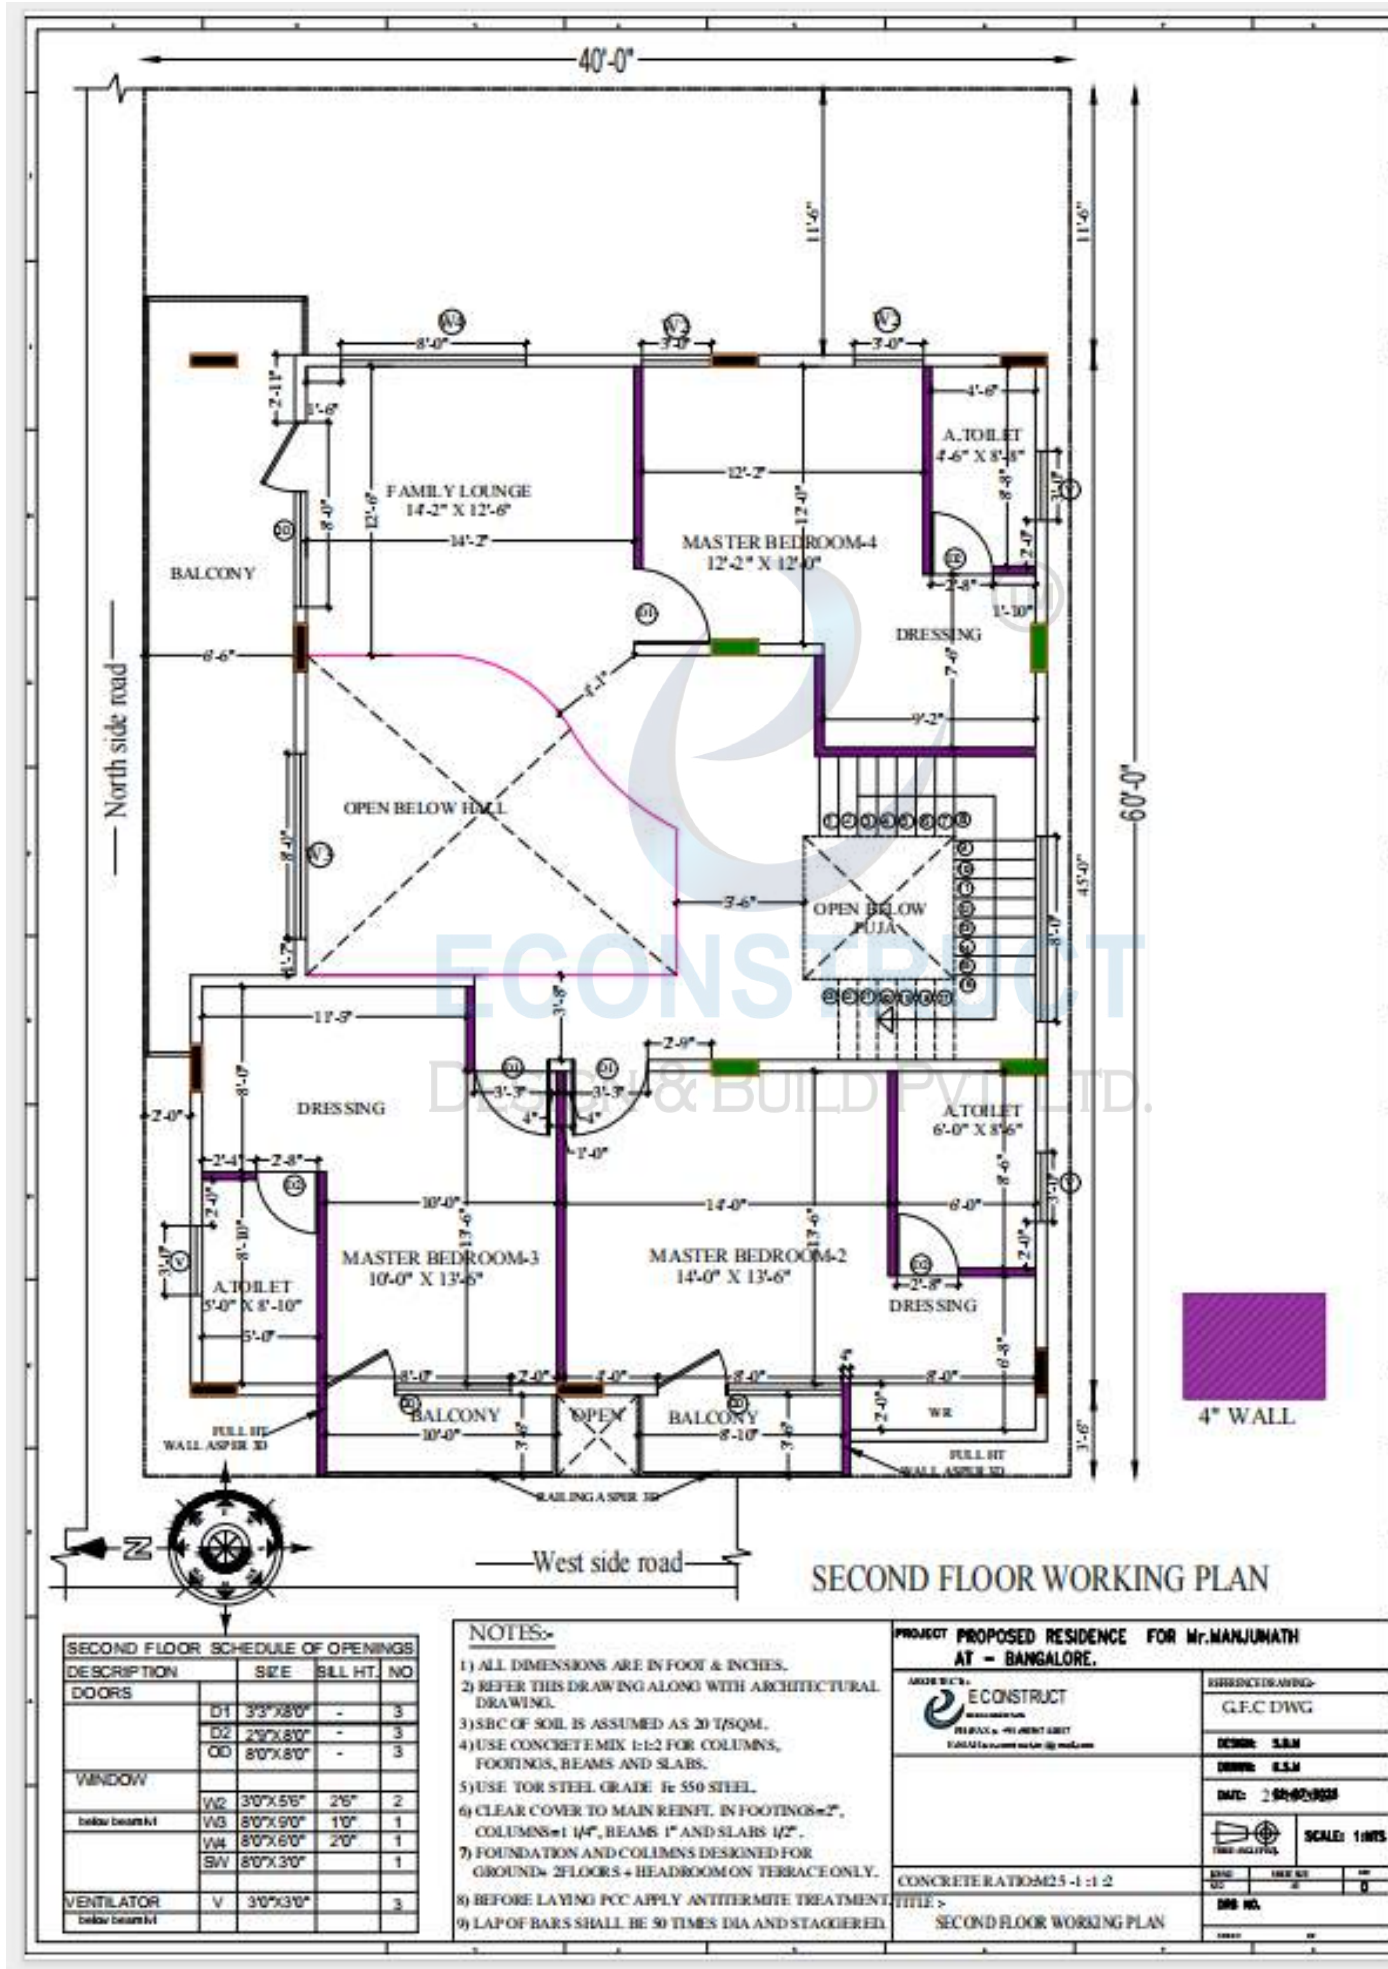


06

TERRACE FLOOR WORKING PLAN

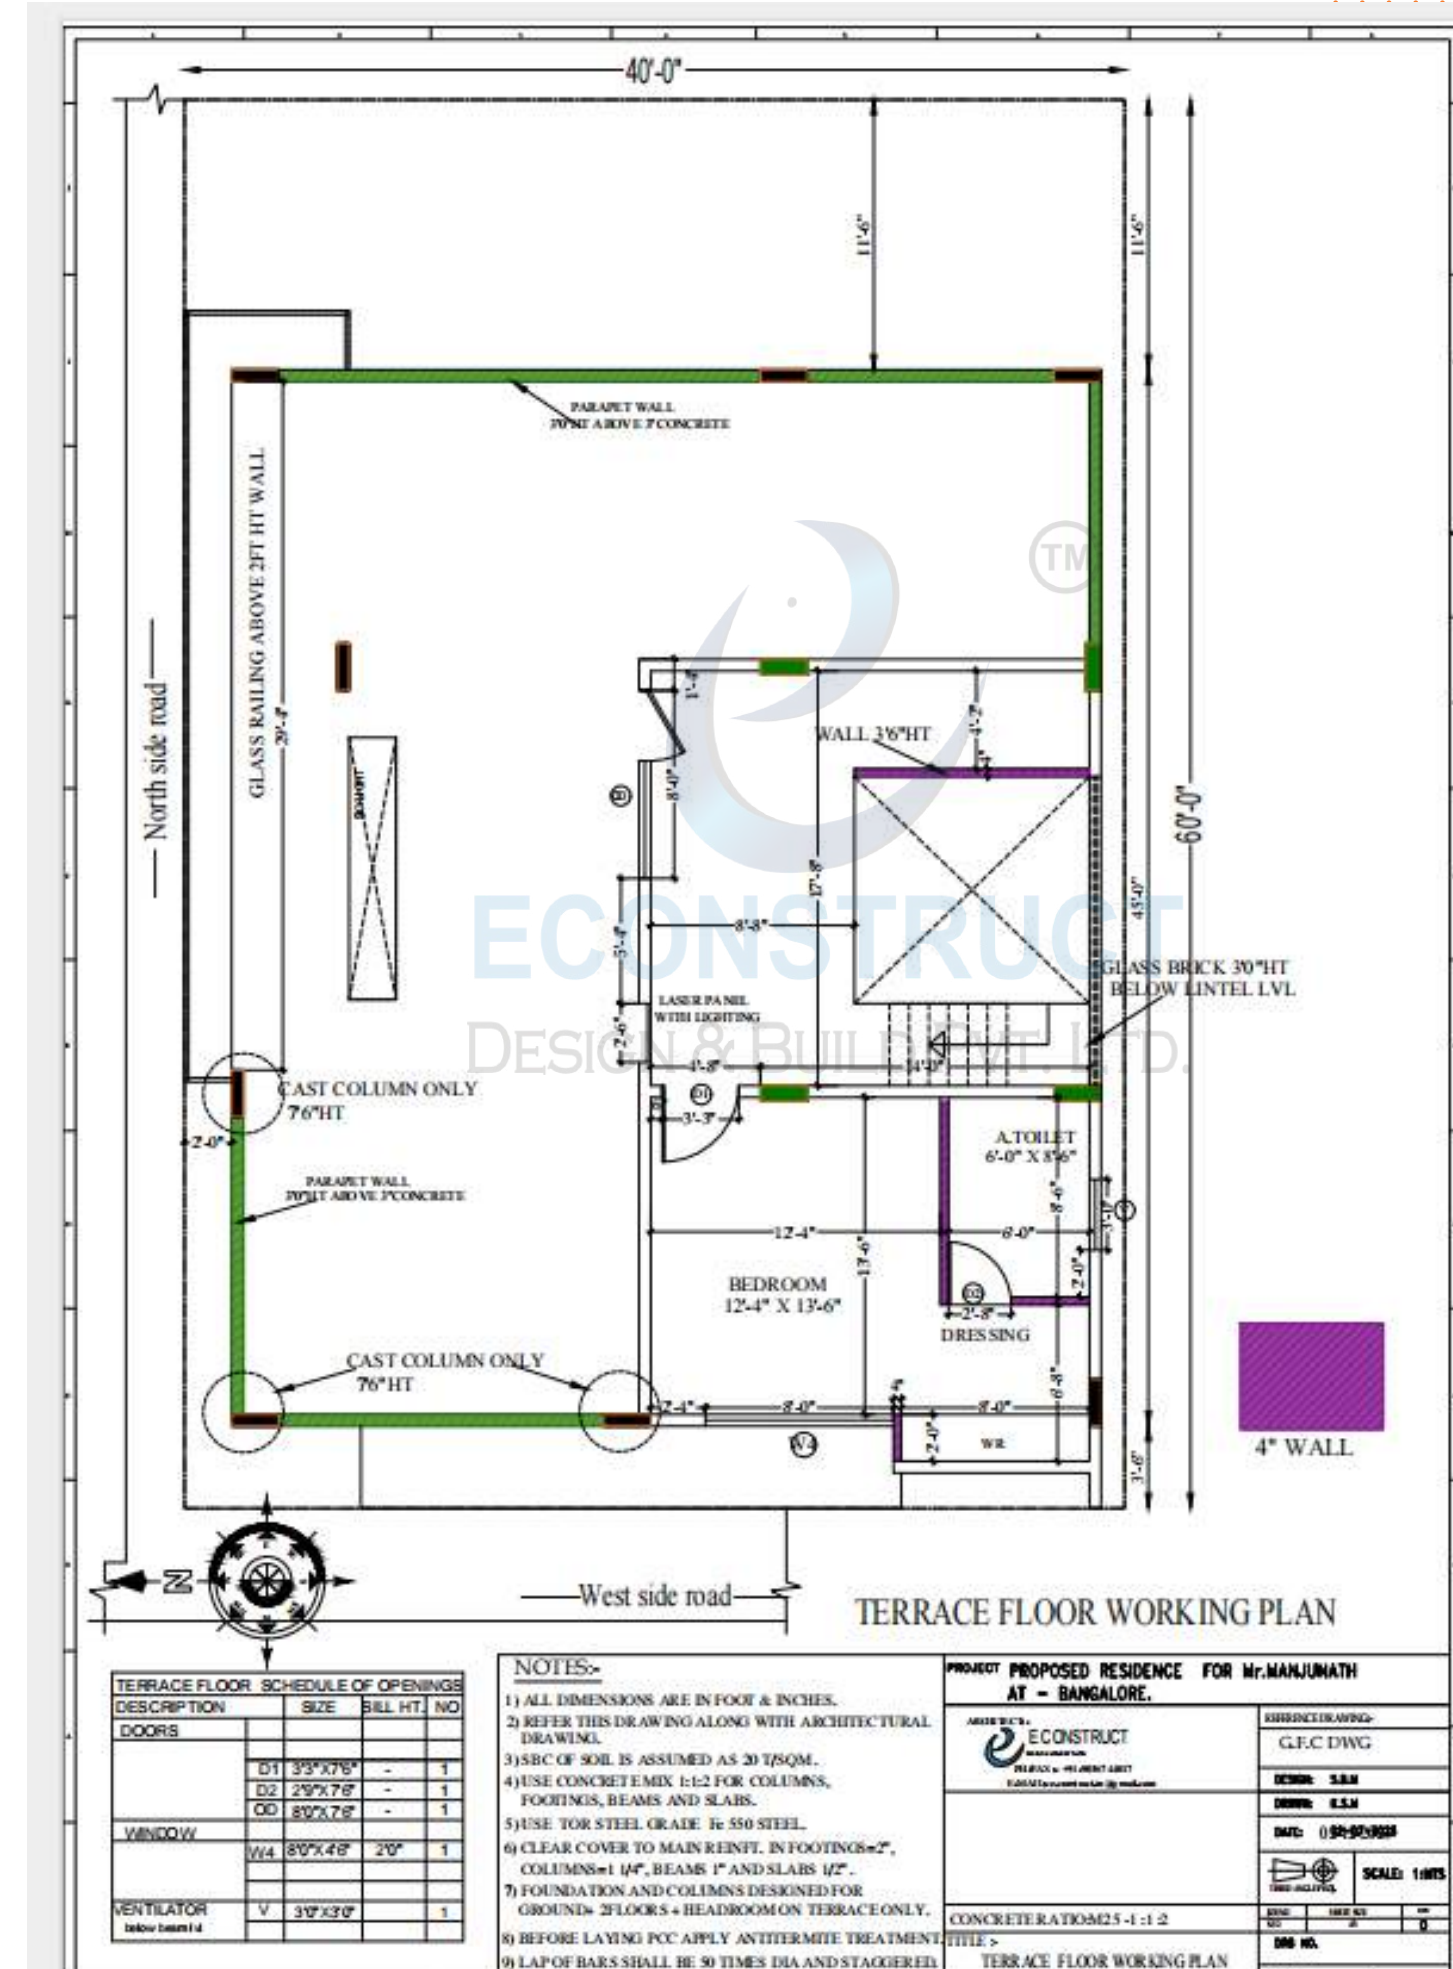


07

GROUND FLOOR - DOORS & WINDOWS, OPENING SCHEDULE

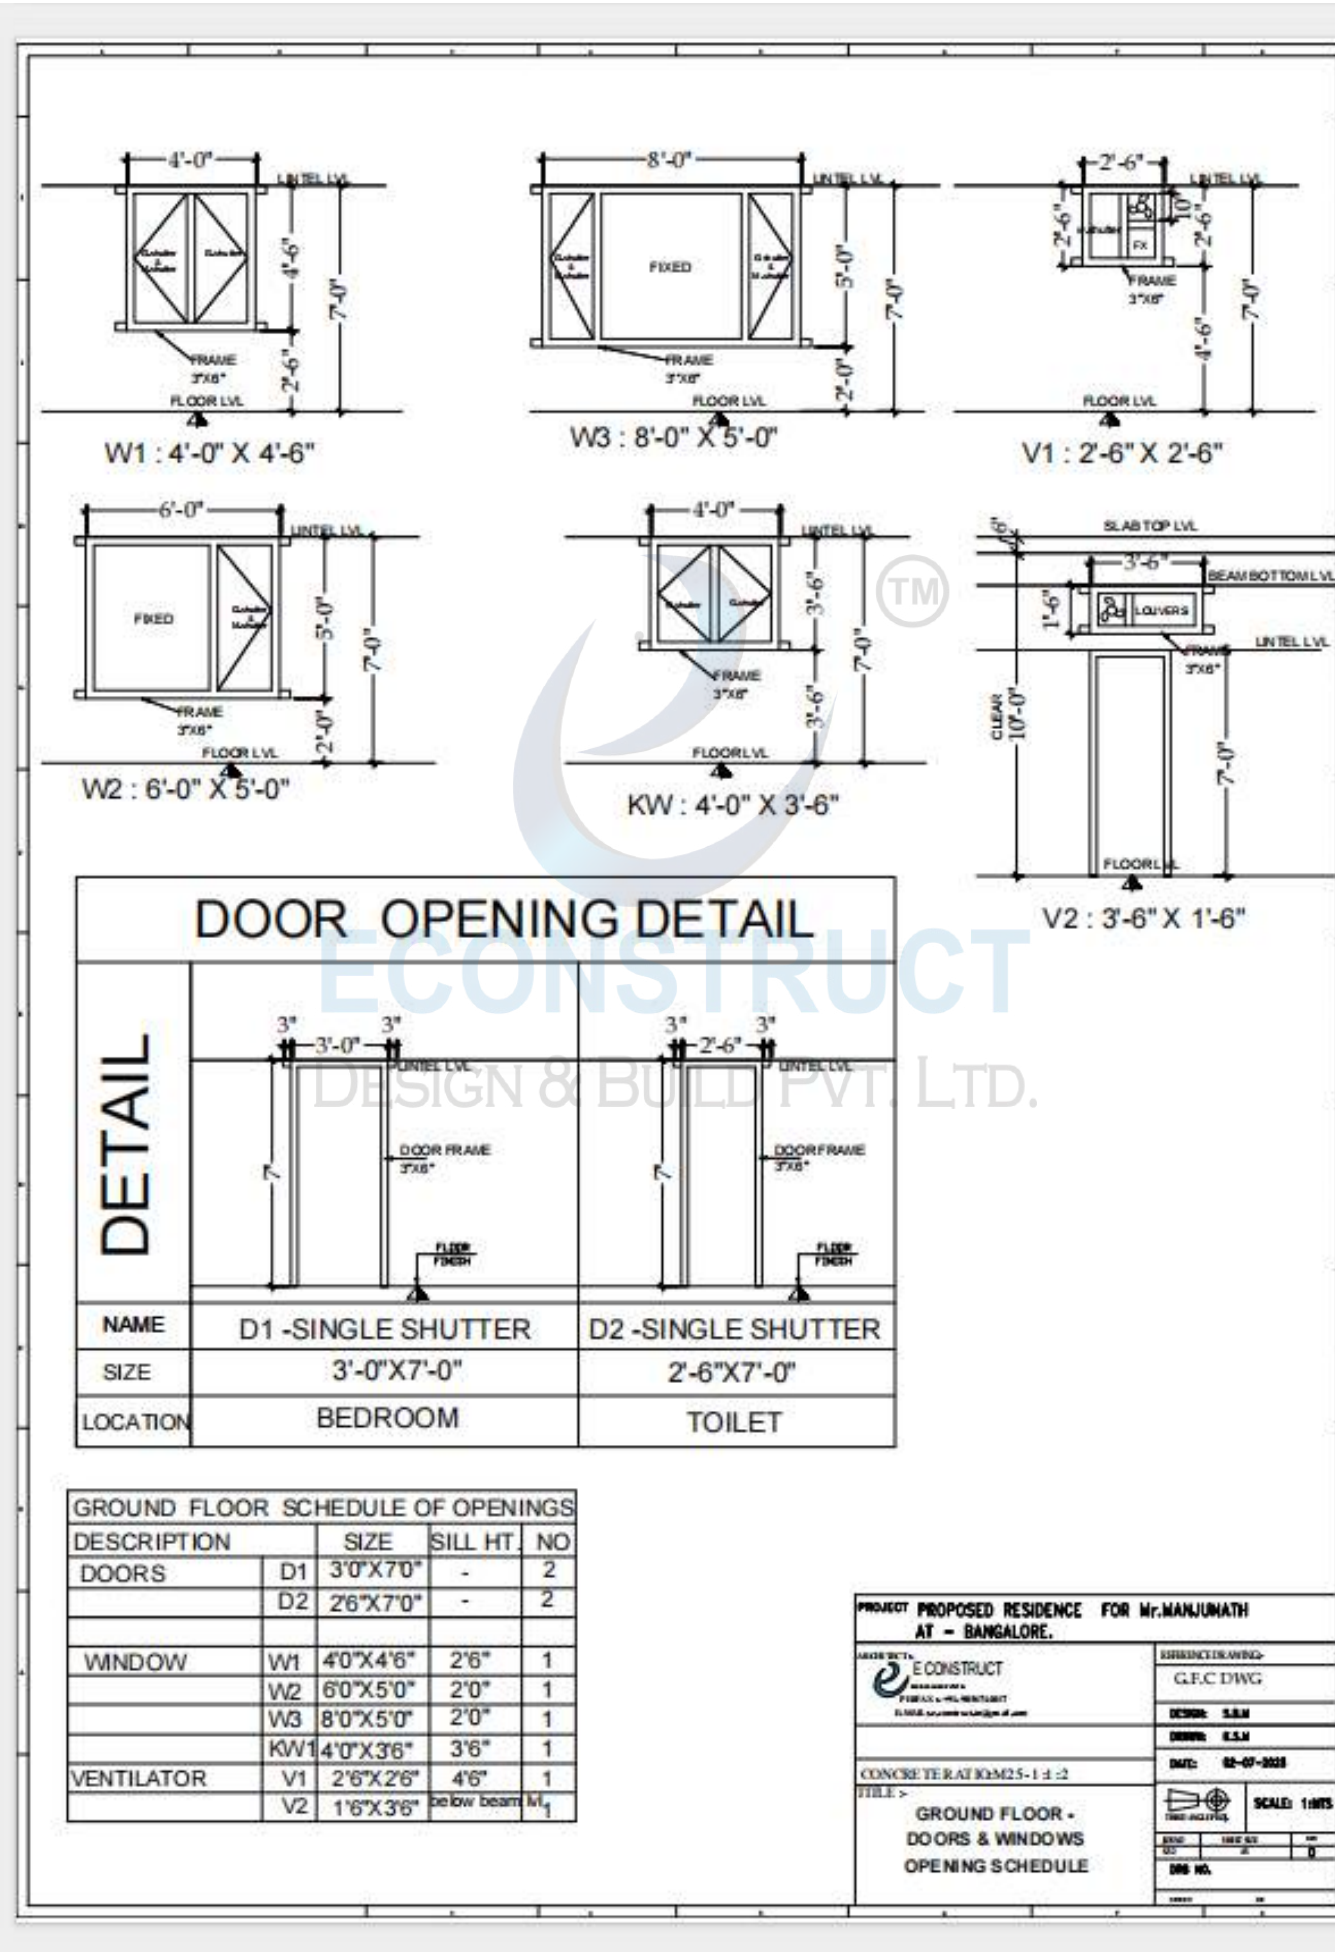


08

DUPLEX HOUSE - WINDOWS, OPENING SCHEDULE, FIRST, SECOND, THIRD FLOOR

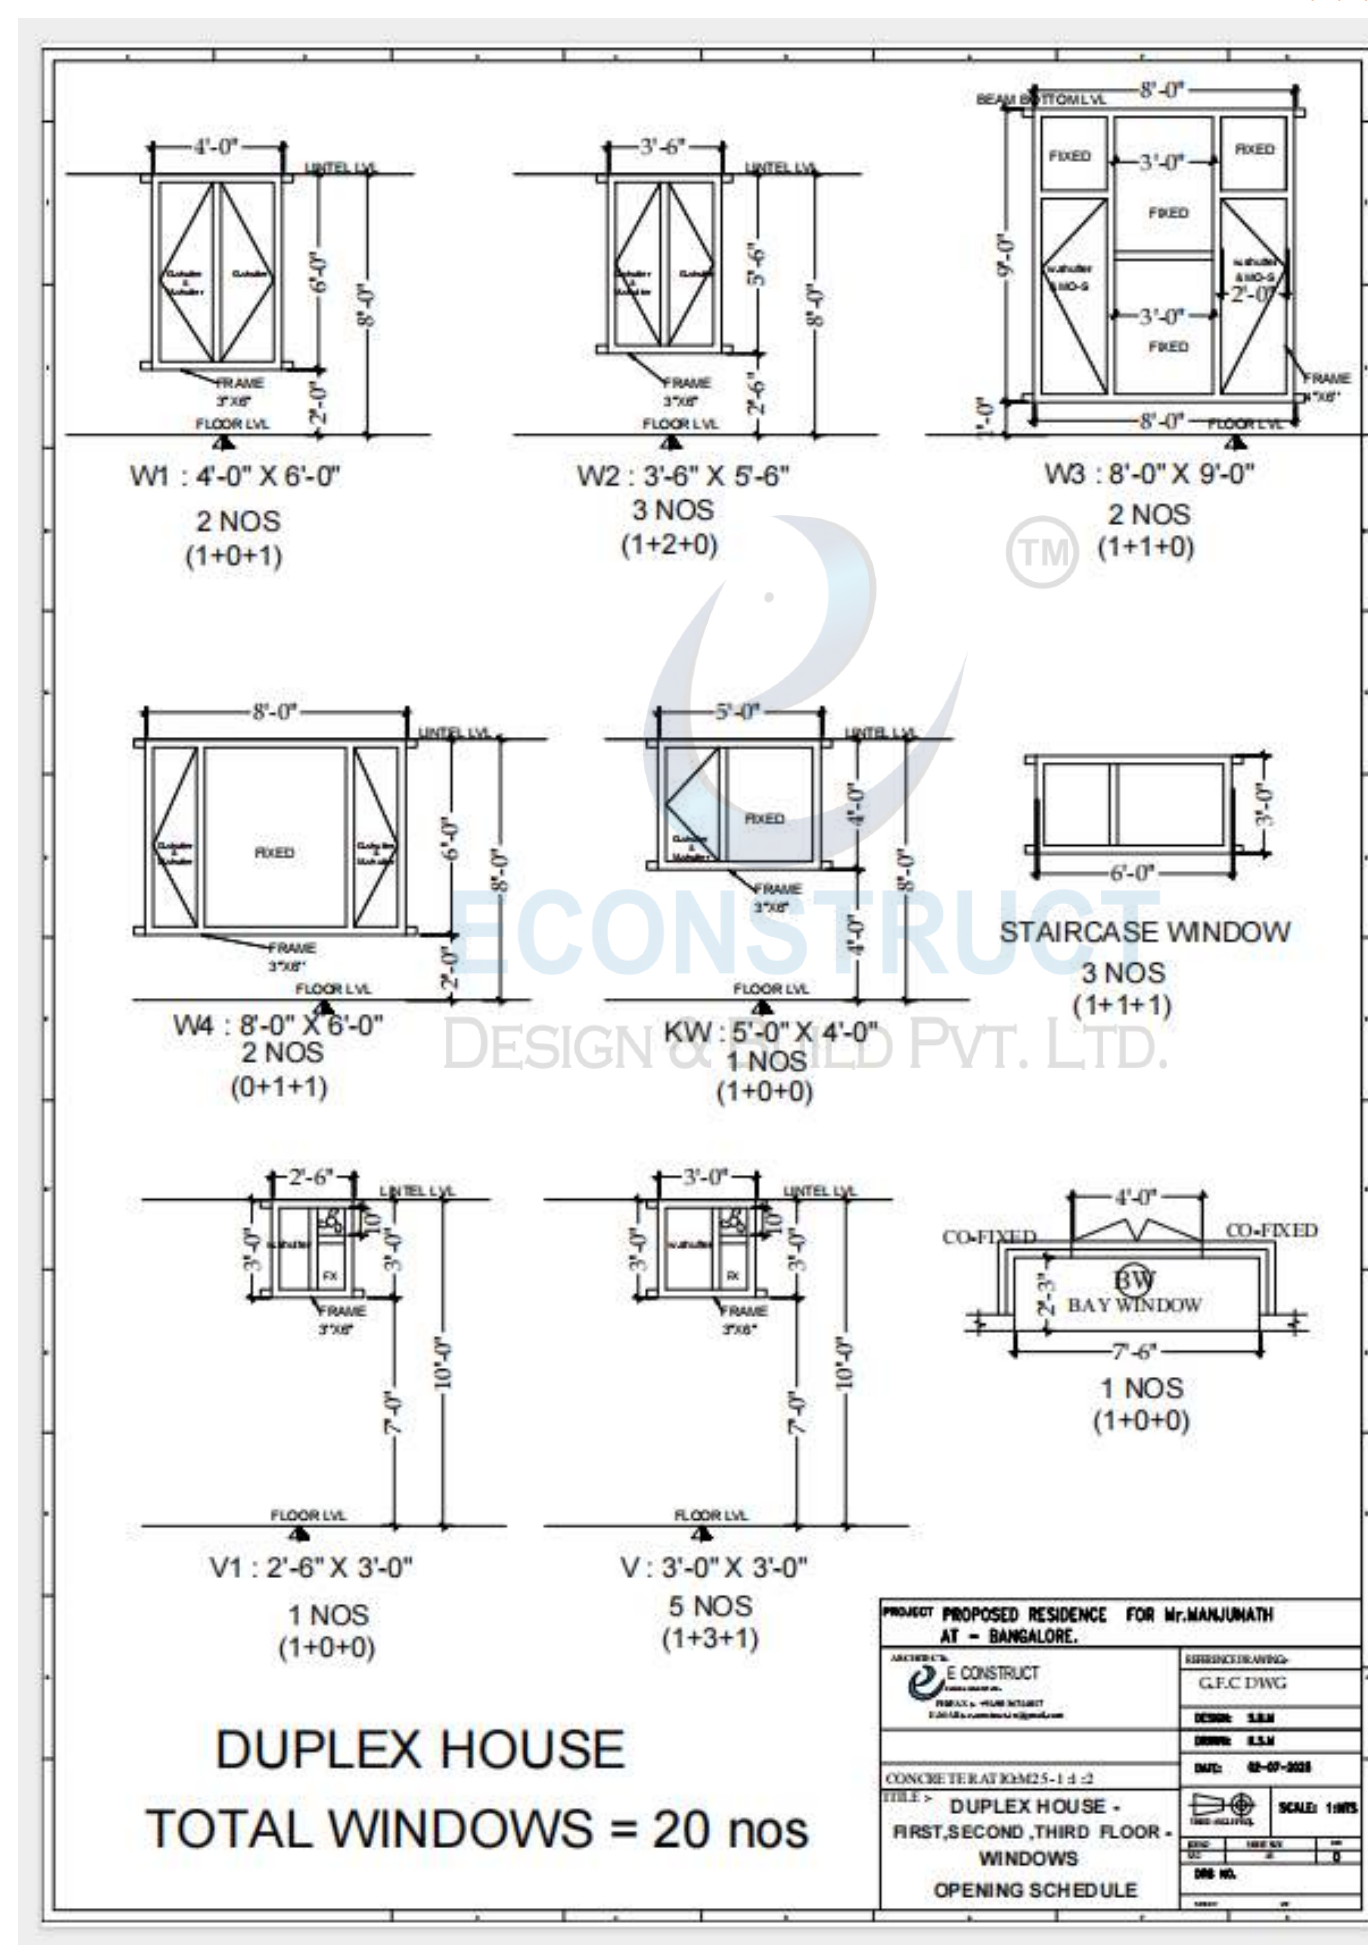


09

DUPLEX HOUSE - TOTAL DOORS =
20 nos

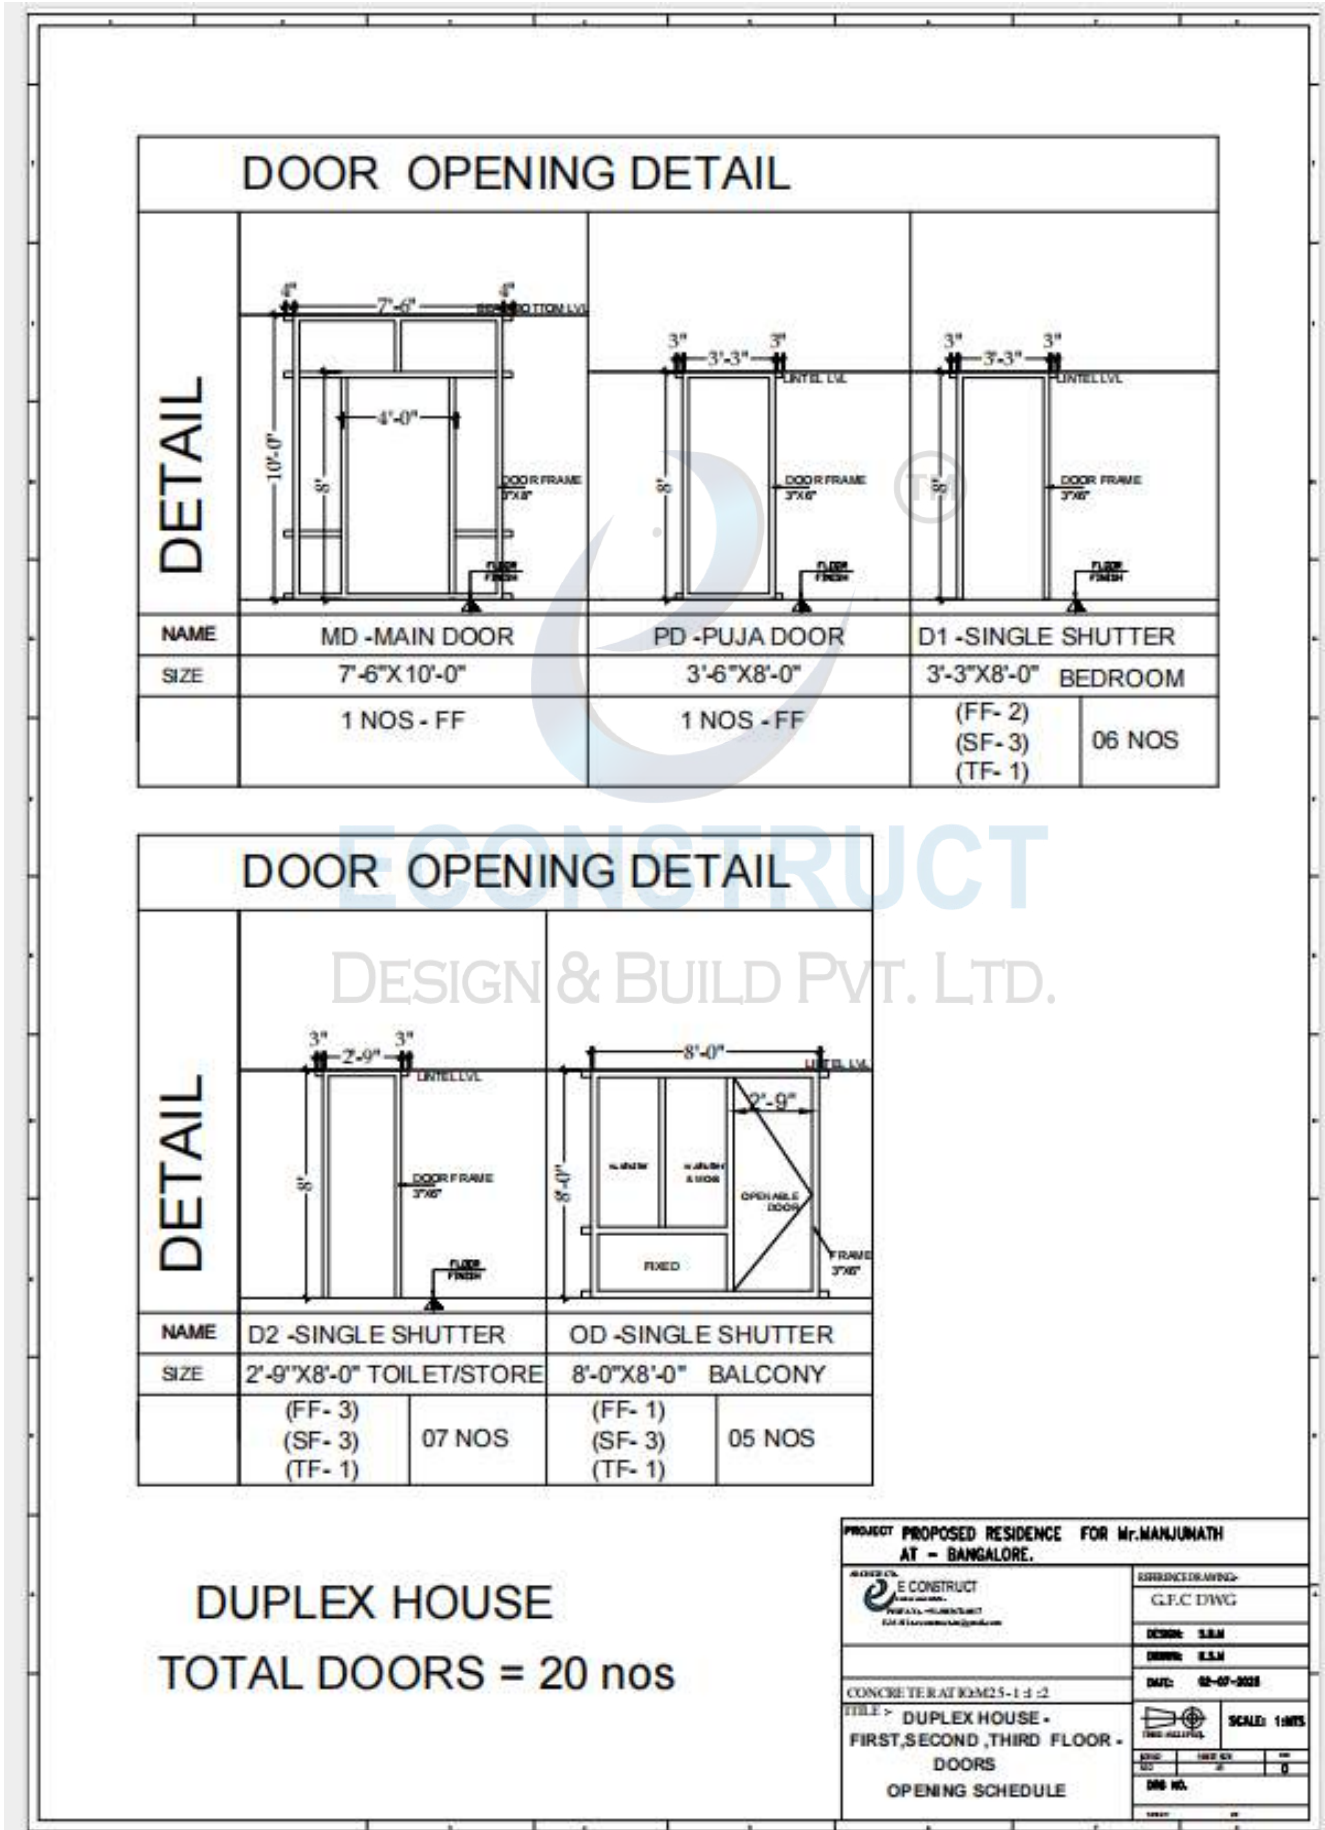


10

PLAN -EX STAIRCASE FROM GROUND
TO FIRST FLOOR ONLY

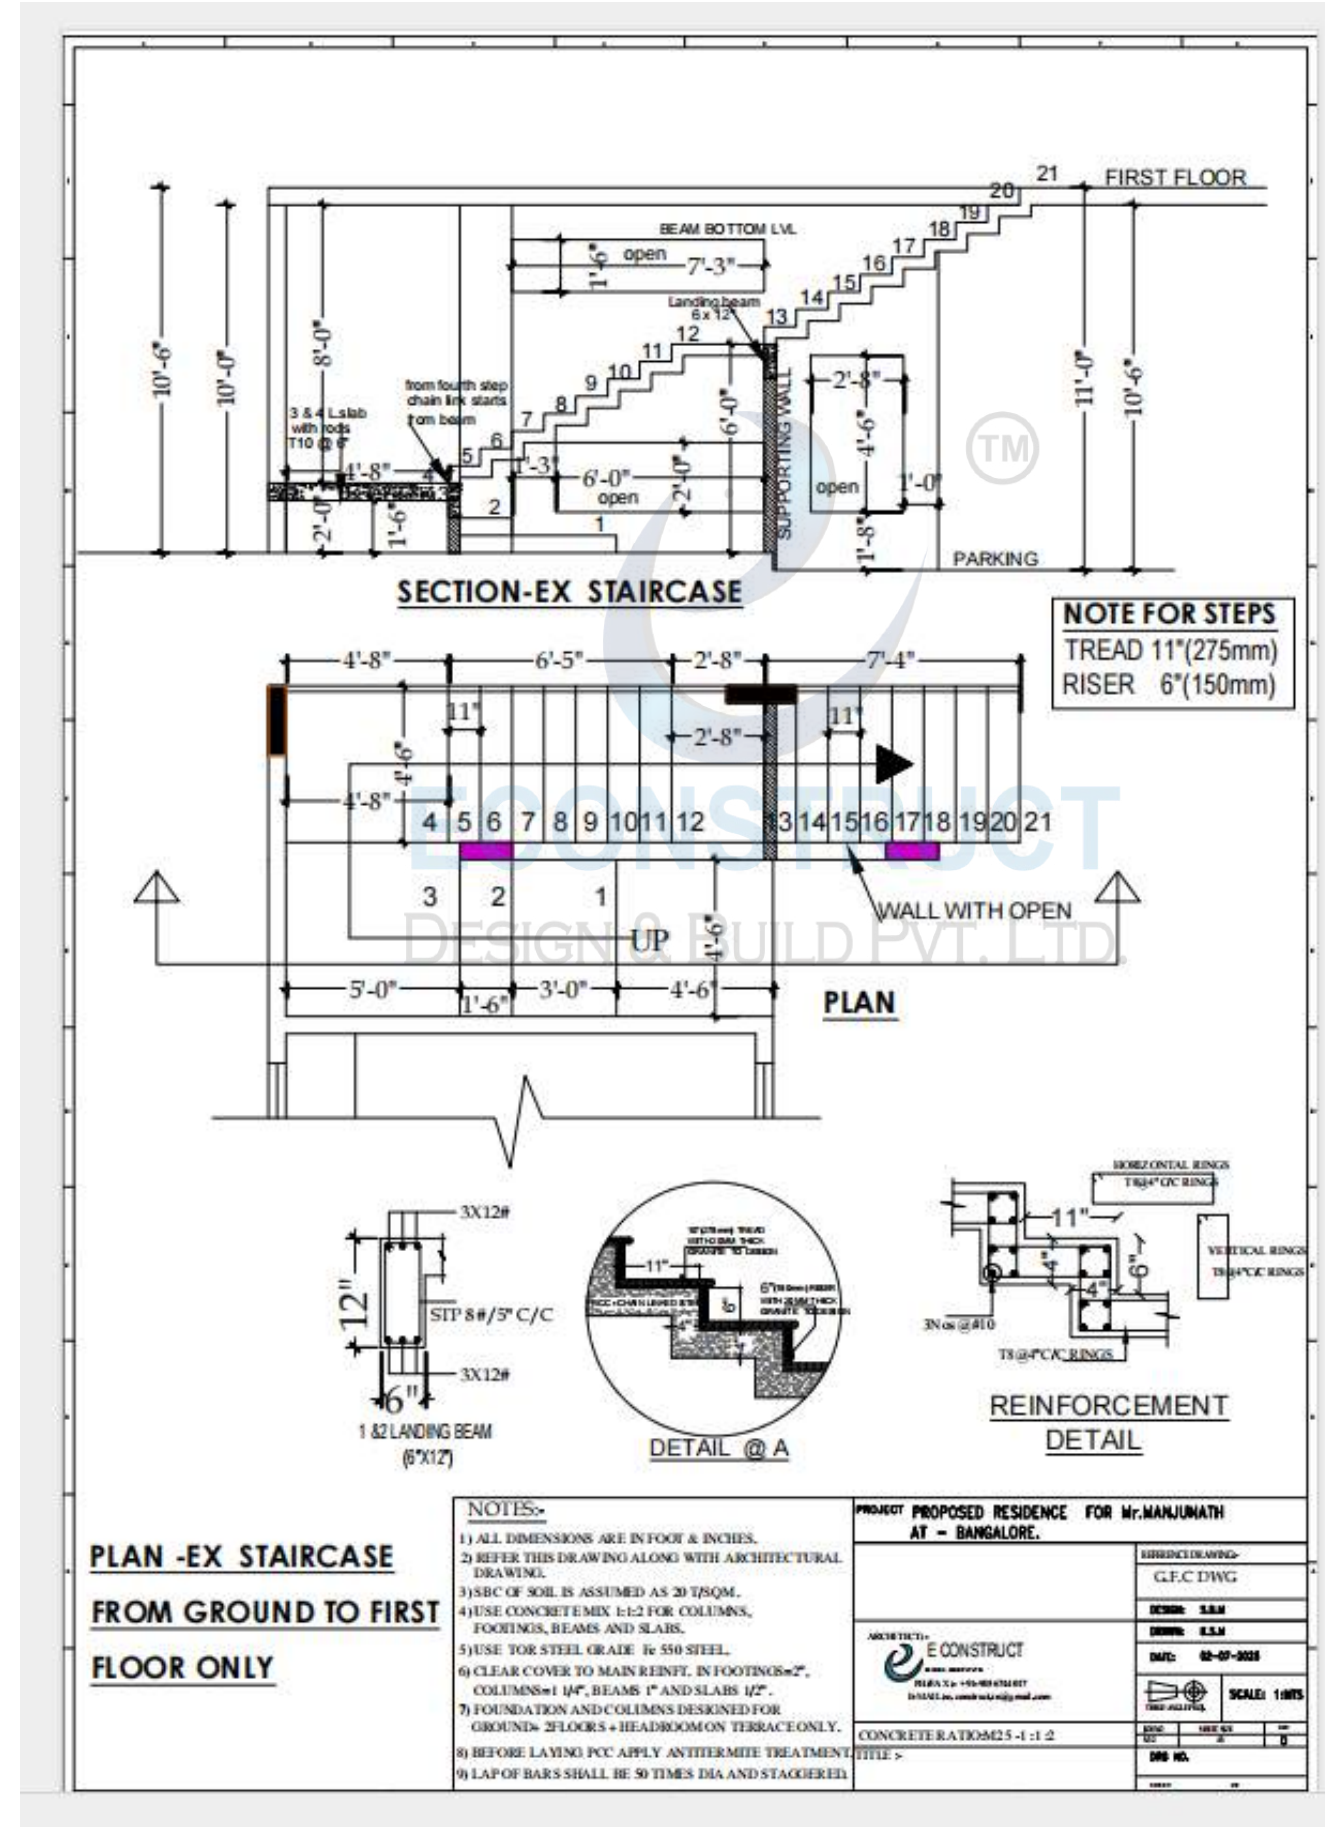


11

PLAN -INSIDE DUPLEX STAIRCASE

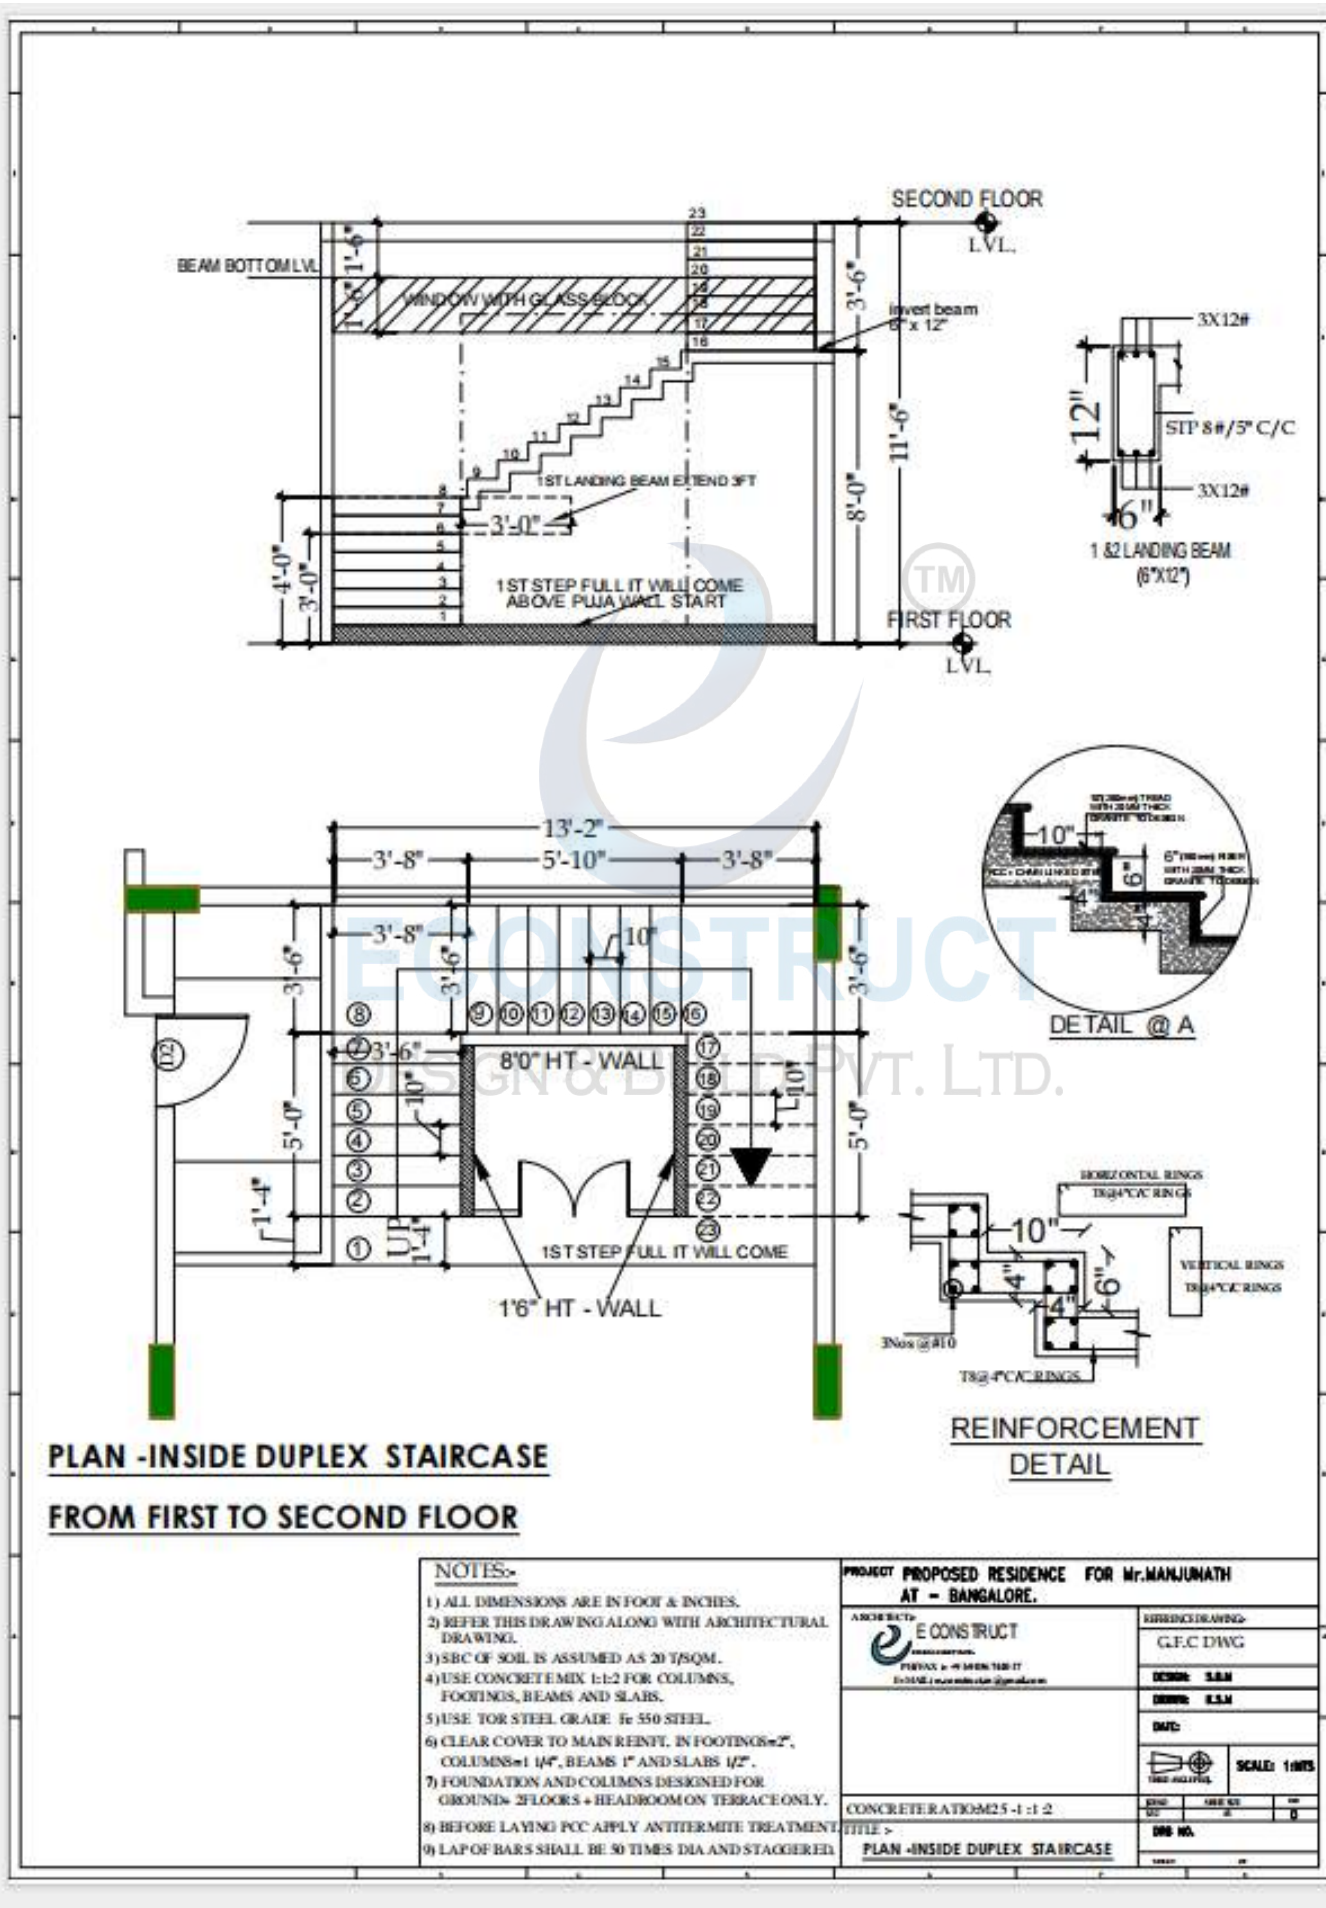


12

GROUND FLOOR PLAN - LOFT & CHAJJA DETAILS

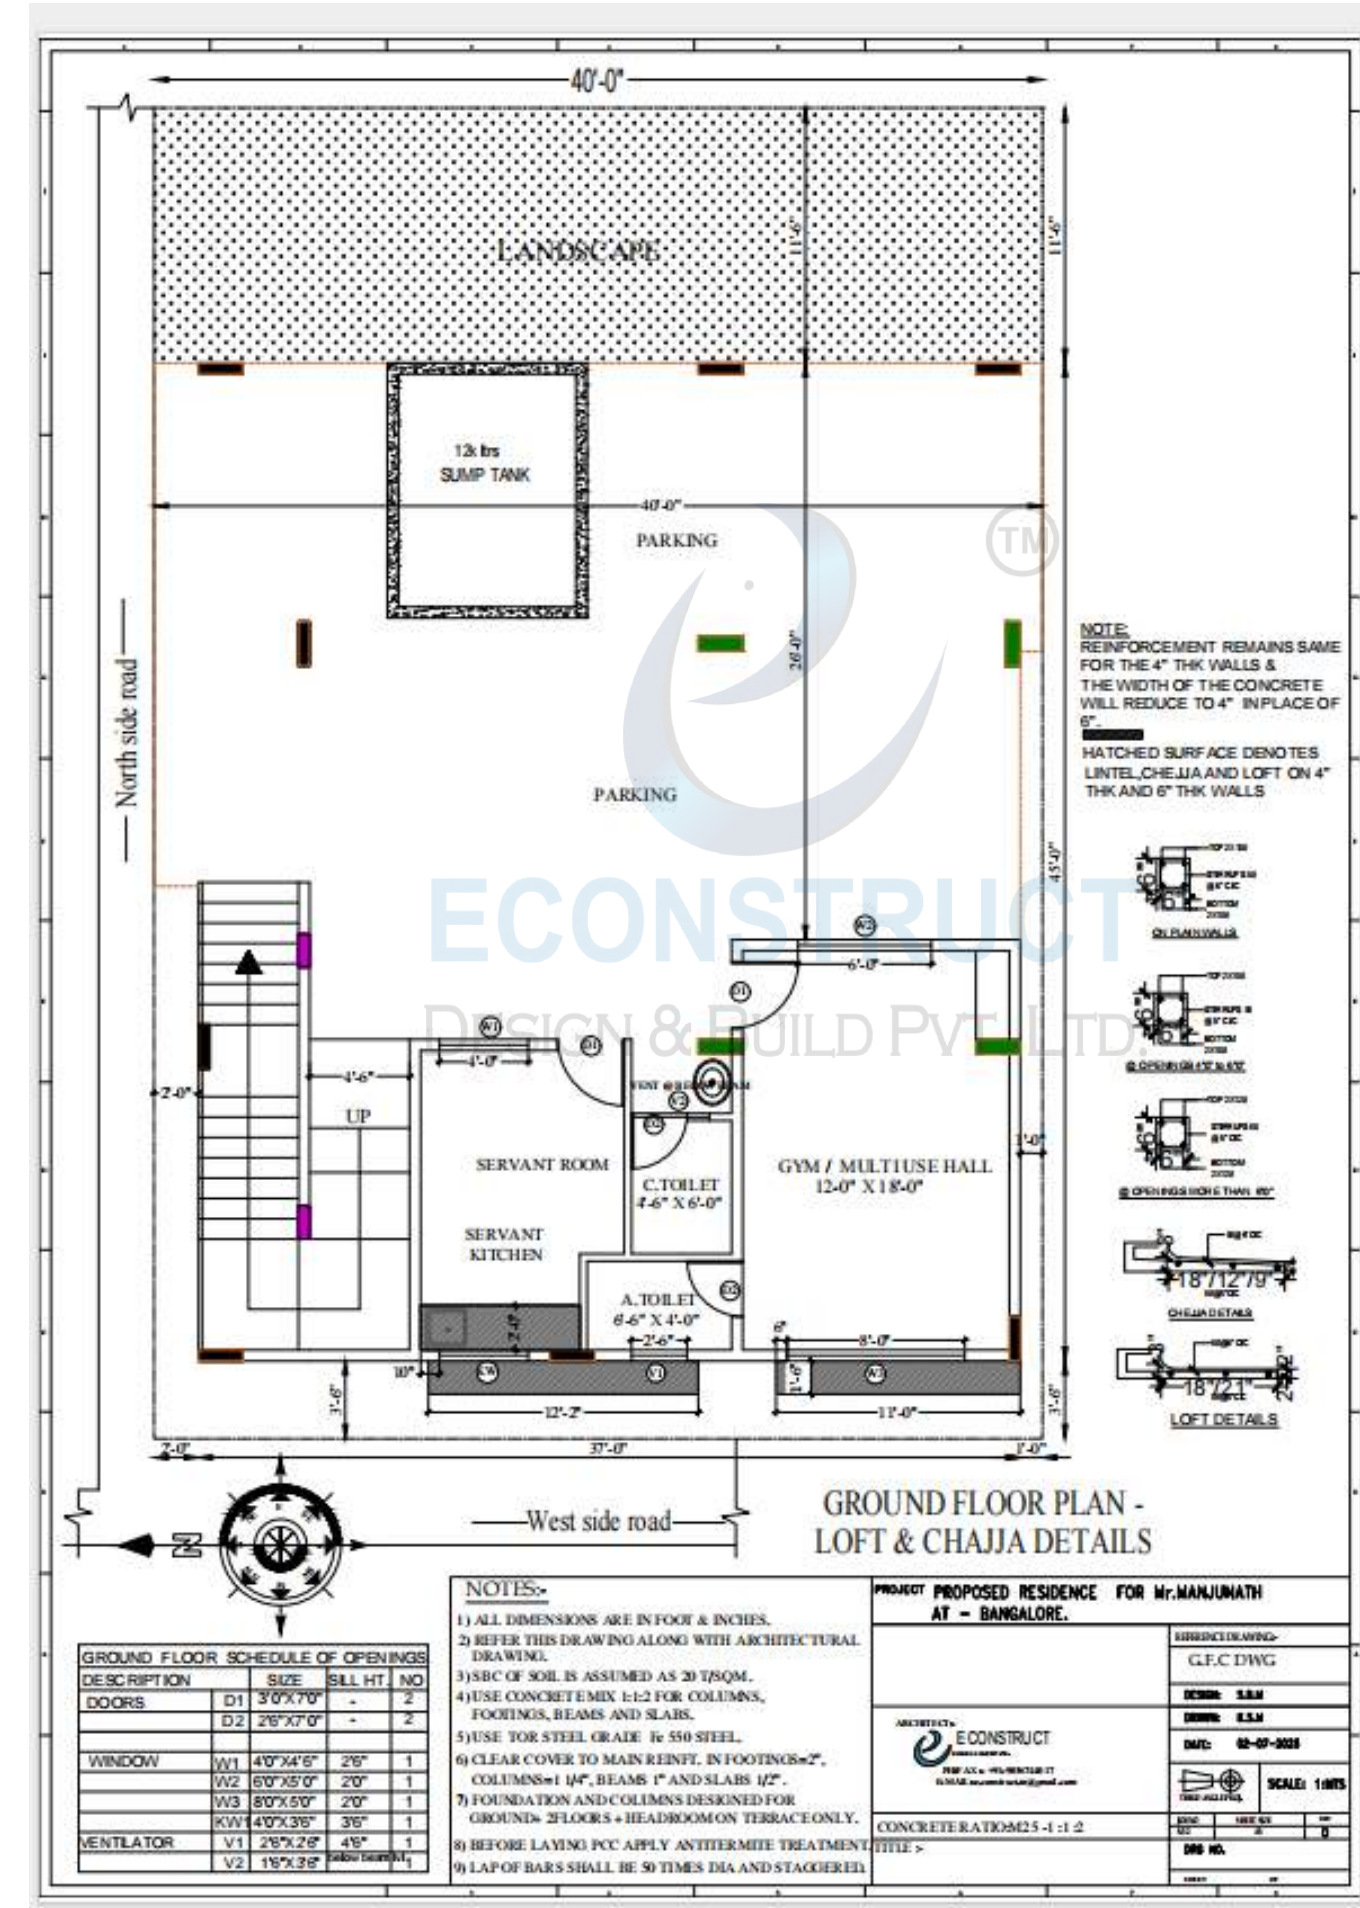


13

FIRST FLOOR PLAN - LOFT & CHAJJA DETAILS

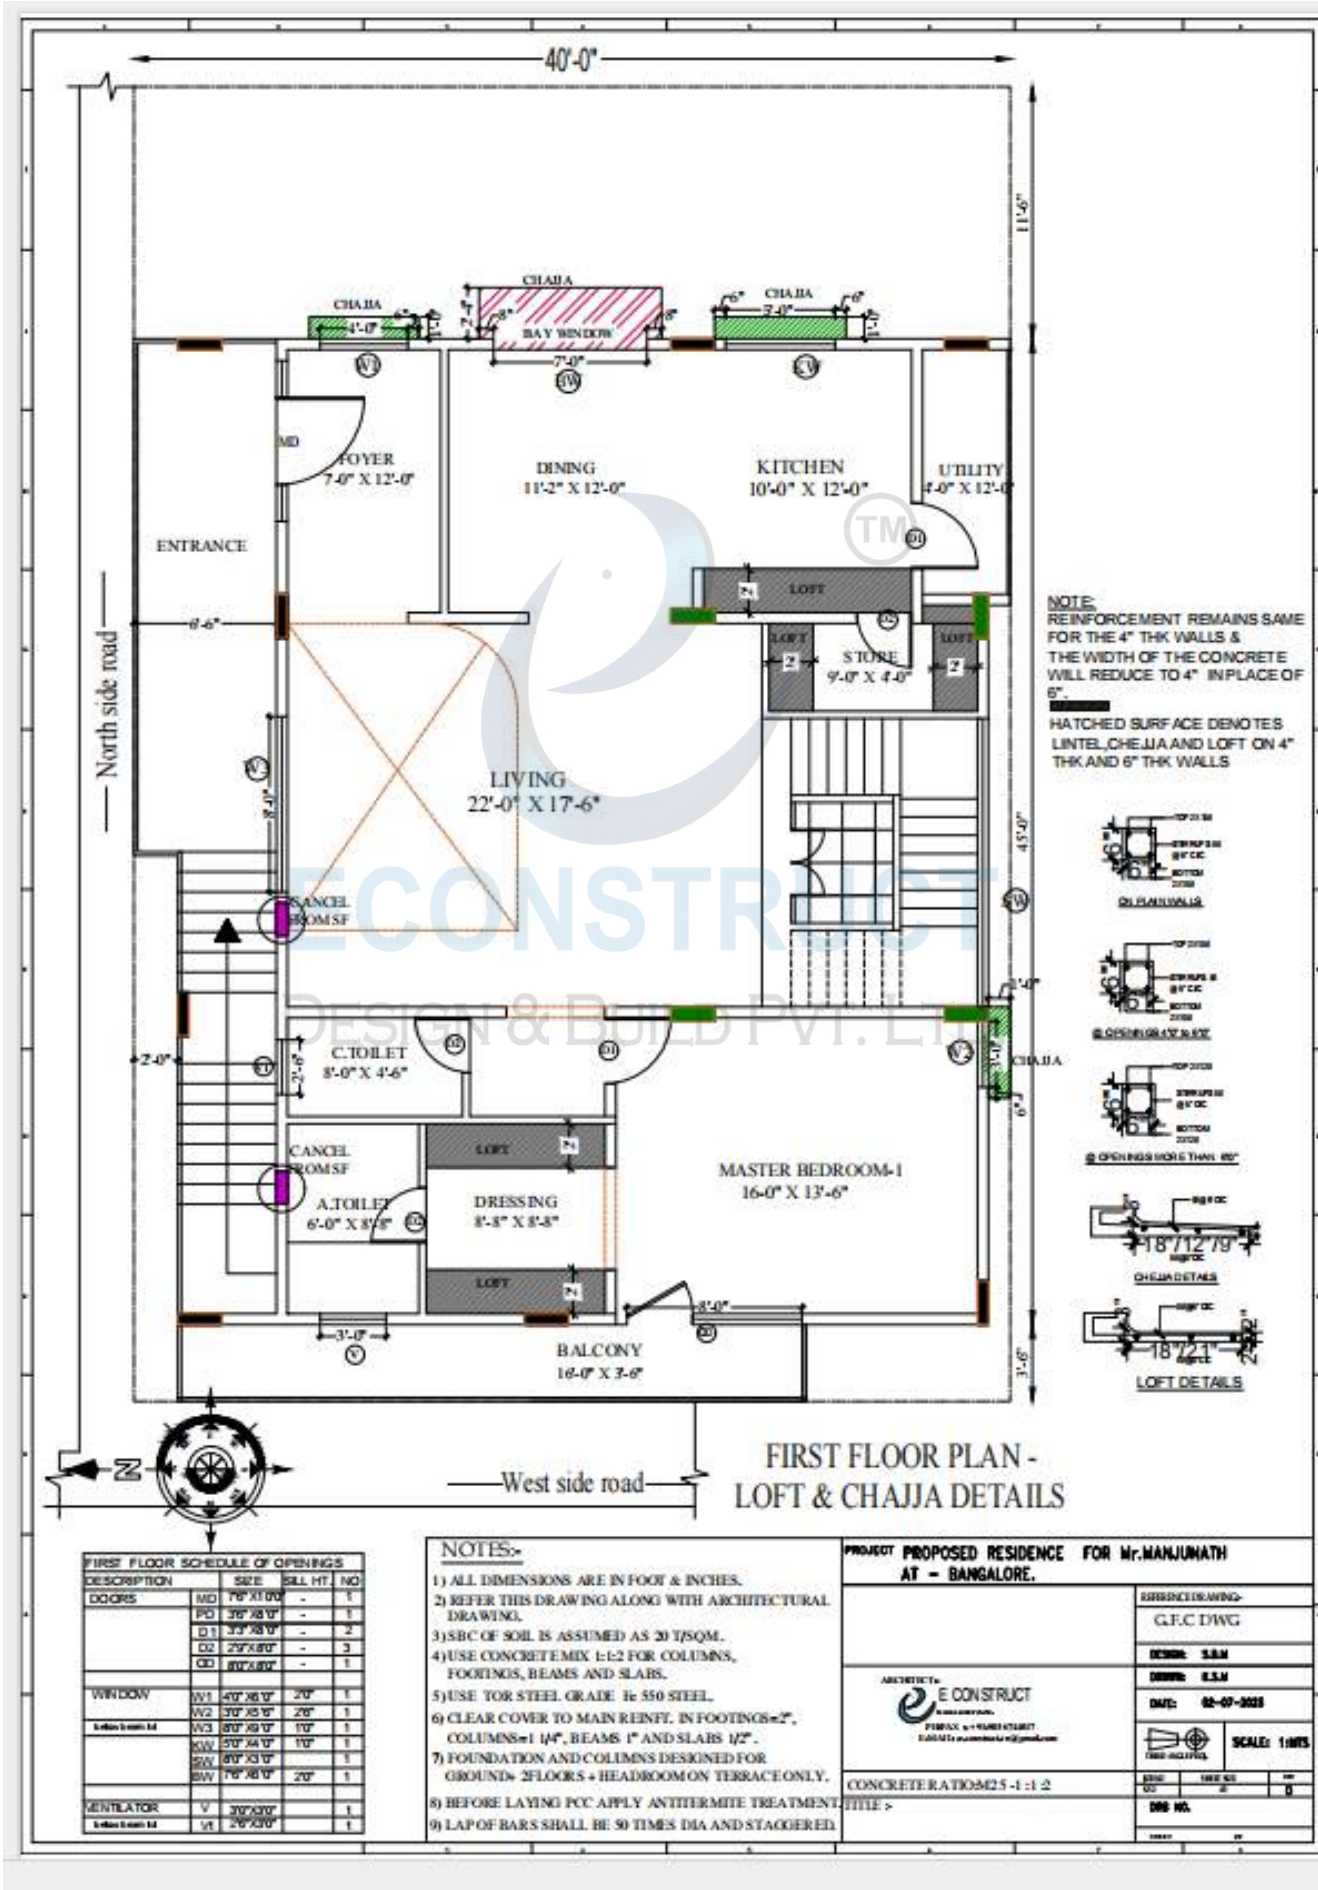


14


SECOND FLOOR PLAN - LOFT & CHAJJA DETAILS

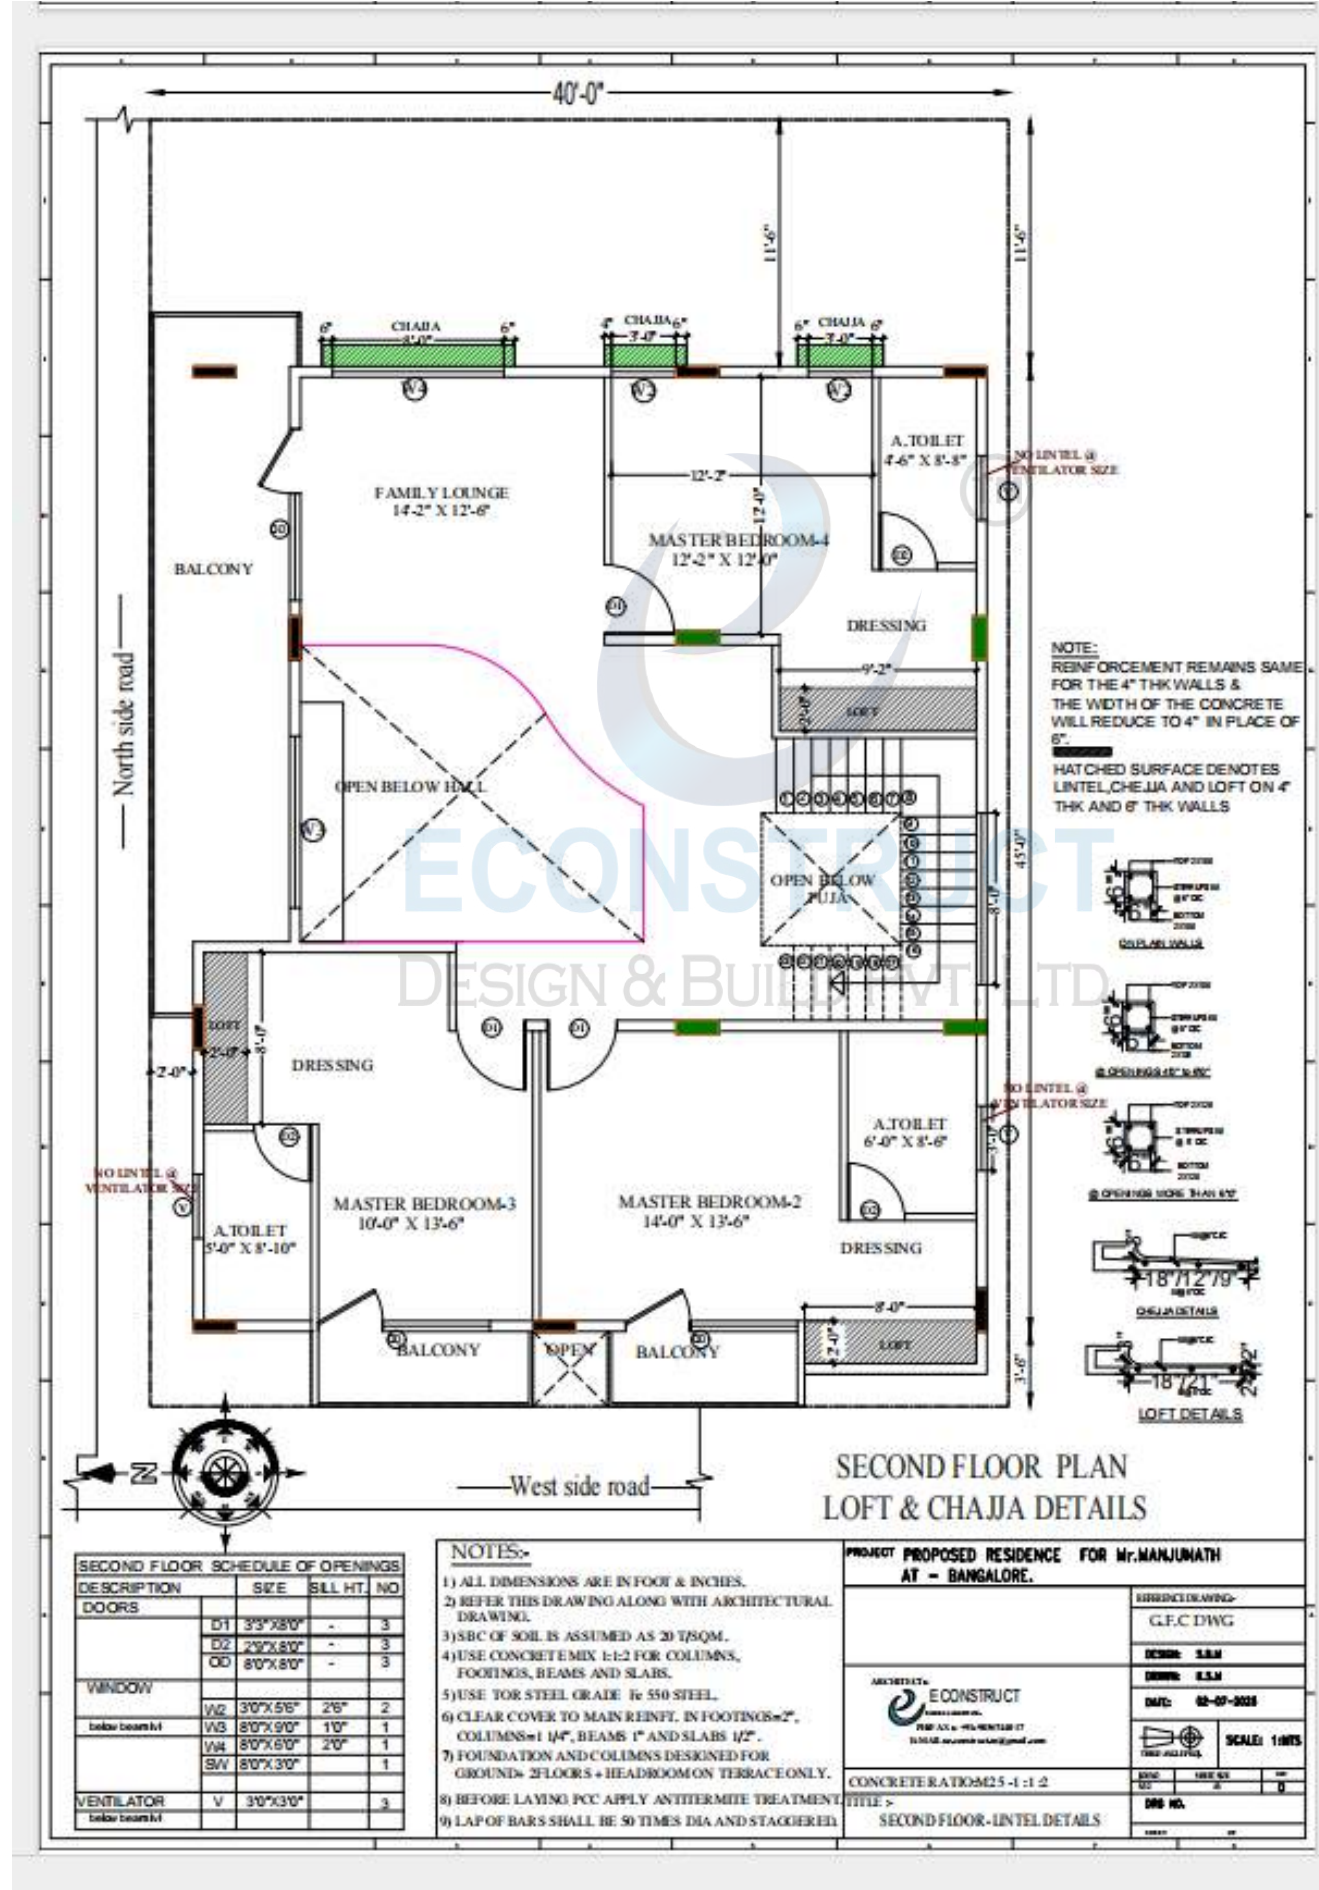

GROUND FLOOR PLAN (RVSD) (ELECTRICAL CEILING FIXTURE LAYOUT)

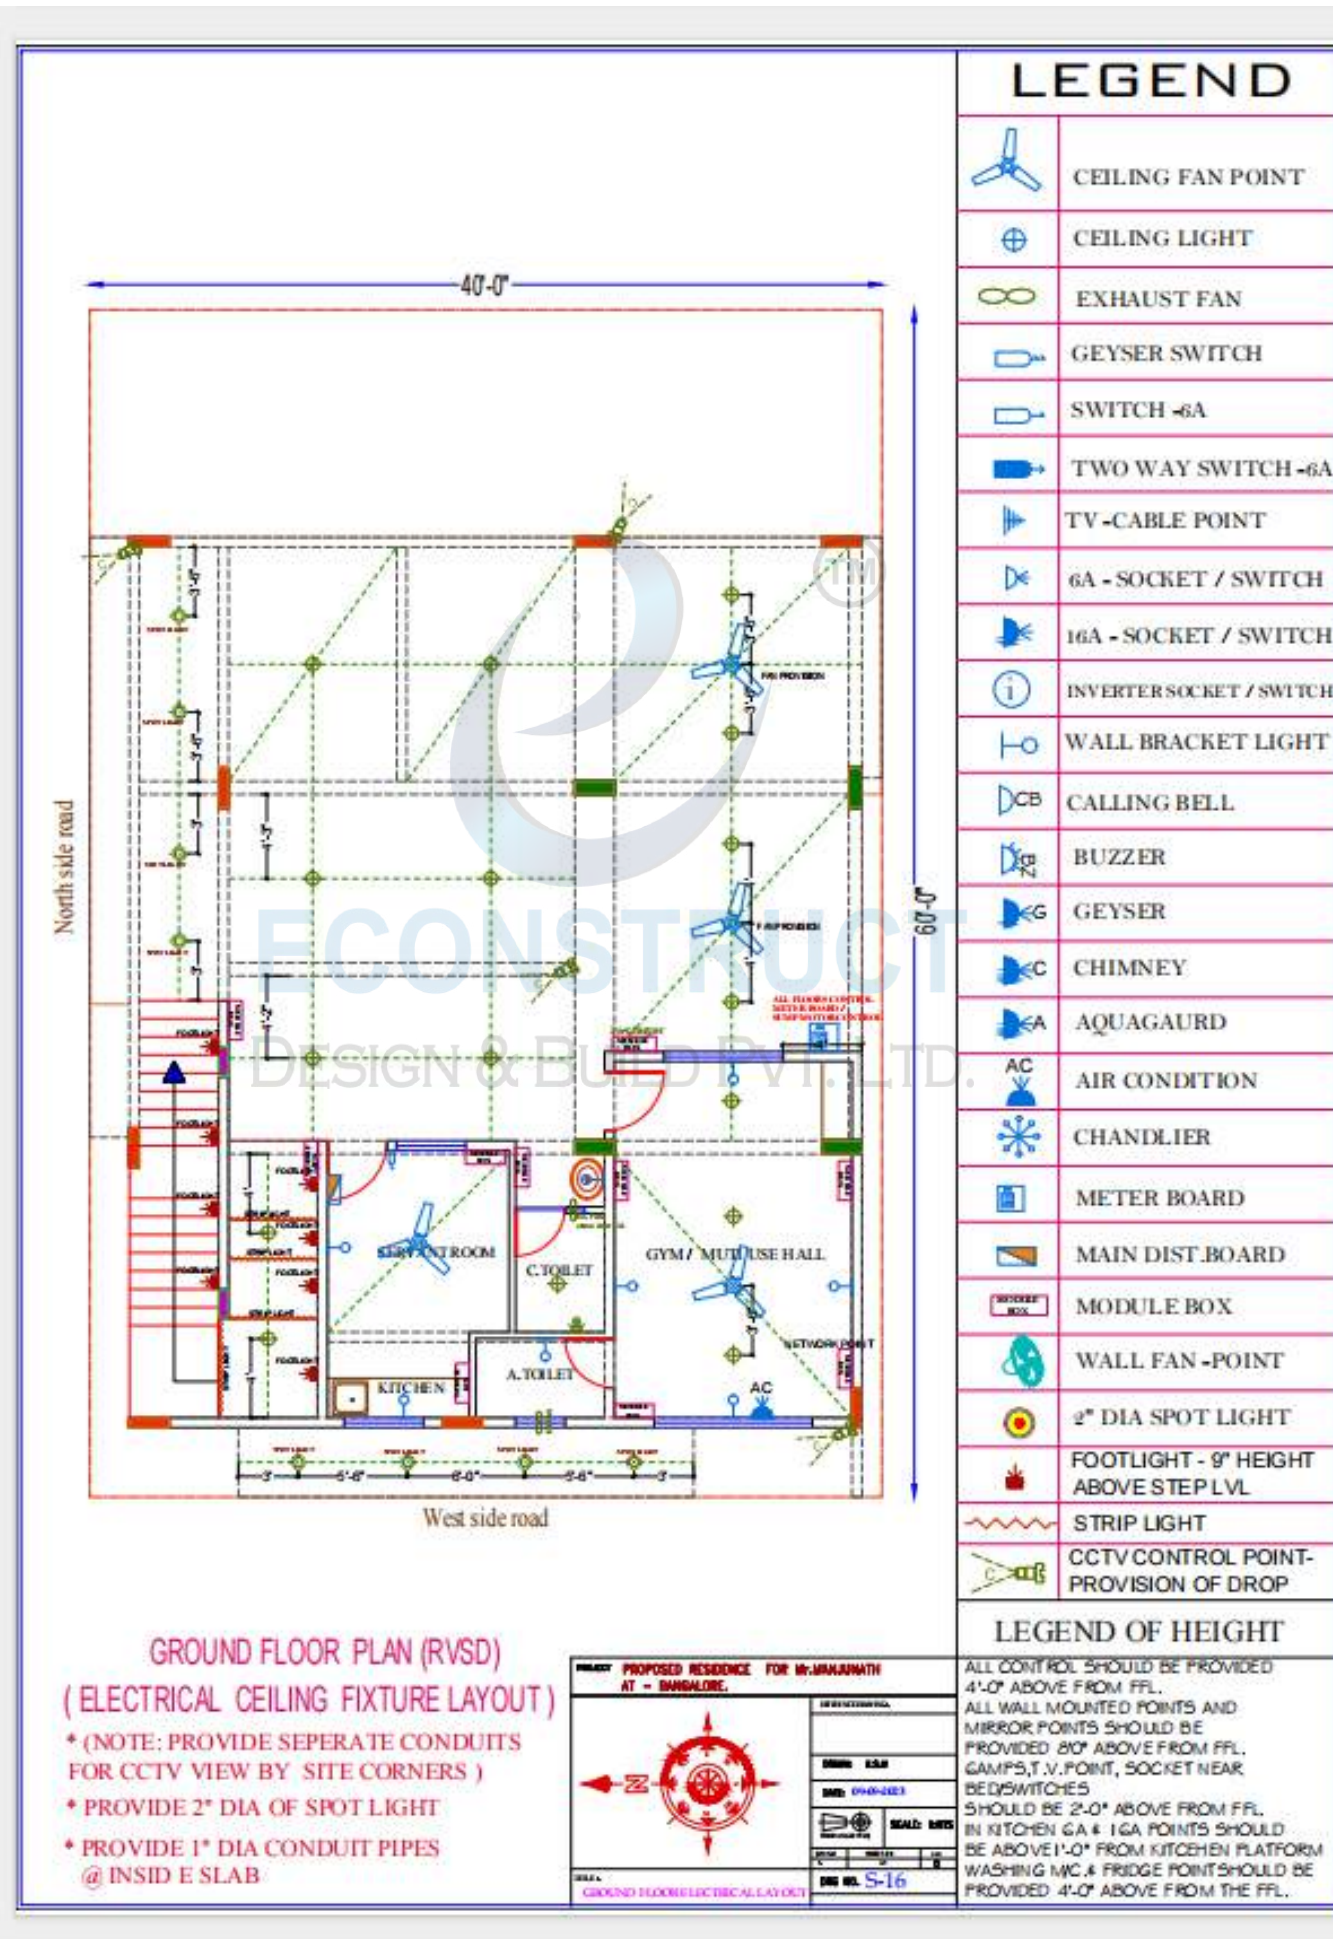


FIRST FLOOR PLAN PROVISION OF DROP (ELECTRICAL CEILING FIXTURE LAYOUT)

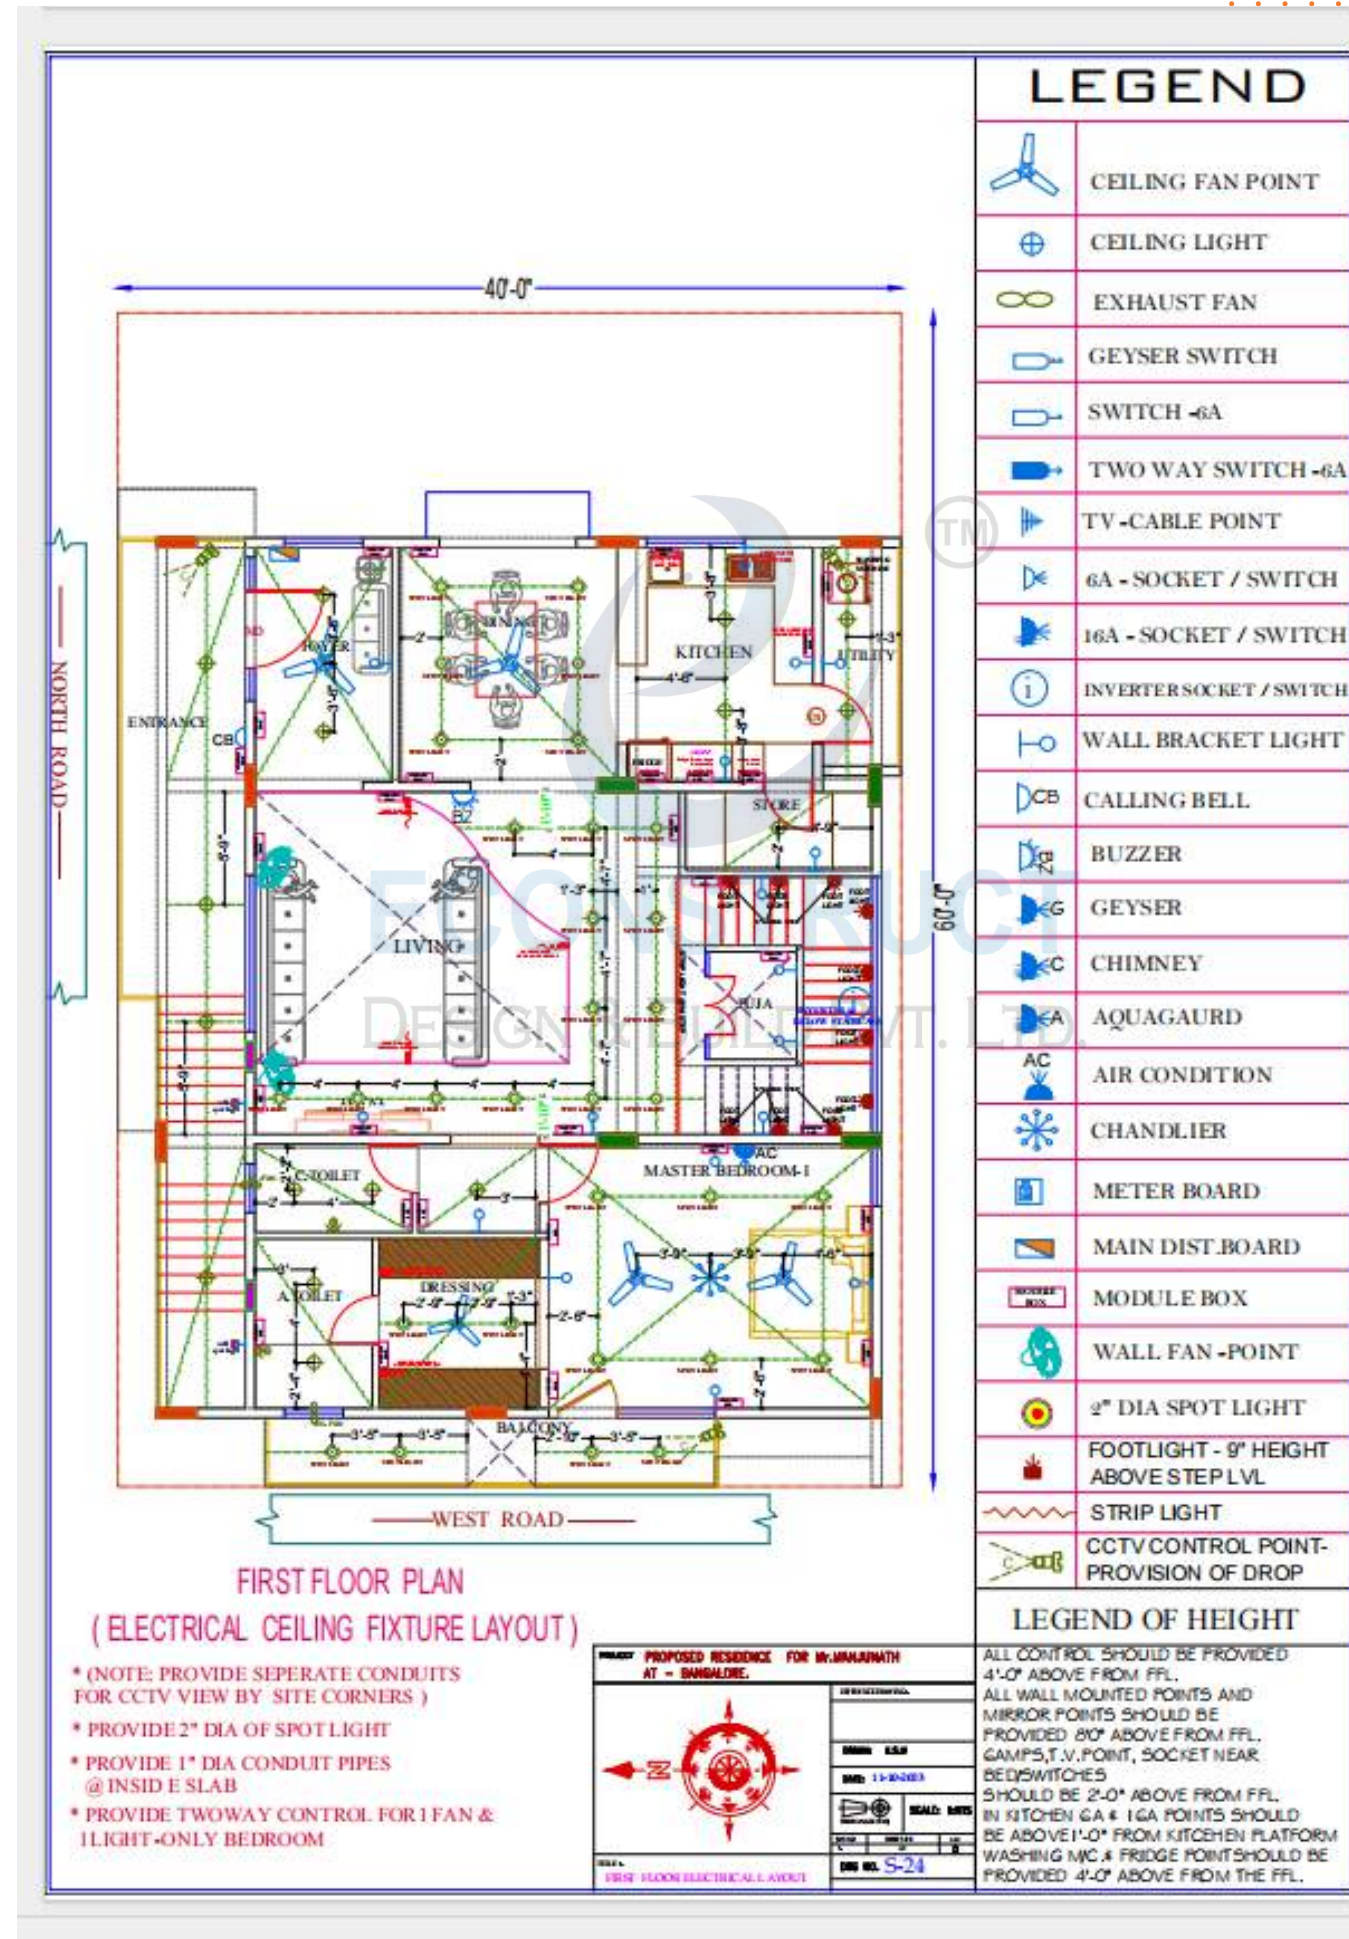


17



SECOND FLOOR PLAN PROVISION OF DROP (ELECTRICAL CEILING FIXTURE LAYOUT)

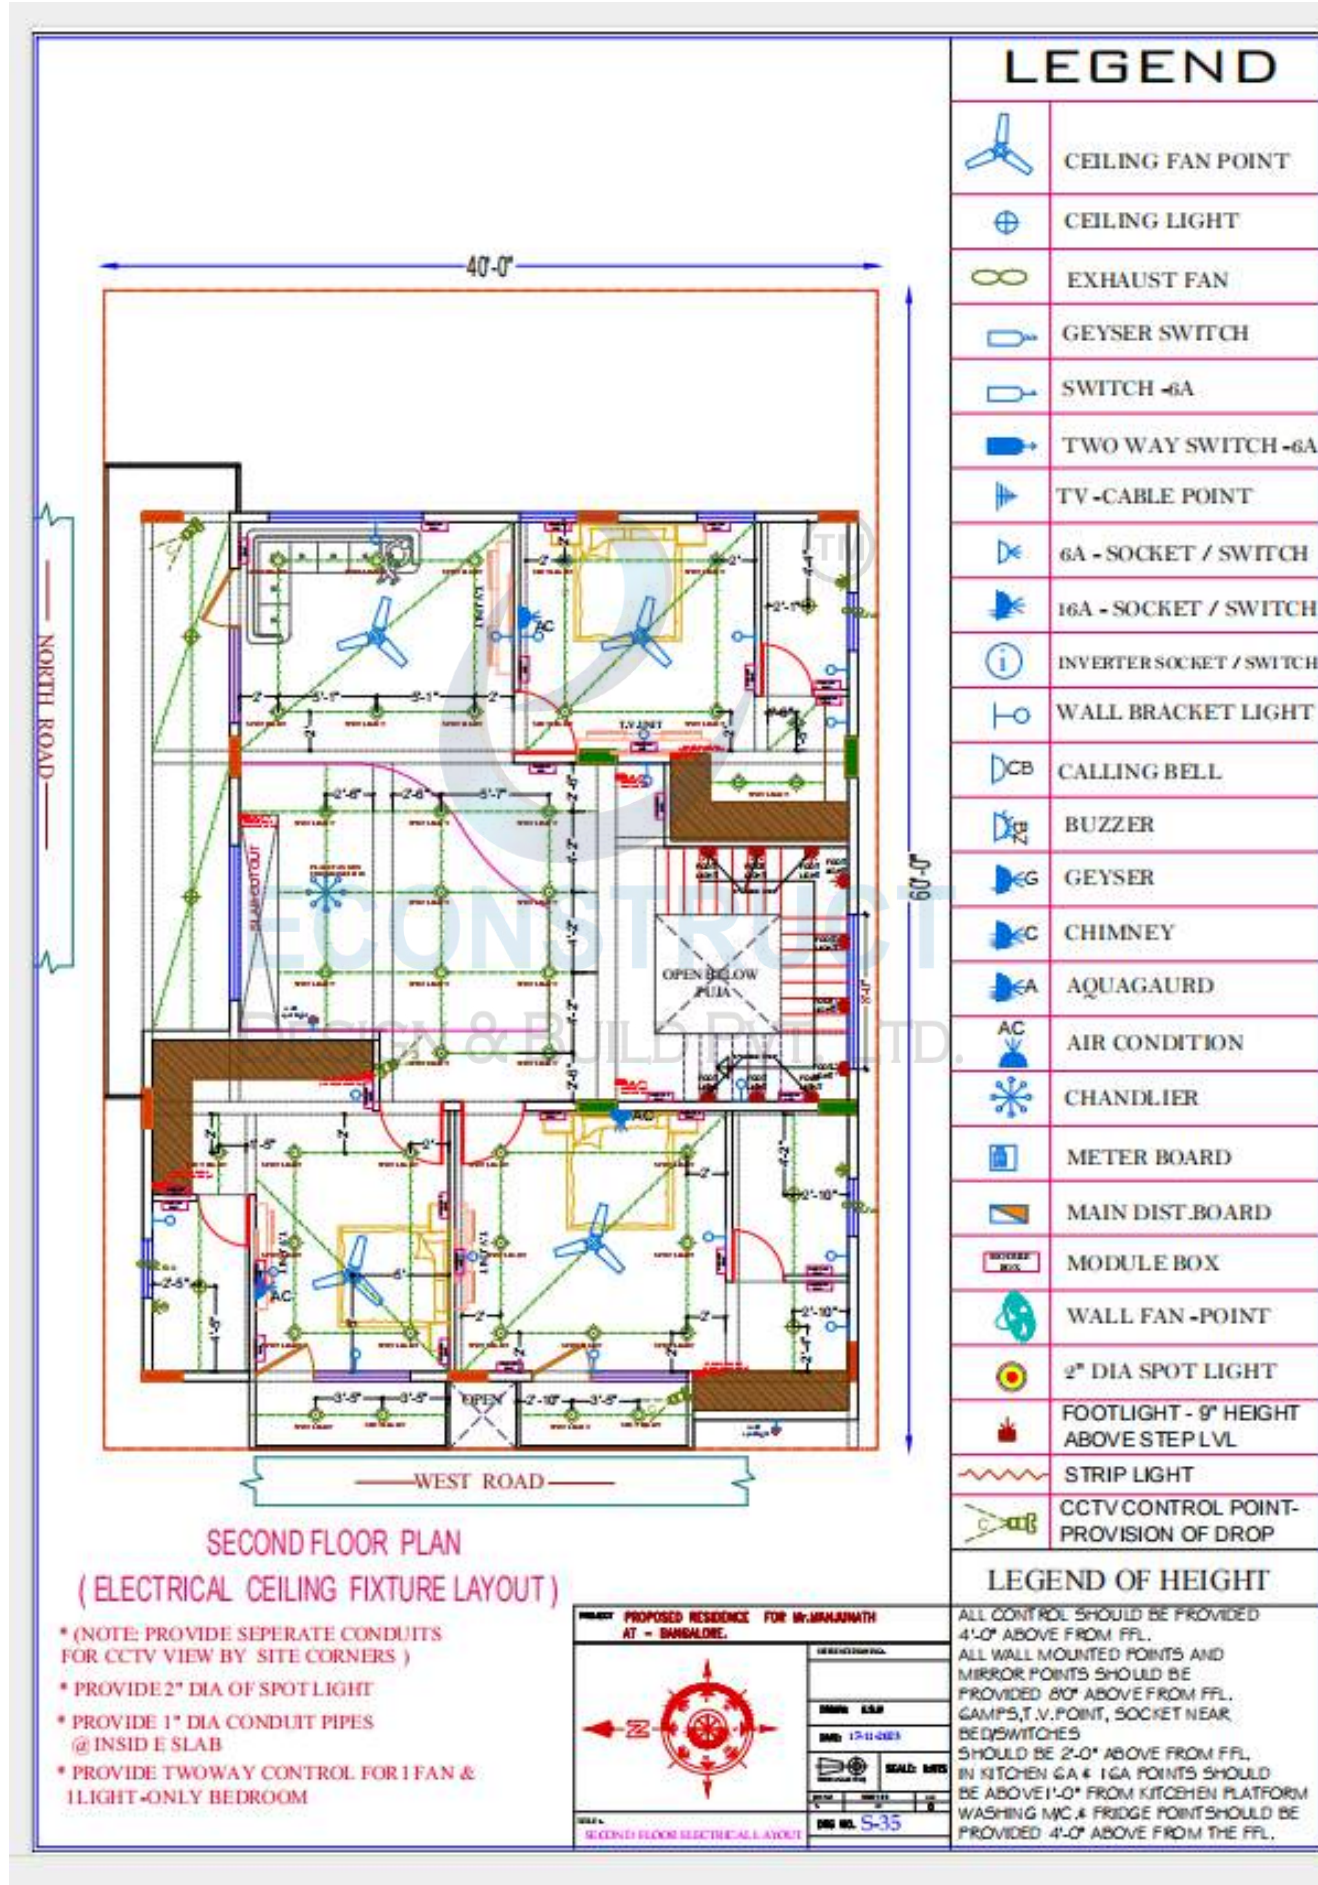

18


TERRACE FLOOR PLAN - (ELECTRICAL CEILING FIXTURE LAYOUT)

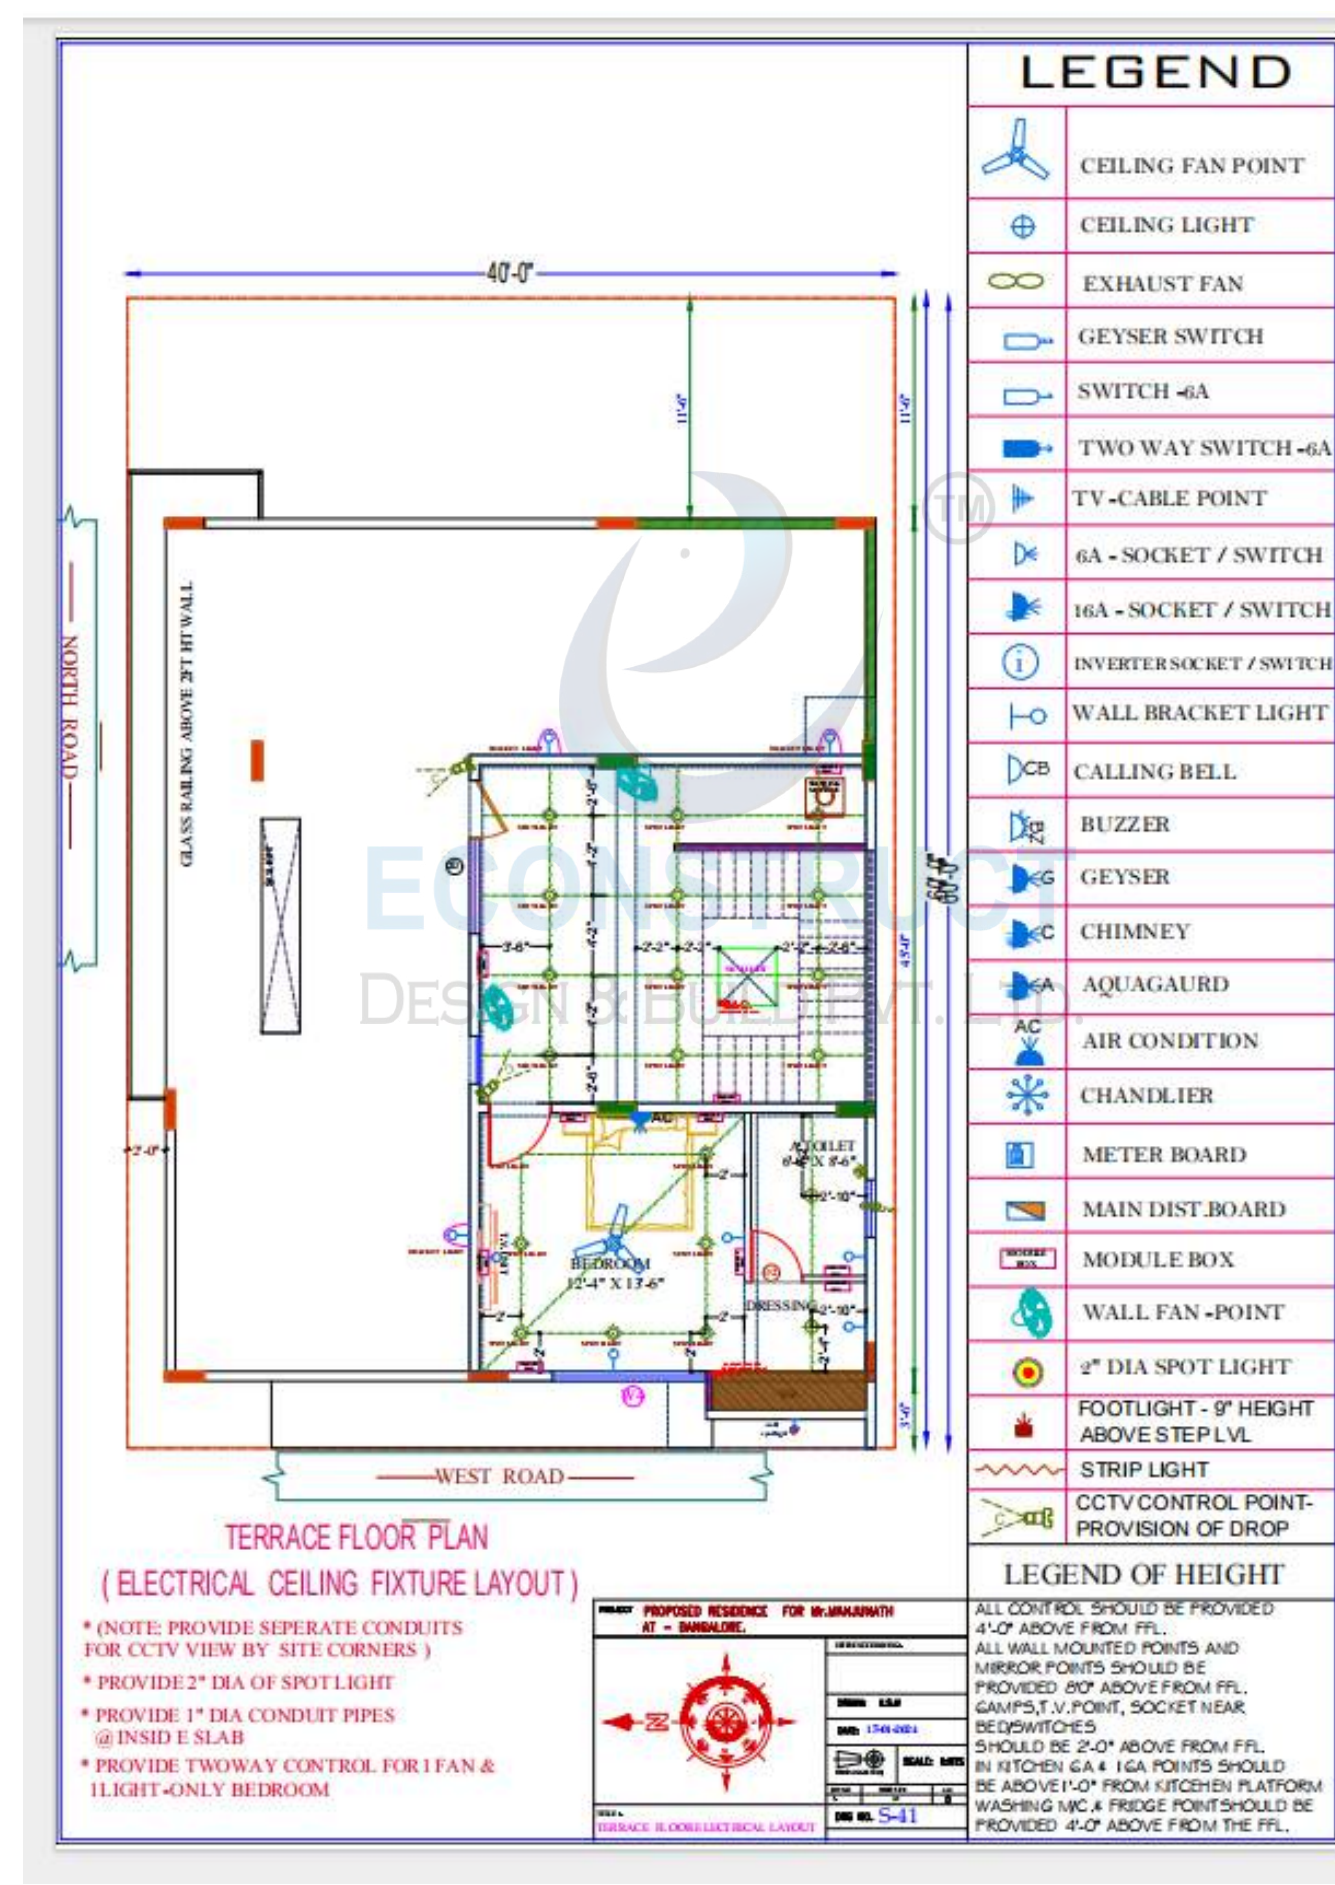

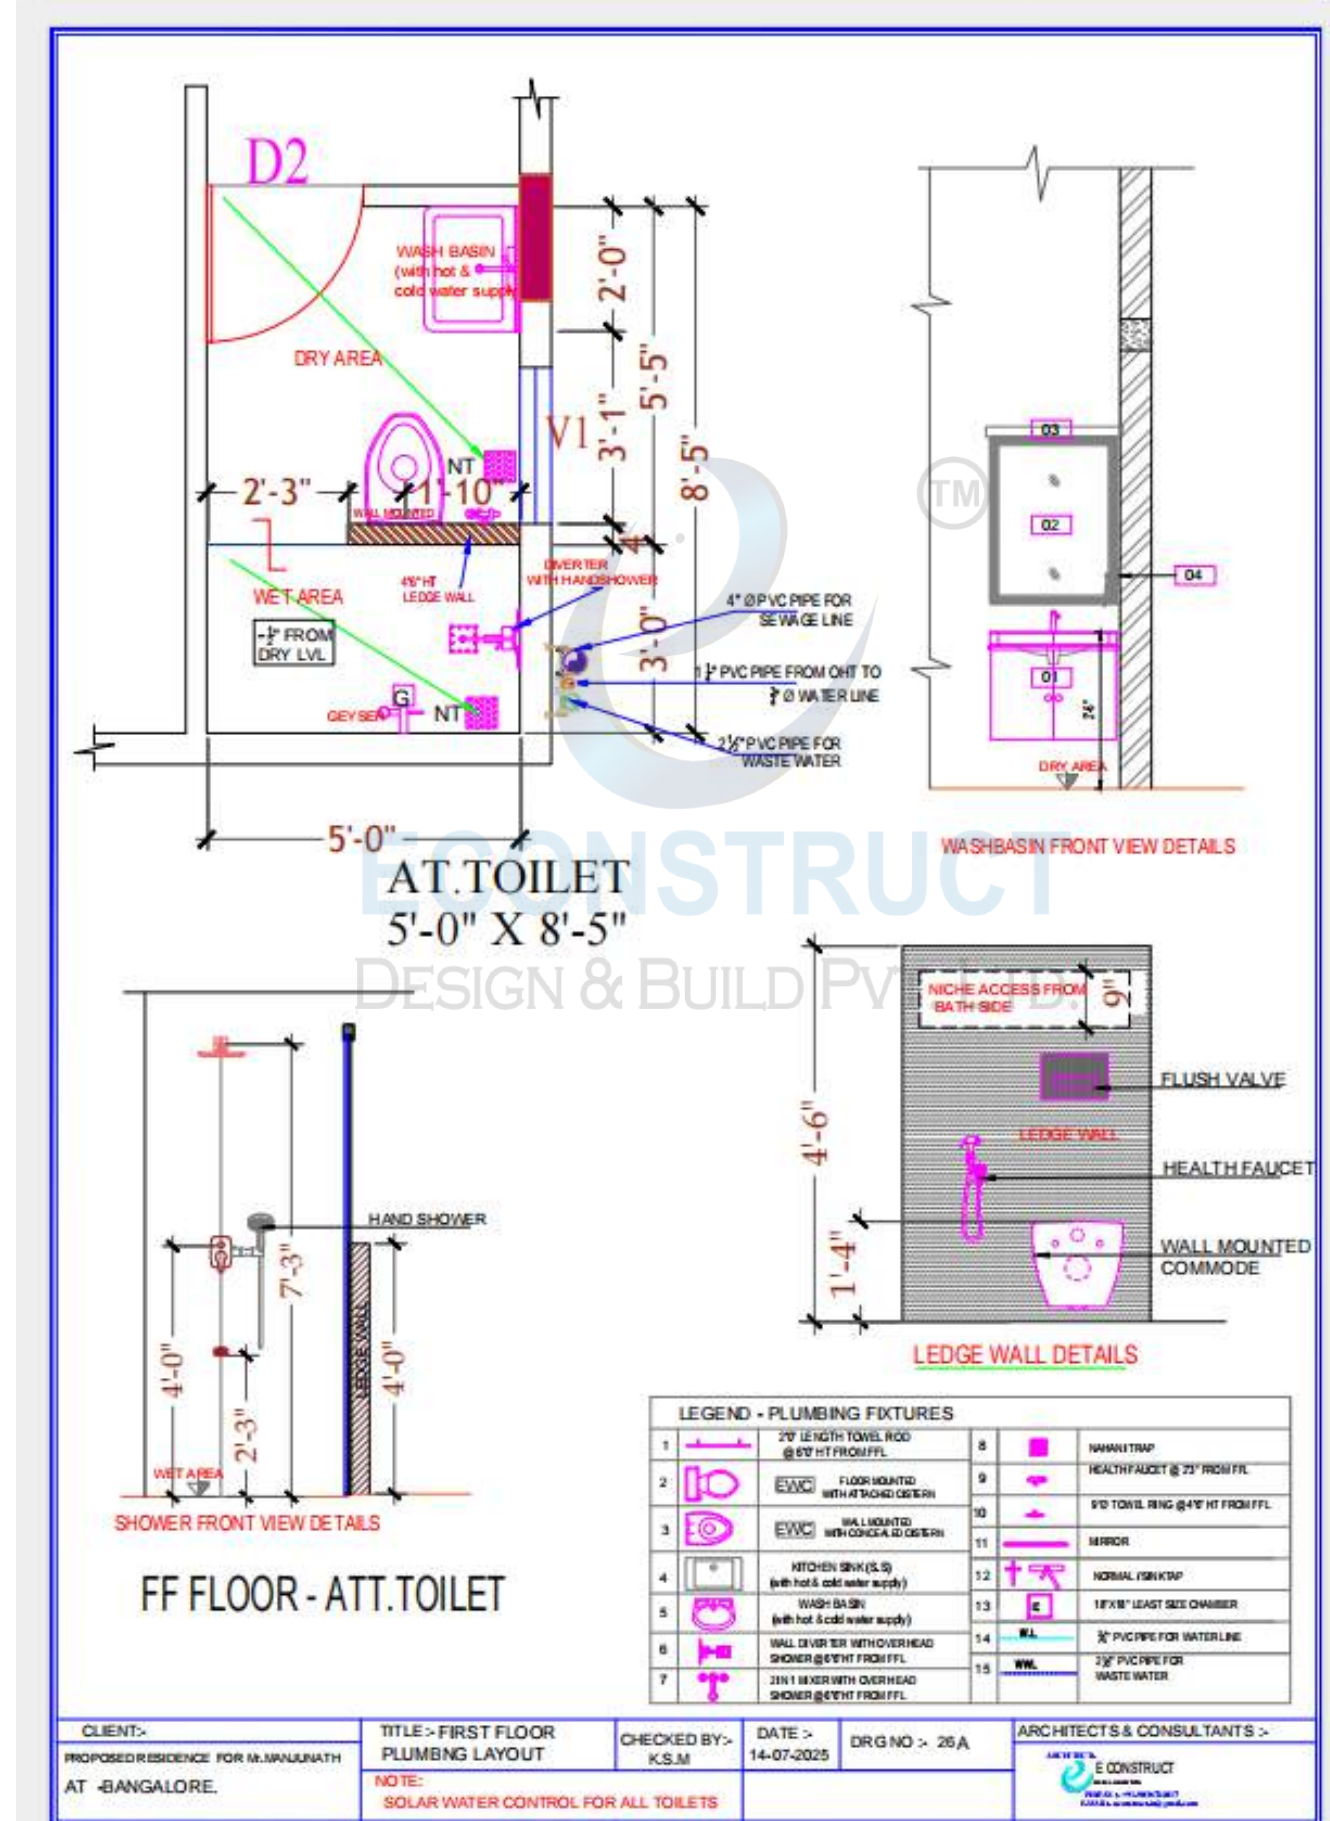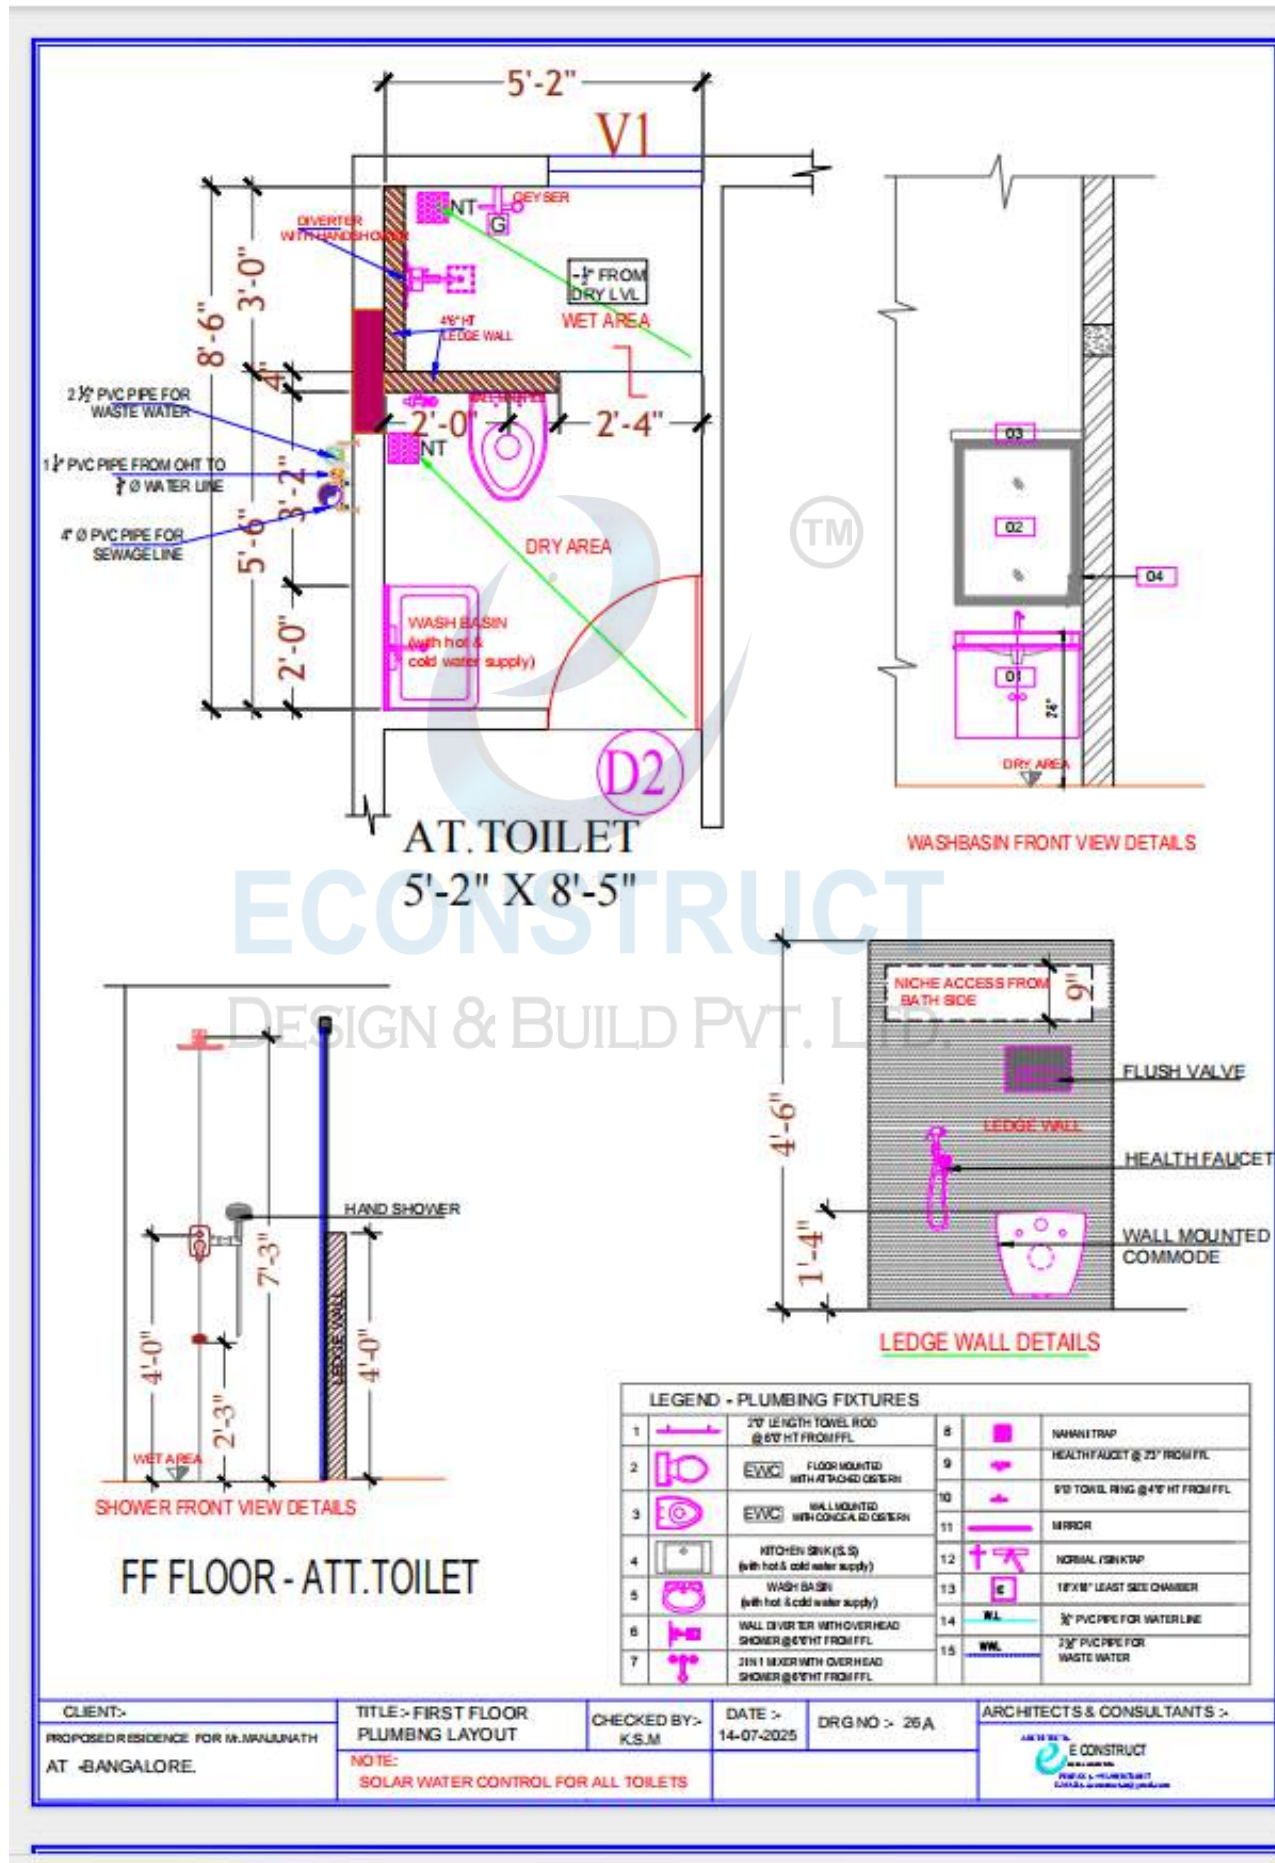


21

FF - KITCHEN / UTILITY

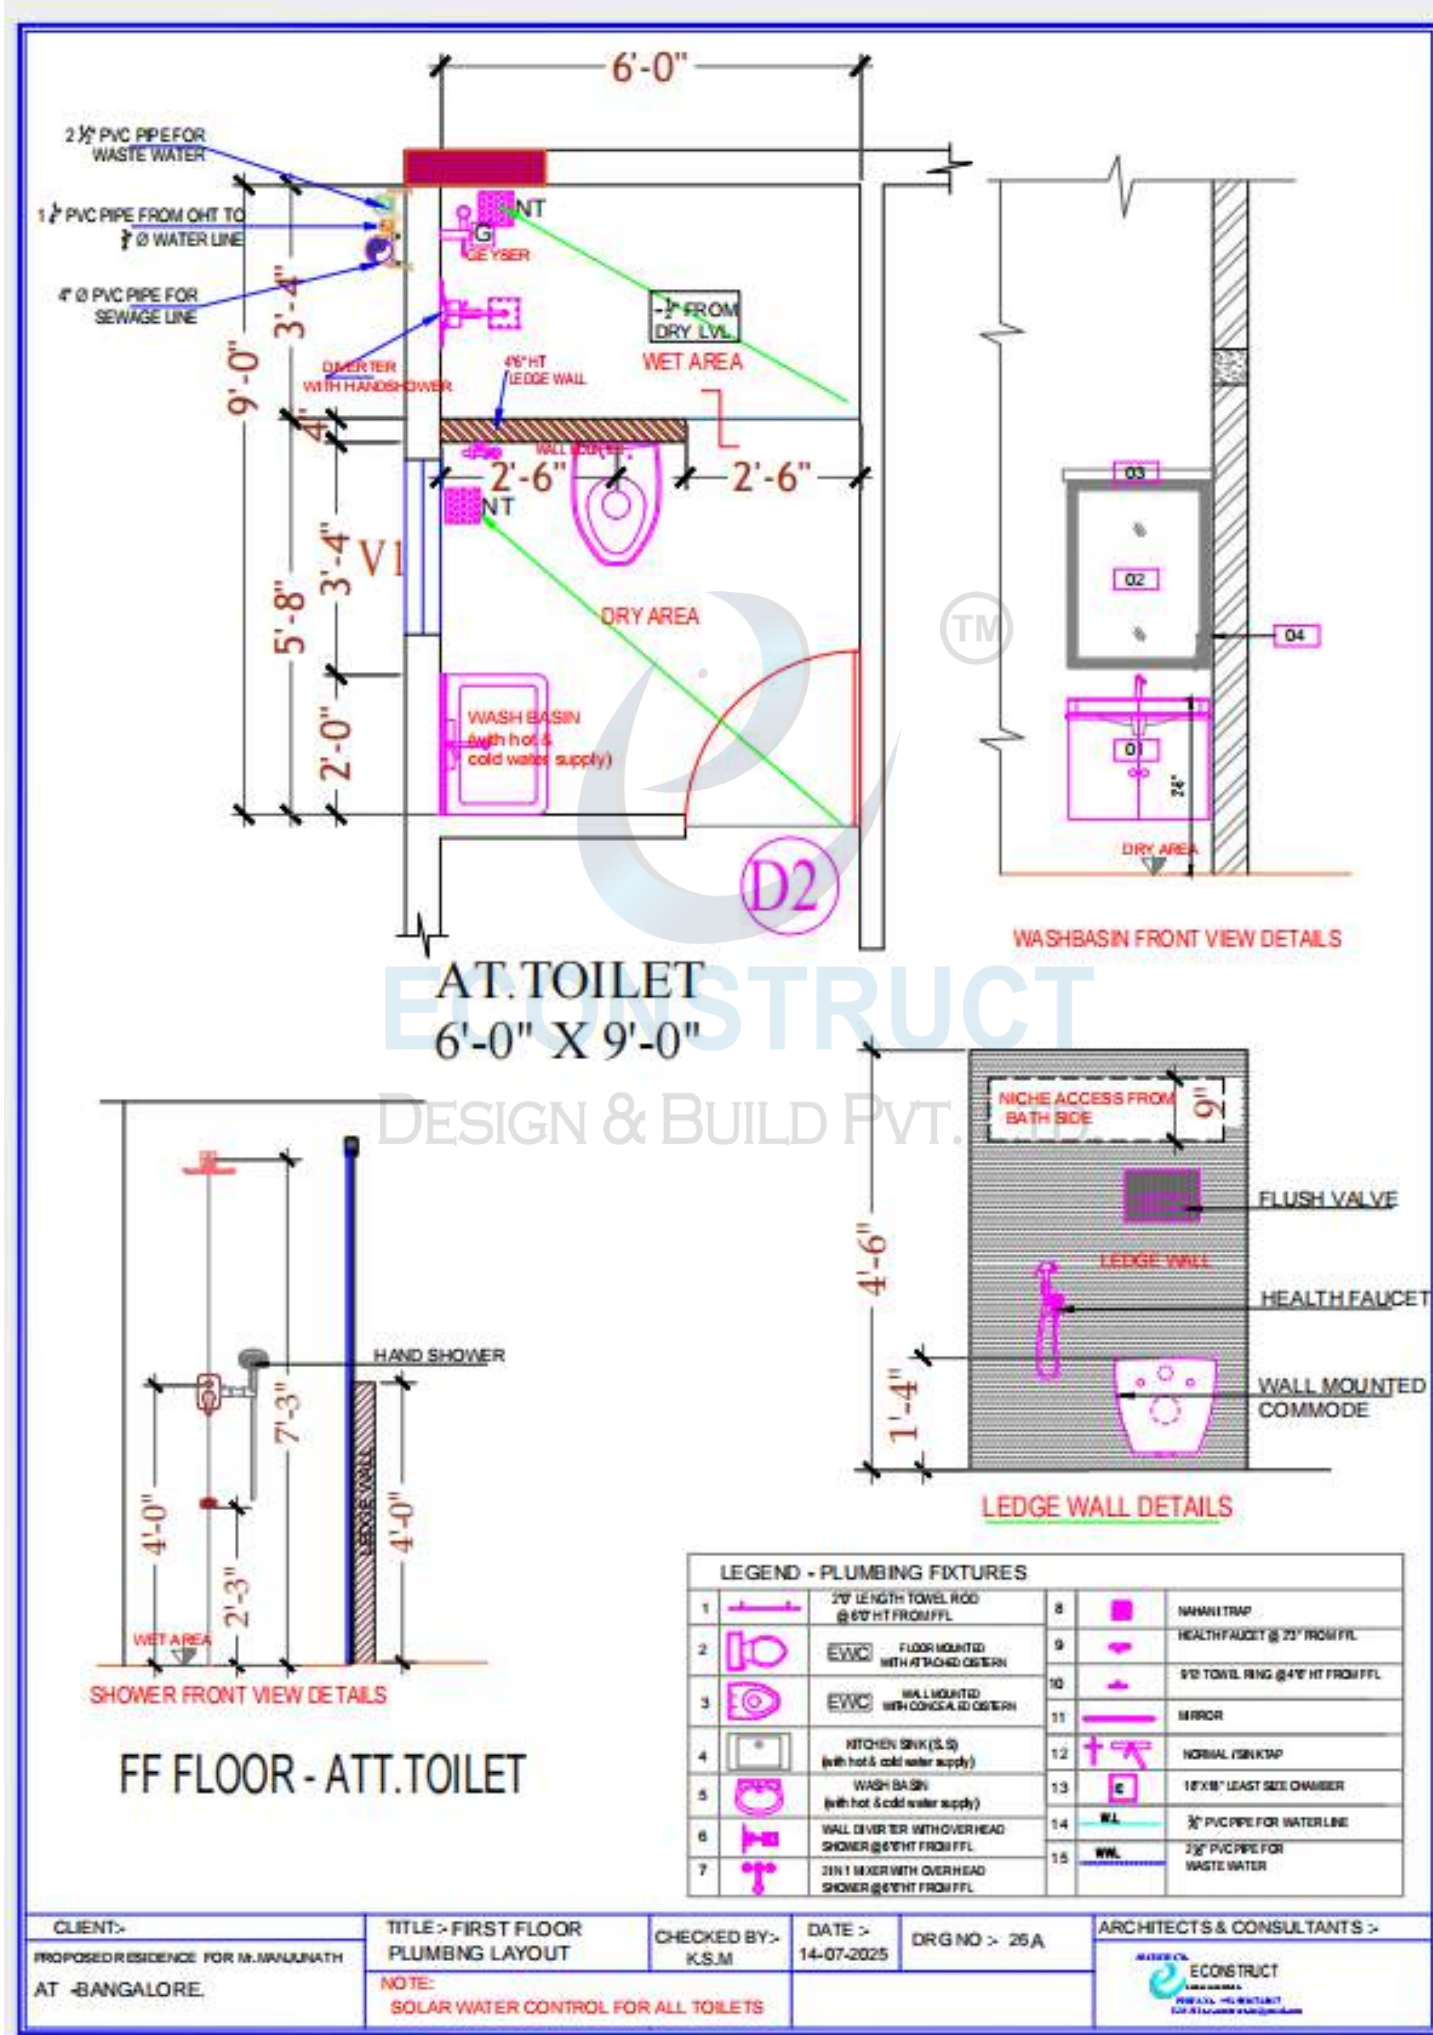


22


COMPOUND DETAILS

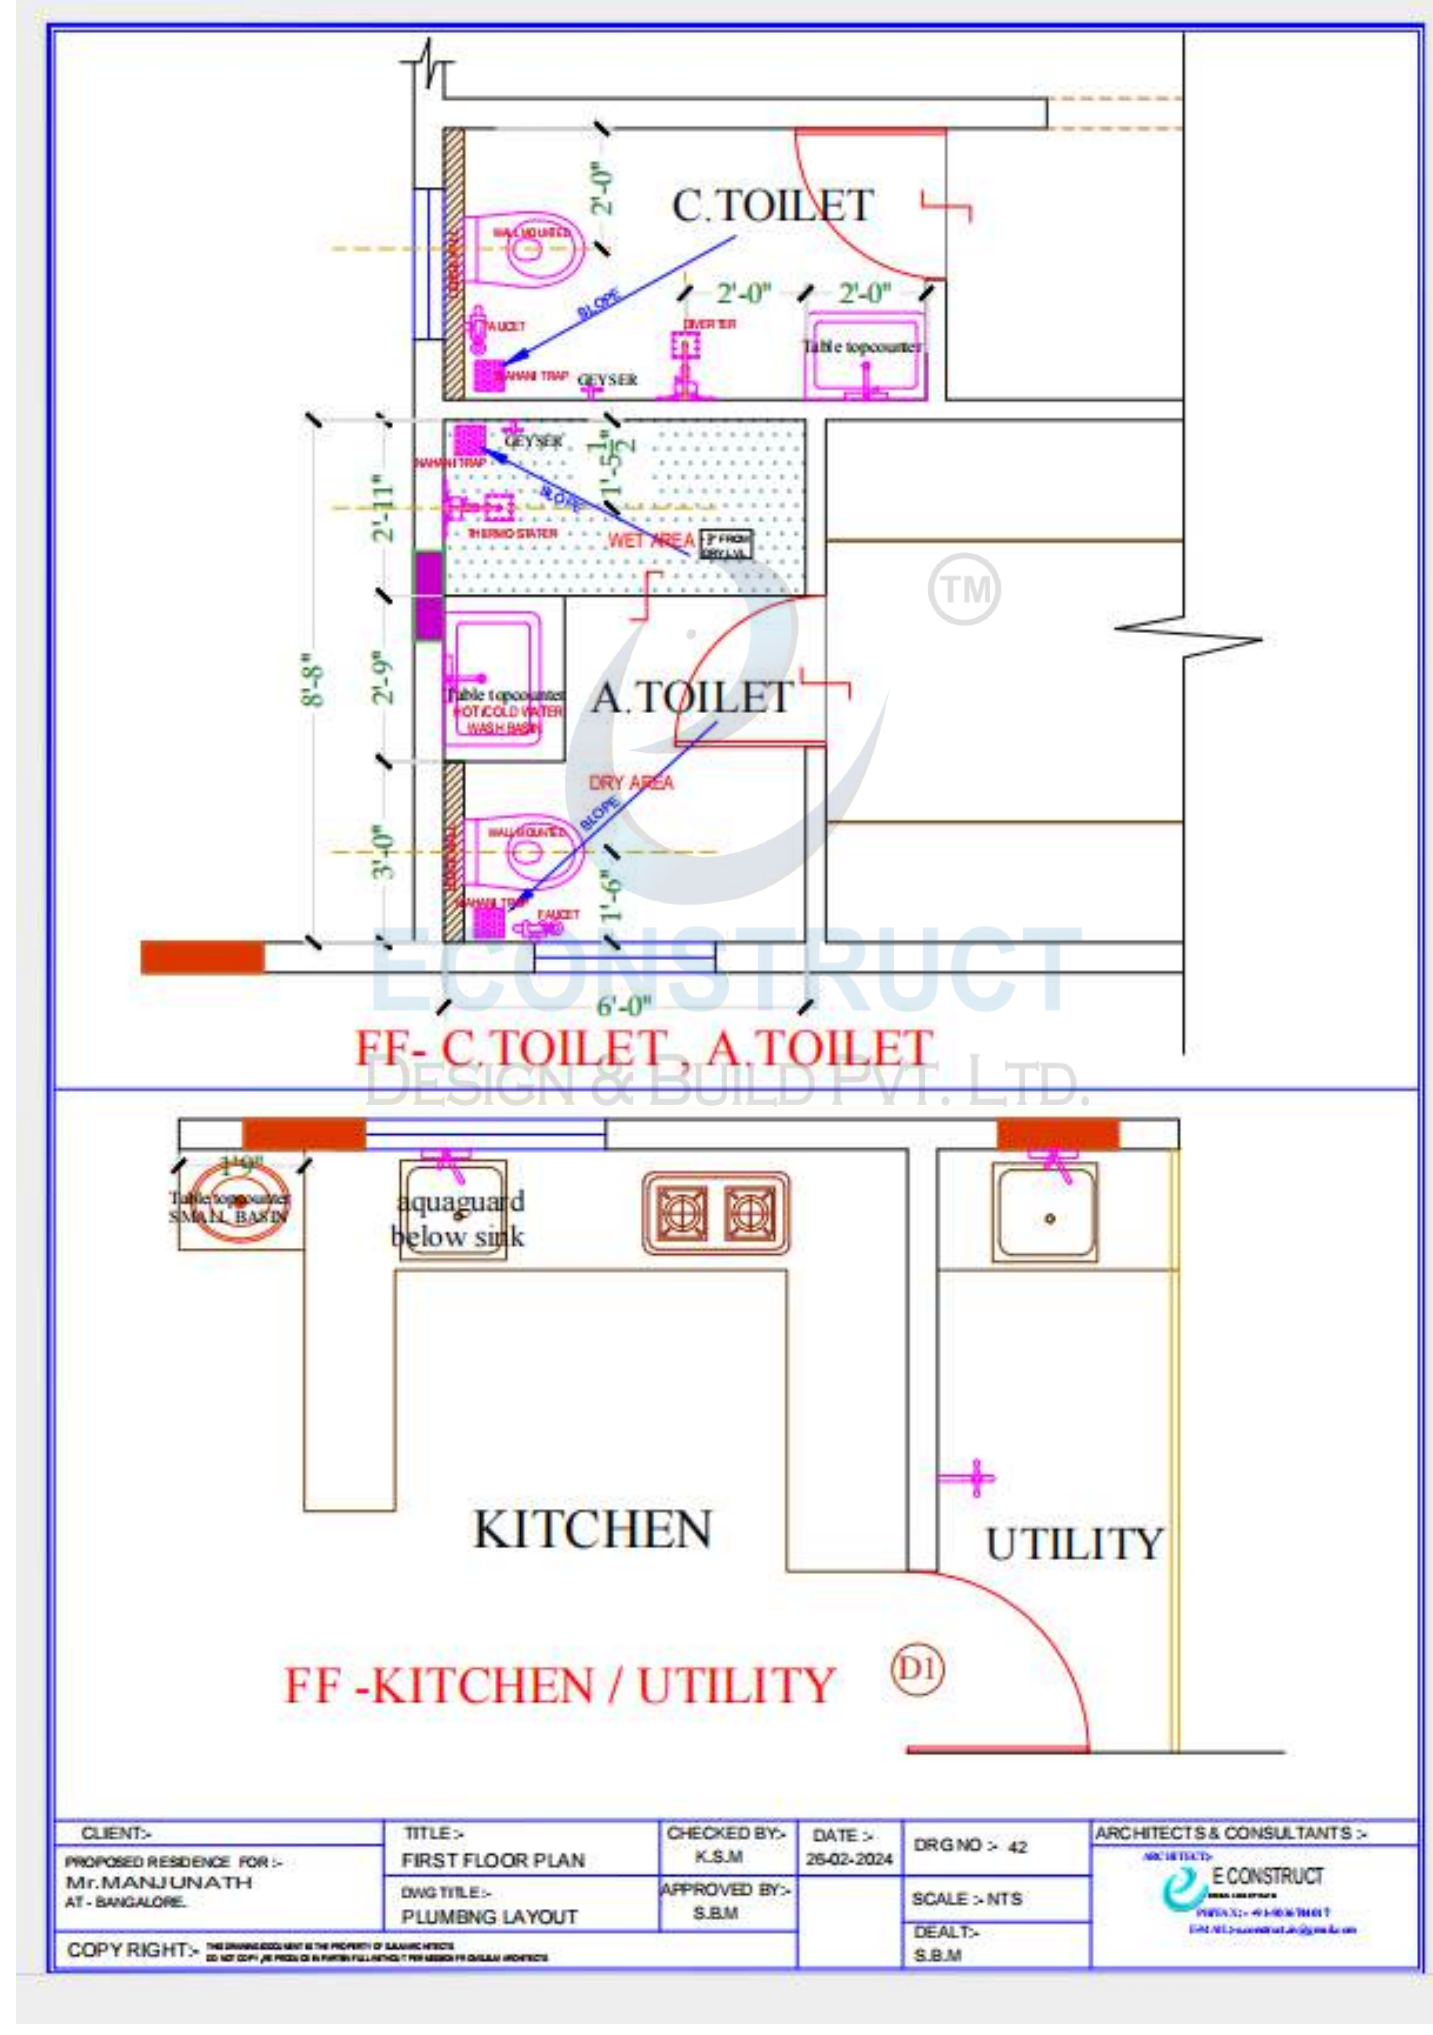


CLIENT:-	TITLE >	CHECKED BY:-	DATE >	DRG NO >	ARCHITECTS & CONSULTANTS >
PROPOSED RESIDENCE FOR :-	FIRST FLOOR PLAN	K.S.M.	26-02-2024	42	ECONSTRUCT
Mr. MANJUNATH	DWG TITLE >	APPROVED BY:-		SCALE >	
AT - BANGALORE.	PLUMBING LAYOUT	S.B.M.		NTS	
				DEALT:-	
				S.B.M.	

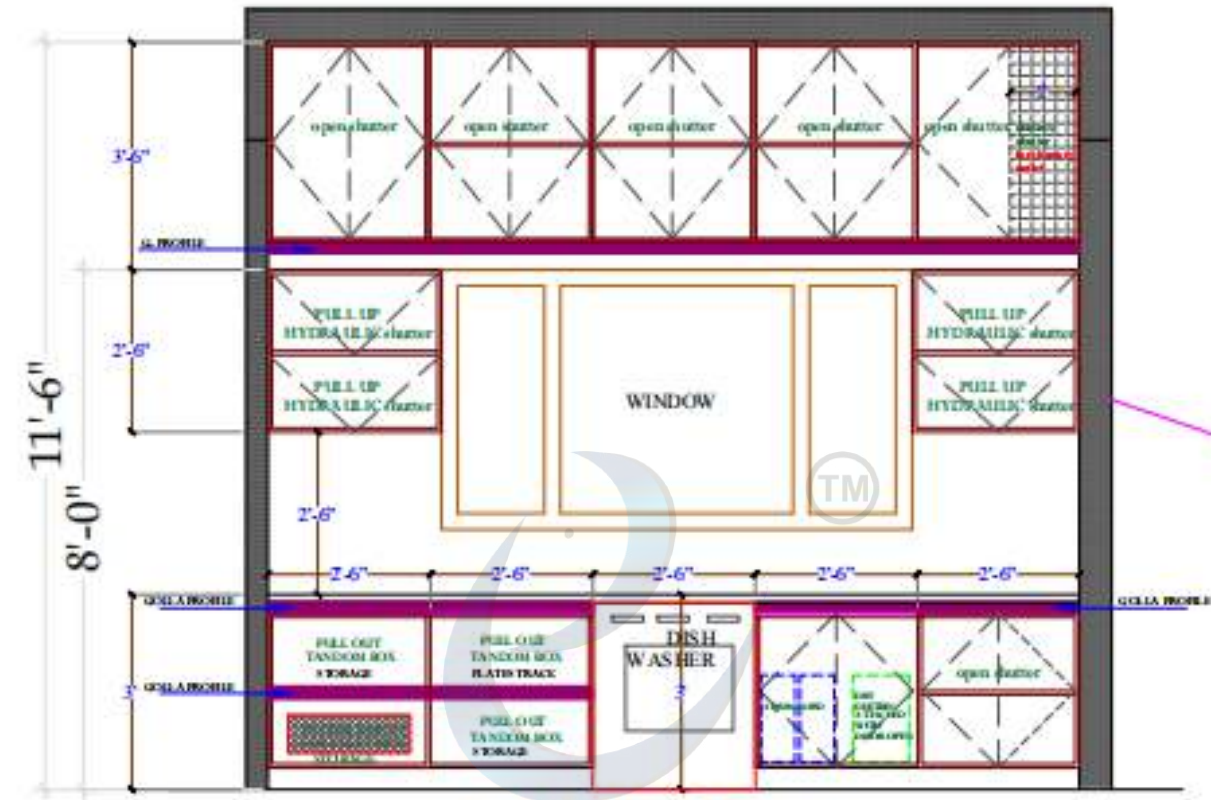

NORTH WALL

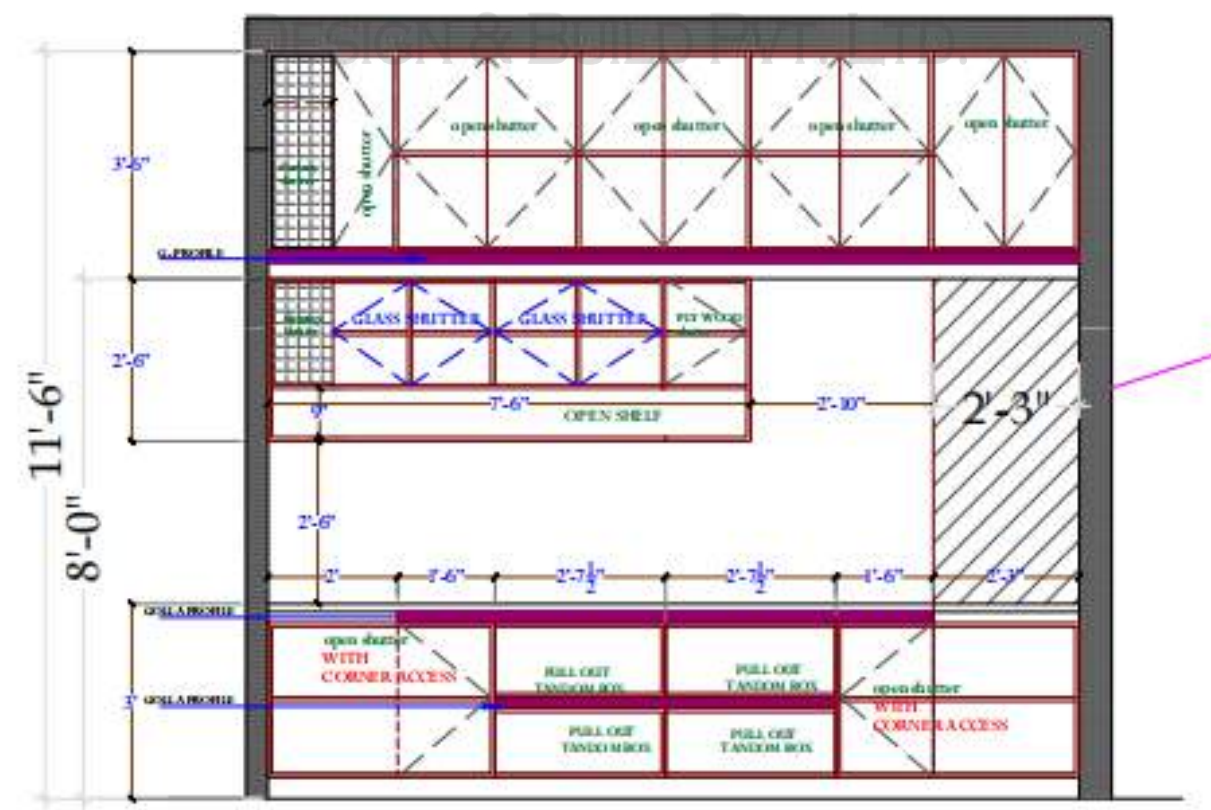


SOUTH WALL

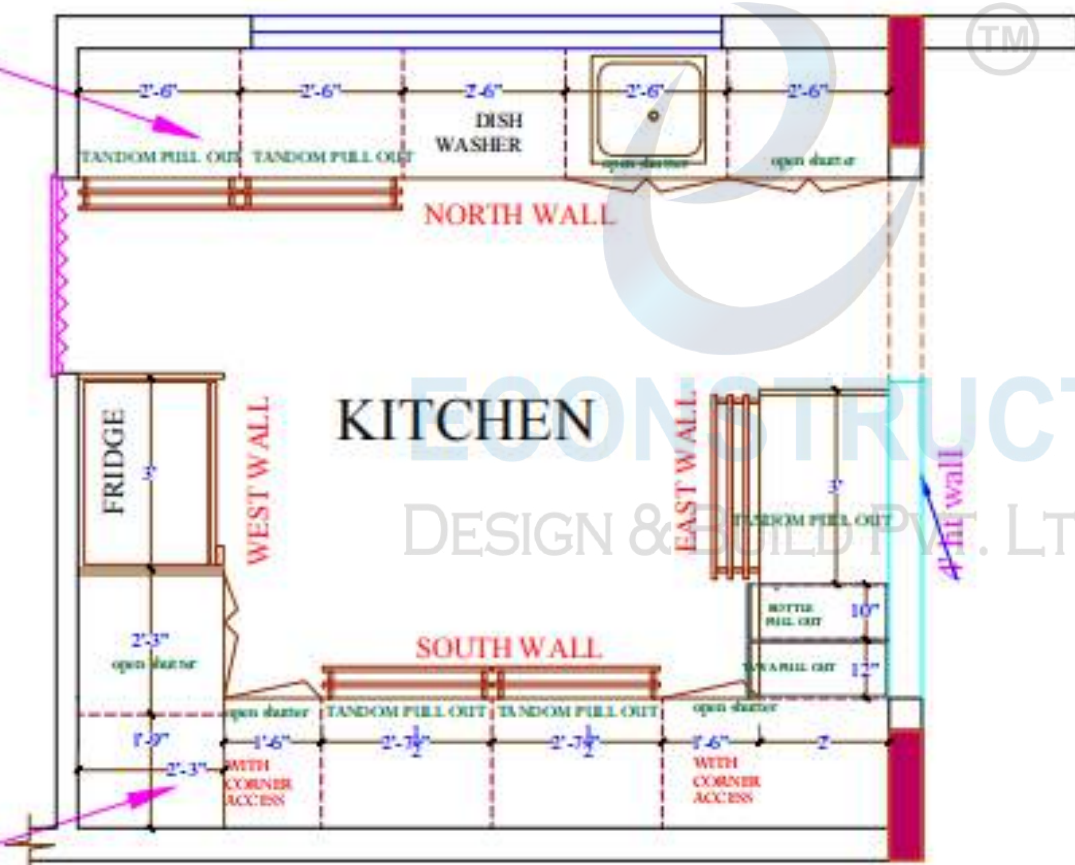


KITCHEN PLAN

REVISION -1




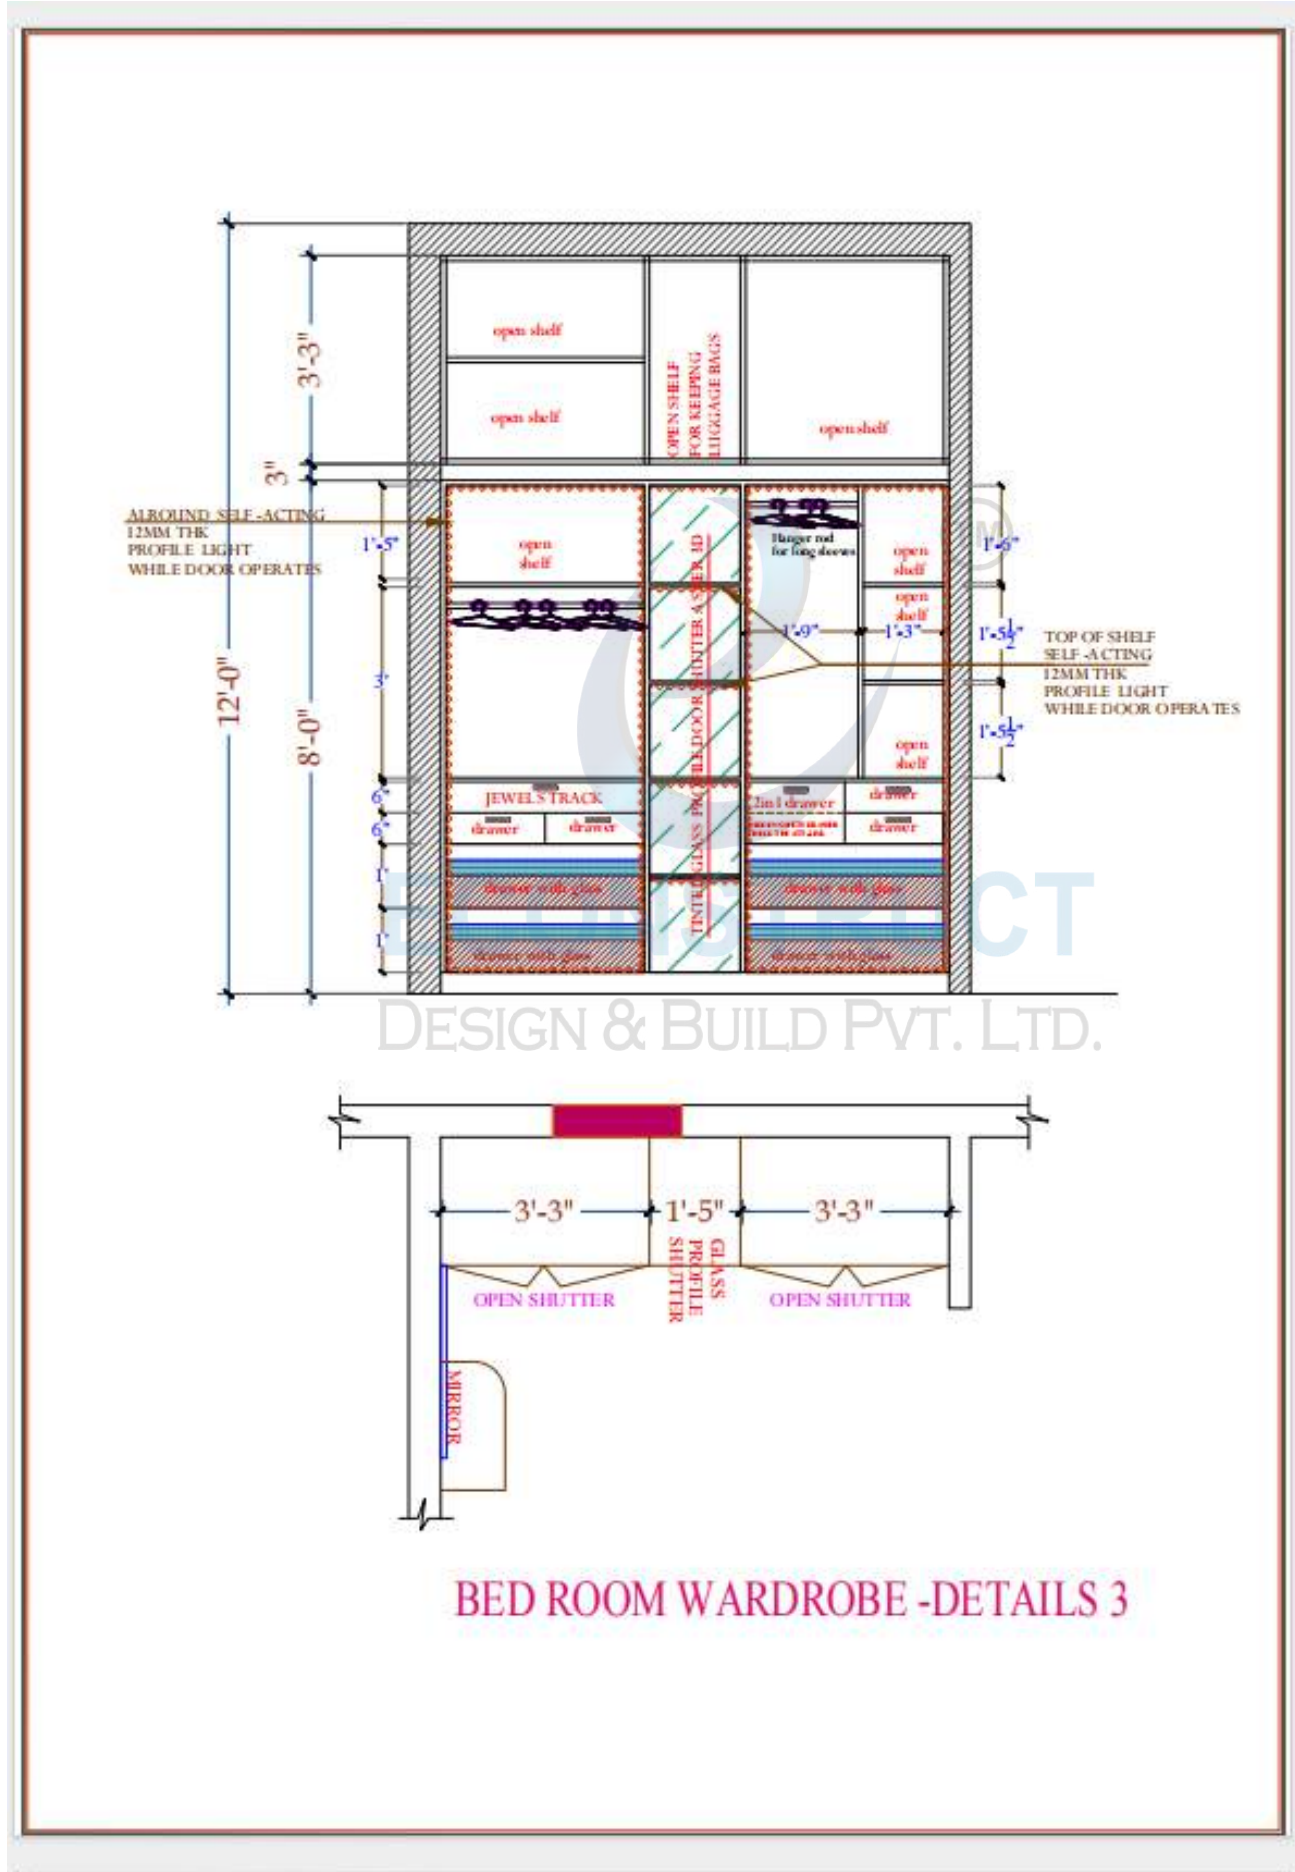


BED ROOM WARDROBE -DETAILS 3

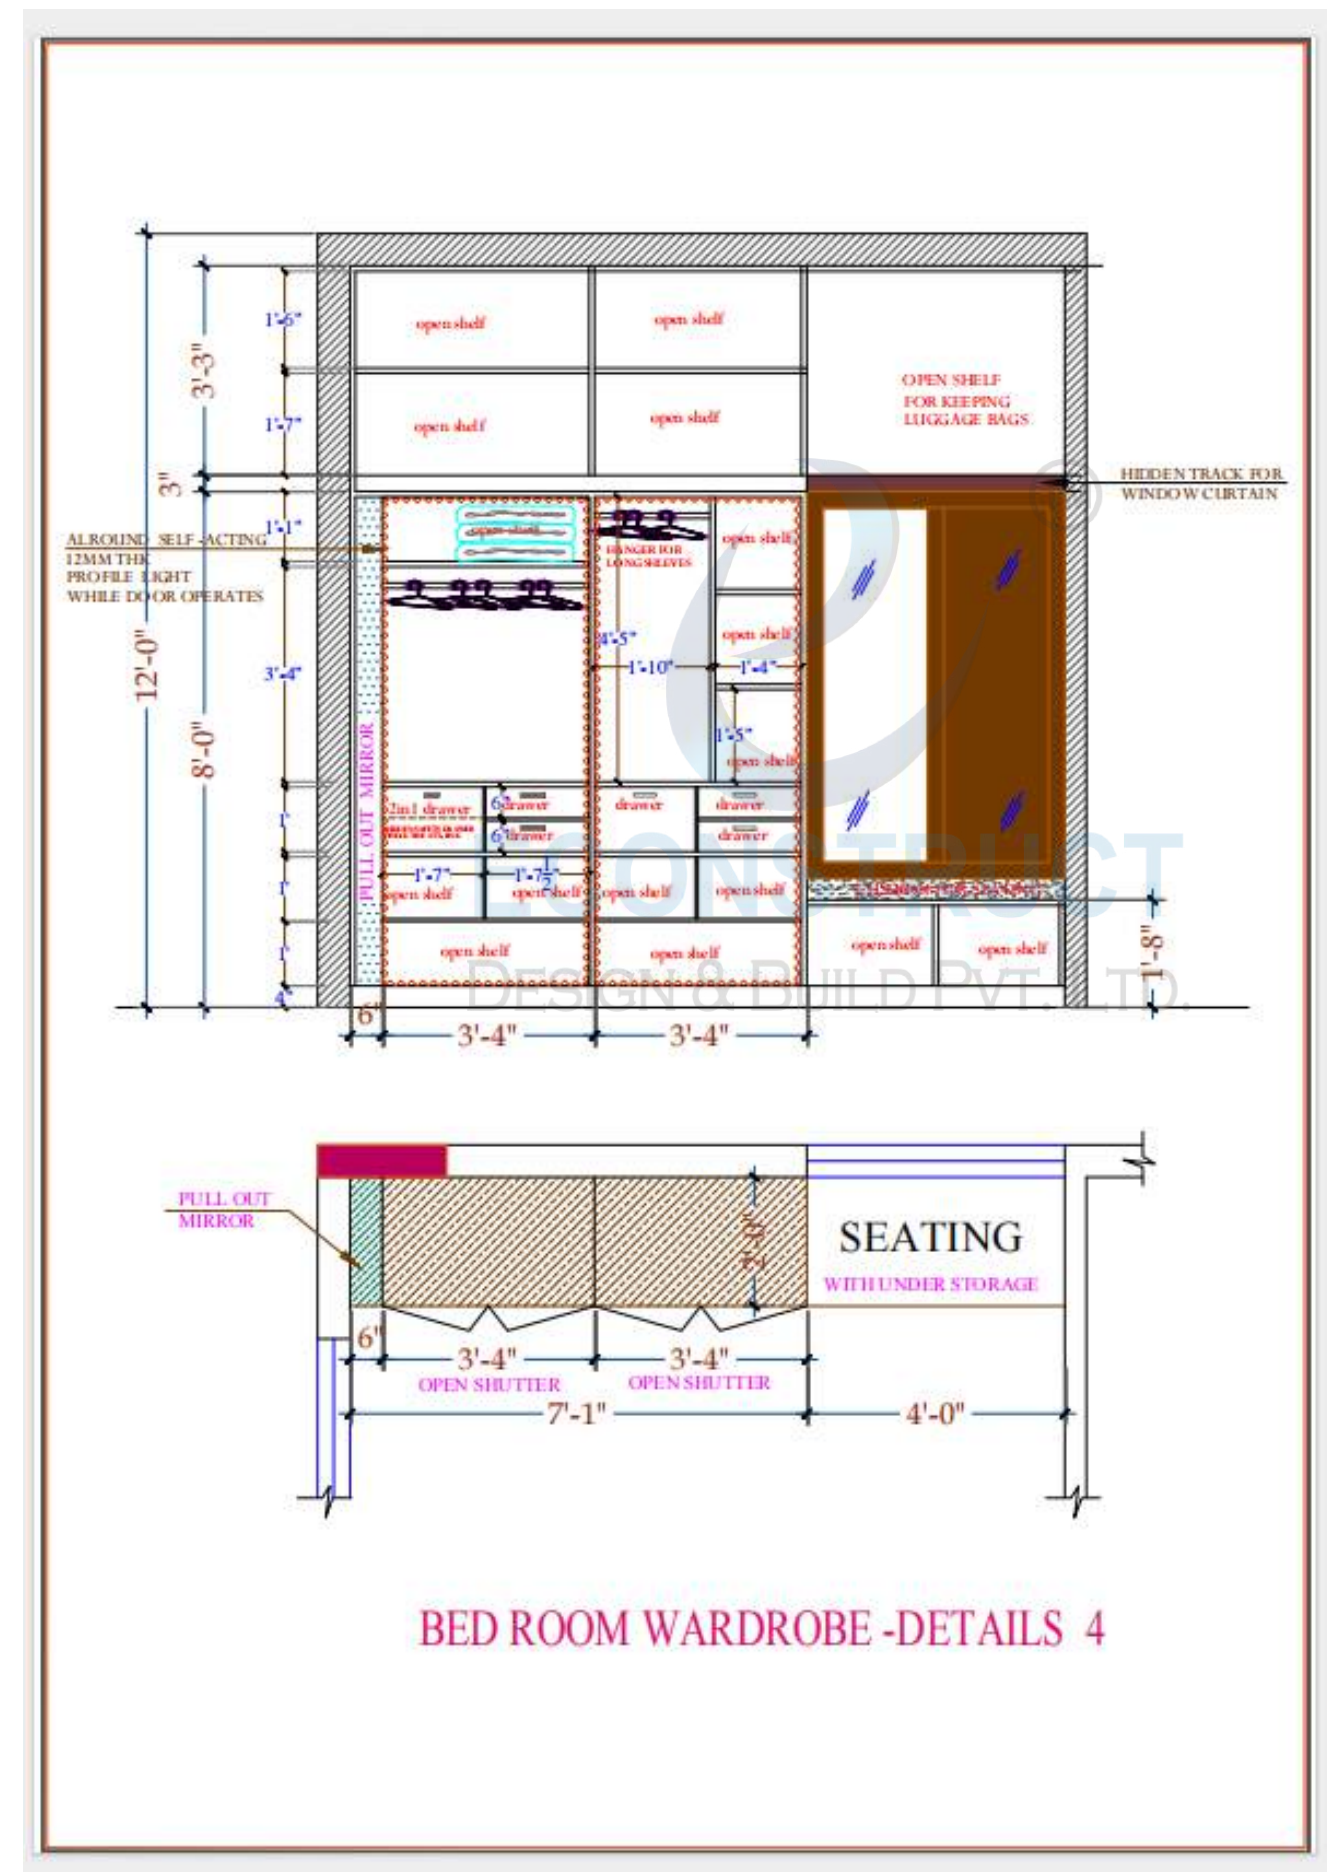

BED ROOM WARDROBE -DETAILS 4



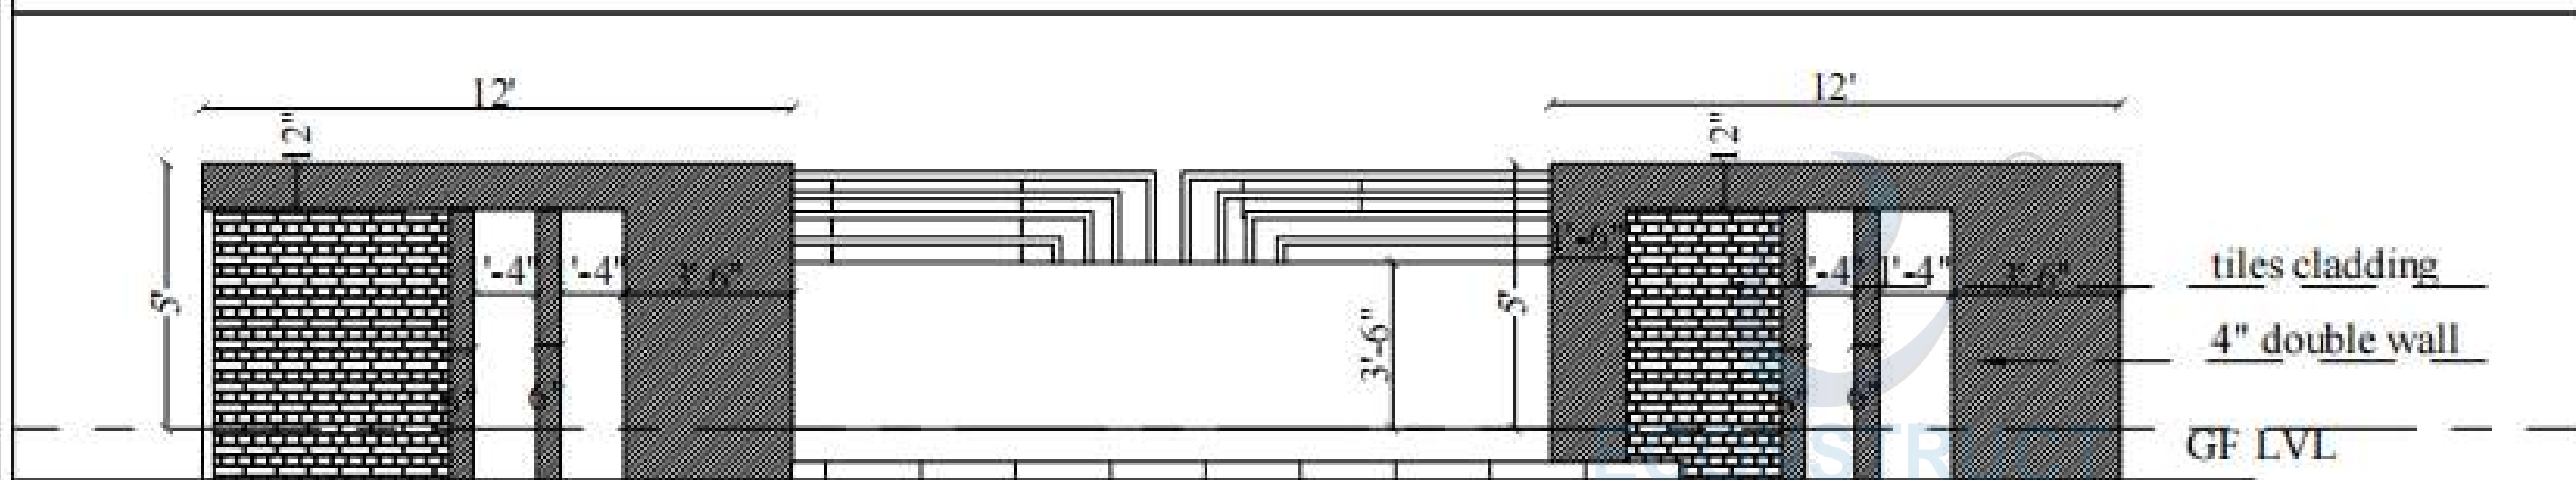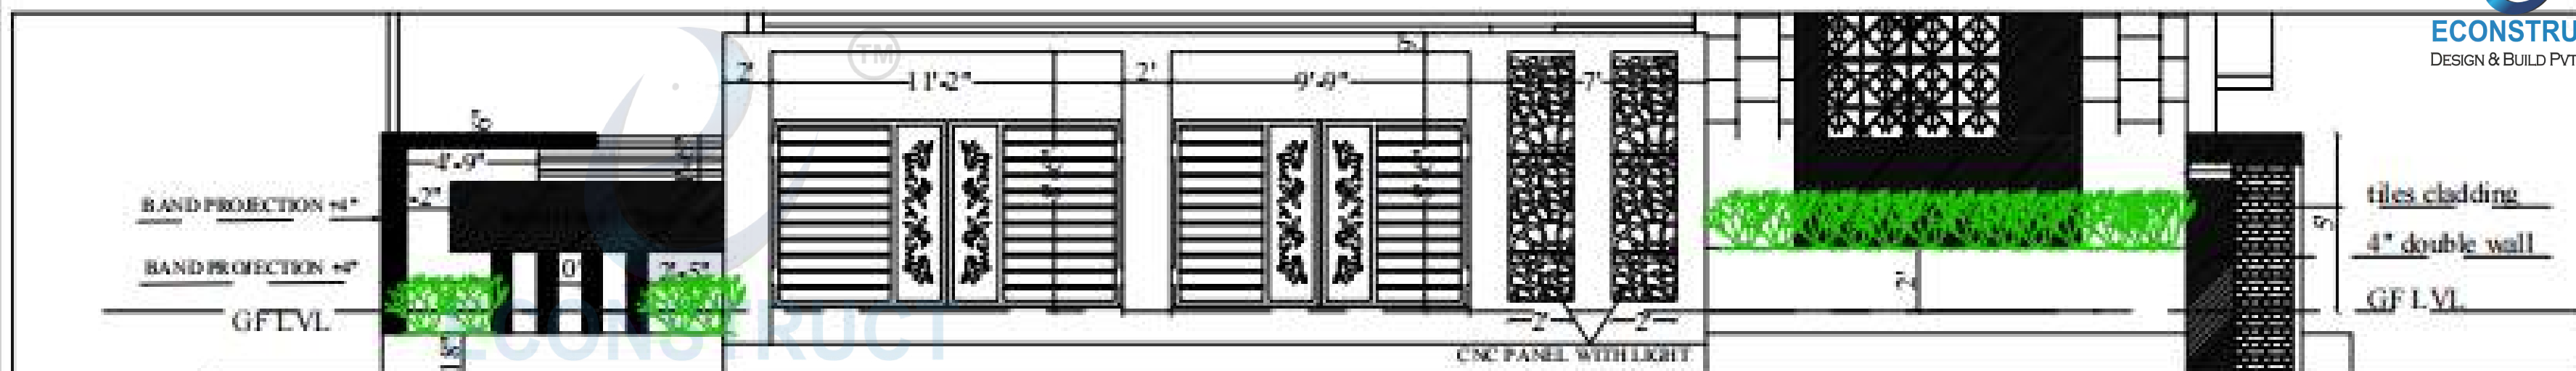

WEST SIDE COMPOUND DETAILS


- **3D
Elevation**



- **Home Interior Entrance**



- Home Interior - Devghar

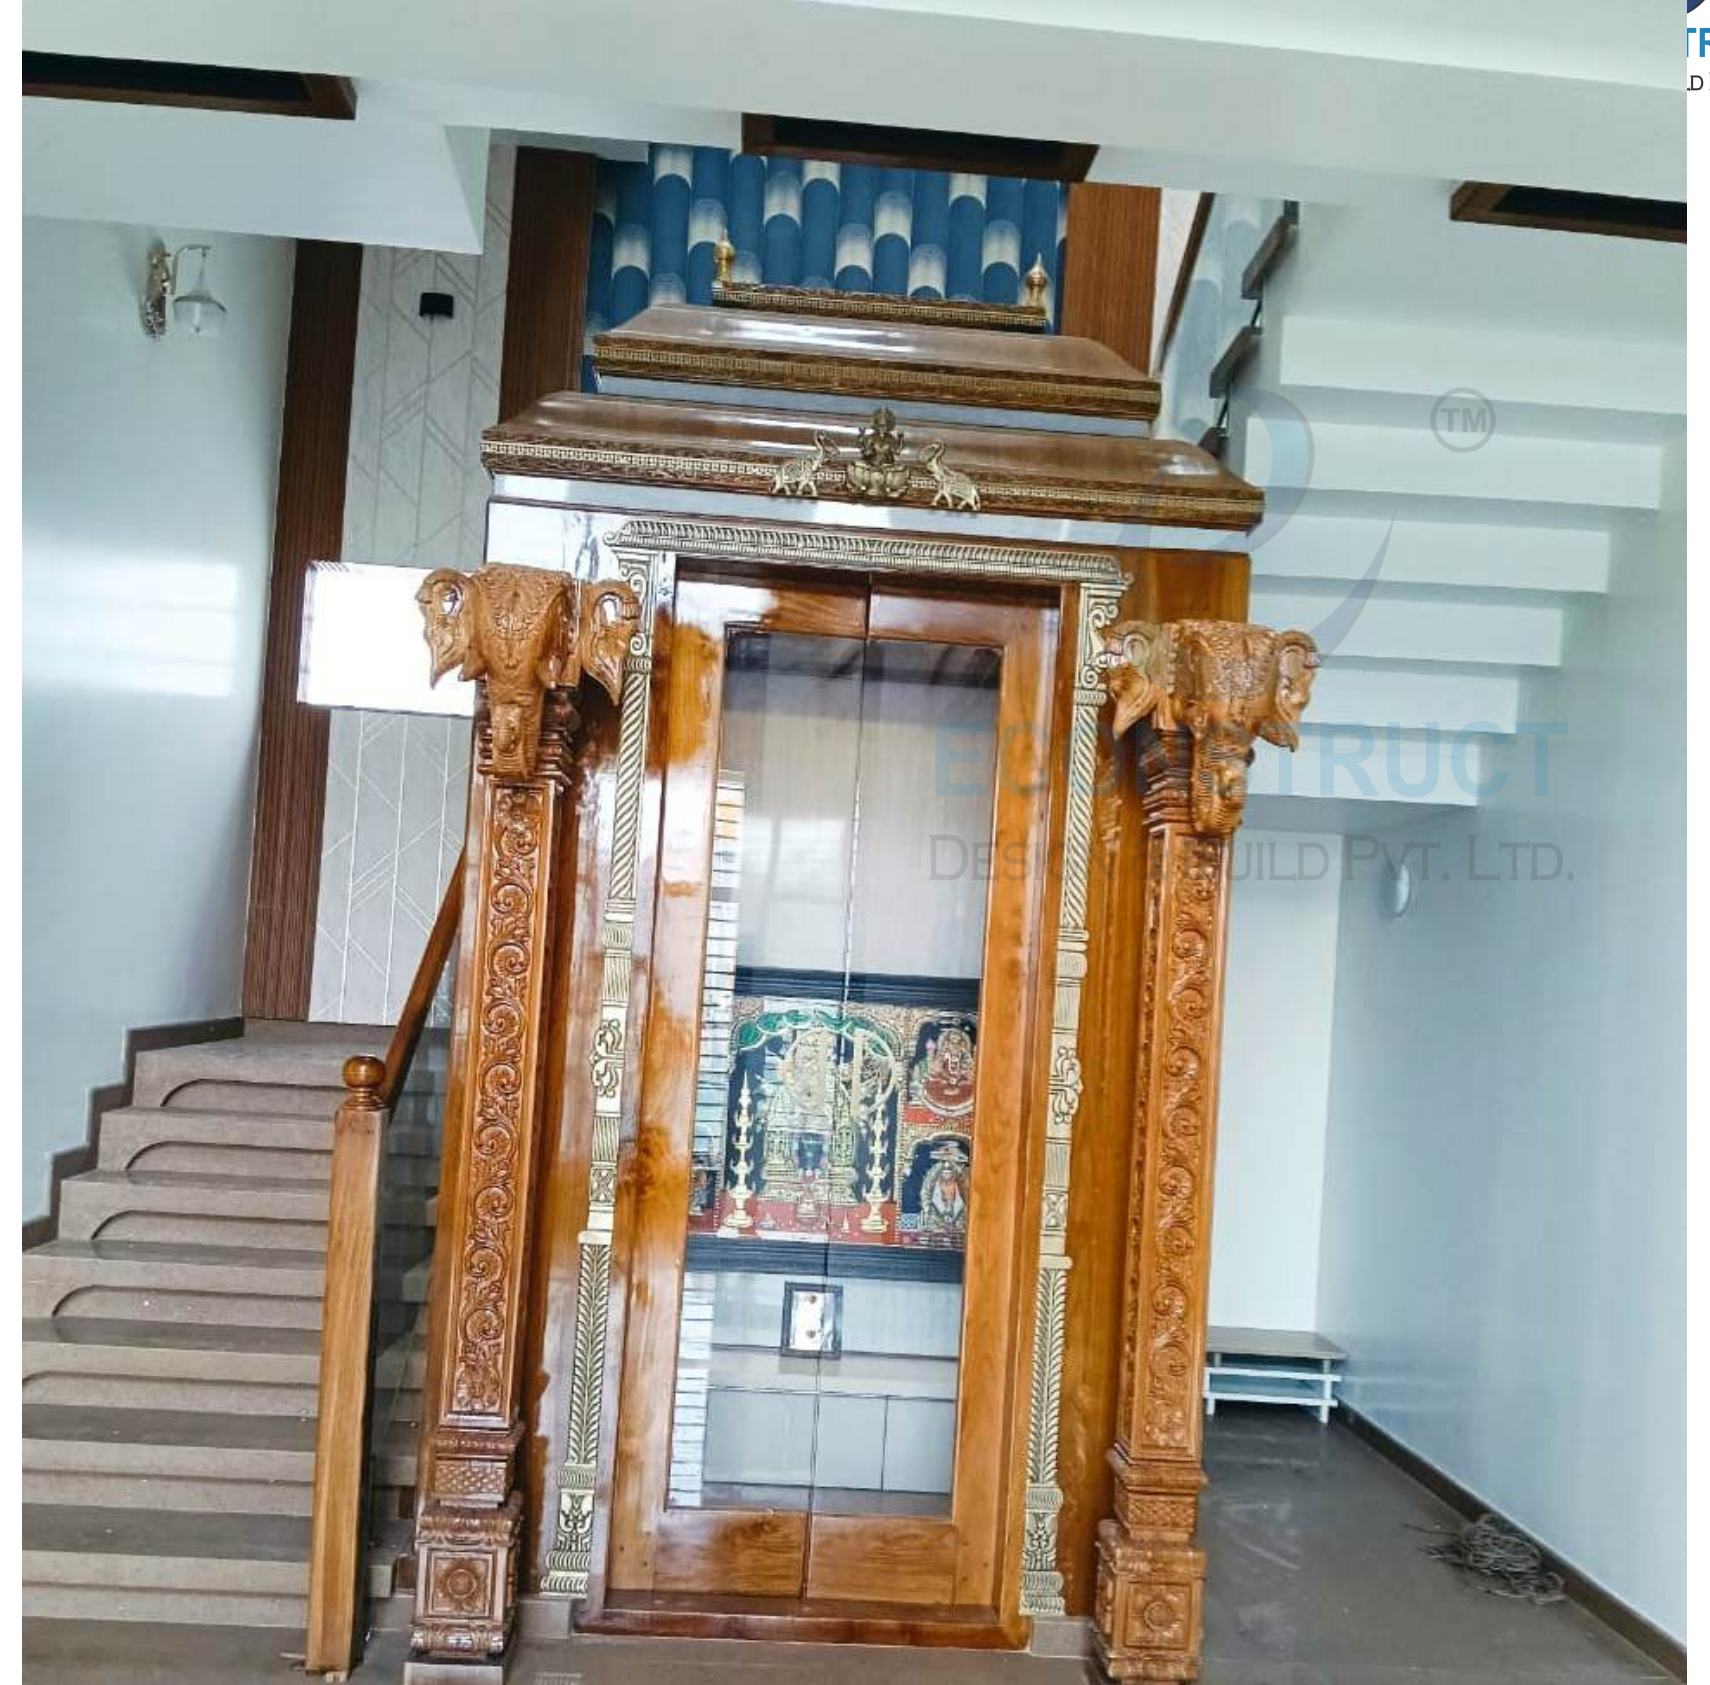

• Home Interior



• Home Interior



- Home Interior



• Turning Vision into Reality



Some images of our projects.



Some images of our projects.



www.e-construct.in

THANK YOU



Build Smart. Build Strong. Build with E-Construct
Don't just build a house — build a home that lasts for generations.

Contact Us: +91 9036744017 / +91 7259921111 / +91 7259222888